## PRESCRIZIONI

*MATERIALI PRESCRITTI:*

**Acciaio** (Secondo: UNI EN 10025-2; UNI EN 10027)
*Tipologia*
n° 1.4401 ( AISI 316 -18% Cr 8%Ni 2.5 Mo - EN X5CrNIMo17-12-2)

*Caratteristiche meccaniche*
**n° 1.4401 (AISI 316)**

| | |
|---|---|
| Tensione di snervamento caratteristico (T ambiente): | $f_{yk}$ = 500 N/mm² |
| Modulo di elasticità (T ambiente): | $f_{tk}$ = 200000 N/mm² |
| Deformazione massima a rottura (T ambiente): Spessore nominale >3mm | A% = 40% |

**Bulloni**
*Tipologia*
Acciaio inossidabile - A2
*Caratteristiche meccaniche*

| | |
|---|---|
| Carico unitario di scostamento dalla prporzionalità: | $f_{yb}$ ≥ 210 N/mm² |
| Carico unitario di rottura: | $f_{tb}$ ≥ 500 N/mm² |
| Allungamento dopo rottura: | >0,6 volte Ø |

**Saldature**
*Tipologia*
Struttura non soggetta a fatica
Giunto: Ad angolo (A)
Testa a Testa (T-T)
*Dimensione*

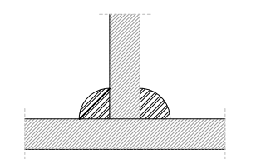

S1≥S2
l=S2
a=0,71xS2

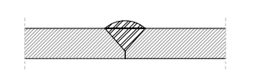

S1≥S2
l=S2
a=0,5xS2

*Criteri di accettabilità (UNI EN ISO 5817:2008)*
Livello di qualità: C

*PRESCRIZIONI COSTRUTTIVE*

Tutte le misure sono da verificare in opere in presenza della Direzione Lavori.

## ABACO CARPENTERIA

| Elemento n° | Tipo | Quantità | Lunghezza (mm) | Larghezza (mm) | Spessore (mm) | Peso (Kg) |
|---|---|---|---|---|---|---|
| P01 | Tubolare 180x100x5 | 12 | 4504 | - | - | 1134 |
| ME01 | Tubolare 180x100x5 | 12 | 1300 | - | - | 328 |
| Piastra 01 | Piastra | 12 | 144 | 60 | 5 | 4 |
| Piastra 02 | Piastra | 12 | 108 | 60 | 5 | 3 |
| Piastra 03 | Piastra | 12 | 108 | 60 | 5 | 3 |
| Piastra 04 | Piastra | 12 | 180 | 100 | 5 | 8.5 |
| Piastra 05 | Piastra | 12 | 300 | 220 | 10 | 62 |
| Nervatura triangolare N01 | Piastra | 24 | 250 | 250 | 5 | 59 |
| Chiusura nervature | Piastra | 12 | 354 | 170 | 5 | 28 |
| Nervatura triangolare N02 | Piastra | 48 | 100 | 60 | 5 | 11 |
| T01 | Tubolare 60x60x3 | 24 | 854 | - | - | 116 |
| T02 | Tubolare 60x60x3 | 12 | 1301 | - | - | 87 |
| T03 | Tubolare 60x60x3 | 12 | 1791 | - | - | 121 |

## SIMULAZIONE FOTOGRAFICA

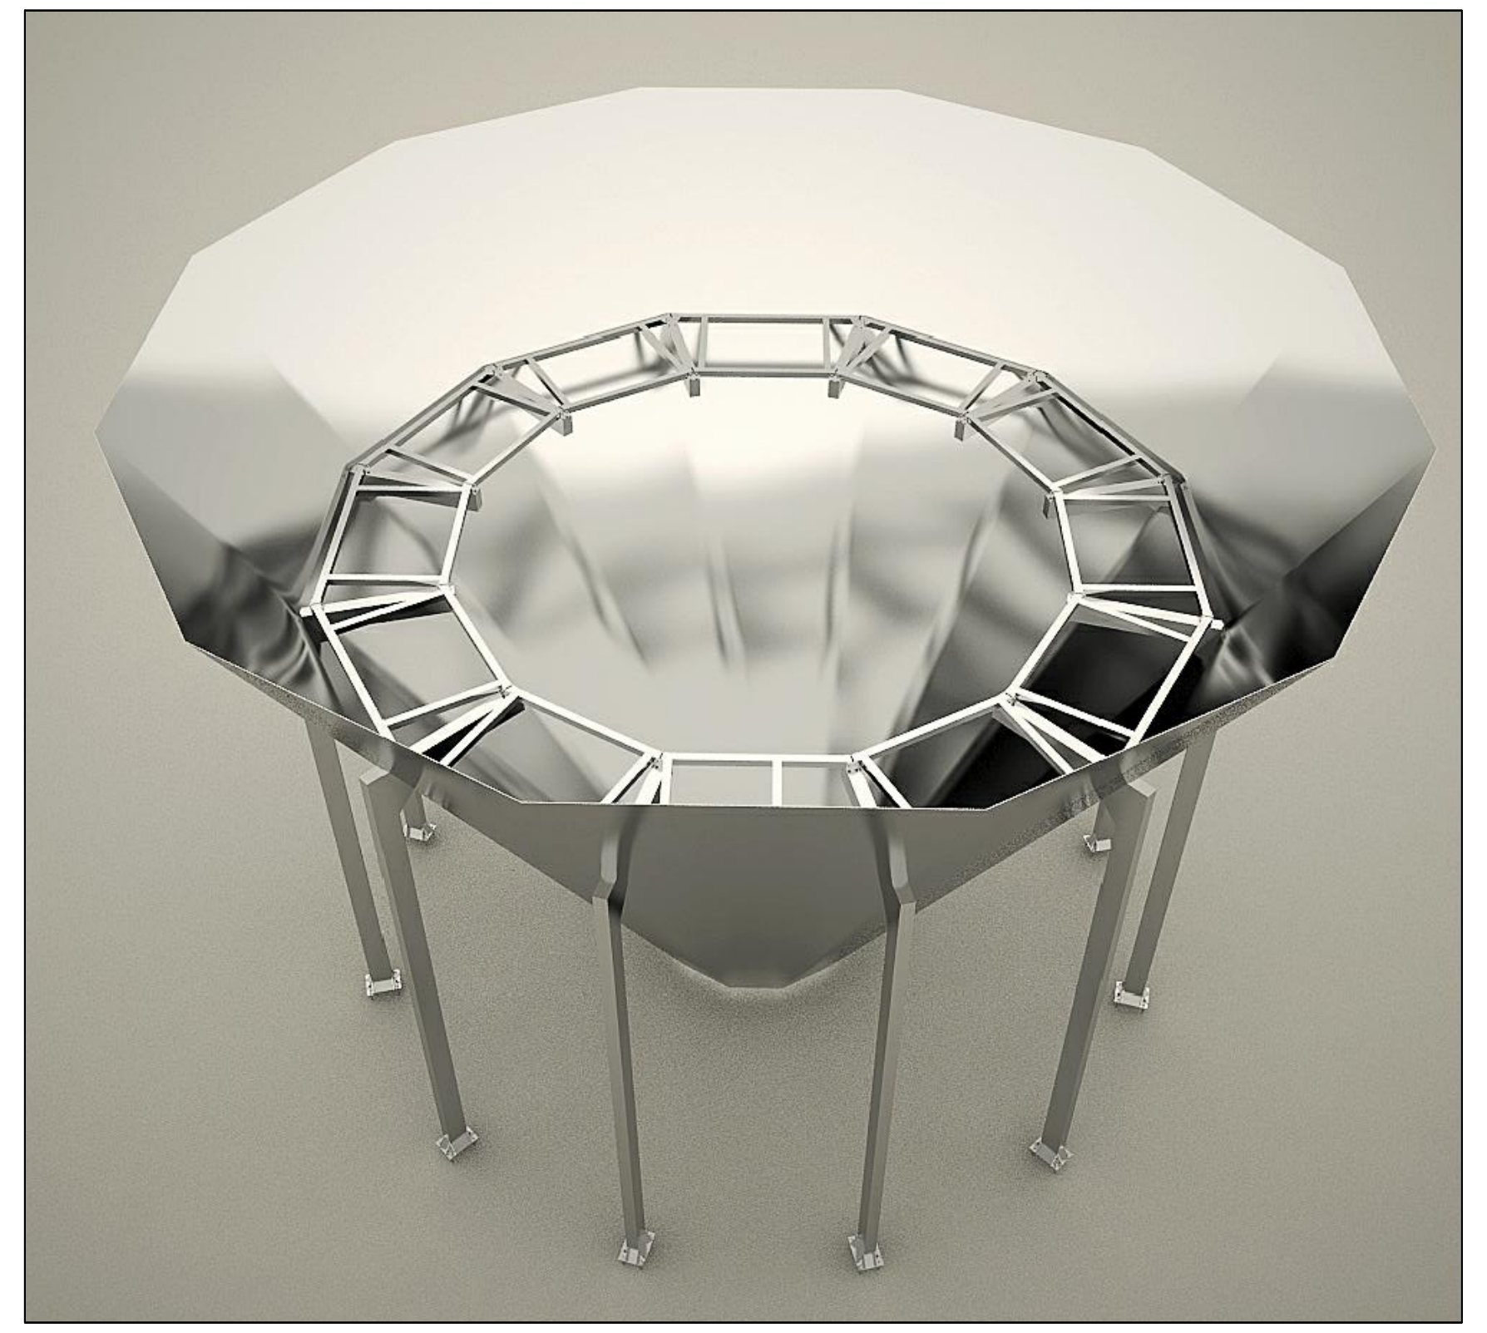

COMUNE DI MELTINA PROVINCIA DI BOLZANO

Oggetto
PROGETTO ESECUTIVO STRUTTURA DI SOSTEGNO PER POSA PACCHI LAMELLARI
DA INSTALLARE SU DEPURATORE SITO IN MELTINA (BZ)

[redacted]

Riferimenti Catastali

Oggetto tavola
- Piante
- Sezioni
- Particolari costruttivi
- Distinte ferri

PROGETTO ESECUTIVO

| | |
|---|---|
| Tav. n° 1 | Variante |
| Data | Scale 1:25 |

[redacted]

Collaboratori

Pianta - Scala 1:25

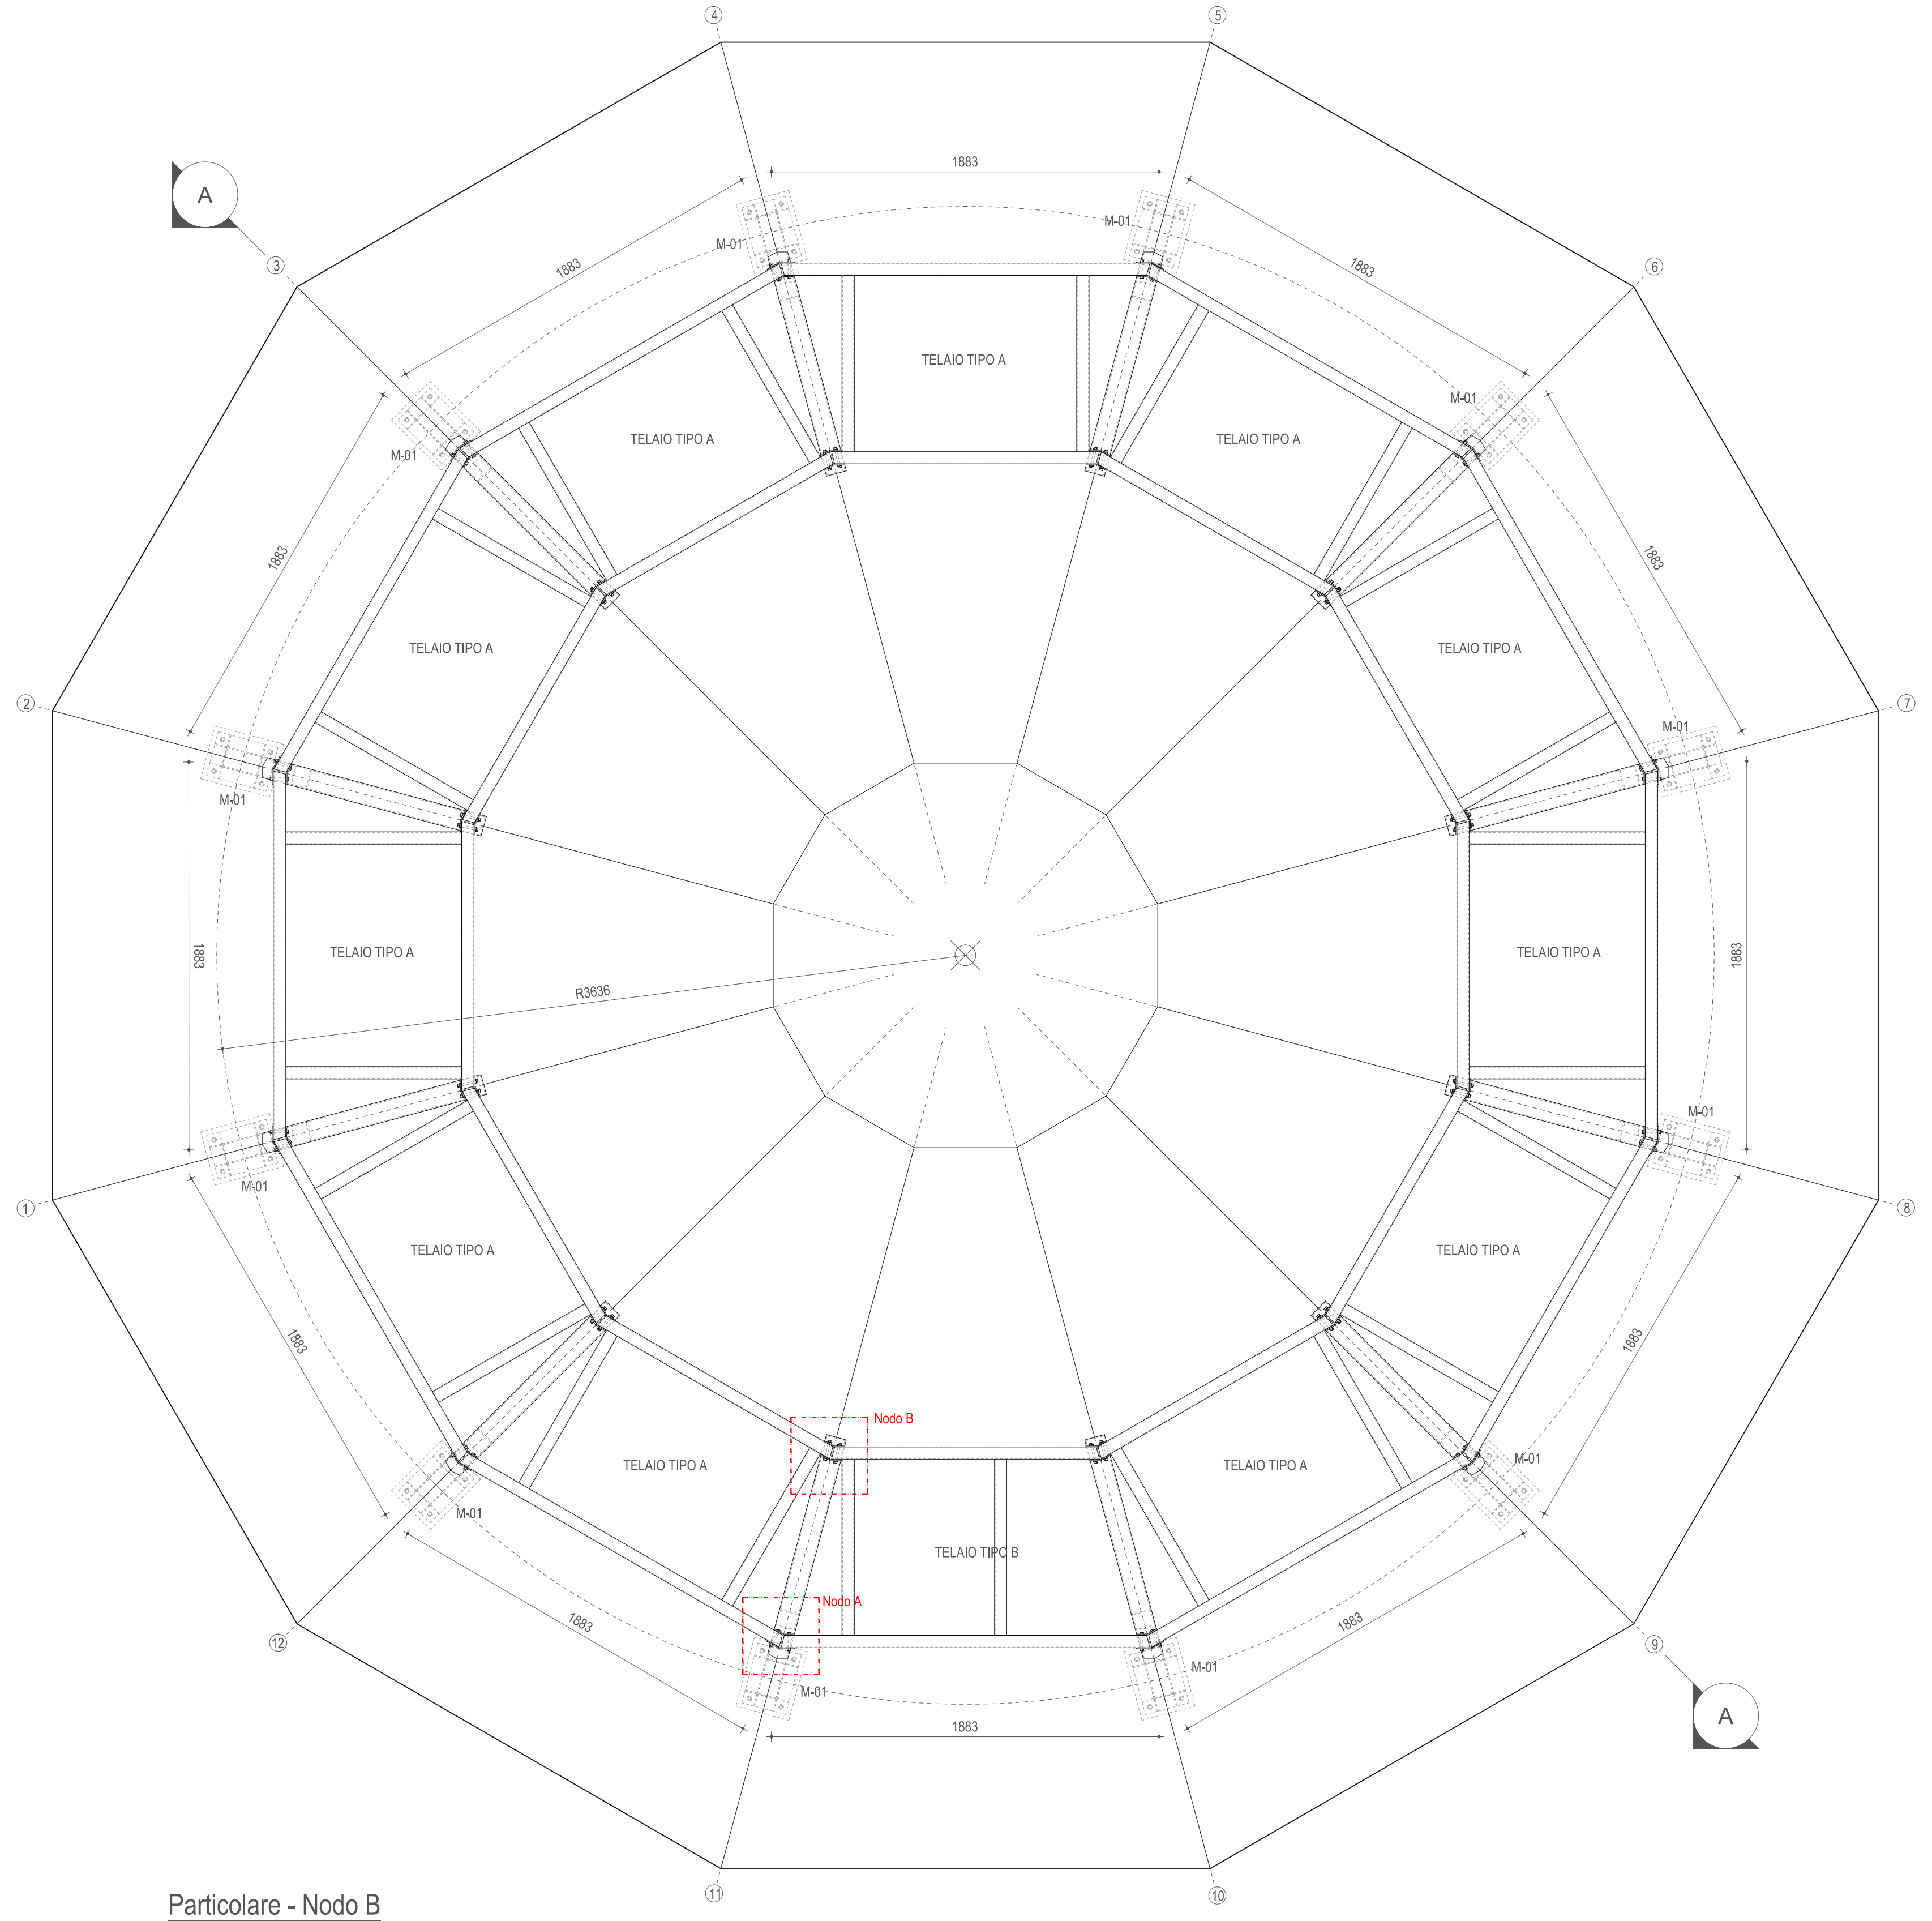

Sezione A-A - Scala 1:25

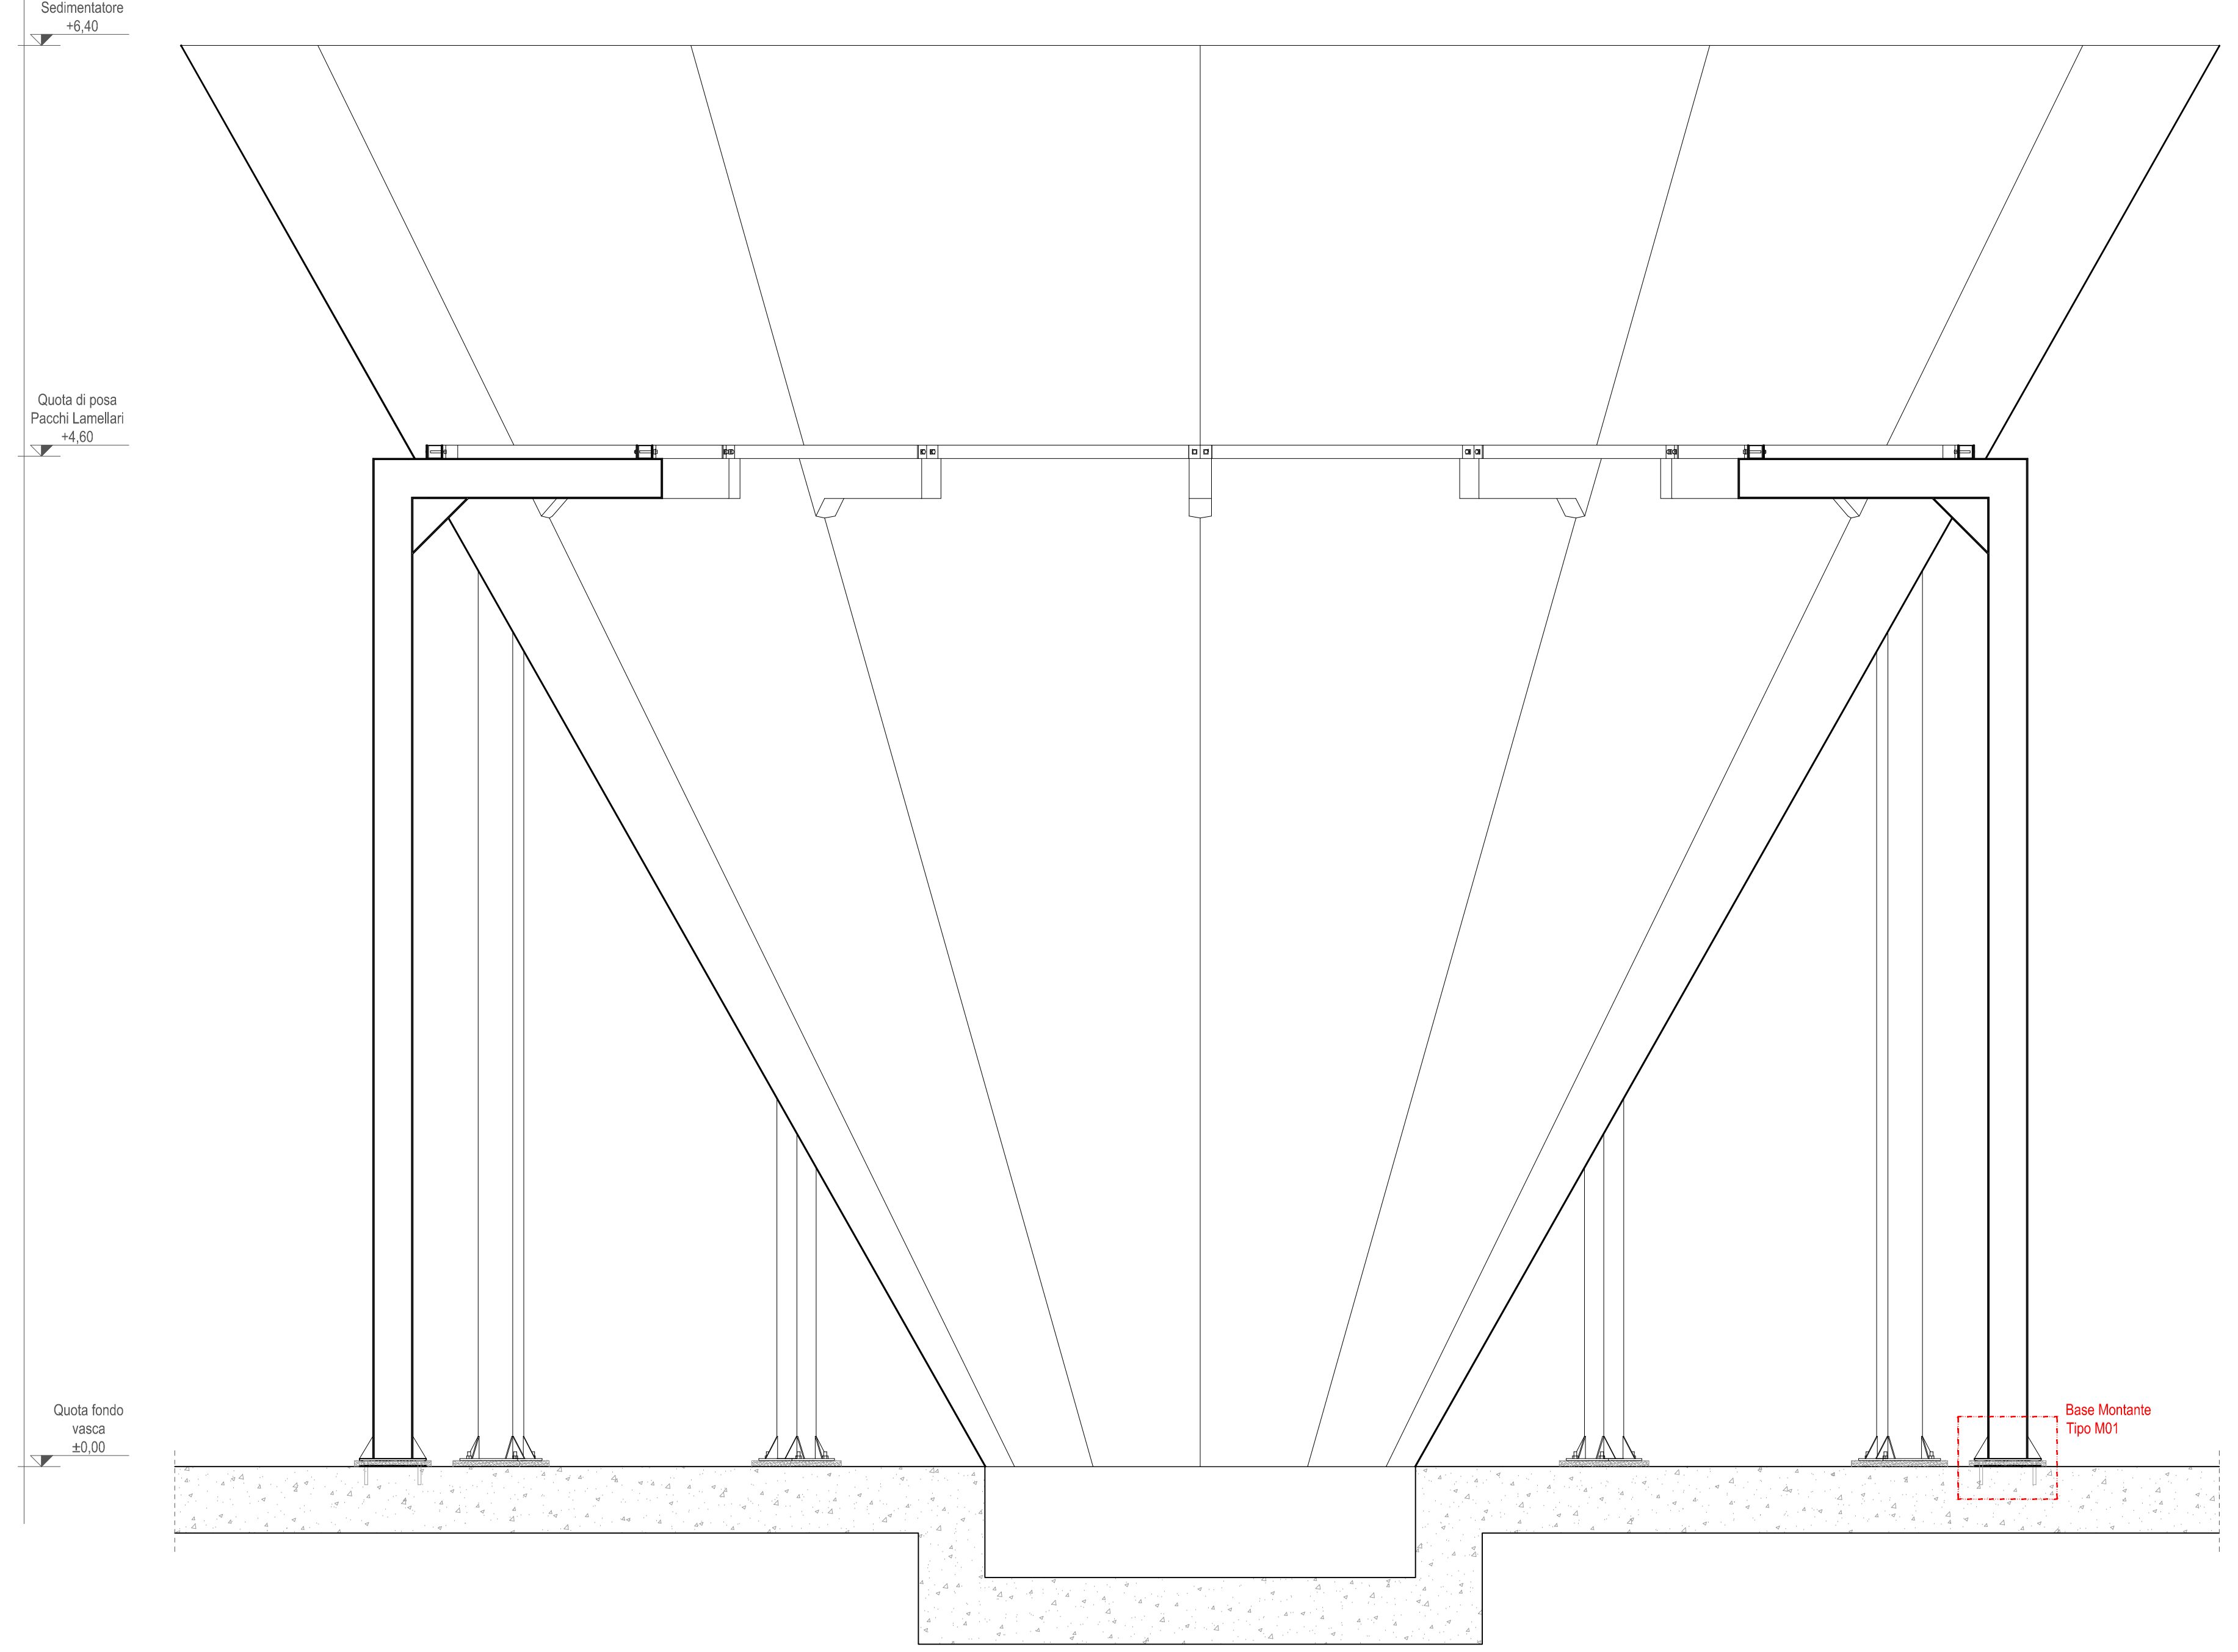
Quota Sedimentatore +6,40
Quota di posa Pacchi Lamellari +4,60
Quota fondo vasca ±0,00
Base Montante Tipo M01

Montante - Tipo M-01
Fronte
Scala 1:10

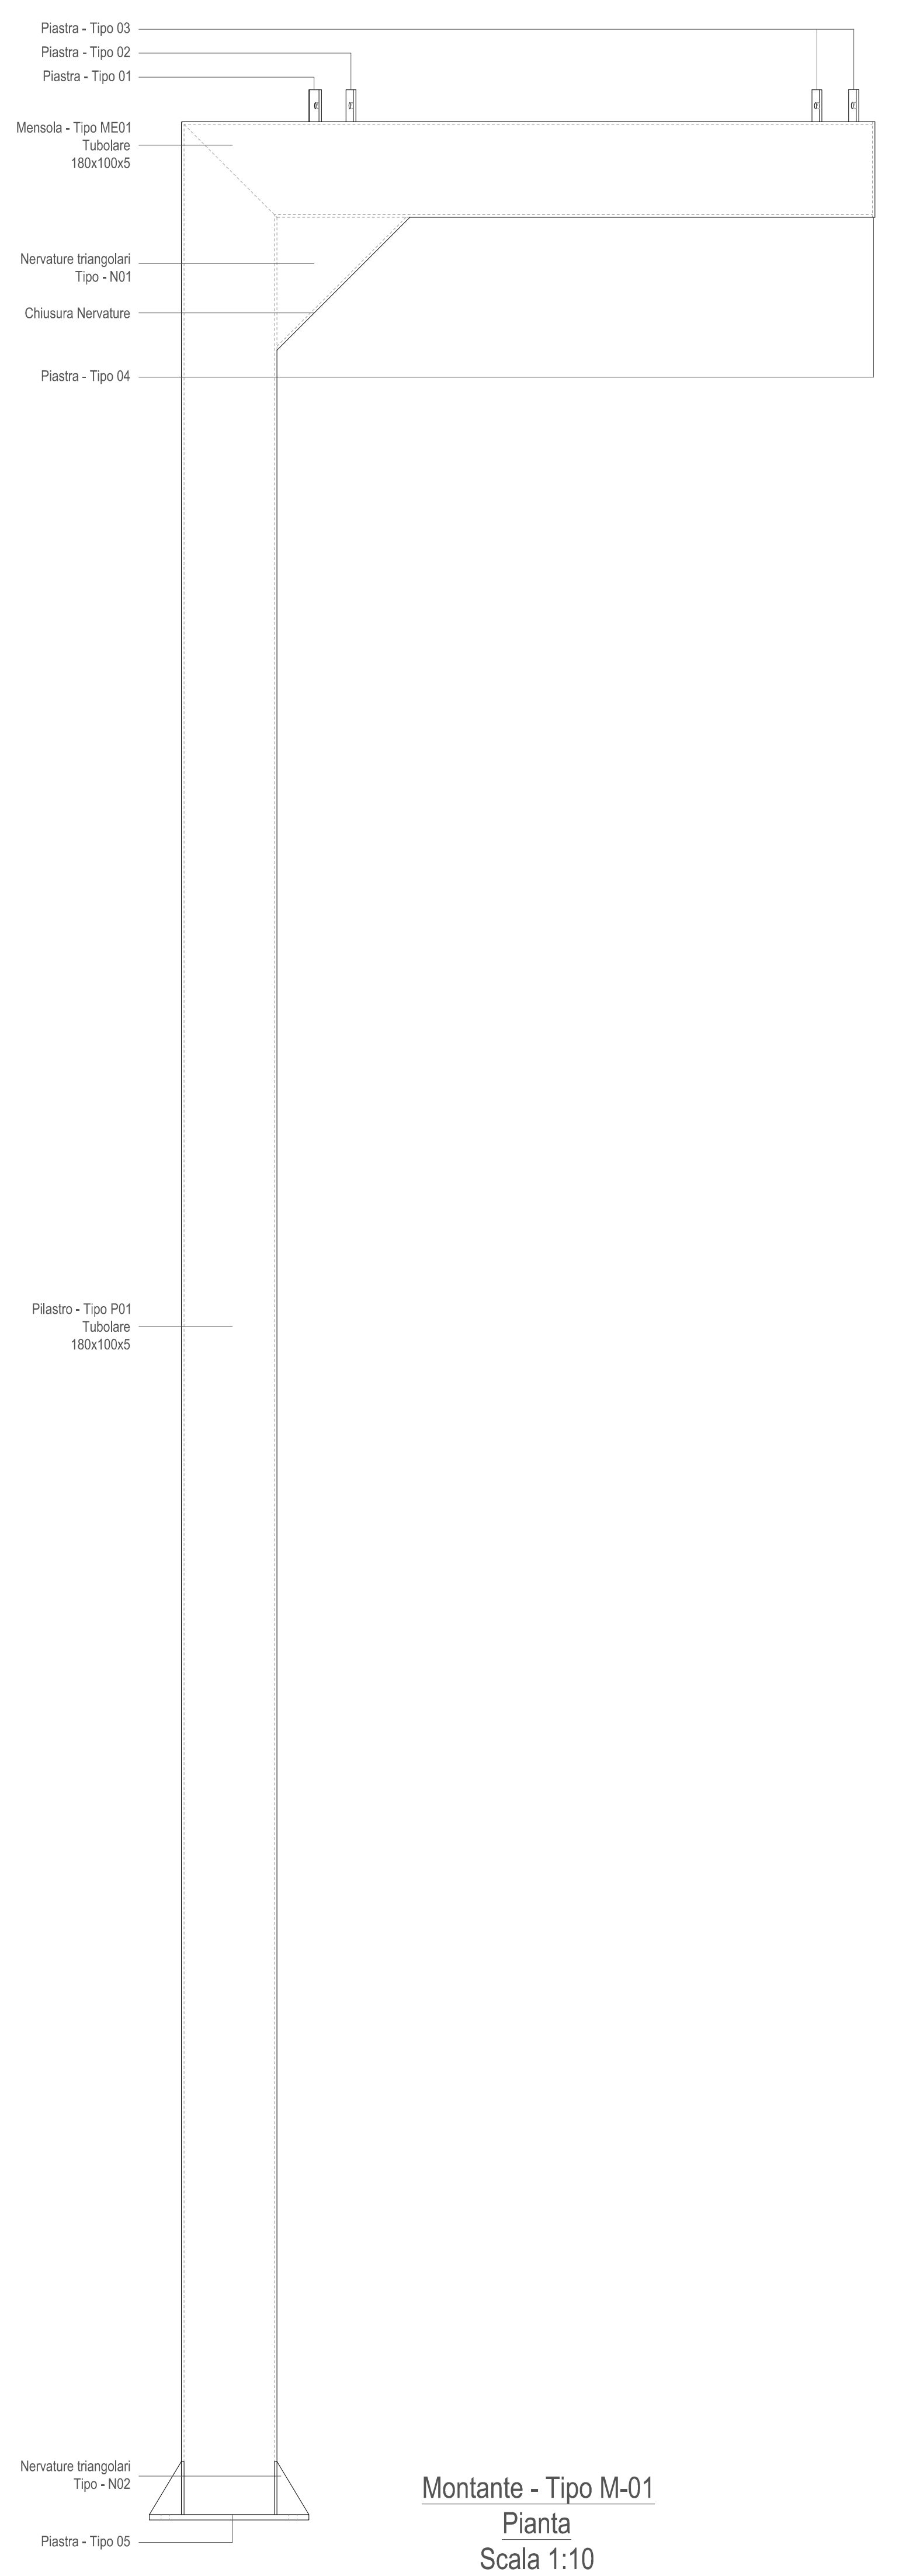
Piastra - Tipo 03
Piastra - Tipo 02
Piastra - Tipo 01
Mensola - Tipo ME01 Tubolare 180x100x5
Nervature triangolari Tipo - N01
Chiusura Nervature
Piastra - Tipo 04
Pilastro - Tipo P01 Tubolare 180x100x5
Nervature triangolari Tipo - N02
Piastra - Tipo 05

Telaio - Tipo A
Scala 1:10
Quantità: n° 11

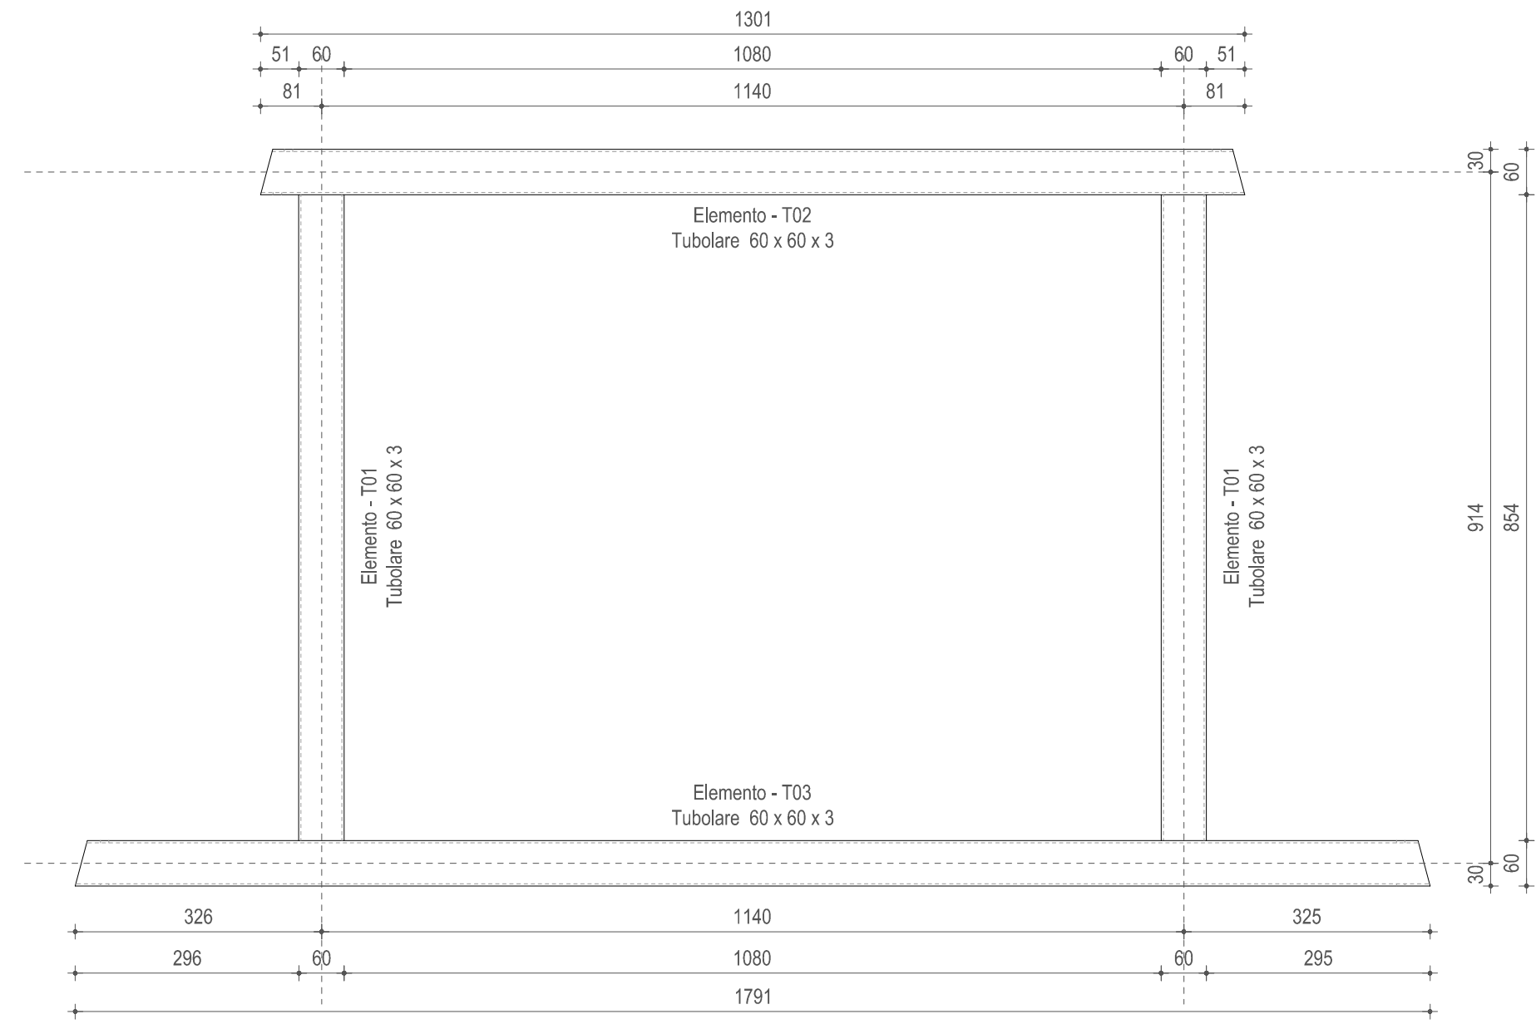
Elemento - T02 Tubolare 60 x 60 x 3
Elemento - T01 Tubolare 60 x 60 x 3
Elemento - T03 Tubolare 60 x 60 x 3
1301
1080
1140
1791
326
296
325
295
914
854
974

Telaio - Tipo B
Scala 1:10
Quantità: n°1

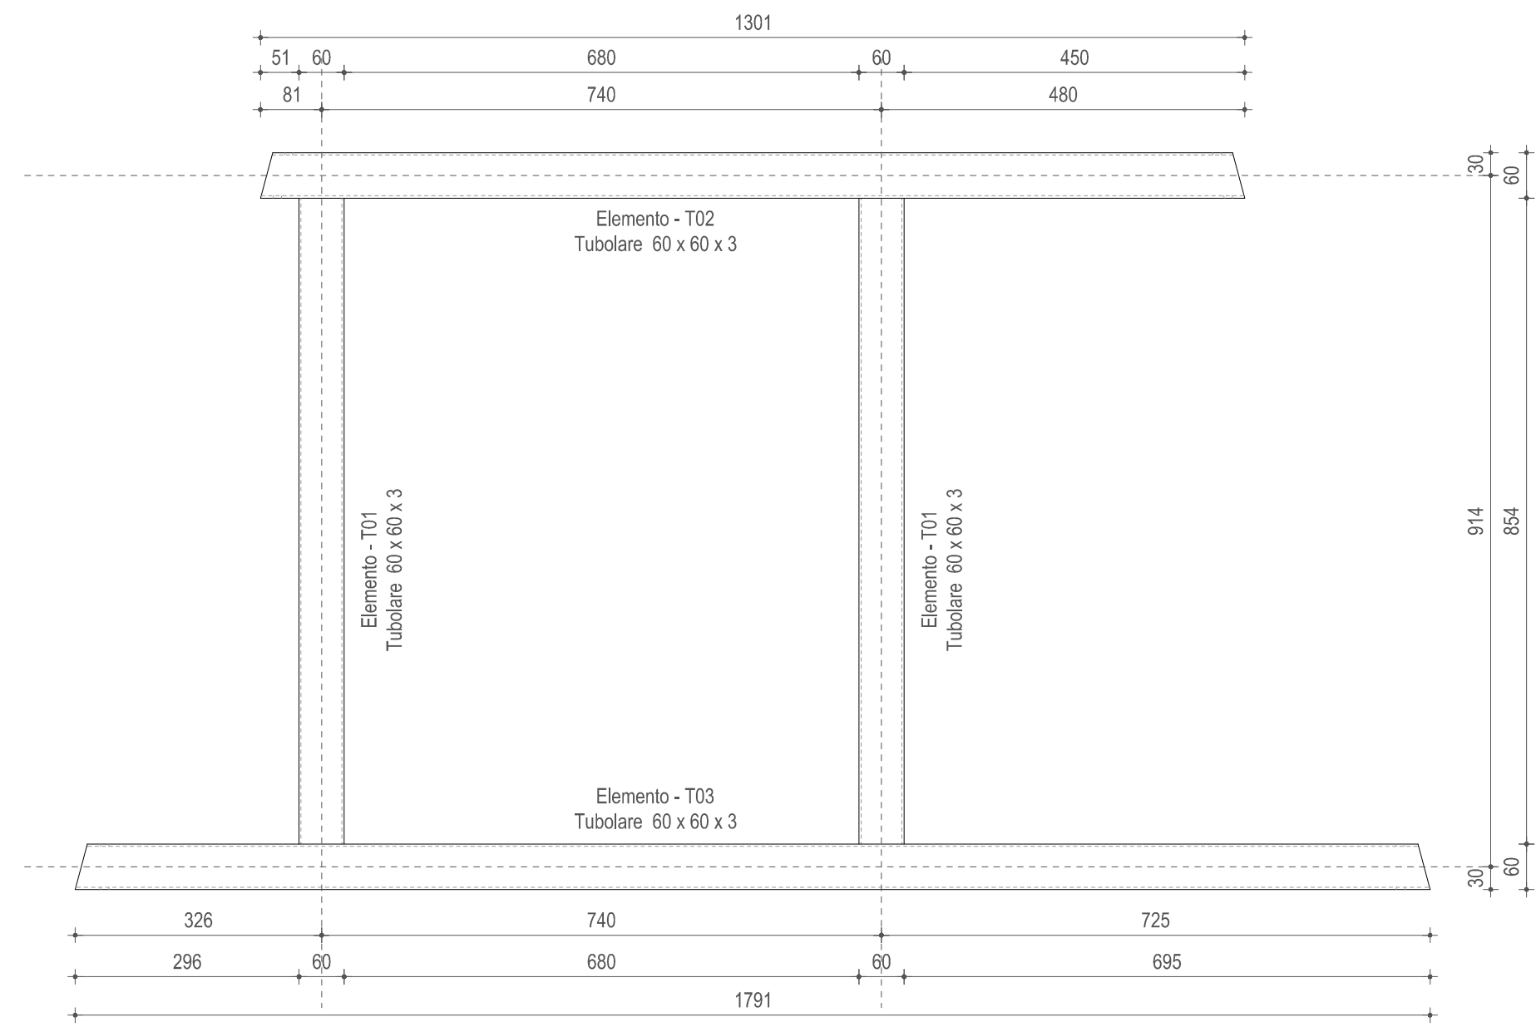
Elemento - T02 Tubolare 60 x 60 x 3
Elemento - T01 Tubolare 60 x 60 x 3
Elemento - T03 Tubolare 60 x 60 x 3
1301
680
450
740
480
326
725
296
695
1791
914
854
974

Spessore
Tipo - S01
Scala 1:1

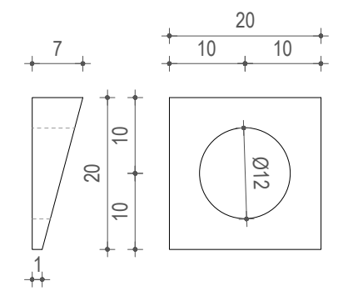

Nervatura Triangolare
Tipo - N01
Scala 1:5
S=5mm

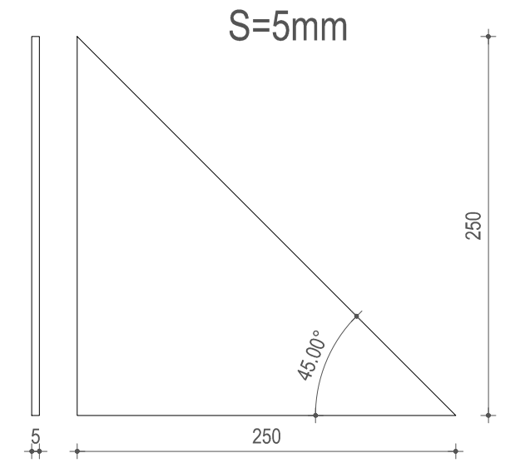

Nervatura Triangolare
Tipo - N02
Scala 1:2
S=5mm

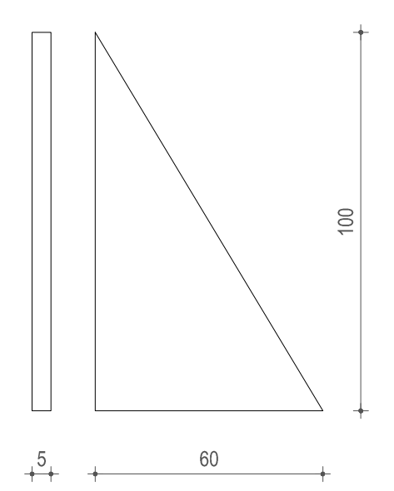

Particolare Base
Montante Tipo M-01
Scala 1:5

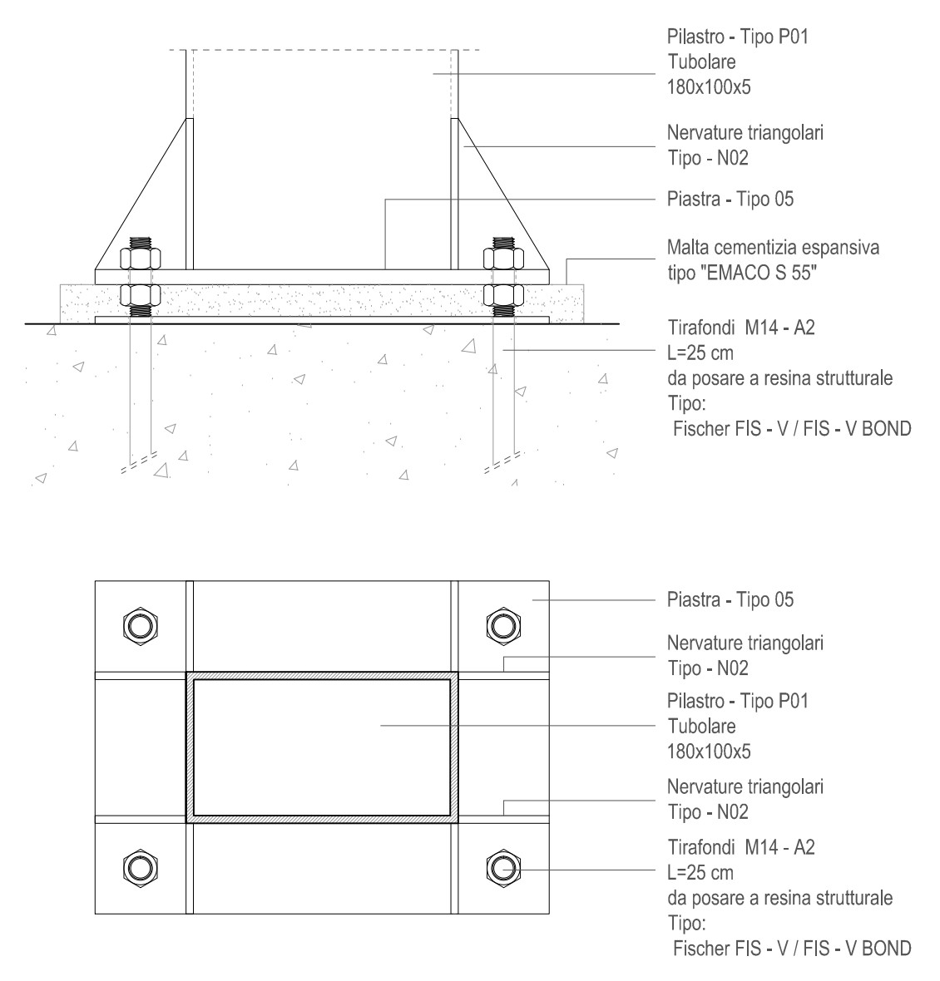
Pilastro - Tipo P01 Tubolare 180x100x5
Nervature triangolari Tipo - N02
Piastra - Tipo 05
Malta cementizia espansiva tipo "EMACO S 55"
Tirafondi M14 - A2 L=25 cm da posare a resina strutturale Tipo: Fischer FIS - V / FIS - V BOND

Particolare - Nodo B
Scala 1:5

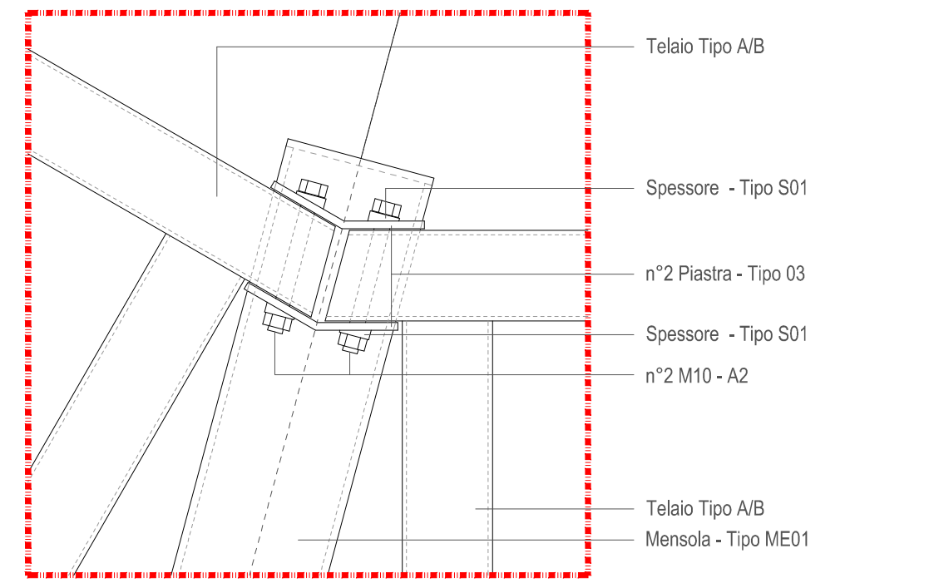

Particolare - Nodo A
Scala 1:5

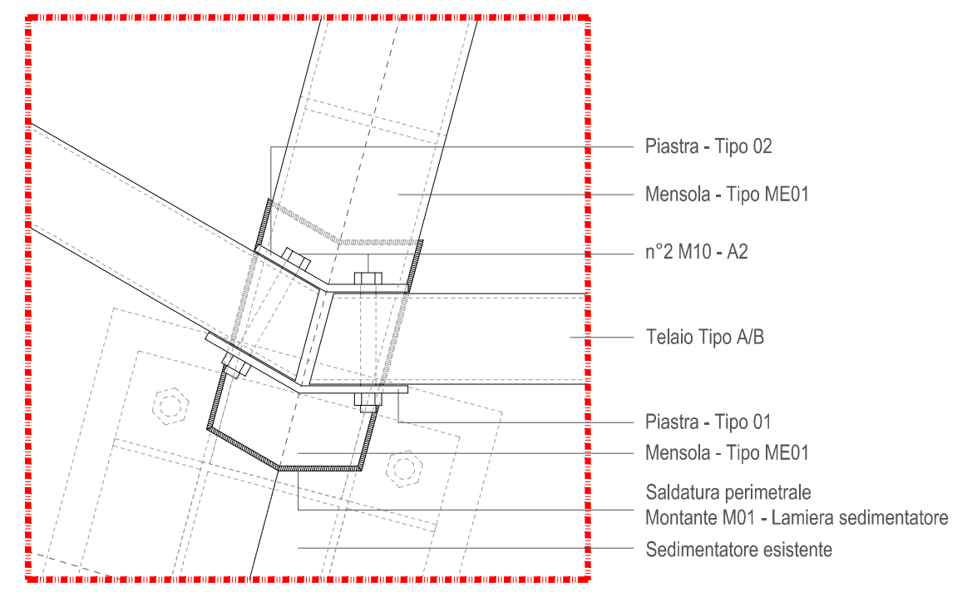

Distinta Pilastro - Tipo P01
Scala 1:10

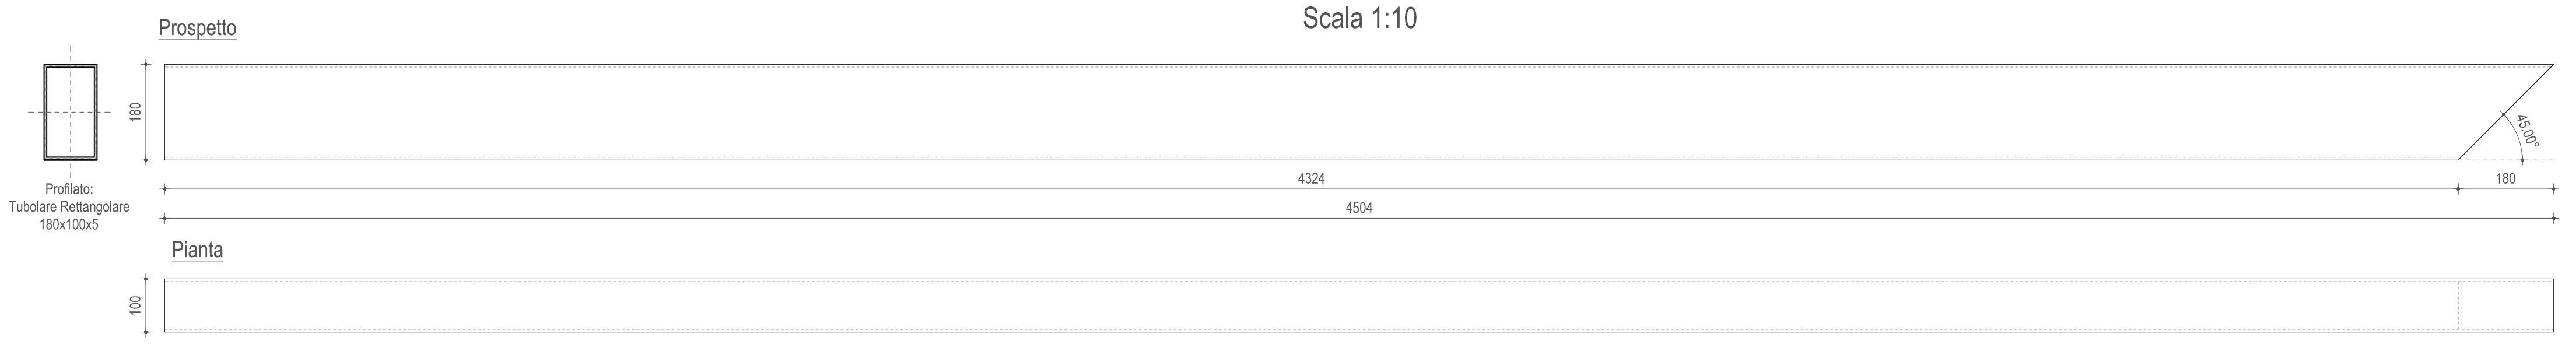

Distinta Mensola - Tipo ME01
Scala 1:10

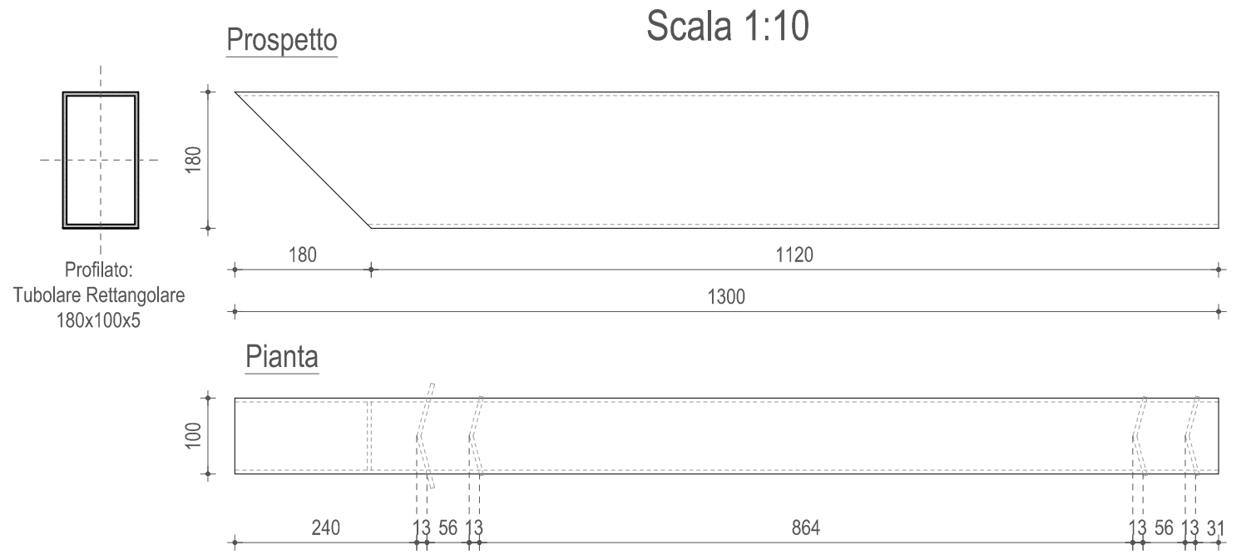

Piastra - Tipo 04
Scala 1:5

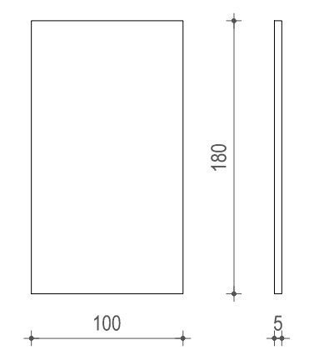

Piastra - Tipo 01
Scala 1:2

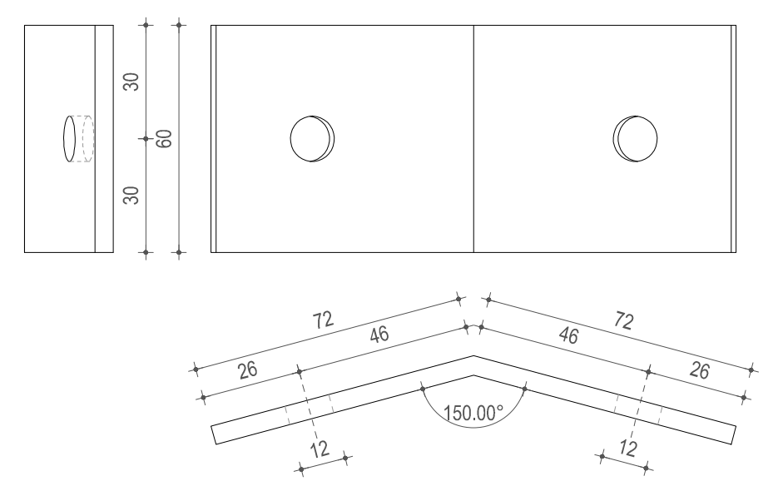

Piastra - Tipo 02
Scala 1:2

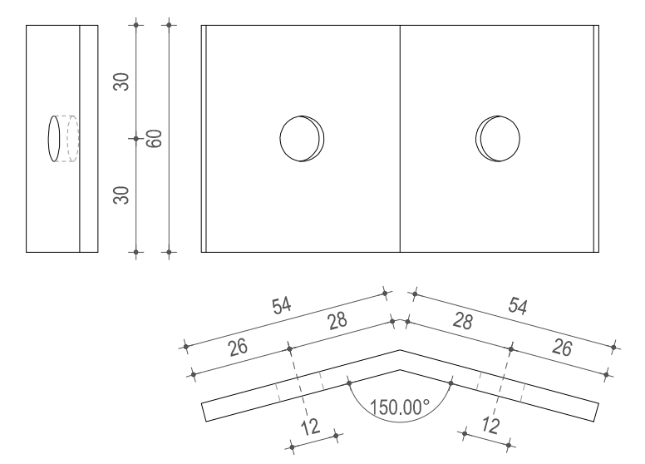

Piastra - Tipo 03
Scala 1:2

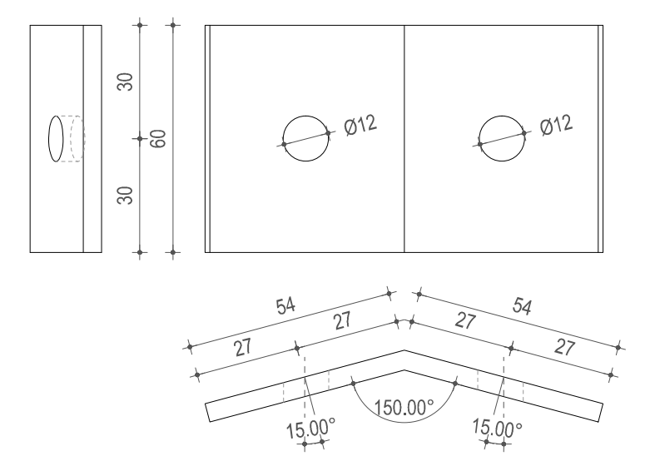

Piastra - Tipo 05
Scala 1:5
S=10mm

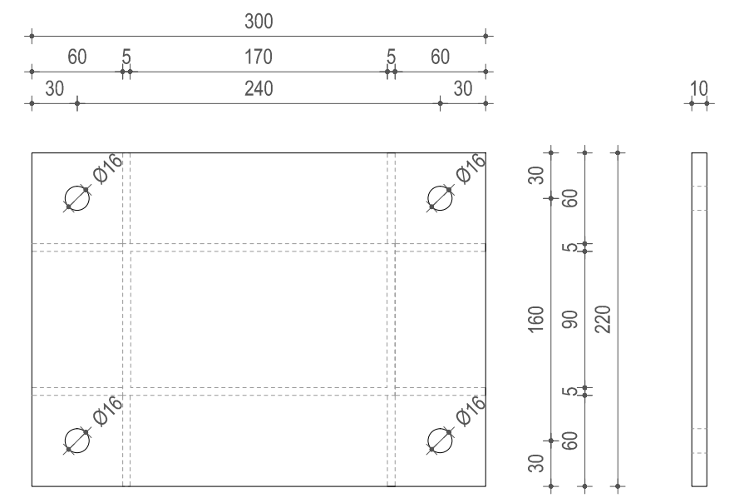

Montante - Tipo M-01
Pianta
Scala 1:10

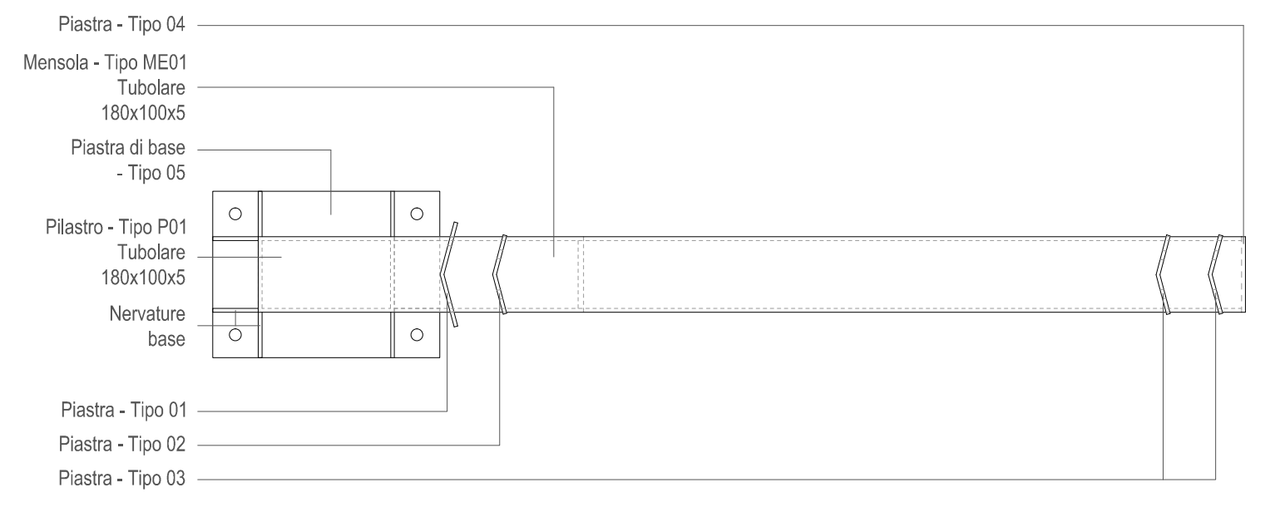
Piastra - Tipo 04
Mensola - Tipo ME01 Tubolare 180x100x5
Piastra di base - Tipo 05
Pilastro - Tipo P01 Tubolare 180x100x5
Nervature base
Piastra - Tipo 01
Piastra - Tipo 02
Piastra - Tipo 03

Elemento - T01: Tubolare 60 x 60 x 3 - L=854 mm

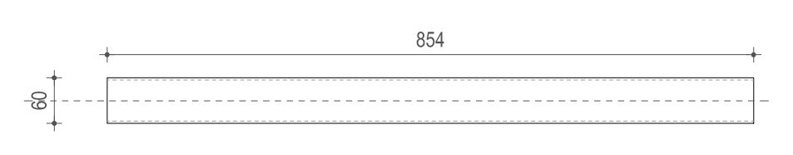

Elemento - T02: Tubolare 60 x 60 x 3 - L=1301 mm

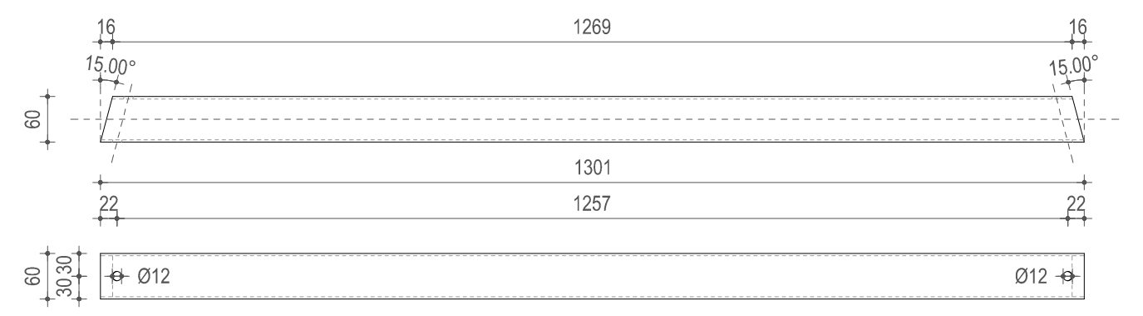

Elemento - T03: Tubolare 60 x 60 x 3 - L=1791 mm