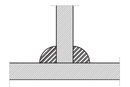
MATERIALI E PRESCRIZIONI

MATERIALI PRESCRITTI:

Acciaio (Secondo UNI EN 10025-2:2004)
Tipologia
S275JR
Caratteristiche meccaniche
S275JR
Tensione di snervamento (T ambiente): Spessore nominale >3≤16 mm f_{yk} = 275 N/mm²
Tensione di rottura (T ambiente): Spessore nominale >3 ≤ 16 mm f_{tk} = 410-560 N/mm²
Deformazione massima a rottura (T ambiente): Spessore nominale >3 ≤ 40 mm A% = 23%
Resilienza: T=20°C Spessore nominale <150 mm Resilienza=27J

Bulloni
Tipologia
Ad alta resistenza: Classe 8.8
Caratteristiche meccaniche $f_{yb} \leq 649$ N/mm²
$f_{tb} \leq 800$ N/mm²

Saldature
Tipologia
Giunto: Ad angolo (A)
Testa a Testa (T-T)
Dimensione


S1≥S2
l=S2
a=0,71xS2


S1≥S2
l=S2
a=0,5xS2

Criteri di accettabilità (UNI EN ISO 5817:2008)
Livello di qualità: C

COMUNE DI PORTO MANTOVANO PROVINCIA DI MANTOVA

Oggetto
[redacted]

Committente
[redacted]

Oggetto tavola
- Fondazioni

Tav. n°
U


Variante

Data
14/08/2019


Scale
1:50 - 1:25 - 1:10

Progettista
[redacted]


PIANTA FILI FISSI
Scala 1:50

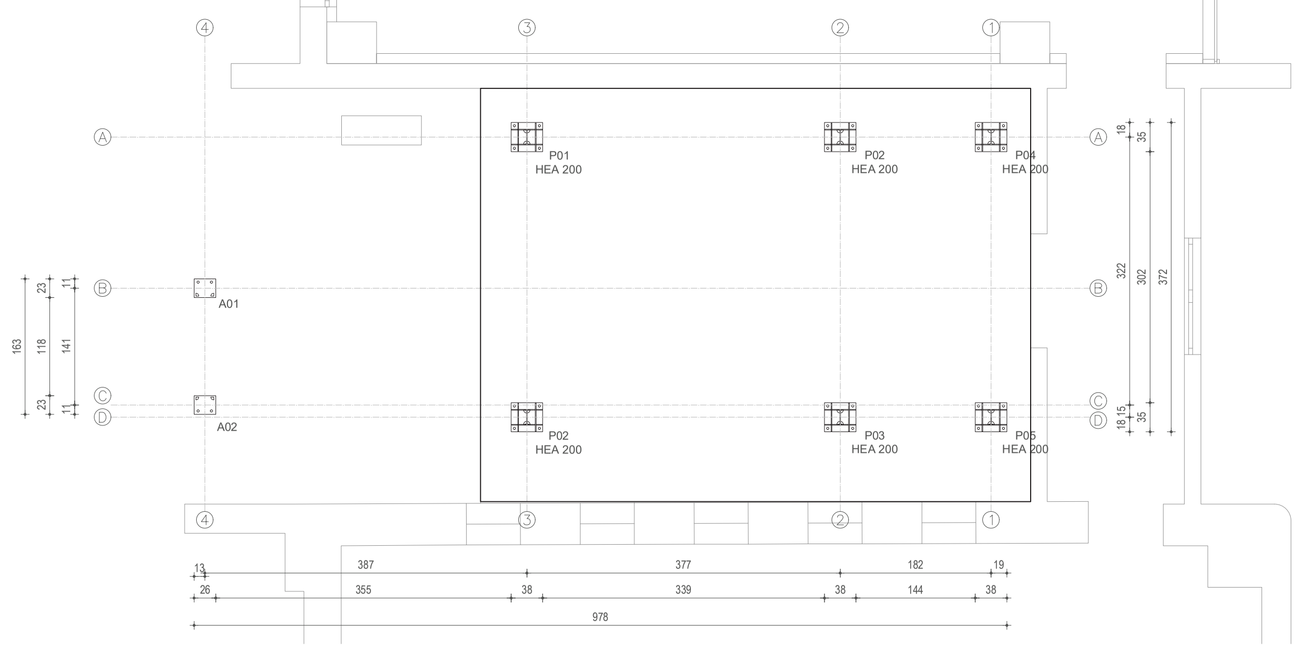


PIANTA 1°P - 2°P
Pianerottolo 2 e 3
Scala 1:50

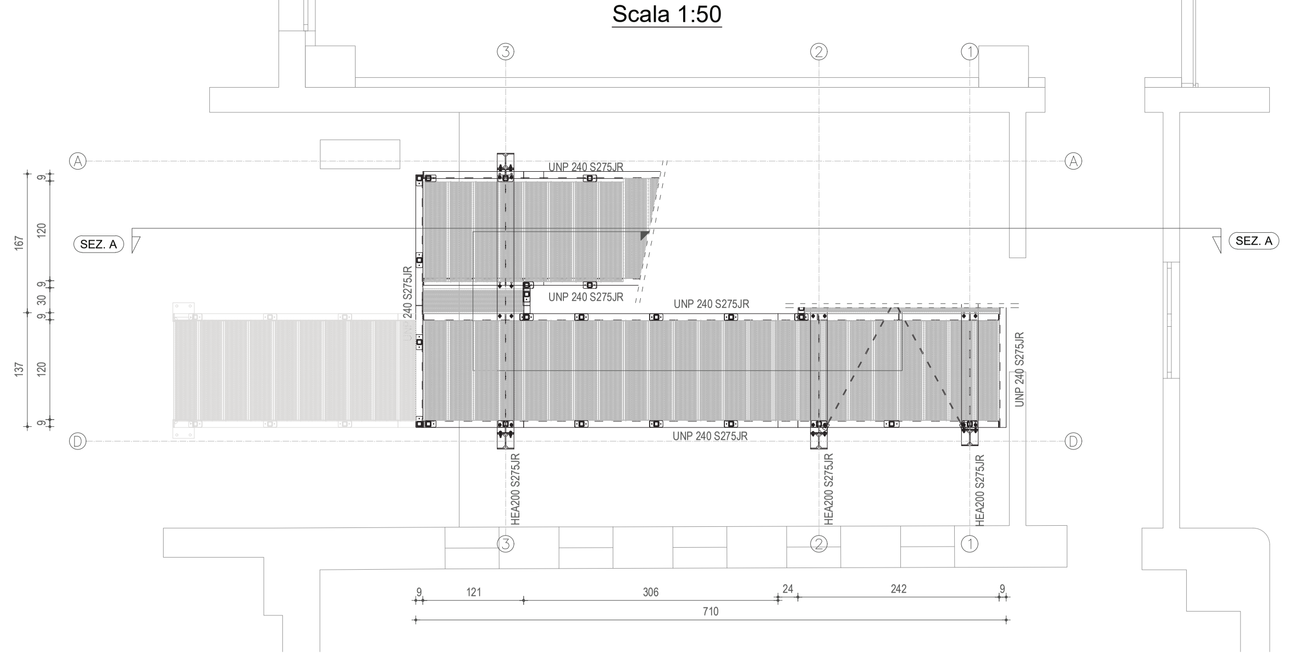


PIANTA PT - 1°P
Pianerottolo 1 e 2
Scala 1:50

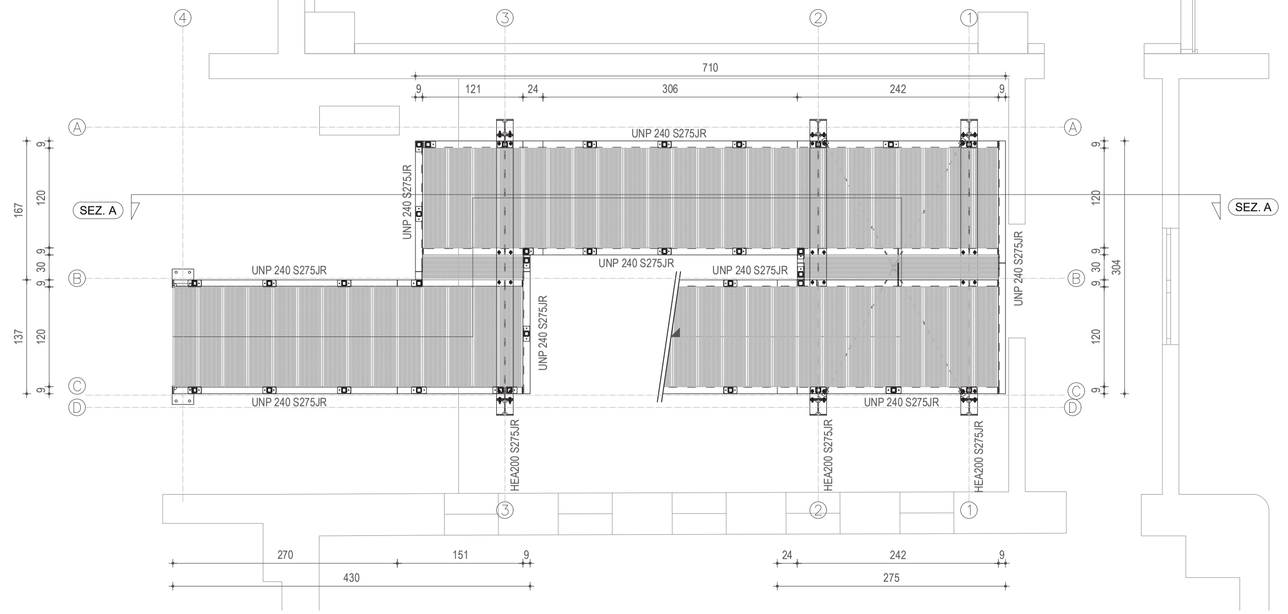


PIANTA 2°P - 3°P
Pianerottolo 3 e 4
Scala 1:50

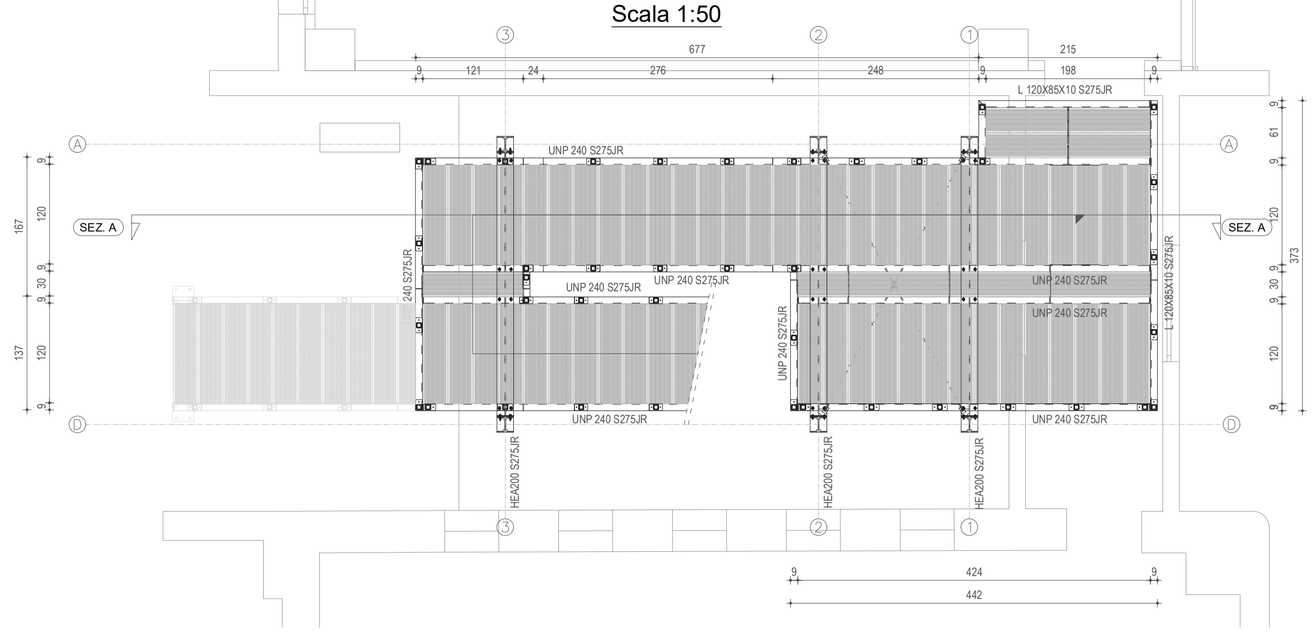


SEZIONE A-A
Scala 1:50

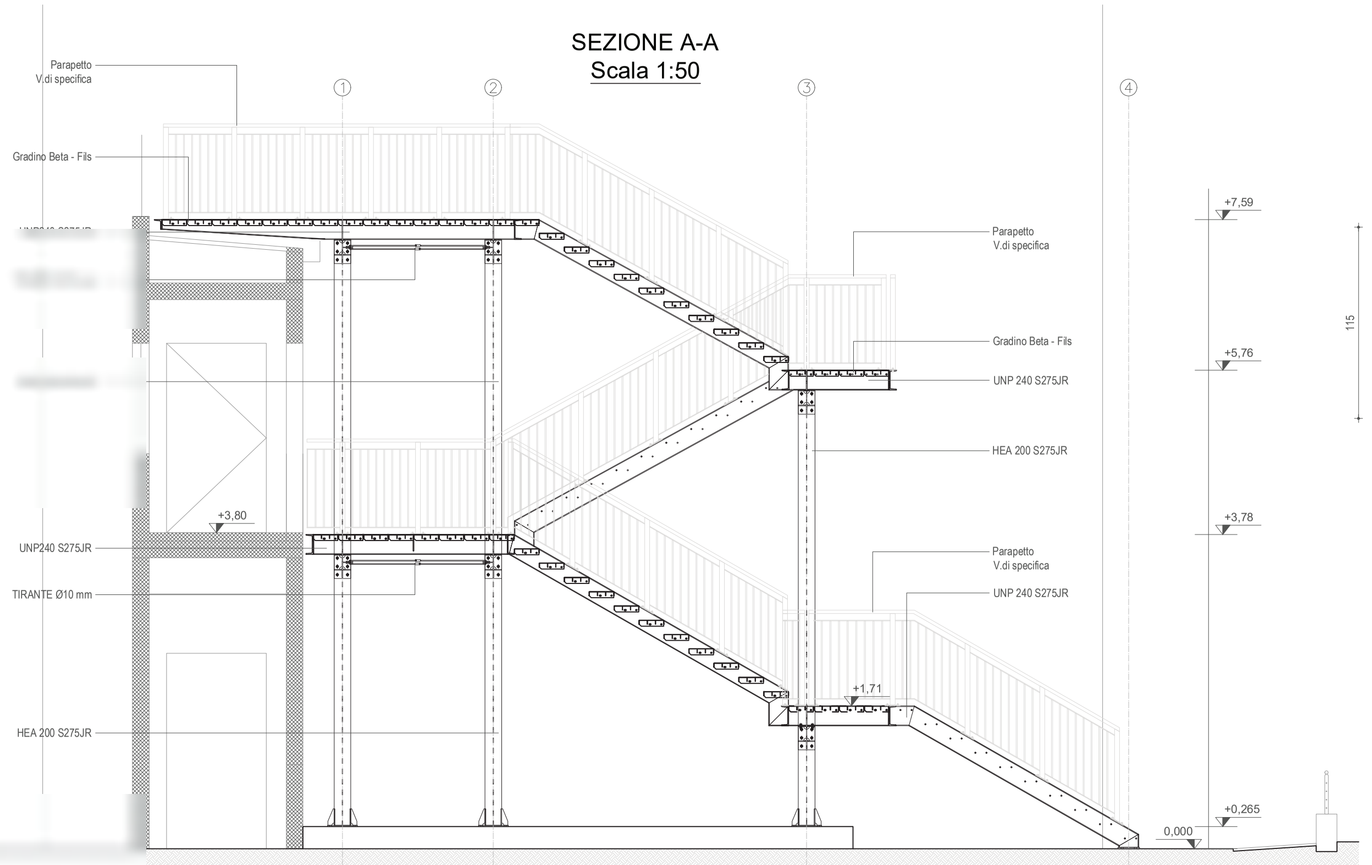


PARAPETTO
Fronte
Scala 1:25

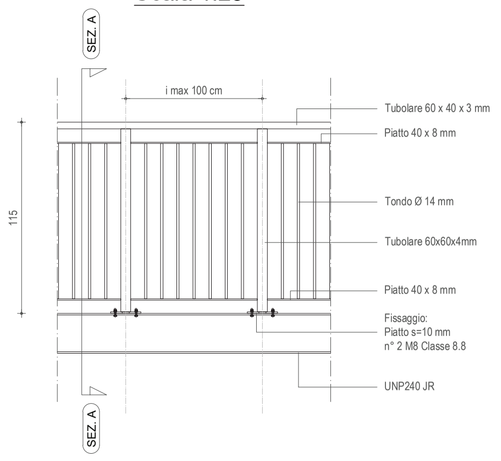


PARAPETTO
Fronte
Scala 1:25

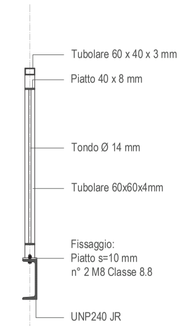

PIASTRA DI BASE UNP 240
Scala 1:10

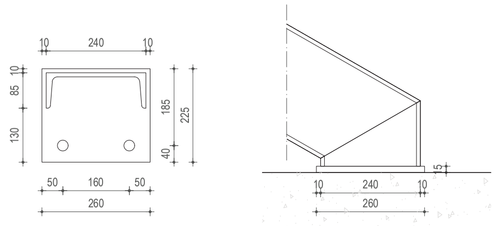


PIASTRA DI BASE HEA 200
Scala 1:10

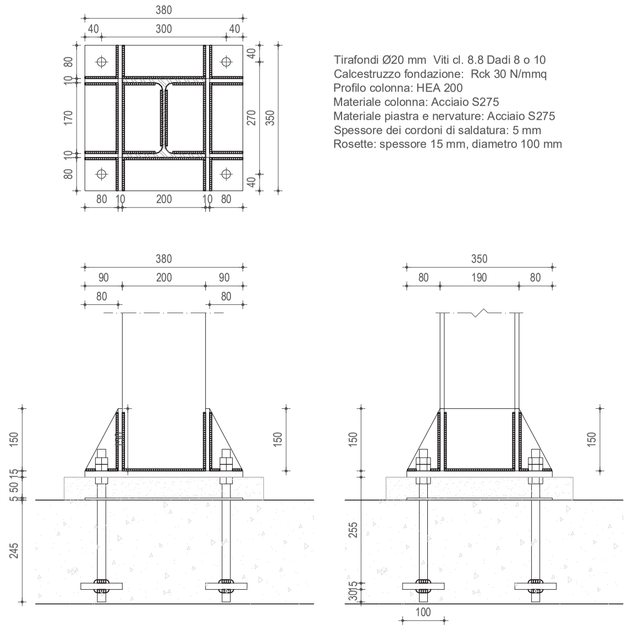


Tirafondi Ø20 mm Viti cl. 8.8 Dadi 8 o 10
Calcestruzzo fondazione: Rck 30 N/mmq
Profilo colonna: HEA 200
Materiale colonna: Acciaio S275
Materiale piastra e nervature: Acciaio S275
Spessore dei cordoni di saldatura: 5 mm
Rosette: spessore 15 mm, diametro 100 mm

Pianta ancoraggio

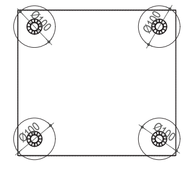

NODO HEA 200 - UNP240
Scala 1:10

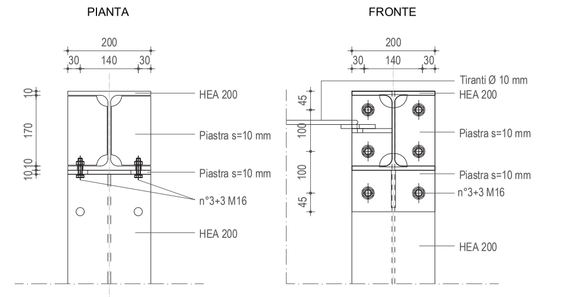

NODO HEA 200 - UNP240
Scala 1:10

