


Trave continua -TC 01- Sezione trasversale
Scala 1:25

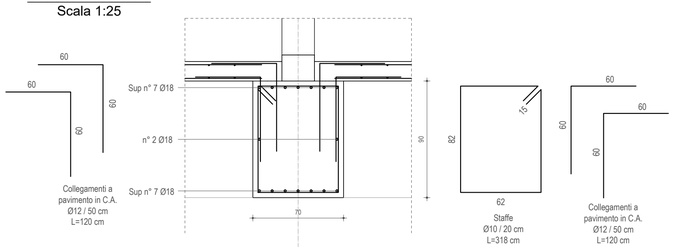

Trave continua -TC 01- Collegamento a TR01
Scala 1:25

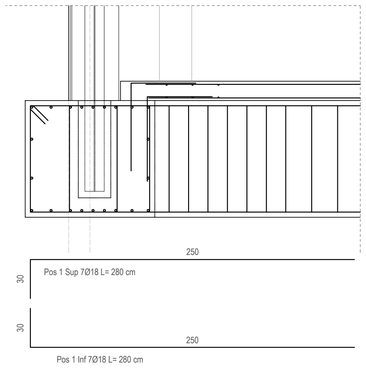

PIANTA FONDAZIONI Scala 1:50

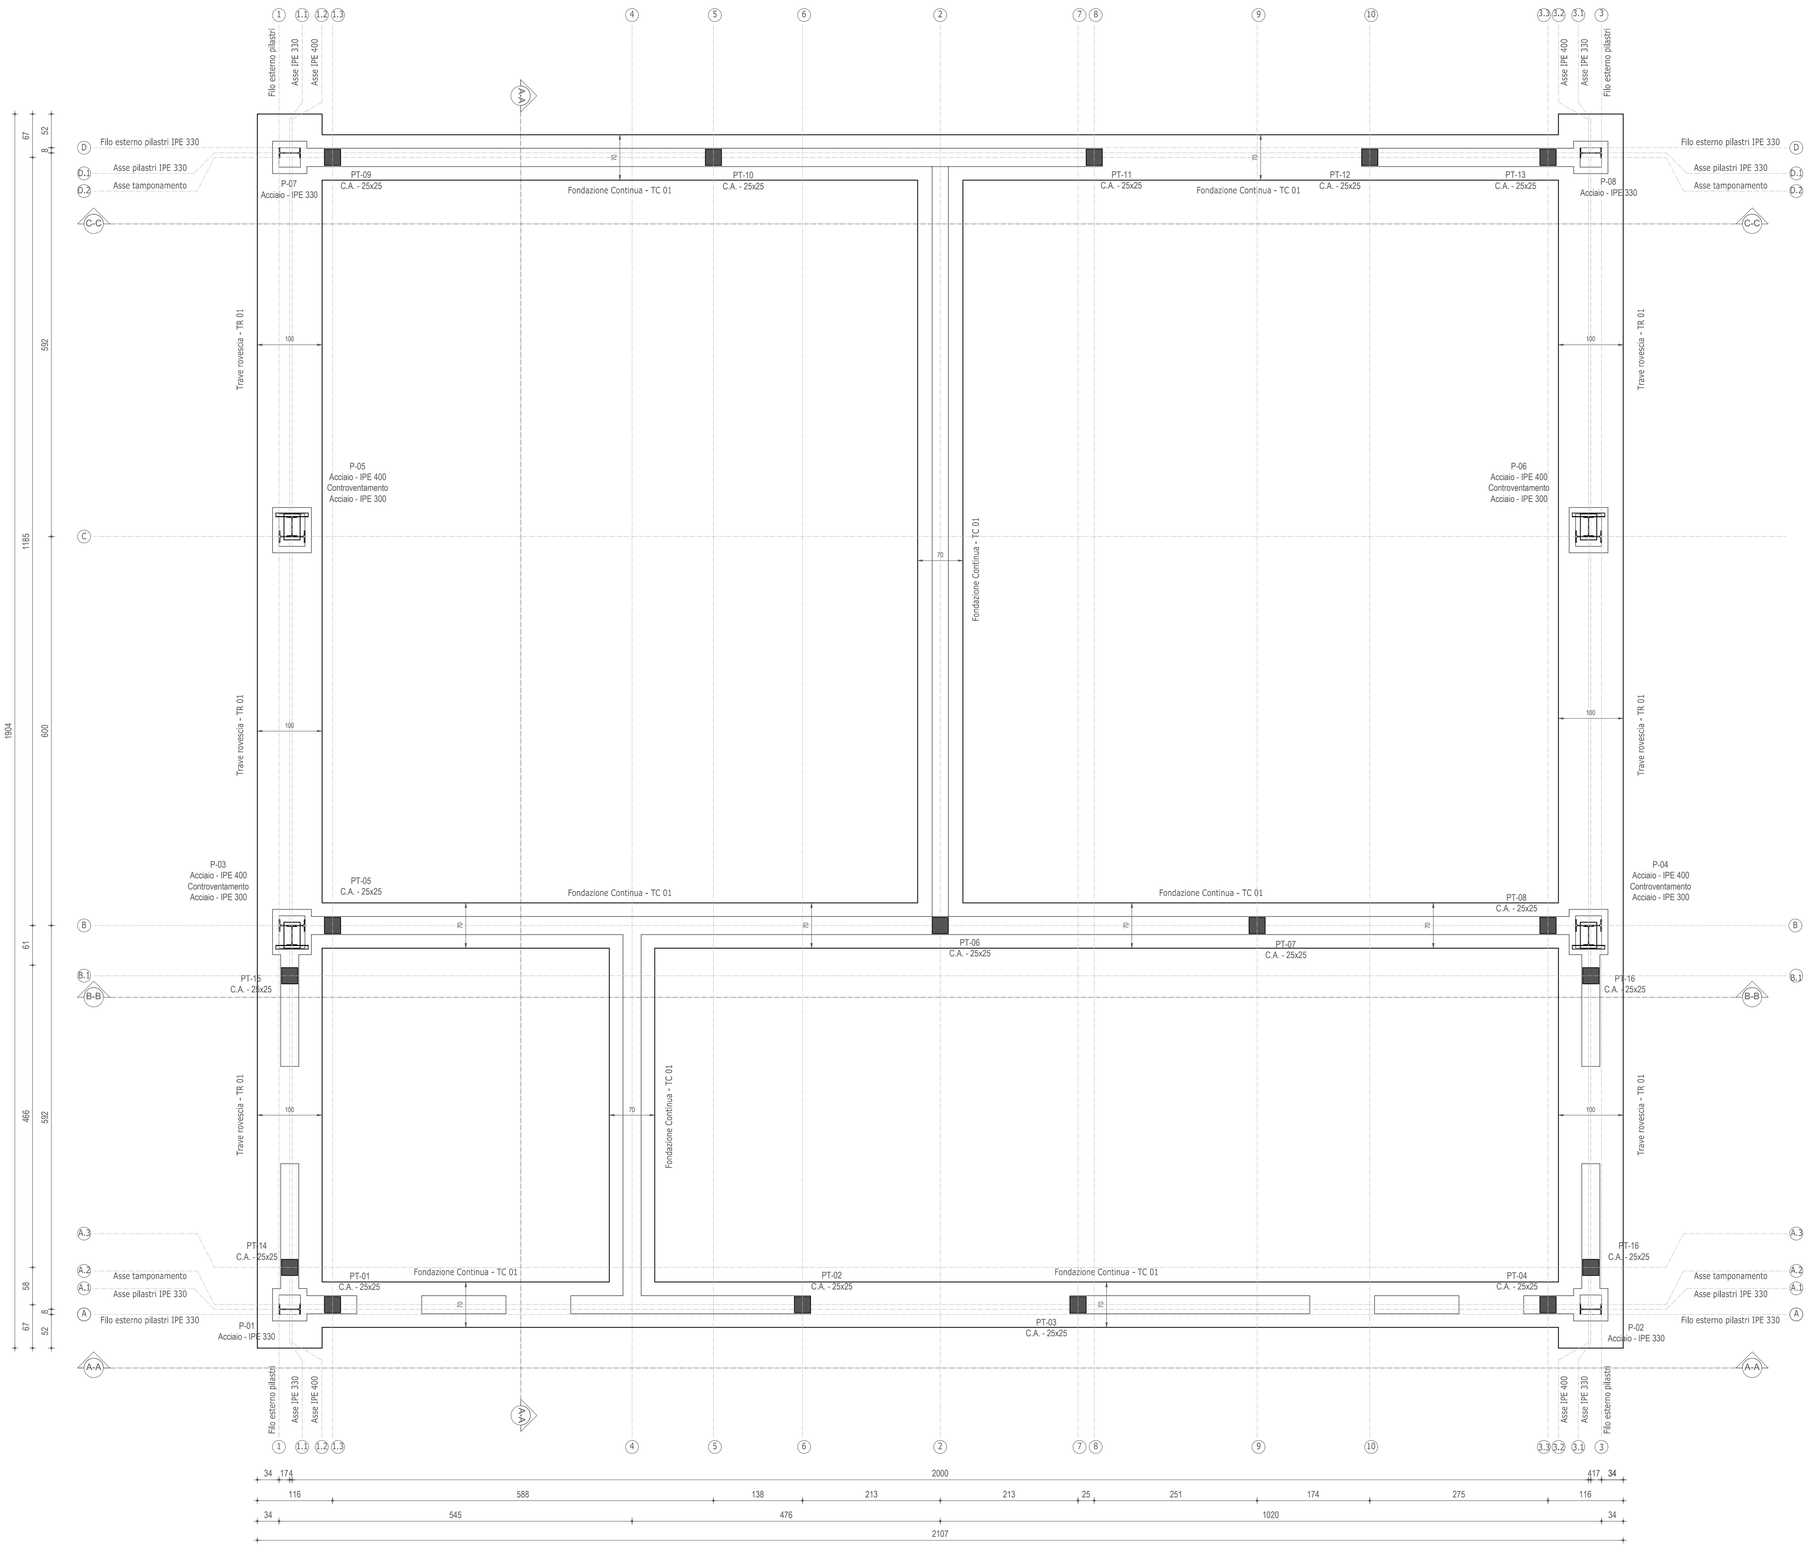

MATERIALI E PRESCRIZIONI

CALCESTRUZZO	FONDAZIONI MURI CONTRO TERRA	TRAVI - SOLETTE POGGIOLI - SCALE	PILASTRI-SETTI NUCLEI ASCENSORE
CLASSE DI RESISTENZA	C 25/30 R ck= 30 MPa	C 25/30 R ck= 30 MPa	C 25/30 R ck= 30 MPa
CLASSE DI ESPOSIZIONE	XC2	XC1	XC1
CLASSE DI CONSISTENZA (Slump)	S4	S4	S4
DIAMETRO MAX AGGREGATI	32 mm	22 mm	22 mm

ACCIAIO PER ARMATURE LENTE (6<Ø<40 mm)	TIPO	f yk	f tk	f yd
	B450C	> 450 MPa	> 540 MPa	> 391 MPa

ACCIAIO PER RETI ELETTROSALDATE (5<Ø<10 mm)	TIPO	f yk	f tk	f yd
	B450A	> 450 MPa	> 540 MPa	> 391 MPa

COPRIFERRO NOMINALE C nom			Chiusura staffe	Ancoraggio barre
C nom	FONDAZIONI	40 mm	10 x Ø, 135°	10 x Ø
	MURI CONTRO TERRA			
	TRAVI - SOLETTE	30 mm		Sovrapposizione barre
	POGGIOLI - SCALE			60 x Ø
	PILASTRI - SETTI NUCLEI ASCENSORE	30 mm		

DIAMETRO BARRA	Ø < 12	12 < Ø < 16	16 < Ø < 25	25 < Ø < 40
DIAMETRO DEL MANDRINO	4 x Ø	5 x Ø	8 x Ø	10 x Ø

COMUNE DI MARMIROLO — PROVINCIA DI MANTOVA

Oggetto

[redacted]

[redacted]

PROGETTO STRUTTURE

Oggetto tavola
- Fondazioni

Tav. n° 01

Revisione 00


Data

Scale 1:50 - 1:25


Progettista

[redacted]


Trave rovescia -TR 01- Scala 1:50

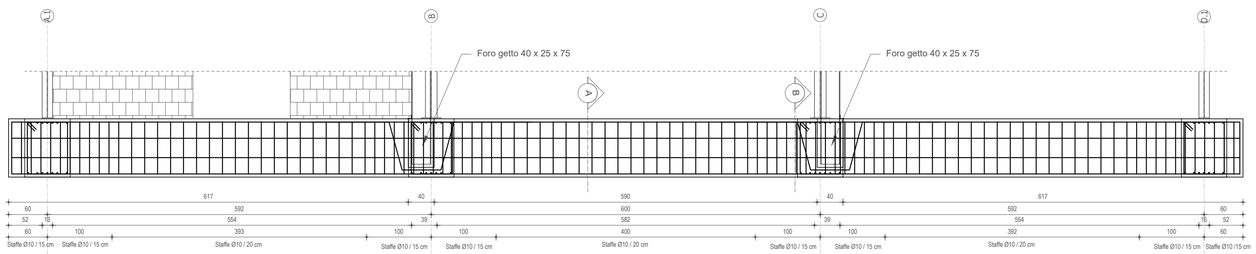

Distinta ferri

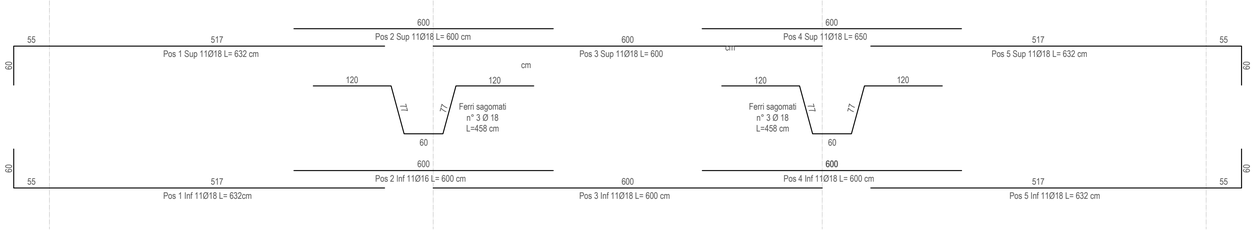

Trave rovescia -TR 01- Sezione A
Scala 1:25

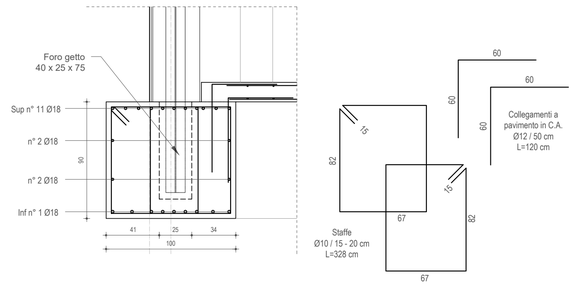

Trave rovescia -TR 01- Sezione B
Scala 1:25

