


PIANTA TAMPONAMENTI Scala 1:50

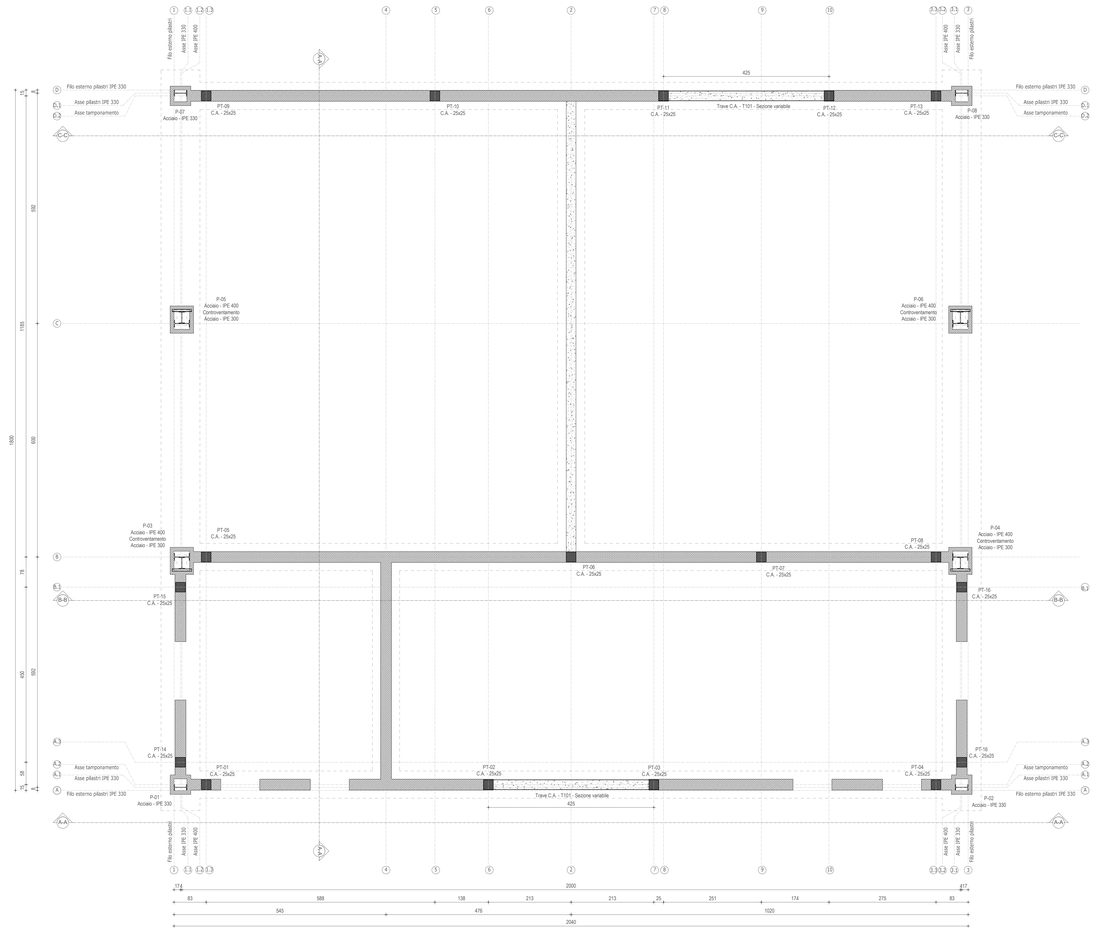


SEZIONE A-A Scala 1:50

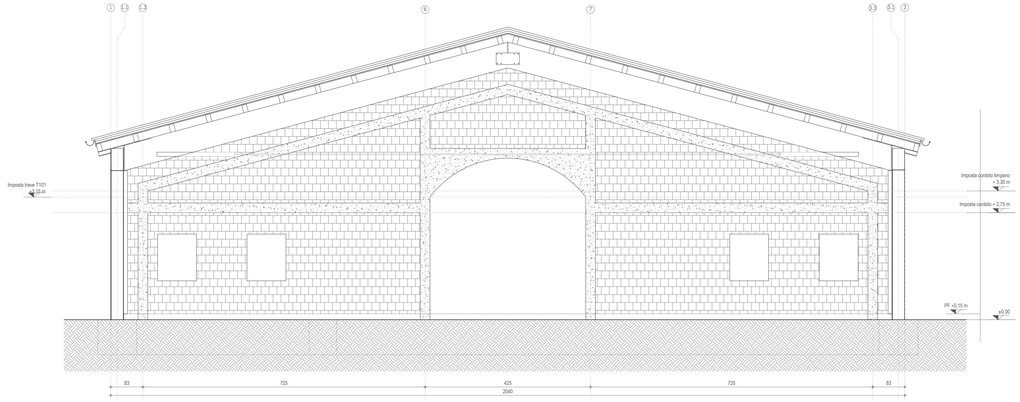

SEZIONE B-B Scala 1:50

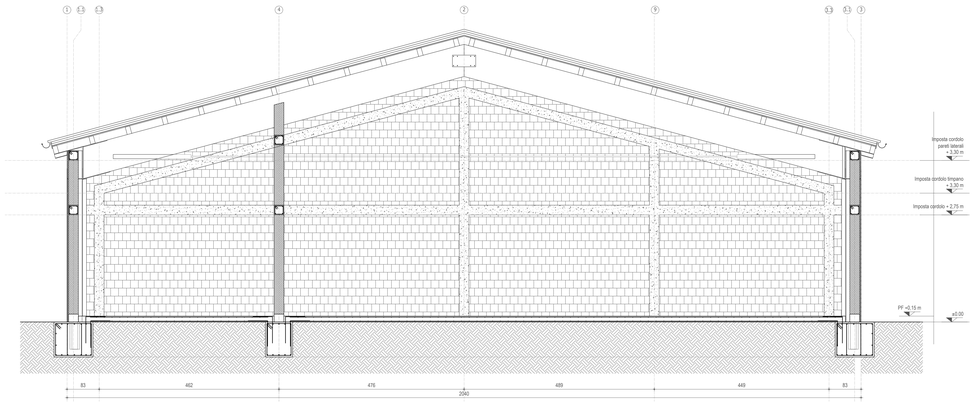

SEZIONE C-C Scala 1:50

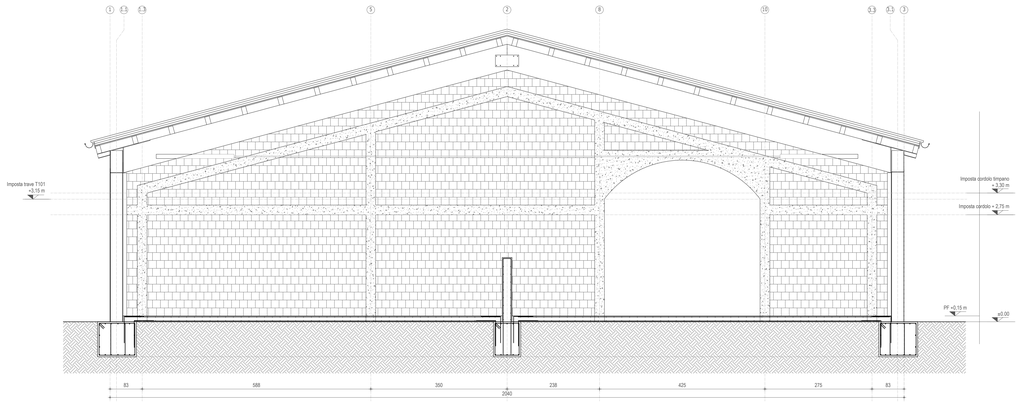


MATERIALI E PRESCRIZIONI

CALCESTRUZZO	FONDAZIONI MURI CONTRO TERRA	TRAVI - SOLETTE POGGIOLI - SCALE	PILASTRI-SETTI NUCLEI ASCENSORE
CLASSE DI RESISTENZA	C 25/30 R ck= 30 MPa	C 25/30 R ck= 30 MPa	C 25/30 R ck= 30 MPa
CLASSE DI ESPOSIZIONE	XC2	XC1	XC1
CLASSE DI CONSISTENZA (Slump)	S4	S4	S4
DIAMETRO MAX AGGREGATI	32 mm	22 mm	22 mm

ACCIAIO PER ARMATURE LENTE (6<Ø<40 mm)	TIPO	f yk	f tk	f yd
	B450C	> 450 MPa	> 540 MPa	> 391 MPa

ACCIAIO PER RETI ELETTROSALDATE (5<Ø<10 mm)	TIPO	f yk	f tk	f yd
	B450A	> 450 MPa	> 540 MPa	> 391 MPa

COPRIFERRO NOMINALE C nom

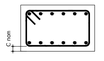

FONDAZIONI MURI CONTRO TERRA	40 mm	
TRAVI - SOLETTE	30 mm	
POGGIOLI - SCALE		
PILASTRI - SETTI	30 mm	
NUCLEI ASCENSORE		

Chiusura staffe



Ancoraggio barre



Sovrapposizione barre



DIAMETRO BARRA	Ø < 12	12 < Ø < 16	16 < Ø < 25	25 < Ø < 40
DIAMETRO DEL MANDRINO	4 x Ø	5 x Ø	8 x Ø	10 x Ø

COMUNE DI MARMIROLO PROVINCIA DI MANTOVA

Oggetto

[redacted]

Committente

[redacted]

PROGETTO STRUTTURE

Oggetto tavola
- Tamponature

Tav. n° 02

Revisione 00


Data

Scale 1:50 - 1:25


Progettista

[redacted]

Trave T 101
Scala 1:25

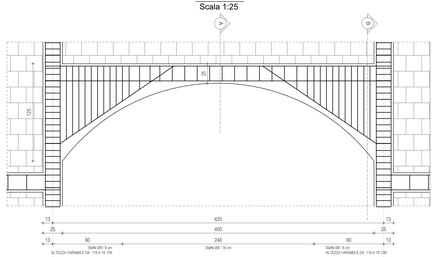


Distinta ferri

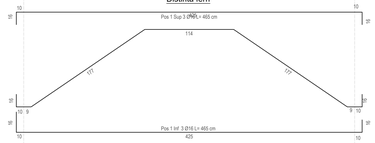


Sezione A-A
Scala 1:25




Sezione B-B
Scala 1:25

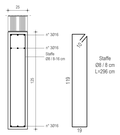


Distinta chiamate pilastri irrigidimento
Scala 1:25

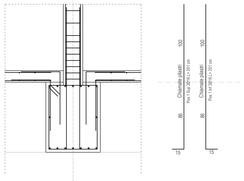

Particolare cordolo
Scala 1:25

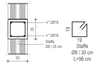

Sezione pilastro irrigidimento
Scala 1:25

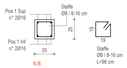

N.B.
Infittire staffe in corrispondenza dei nodi cordolo - pilastro per una lunghezza di 60 cm per ogni lato