

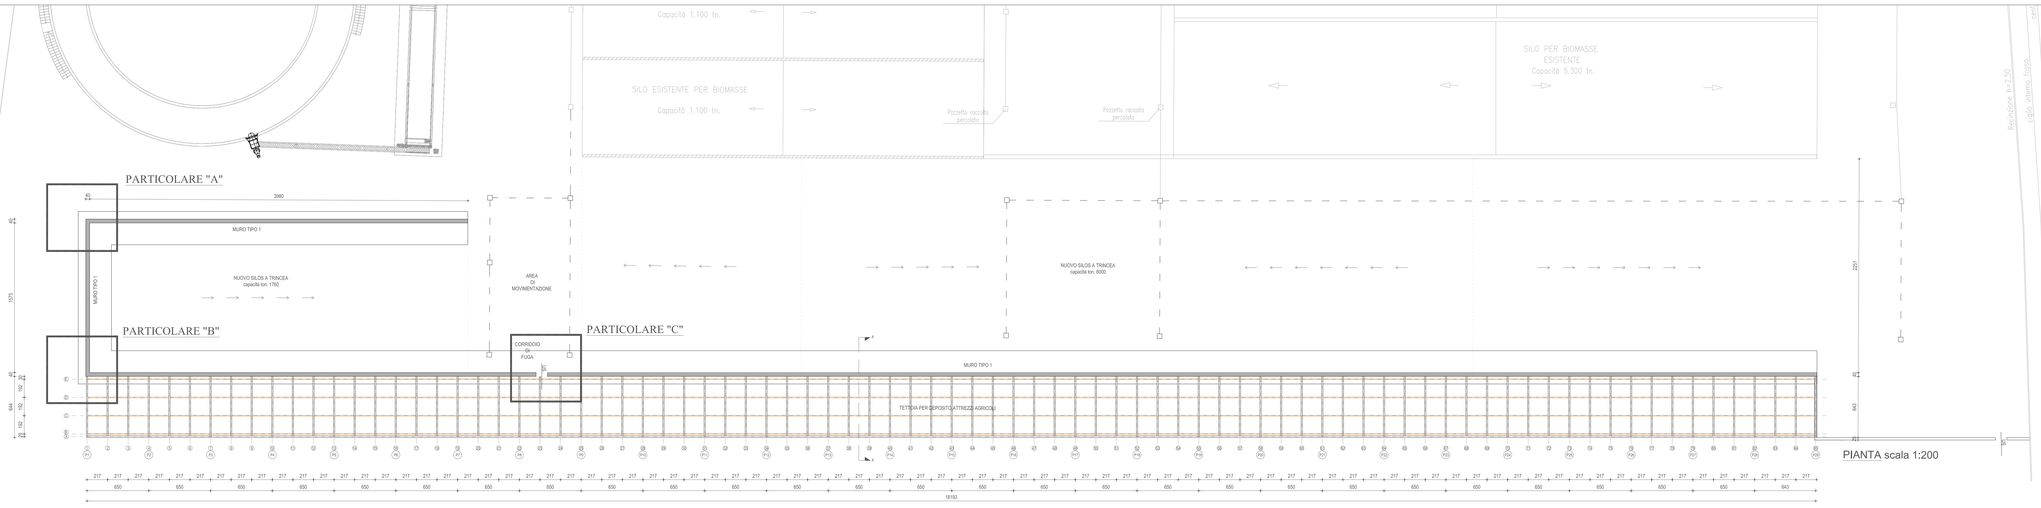



PLANTA scala 1:200

PARTICOLARE "A" scala 1:25

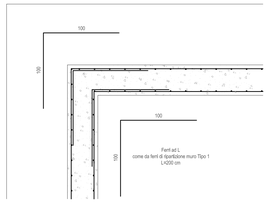


PARTICOLARE "B" scala 1:25

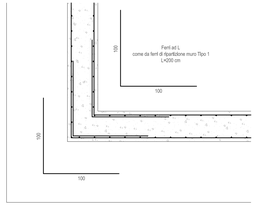

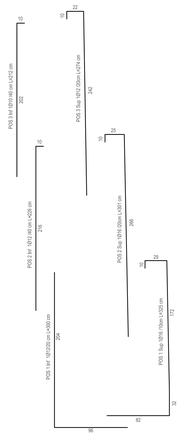

MURO TIPO 1 H=5m
scala 1:25

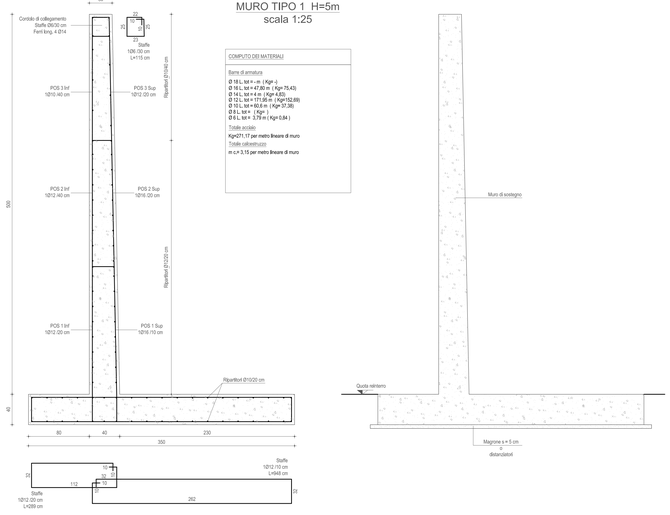

COMPUTO DEI MATERIALI

Barre di armatura


Ø 18 L. tot = -n. (Kg= -)
Ø 16 L. tot = 47.80 m (Kg= 75.43)
Ø 14 L. tot = 4 m (Kg= 4.93)
Ø 12 L. tot = 101.6 m (Kg=152.88)
Ø 10 L. tot = 57.6 m (Kg= 37.58)
Ø 8 L. tot = (Kg=)
Ø 6 L. tot = 3.72 m (Kg= 0.84)

Totale acciaio
Kg=271,17 per metro lineare di muro


Totale calcestruzzo
m.c= 3,15 per metro lineare di muro

PARTICOLARE "C"
ARMATURA APERTURA
scala 1:25

PROSPETTO

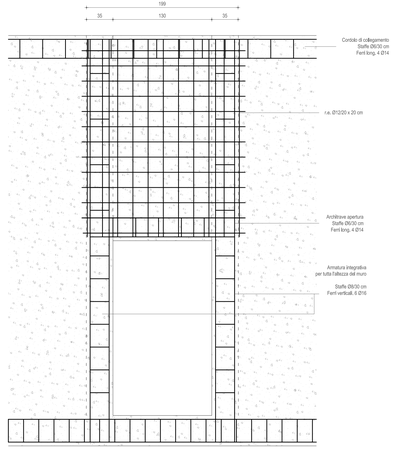

SEZIONE

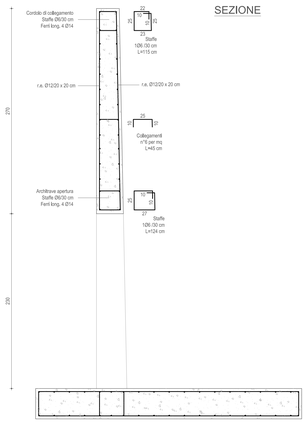

PIANTA



COMUNE DI RODIGO — PROVINCIA DI MANTOVA

MATERIALI PRESCRITTI:

- CLS per opere di fondazione e muri in c.a. Rck ≥ 30 (C25/30)

Classe di esposizione	XA1
Rapporto a/c massimo	0,60
Ricoprimento minimo	40 mm
Classe di consistenza allo scarico	S4

- Acciaio per tutte le strutture — B450 C controllato

Oggetto

PROGETTO PER LA REALIZZAZIONE DI AMPLIAMENTO DI IMPIANTO BIOGAS

Committente

[redacted]

Oggetto tavola

- Disegni esecutivi
  Muri di sostegno

Denuncia C.A.

Tav., n°	Variante
1	
Data	Scala
	1:200, 1:25

Progettazione

[redacted]

Collaboratori