


Particolare armatura d'angolo
scala 1:10

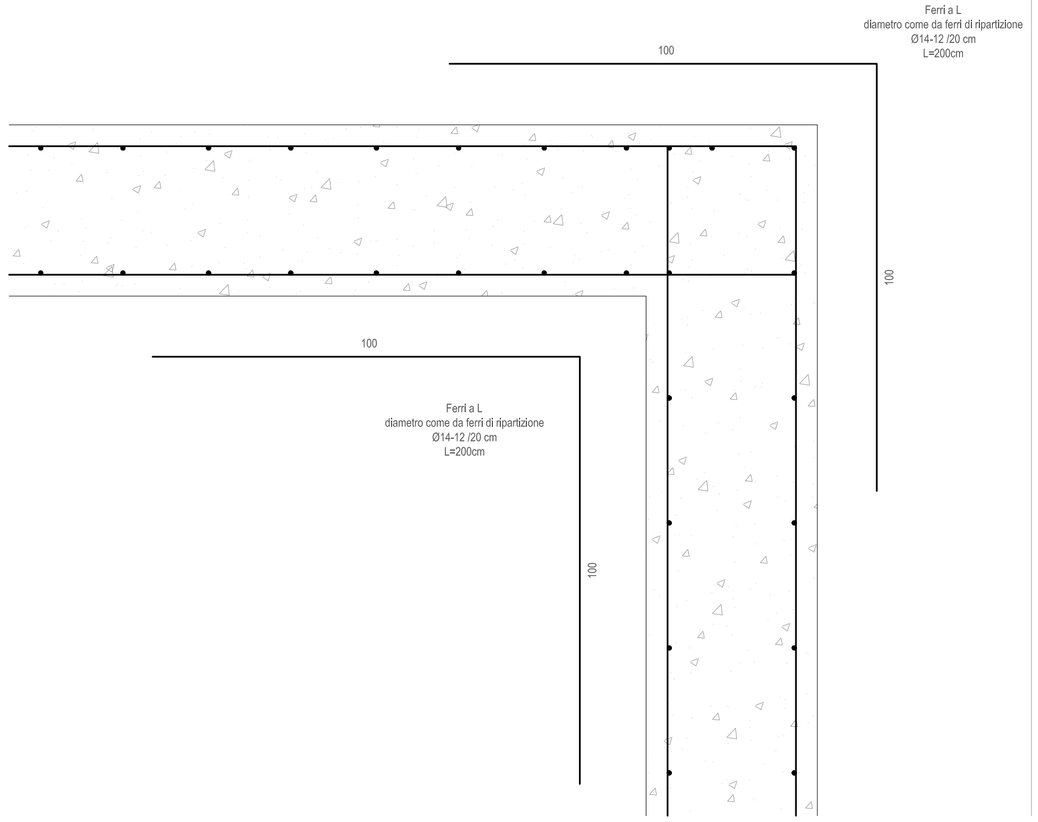


Particolare giunti di dilatazione
scala 1:10

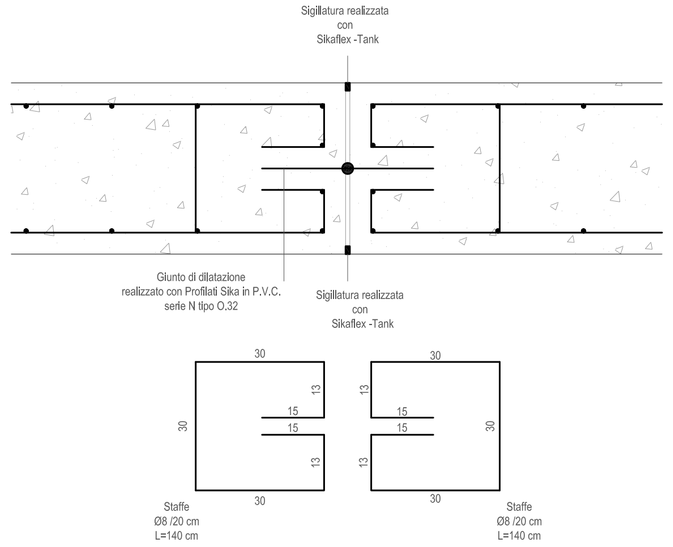


Pianta Vasche
scala 1:200

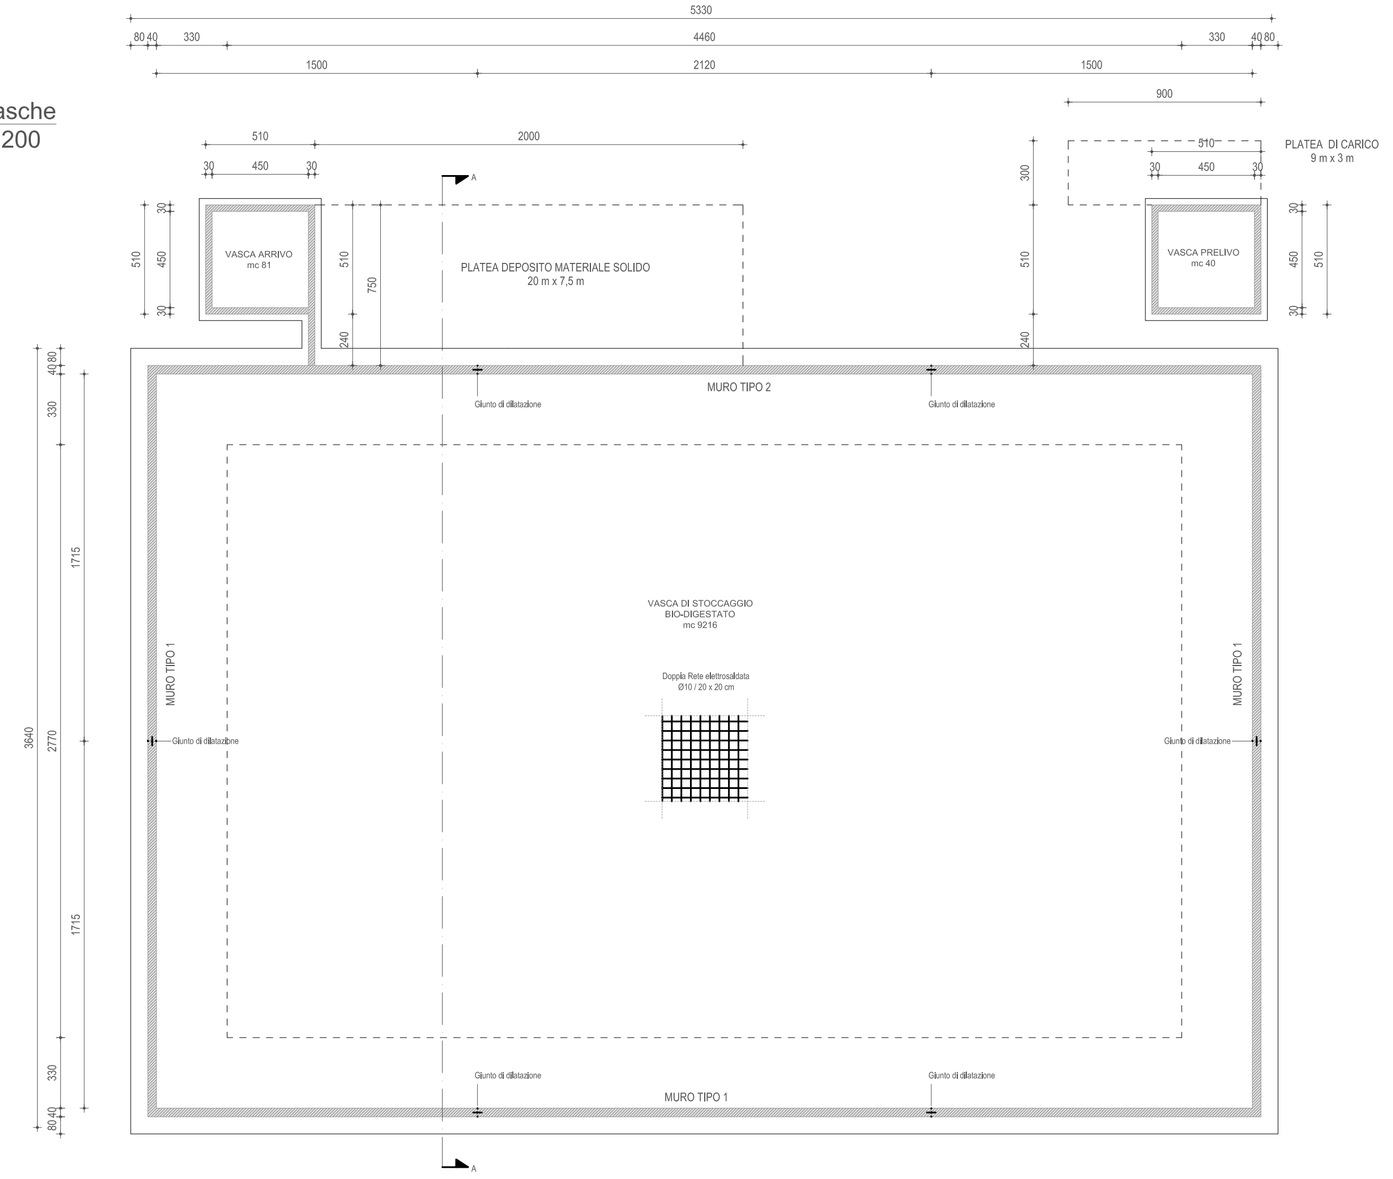

Muro Vasca h=5,5 m
scala 1:25

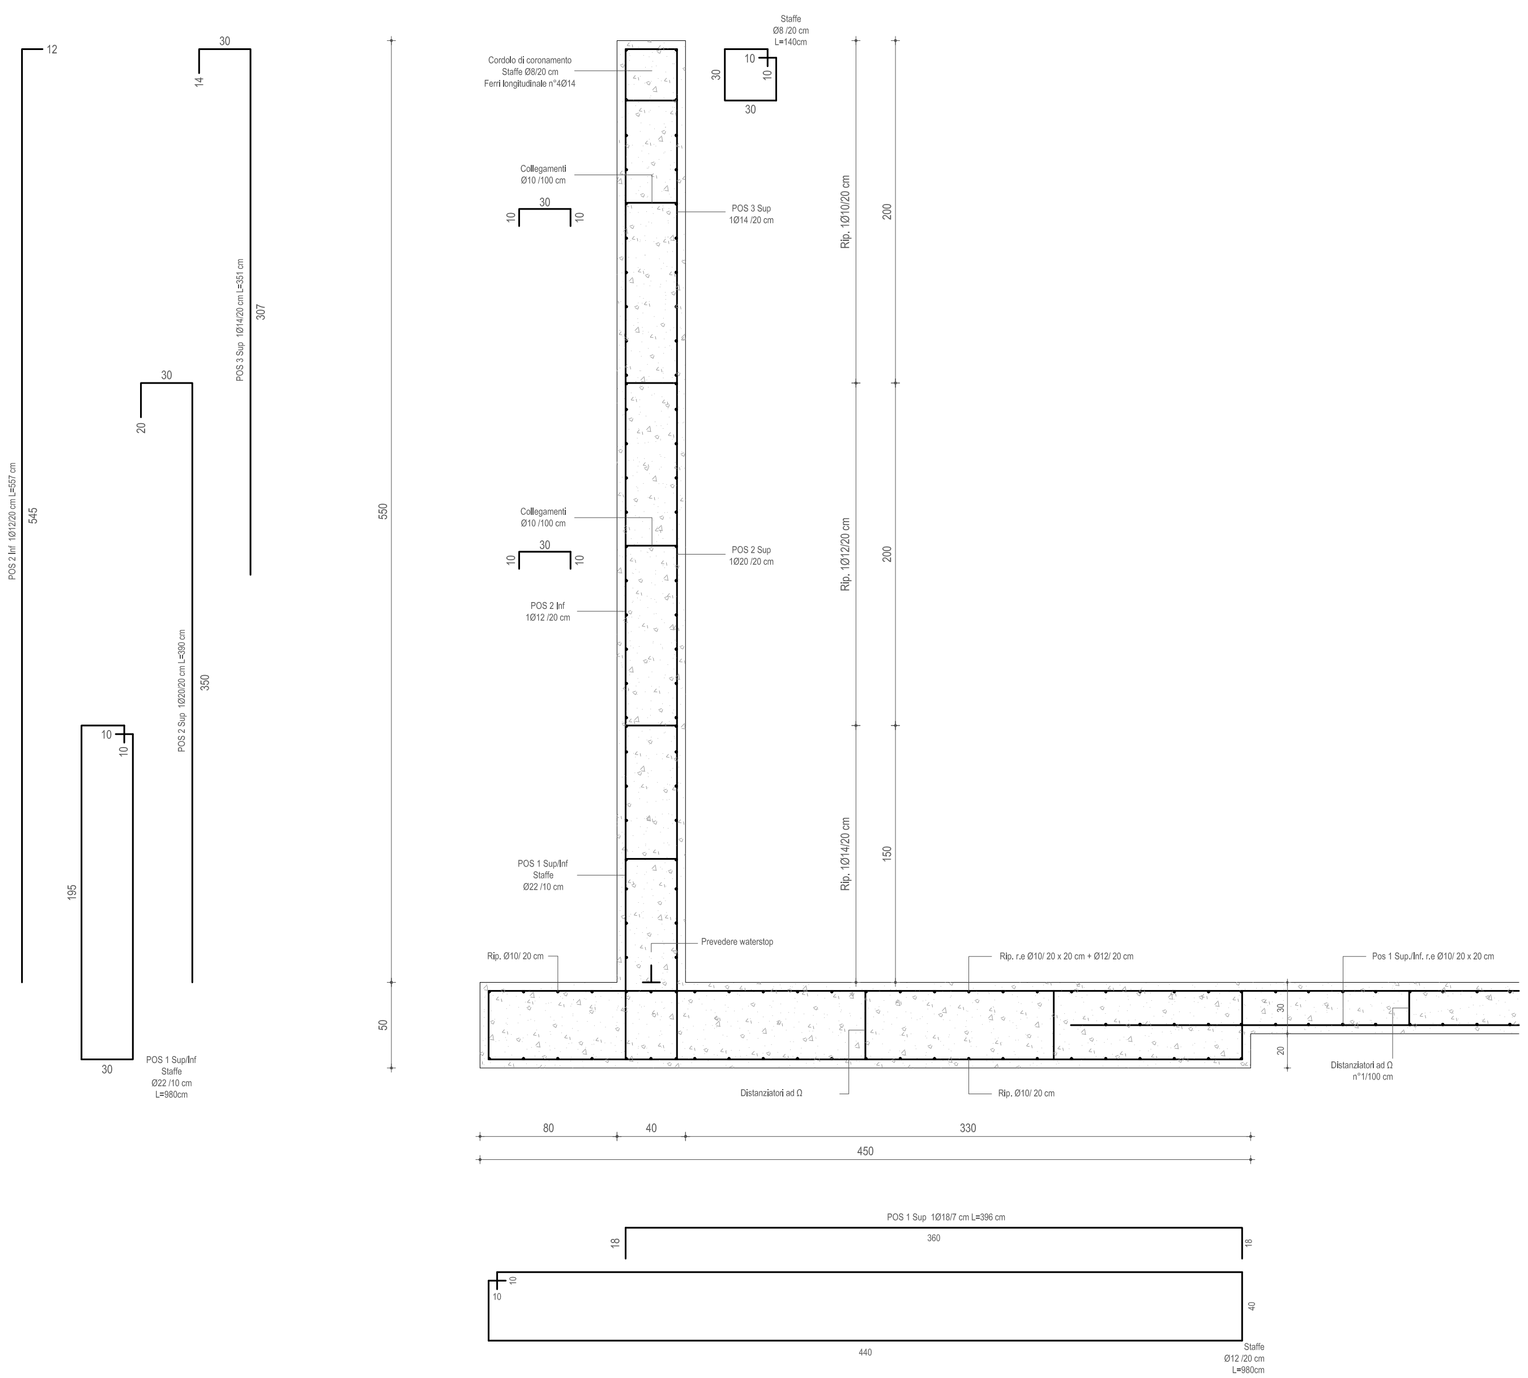

Muro Vasca h=6,5 m
scala 1:25

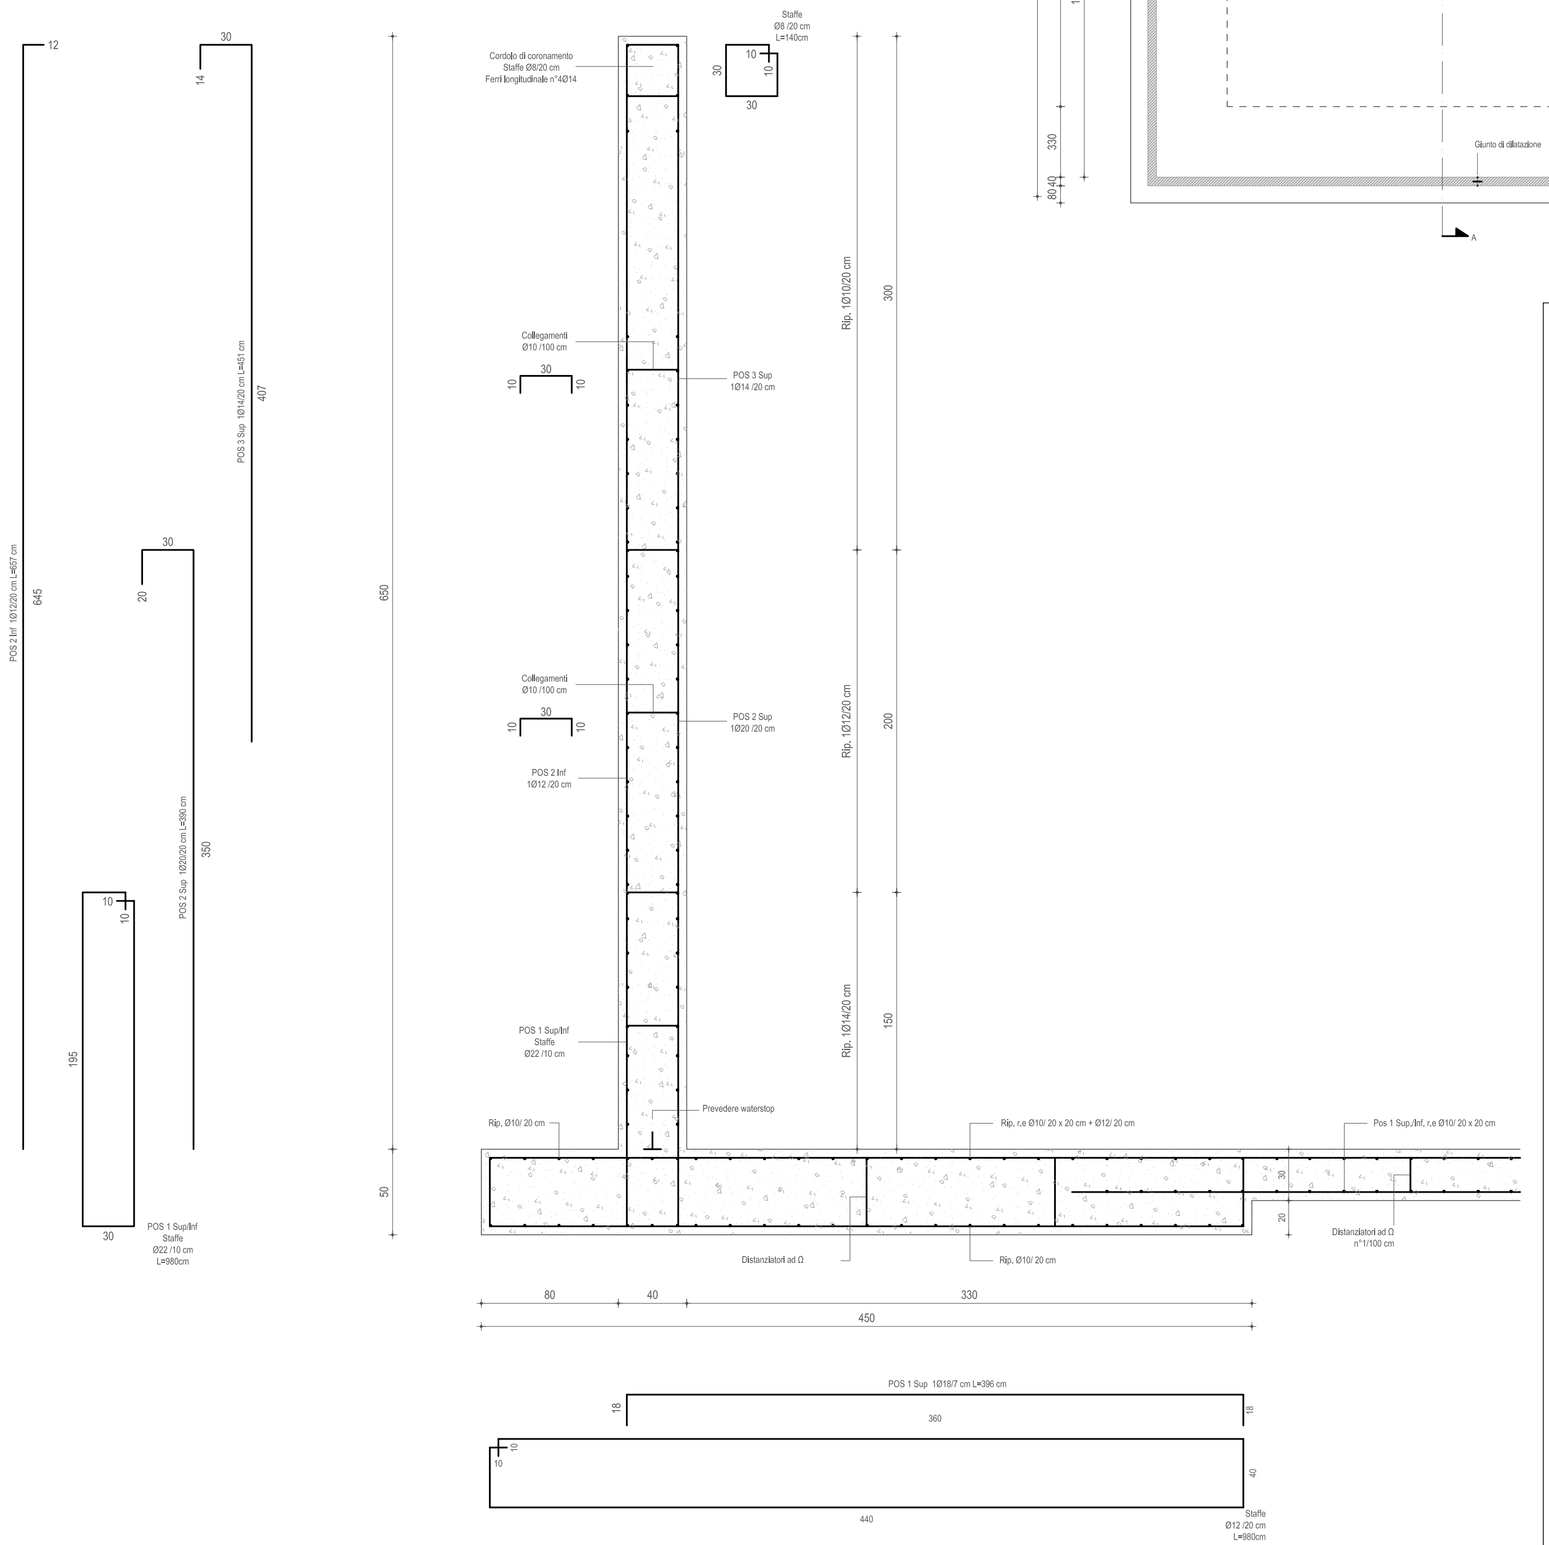

COMUNE DI RODIGO — PROVINCIA DI MANTOVA

MATERIALI PRESCRITTI:

- CLS per opere di fondazione e muri in c.a. C28/35

Classe di esposizione	XA1
Rapporto a/c massimo	0,55
Ricoprimento minimo	50 mm
Classe di consistenza allo scarico	S4
Granulometria inerti	Ømax=25mm

- Acciaio per tutte le strutture — B450 C controllato

Oggetto

PROGETTO PER LA REALIZZAZIONE DI AMPLIAMENTO DI IMPIANTO BIOGAS

C [redacted]

Oggetto tavola

- Disegni esecutivi:
  Vasca stoccaggio Bio-digestato

Denuncia C.A.

Tav. n° 1	Variante
Data	Scale 1:200, 1:25, 1:50

P [redacted] laboratori