


Pianta Vasche
scala 1:200

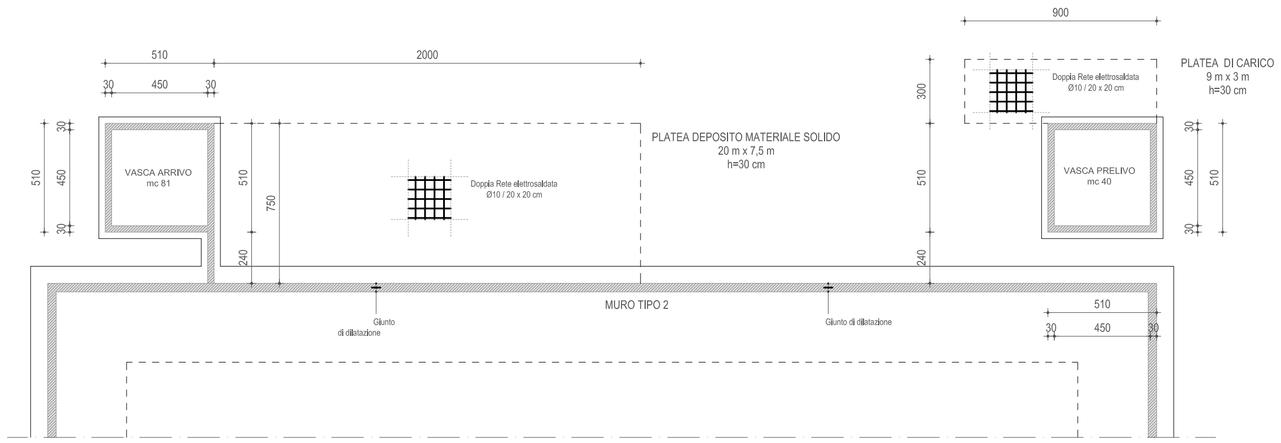


Particolare armatura d'angolo
scala 1:10

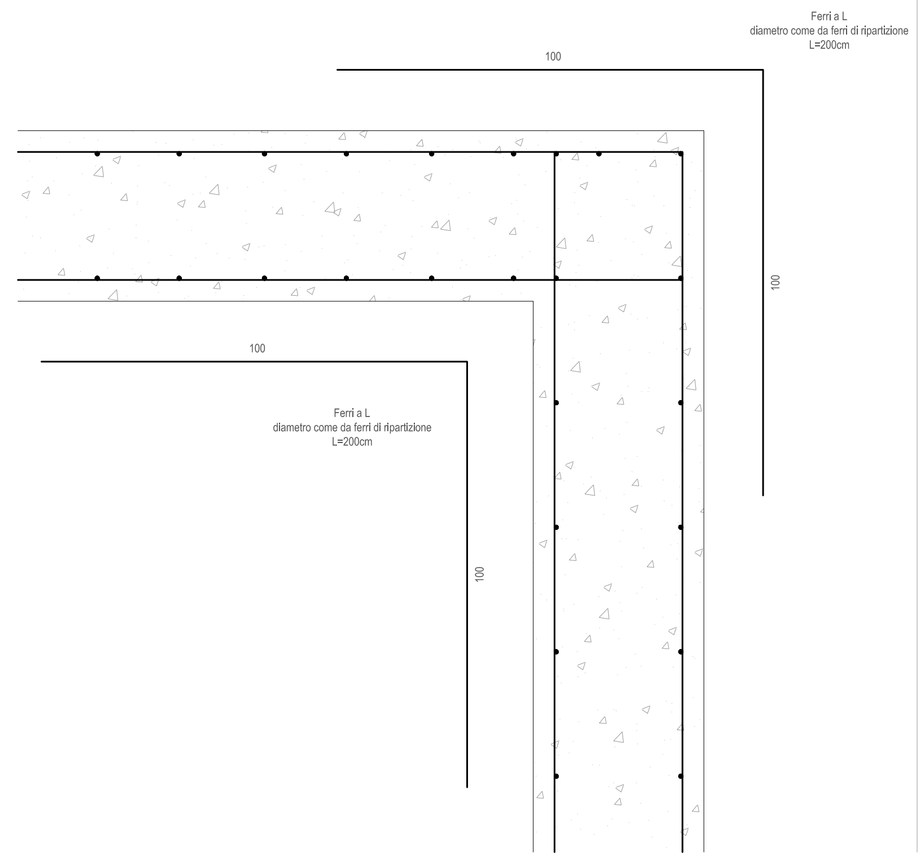

Vasca Arrivo
scala 1:25

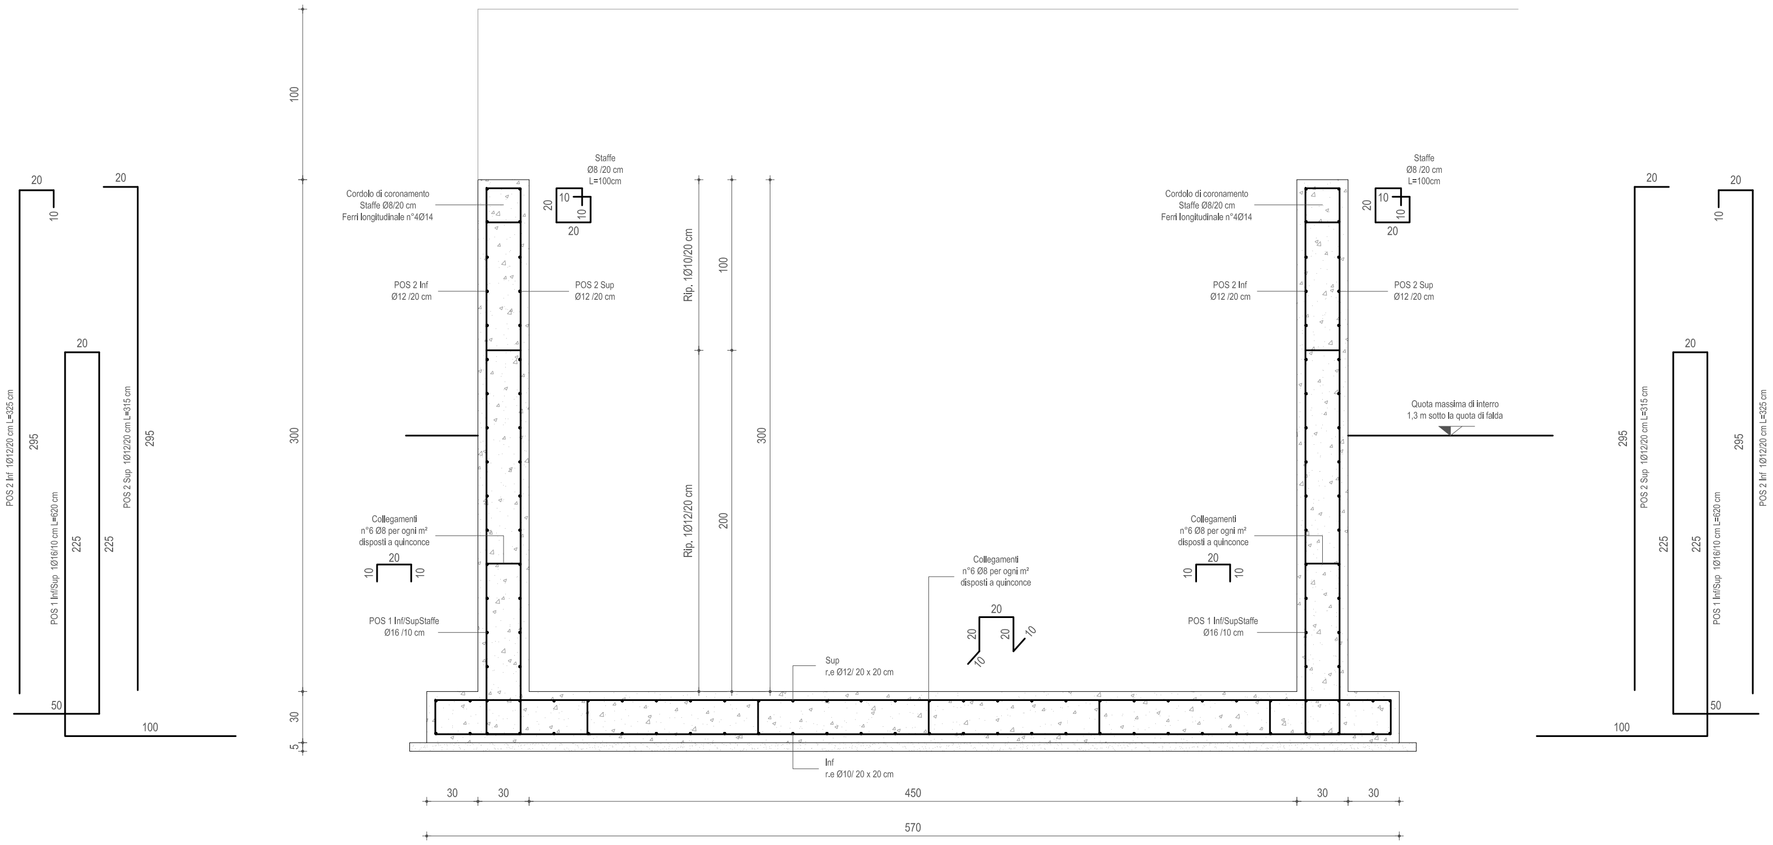

Vasca Prelievo
scala 1:25

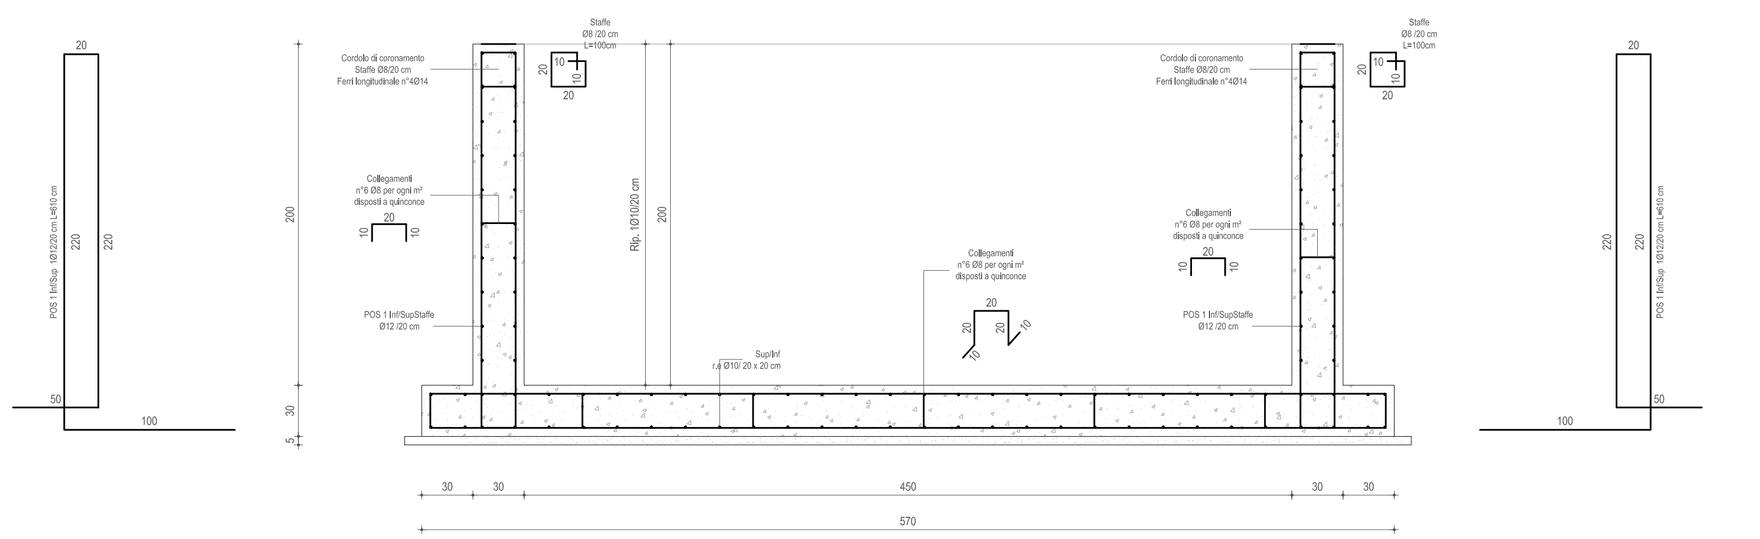

COMUNE DI RODIGO — PROVINCIA DI MANTOVA

MATERIALI PRESCRITTI:

- CLS per opere di fondazione e muri in c.a. C28/35

Classe di esposizione	XA1
Rapporto a/c massimo	0,55
Ricoprimento minimo	50 mm
Classe di consistenza allo scarico	S4
Granulometria inerti	Ømax=25mm

- Acciaio per tutte le strutture — B450 C controllato

Oggetto

PROGETTO PER LA REALIZZAZIONE DI AMPLIAMENTO DI IMPIANTO BIOGAS

Com
MA
Via

Ogg

- Disegni esecutivi:
  Vasca Arrivo
  Vasca Prelievo

Denuncia C.A.

Tav. n° 2

Variante

Data

Scale 1:200, 1:25, 1:50

Prog — oratori