MATERIALI E PRESCRIZIONI

MATERIALI PRESCRITTI:

Calcestruzzo
Per opere di: Fondazioni

- Classe di resistenza : C25/30 (Rck 30)
- Condizioni ambientali: Strutture completamente interrate in terreno permeabile
- Classe di esposizione : XC2
- Rapporto massimo acqua/cemento: 0,60
- Classe di consistenza: S3 (Plastica)
- Diametro massimo degli aggregati: 16 mm

Acciaio per C.A.
Per tutte le strutture B450 C controllato

Acciaio (Secondo UNI EN 10025-2:2004)
Tipologia
S275JR
Caratteristiche meccaniche
S275JR

Tensione di snervamento (T ambiente): Spessore nominale >3≤16 mm	f_{yk} = 275 N/mm²
Tensione di rottura (T ambiente): Spessore nominale >3 ≤ 16 mm	f_{tk} = 410-560 N/mm²
Deformazione massima a rottura (T ambiente): Spessore nominale >3 ≤ 40 mm	A% = 23%
Resilienza: T=20°C Spessore nominale <150 mm	Resilienza=27J

Bulloni
Tipologia
Ad alta resistenza: Classe 8.8
Caratteristiche meccaniche f_{yb} ≤ 649 N/mm²
f_{tb} ≤ 800 N/mm²

Saldature
Tipologia
Giunto: Ad angolo (A)
Testa a Testa (T-T)
Dimensione

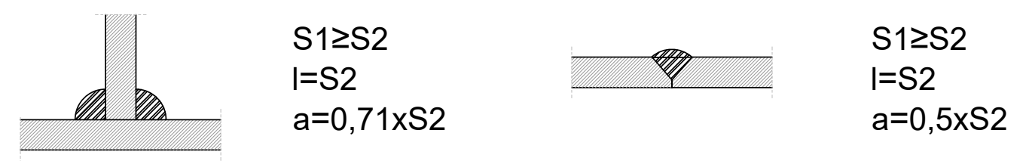
S1≥S2
l=S2
a=0,71xS2
S1≥S2
l=S2
a=0,5xS2

Criteri di accettabilità (UNI EN ISO 5817:2008)
Livello di qualità: C

COMUNE DI VOLTA MANTOVANA PROVINCIA DI MANTOVA

Oggetto
[redacted]

Committente
UNIONE COLLI MANTOVANI
Comune di Volta Mantovana
Comune di Monzambano
[redacted]

PROGETTO ESECUTIVO
DELLE STRUTTURE

Oggetto tavola
- Fondazioni
- Piante
- Prospetti
- Sezioni
- Particolari costruttivi

Tav. n°	Variante
U	-

Data	Scale
	1:25-1:10

Progettista
[redacted]

PIANTA Scala 1:25

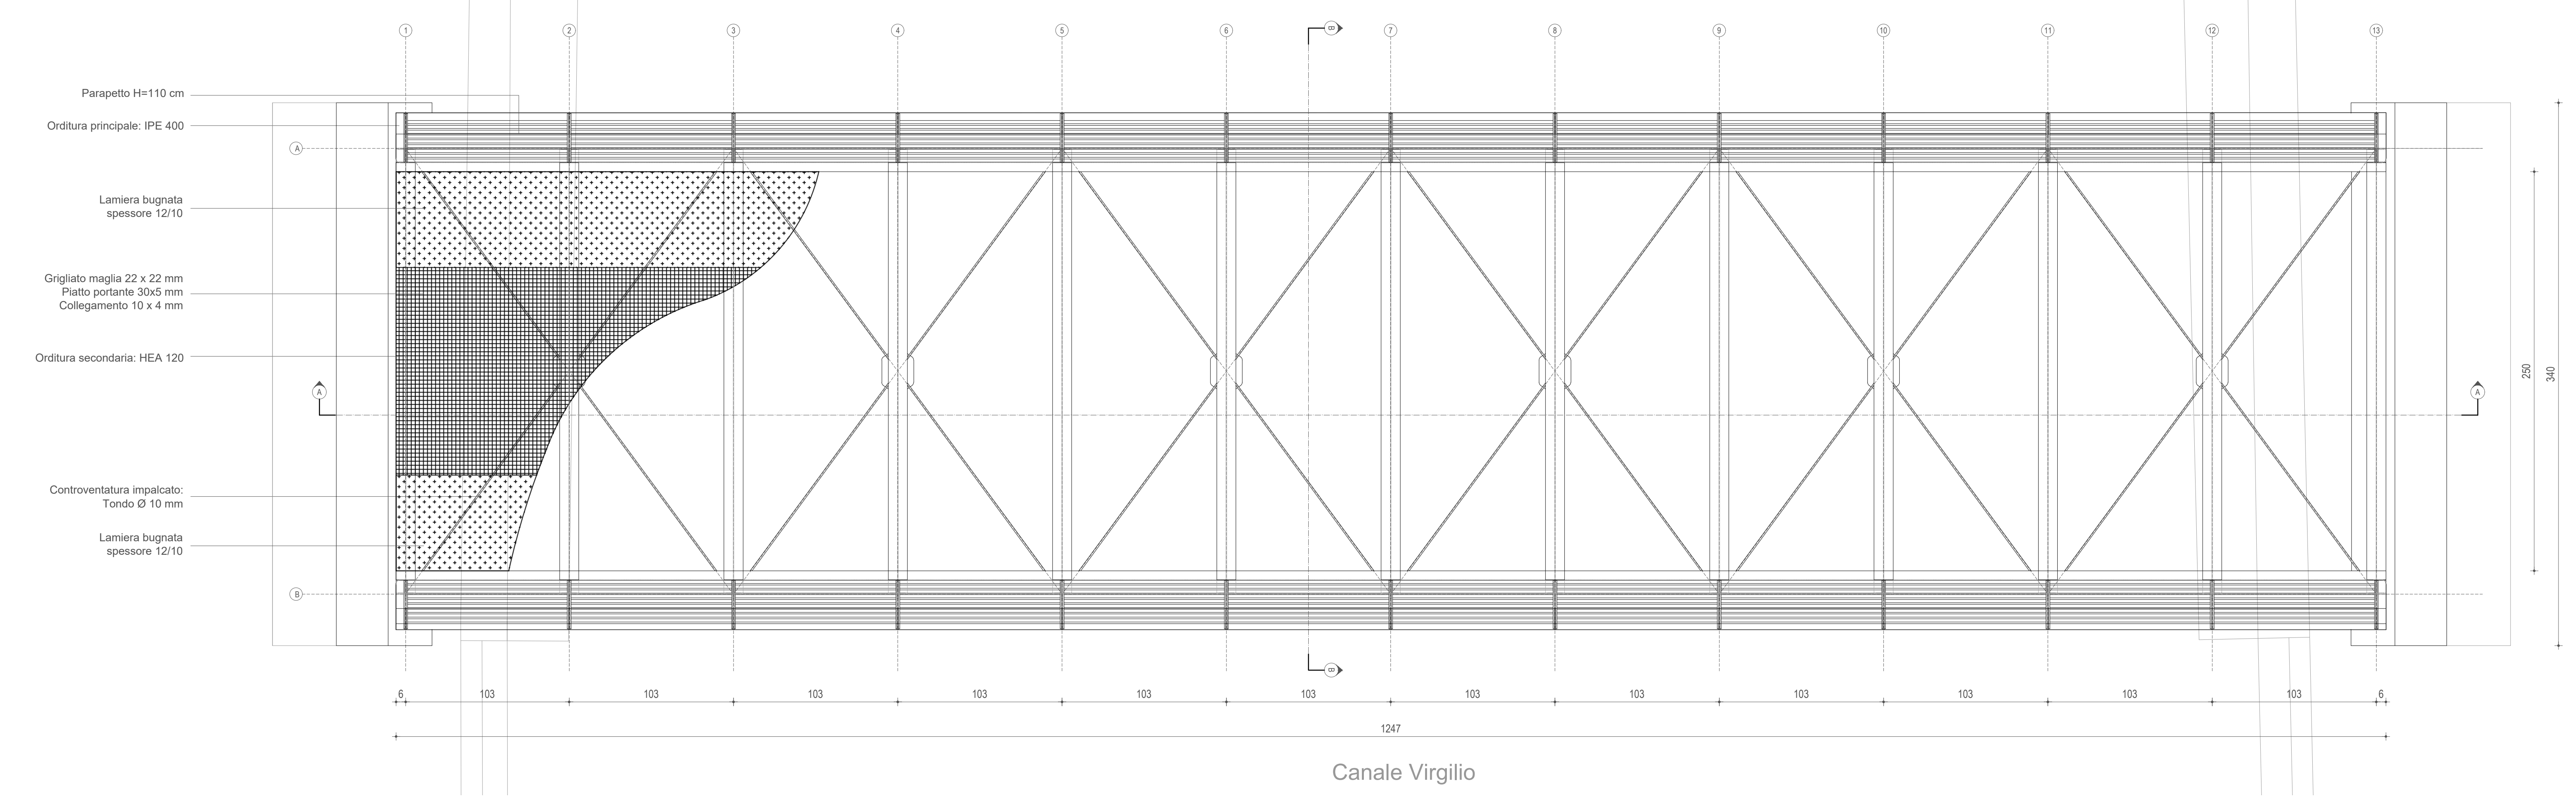
Parapetto H=110 cm
Orditura principale: IPE 400
Lamiera bugnata spessore 12/10
Grigliato maglia 22 x 22 mm
Piatto portante 30x5 mm
Collegamento 10 x 4 mm
Orditura secondaria: HEA 120
Controventatura impalcato: Tondo Ø 10 mm
Lamiera bugnata spessore 12/10
A
B
1
2
3
4
5
6
7
8
9
10
11
12
13
6
103
1247
290
340
Canale Virgilio

Prospetto Scala 1:25

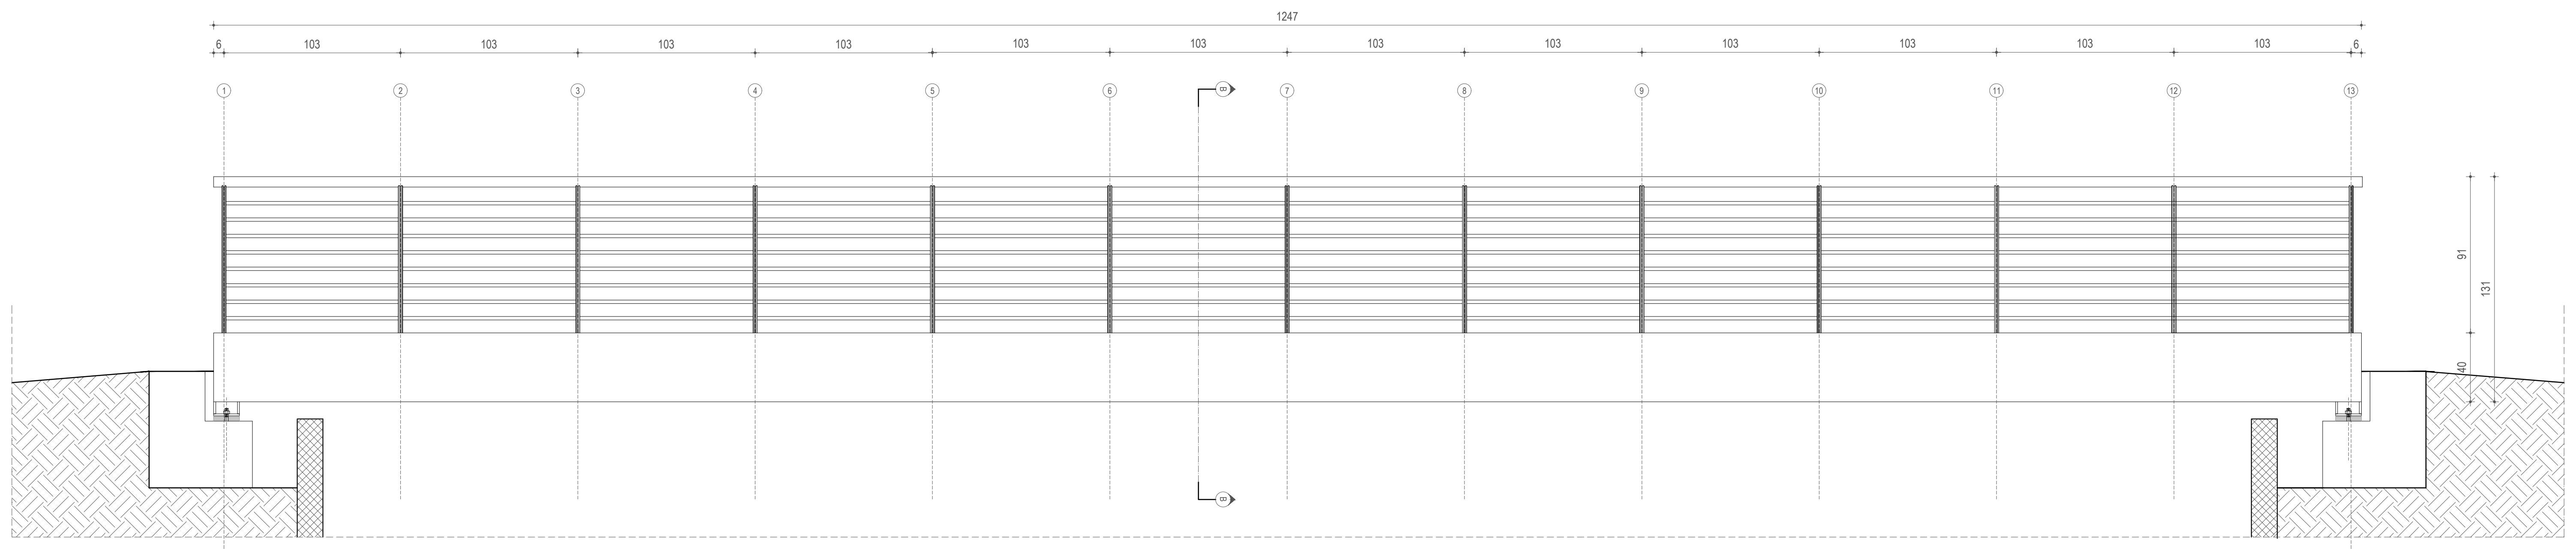
1247
6
103
91
121
40

Sezione A-A Scala 1:25

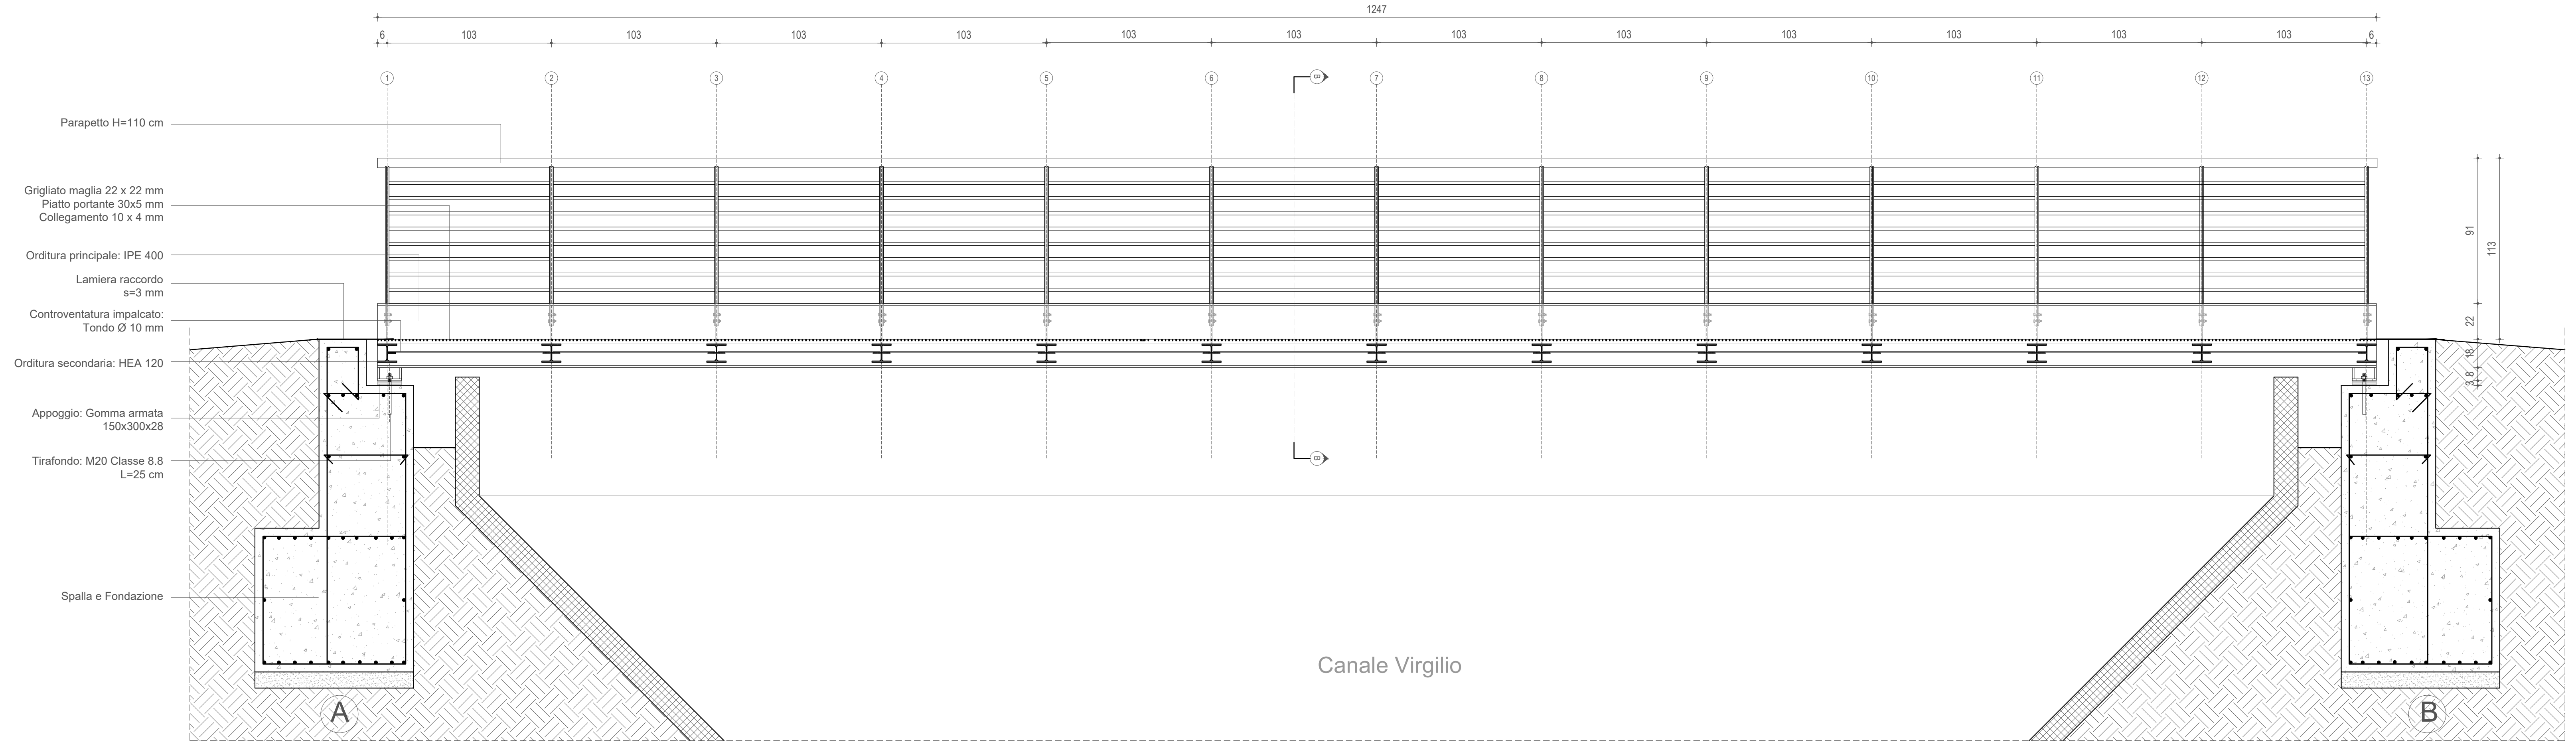
1247
6
103
1
2
Parapetto H=110 cm
Grigliato maglia 22 x 22 mm
Piatto portante 30x5 mm
Collegamento 10 x 4 mm
Orditura principale: IPE 400
Lamiera raccordo s=3 mm
Controventatura impalcato: Tondo Ø 10 mm
Orditura secondaria: HEA 120
Appoggio: Gomma armata 150x300x28
Tirafondo: M20 Classe 8.8 L=25 cm
Spalla e Fondazione
91
113
22
A
B
Canale Virgilio

Sezione B-B
Scala 1:25

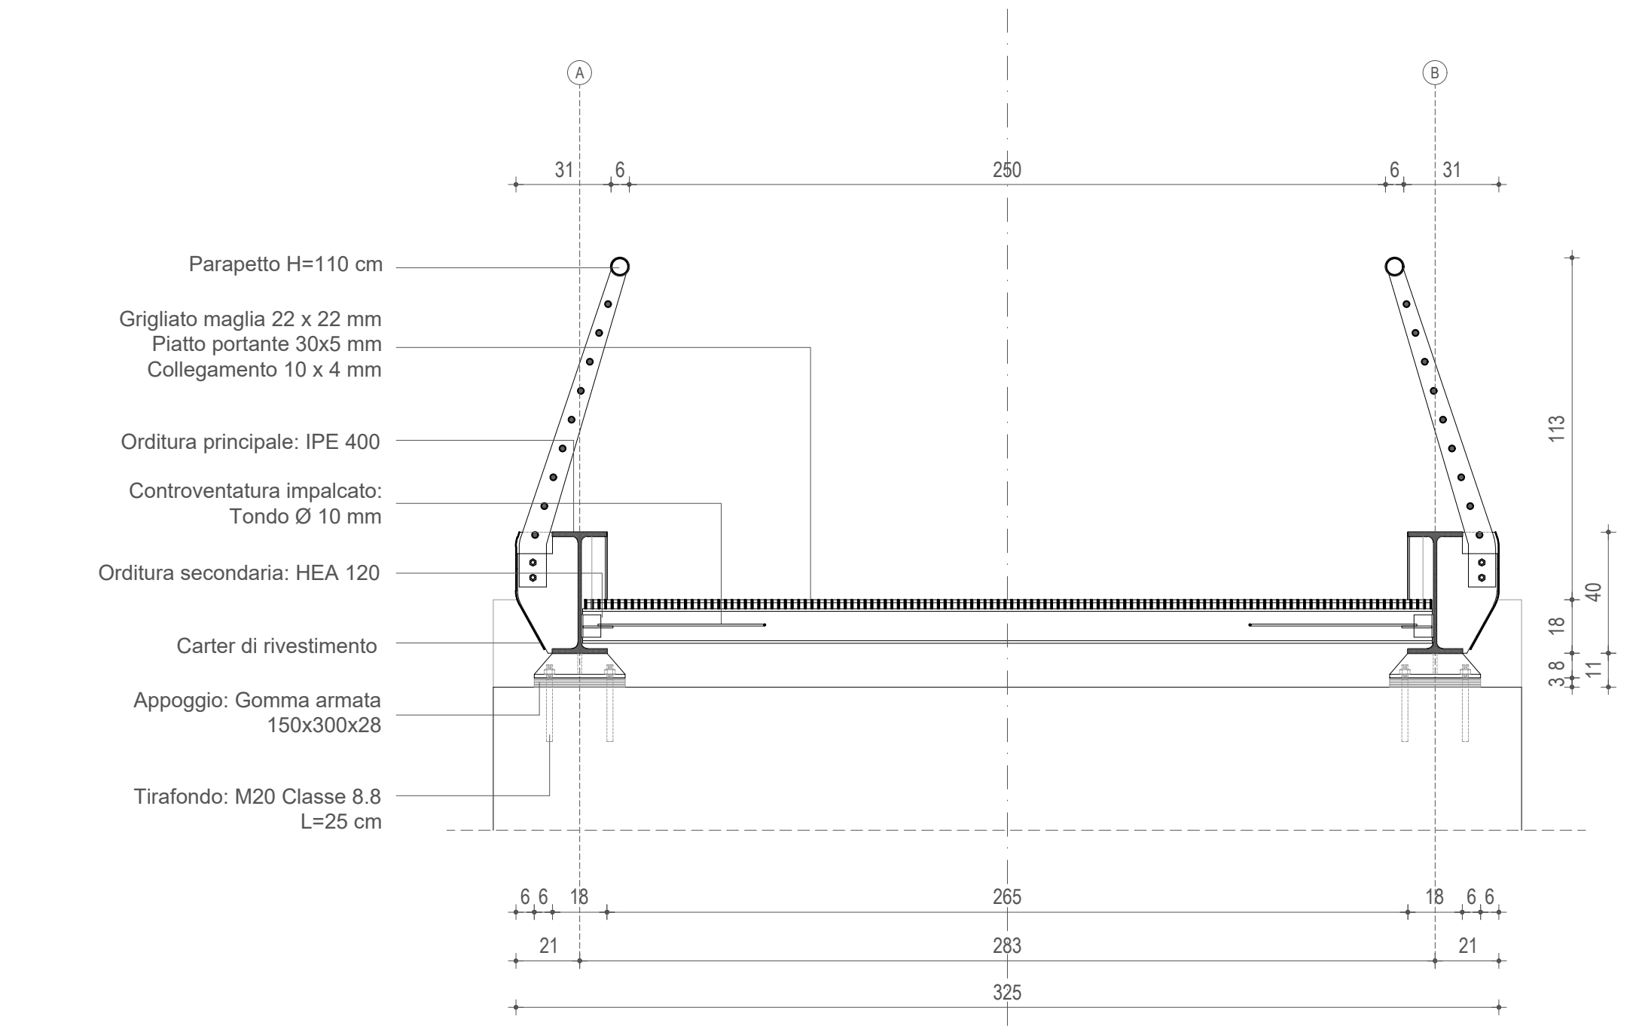
A
B
31
6
250
Parapetto H=110 cm
Grigliato maglia 22 x 22 mm
Piatto portante 30x5 mm
Collegamento 10 x 4 mm
Orditura principale: IPE 400
Controventatura impalcato: Tondo Ø 10 mm
Orditura secondaria: HEA 120
Carter di rivestimento
Appoggio: Gomma armata 150x300x28
Tirafondo: M20 Classe 8.8 L=25 cm
113
40
18
3 8
11
6 6 18
265
21
283
325

Fondazione
L=3,40 m
Scala 1:25

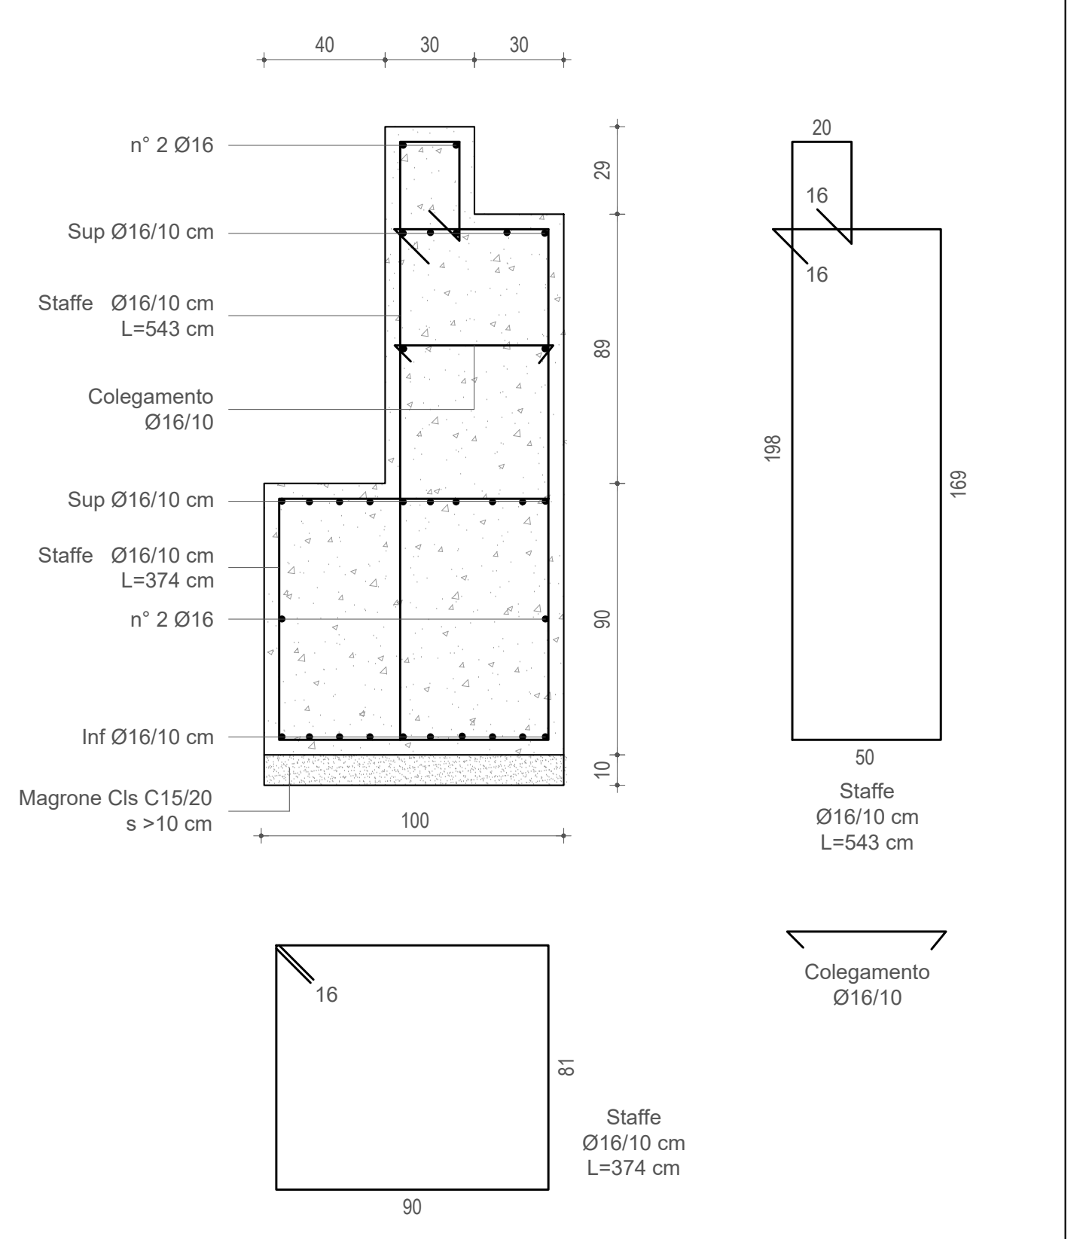
40
30
30
n° 2 Ø16
Sup Ø16/10 cm
Staffe Ø16/10 cm L=543 cm
Colegamento Ø16/10
Sup Ø16/10 cm
Staffe Ø16/10 cm L=374 cm
n° 2 Ø16
Inf Ø16/10 cm
Magrone Cls C15/20 s >10 cm
100
29
89
90
10
20
16
16
198
169
50
Staffe Ø16/10 cm L=543 cm
Colegamento Ø16/10
16
81
90
Staffe Ø16/10 cm L=374 cm

Particolare Appoggi A-B
Scala 1:10

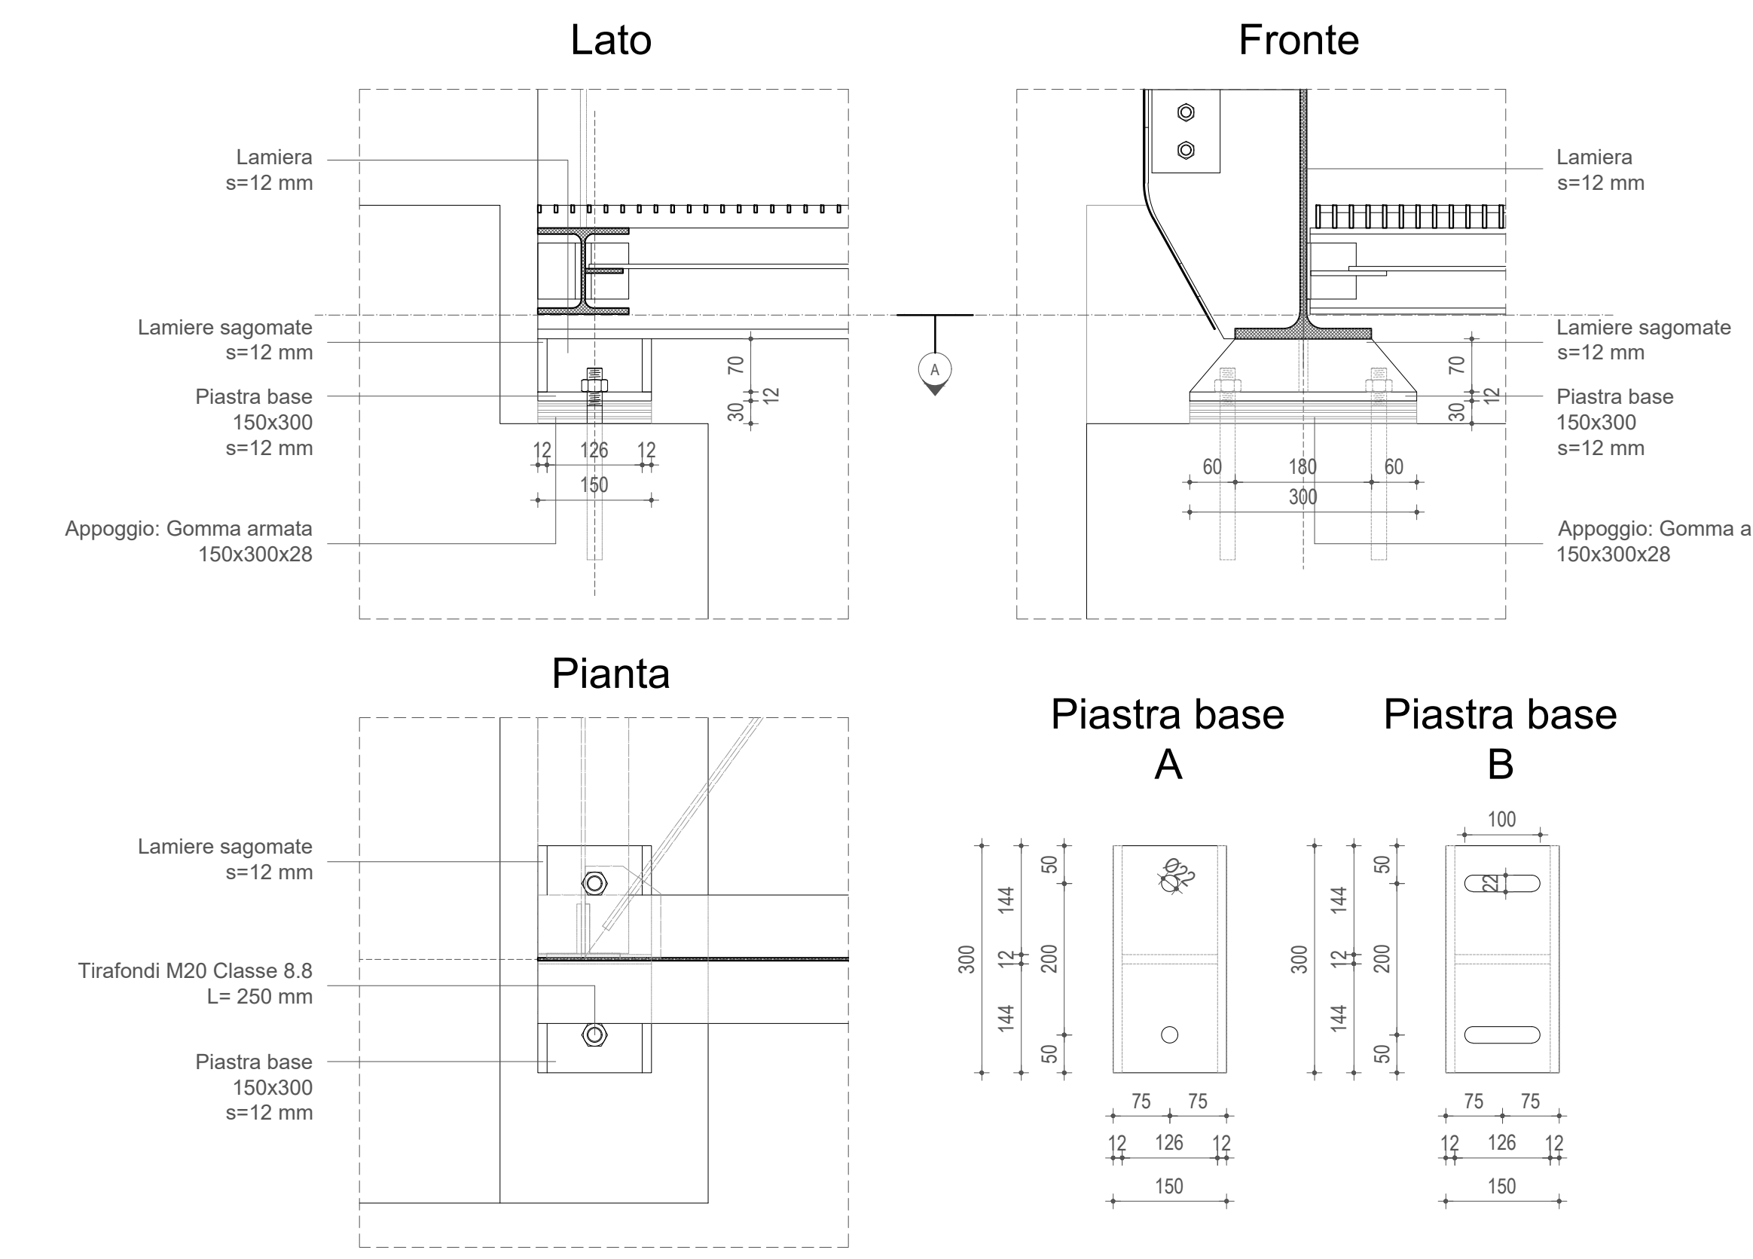
Lato
Fronte
Pianta
Piastra base A
Piastra base B
Lamiera s=12 mm
Lamiere sagomate s=12 mm
Piastra base 150x300 s=12 mm
Appoggio: Gomma armata 150x300x28
70
30
12
12
126
12
150
A
60
180
60
300
Lamiere sagomate s=12 mm
Tirafondi M20 Classe 8.8 L= 250 mm
Piastra base 150x300 s=12 mm
300
144
12
144
50
200
50
Ø22
75
75
126
150
100
22

Controventatura
Particolare nodo HEA 120 -IPE400
Scala 1:10

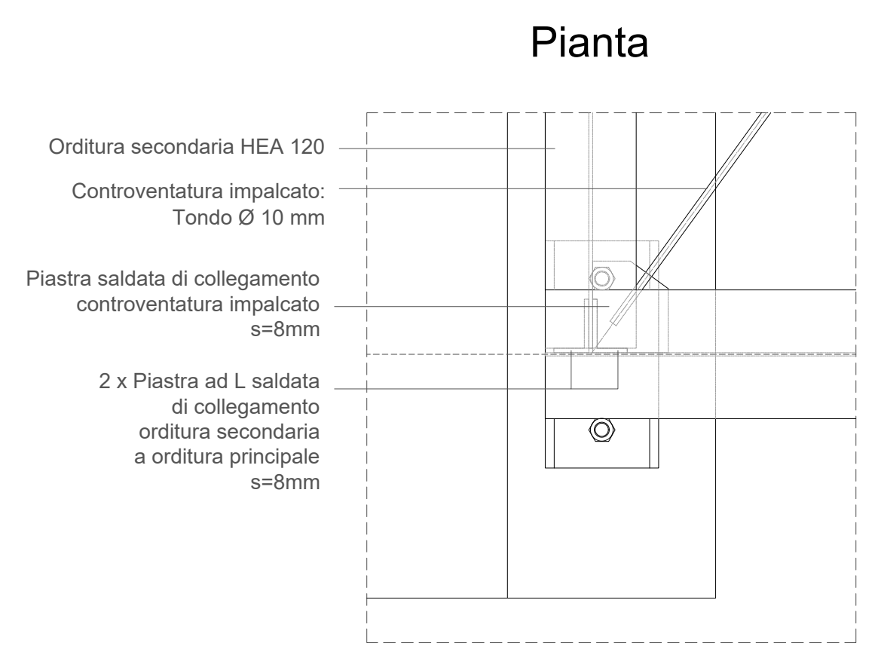
Pianta
Orditura secondaria HEA 120
Controventatura impalcato: Tondo Ø 10 mm
Piastra saldata di collegamento controventatura impalcato s=8mm
2 x Piastra ad L saldata di collegamento orditura secondaria a orditura principale s=8mm

Controventatura
Particolare nodo HEA 120
Scala 1:10

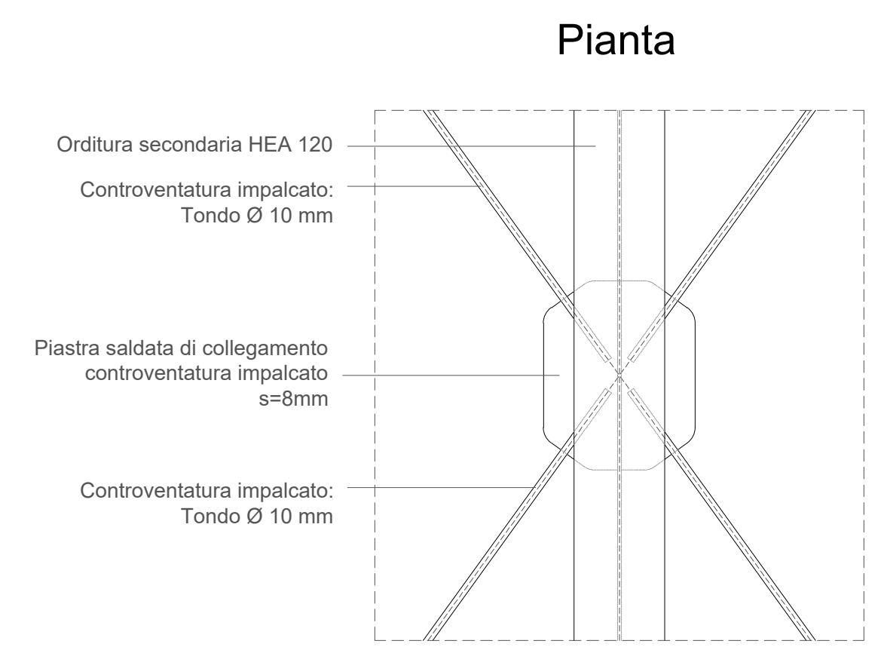
Pianta
Orditura secondaria HEA 120
Controventatura impalcato: Tondo Ø 10 mm
Piastra saldata di collegamento controventatura impalcato s=8mm
Controventatura impalcato: Tondo Ø 10 mm

Particolare parapetto
Scala 1:10

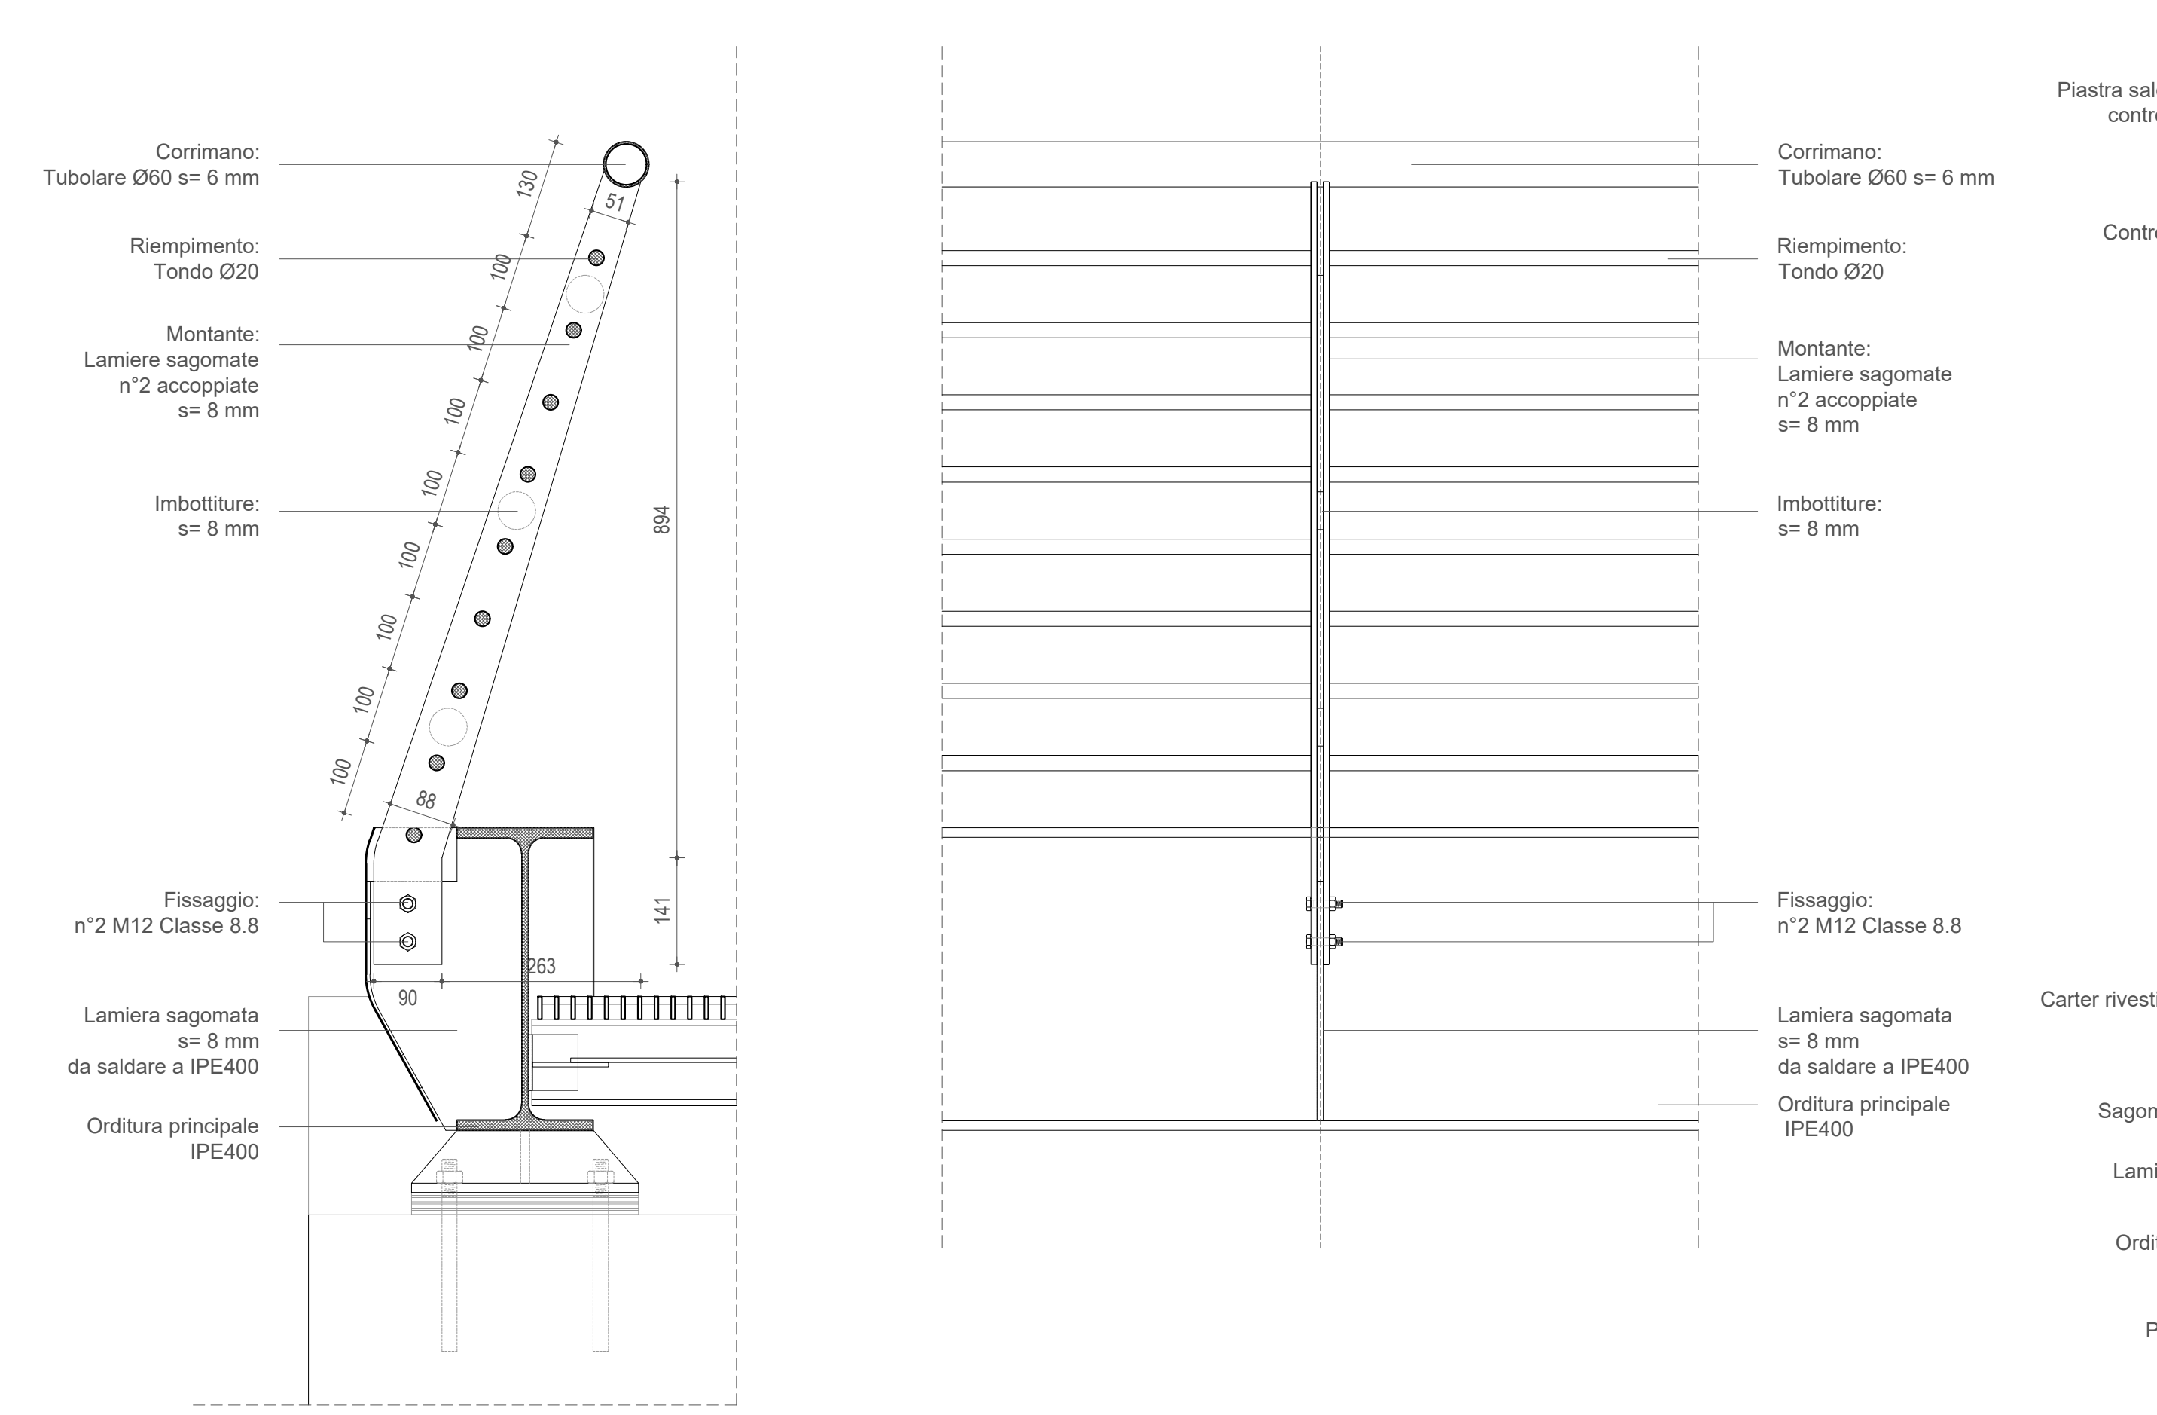
Lato
Fronte
Corrimano: Tubolare Ø60 s= 6 mm
Riempimento: Tondo Ø20
Montante: Lamiere sagomate n°2 accoppiate s= 8 mm
Imbottiture: s= 8 mm
Fissaggio: n°2 M12 Classe 8.8
Lamiera sagomata s= 8 mm da saldare a IPE400
Orditura principale IPE400
130
51
100
88
894
141
263
90

Particolare protezione testata IPE 400
Scala 1:10

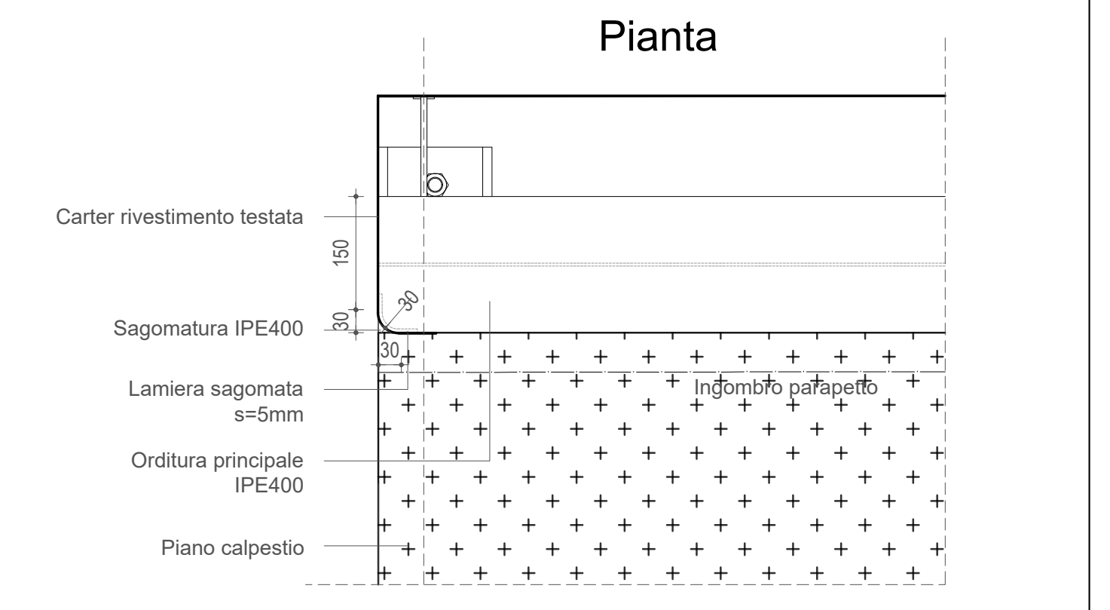
Pianta
Carter rivestimento testata
Sagomatura IPE400
Lamiera sagomata s=5mm
Orditura principale IPE400
Piano calpestio
150
30
30
30
Ingombro parapetto