MATERIALI E PRESCRIZIONI

MATERIALI PRESCRITTI:

Calcestruzzo
Per opere di: Fondazioni

- Classe di resistenza : C25/30 (Rck 30)
- Condizioni ambientali: Strutture completamente interrate in terreno permeabile
- Classe di esposizione : XC2
- Rapporto massimo acqua/cemento: 0,60
- Classe di consistenza: S3 (Plastica)
- Diametro massimo degli aggregati: 16 mm

Acciaio per C.A.
Per tutte le strutture B450 C controllato

Acciaio (Secondo UNI EN 10025-2:2004)
Tipologia
S275JR
Caratteristiche meccaniche
S275JR
Tensione di snervamento (T ambiente): Spessore nominale >3≤16 mm f_{yk} = 275 N/mm²
Tensione di rottura (T ambiente): Spessore nominale >3 ≤ 16 mm f_{tk} = 410-560 N/mm²
Deformazione massima a rottura (T ambiente): Spessore nominale >3 ≤ 40 mm A% = 23%
Resilienza: T=20°C Spessore nominale <150 mm Resilienza=27J

Bulloni
Tipologia
Ad alta resistenza: Classe 8.8
Caratteristiche meccaniche $f_{yb} \leq 649$ N/mm²
$f_{tb} \leq 800$ N/mm²

Saldature
Tipologia
Giunto: Ad angolo (A)
Testa a Testa (T-T)
Dimensione



S1≥S2
l=S2
a=0,71xS2



S1≥S2
l=S2
a=0,5xS2

Criteri di accettabilità (UNI EN ISO 5817:2008)
Livello di qualità: C

COMUNE DI REMEDELLO — PROVINCIA DI BRESCIA

Oggetto

[redacted]

[redacted]

PROGETTO STRUTTURE

Oggetto tavola
- Fondazioni

Tav. n° 01


Variante

Data 29/03/2019


Scale 1:10 - 1:50

[redacted]


PIANTA BASE
Scala 1:50

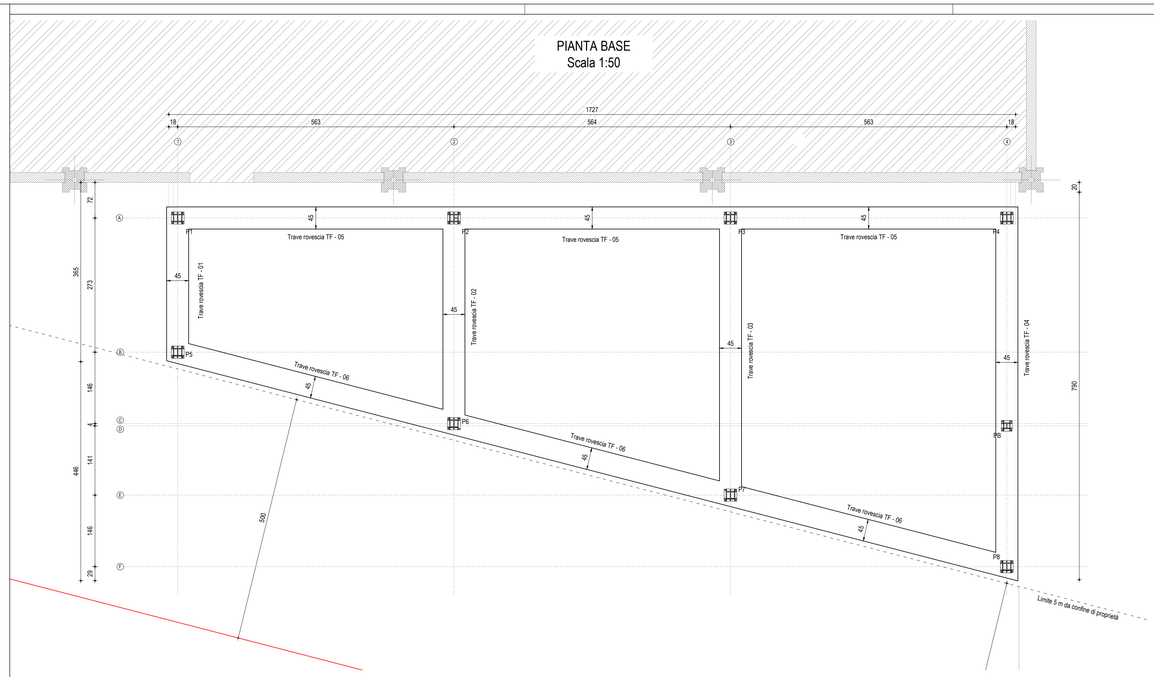

Trave rovescia TF-01
Scala 1:50

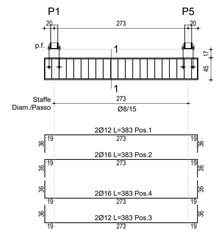


Sezione 1-1
Scala 1:20

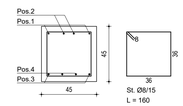


PARTICOLARE PIASTRA ANCORAGGIO

Tirafondi Ø18 mm Viti cl. 8.8 Dadi 8 o 10
Calcestruzzo fondazione: Rck 30 N/mmq
Profilo colonna: HEA 160
Materiale colonna: Acciaio S275
Materiale piastra e nervature: Acciaio S275
Spessore dei cordoni di saldatura: 5 mm
Rosette: spessore 15 mm


Pianta contropiastra s= 5 mm
Scala 1:5

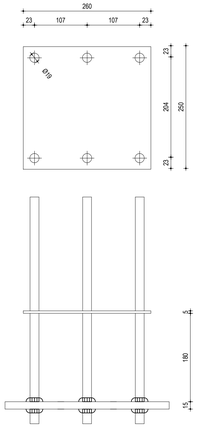


Trave rovescia TF-02
Scala 1:50

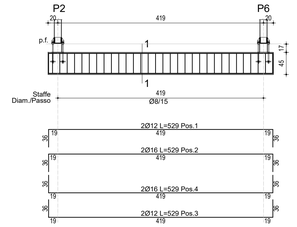


Sezione 1-1
Scala 1:20

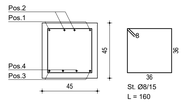


Pianta piastra ancoraggio s= 15 mm
Scala 1:5

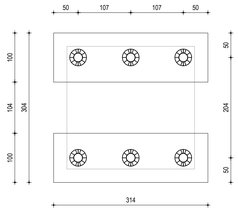

Trave rovescia TF-03
Scala 1:50

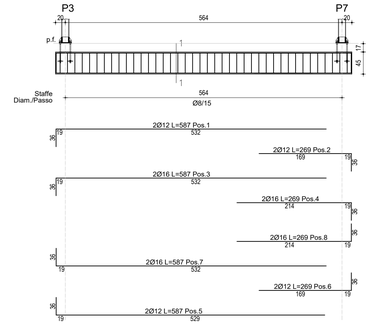


Sezione 1-1
Scala 1:20

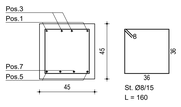


PARTICOLARE PIASTRA ANCORAGGIO
VARIANTE PILASTRO BARACCATURA
PB


Pianta contropiastra s= 5 mm
Scala 1:5

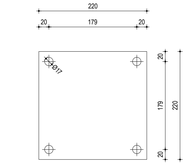


Trave rovescia TF-05
Scala 1:50

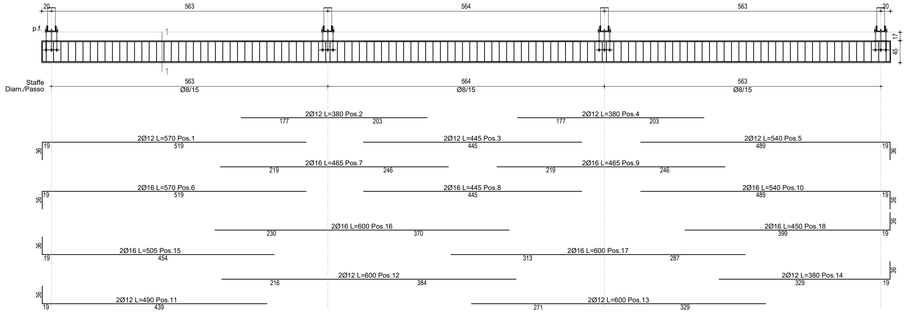


Sezione 1-1
Scala 1:20

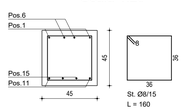


Trave rovescia TF-06
Scala 1:50

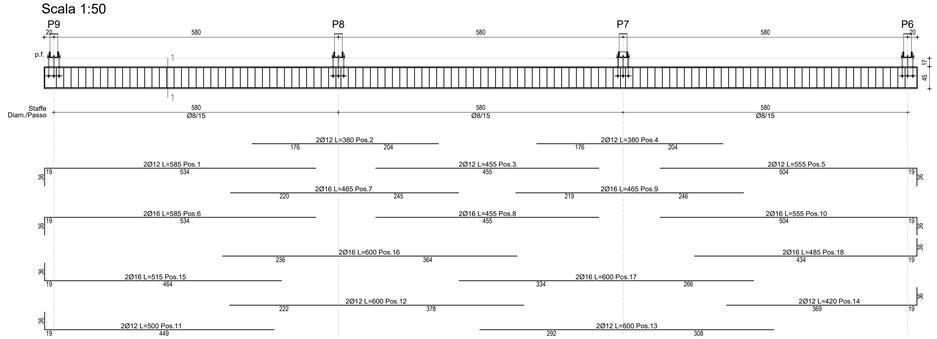


Sezione 1-1
Scala 1:20

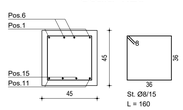


Trave rovescia TF-04
Scala 1:50

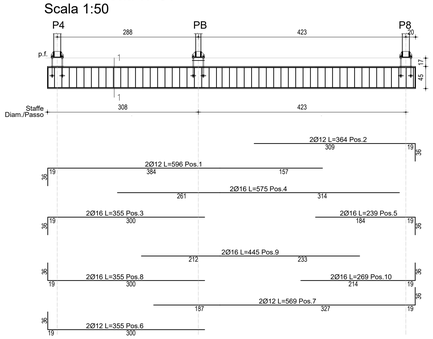


Sezione 1-1
Scala 1:20

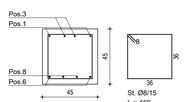

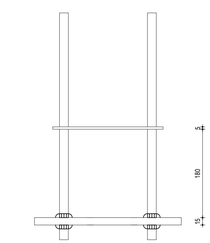

Pianta piastra ancoraggio s= 15 mm
Scala 1:10

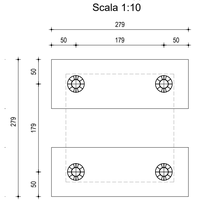

MATERIALI E PRESCRIZIONI

MATERIALI PRESCRITTI:

Calcestruzzo
Per opere di: Fondazioni

- Classe di resistenza : C25/30 (Rck 30)
- Condizioni ambientali: Strutture completamente interrate in terreno permeabile
- Classe di esposizione : XC2
- Rapporto massimo acqua/cemento: 0,60
- Classe di consistenza: S3 (Plastica)
- Diametro massimo degli aggregati: 16 mm

Acciaio per C.A.
Per tutte le strutture B450 C controllato

Acciaio (Secondo UNI EN 10025-2:2004)
Tipologia
S275JR
Caratteristiche meccaniche
S275JR
Tensione di snervamento (T ambiente): Spessore nominale >3≤16 mm f_{yk} = 275 N/mm²
Tensione di rottura (T ambiente): Spessore nominale >3 ≤ 16 mm f_{tk} = 410-560 N/mm²
Deformazione massima a rottura (T ambiente): Spessore nominale >3 ≤ 40 mm A% = 23%
Resilienza: T=20°C Spessore nominale <150 mm Resilienza=27J

Bulloni
Tipologia
Ad alta resistenza: Classe 8.8
Caratteristiche meccaniche $f_{yb} \leq 649$ N/mm²
$f_{tb} \leq 800$ N/mm²

Saldature
Tipologia
Giunto: Ad angolo (A)
Testa a Testa (T-T)
Dimensione



S1≥S2
l=S2
a=0,71xS2

S1≥S2
l=S2
a=0,5xS2

Criteri di accettabilità (UNI EN ISO 5817:2008)
Livello di qualità: C

COMUNE DI REMEDELLO PROVINCIA DI BRESCIA

Oggetto

[redacted]


[redacted]

PROGETTO STRUTTURE


Oggetto tavola	Tav. n°	Variante
- Elevazione	02	
	Data: 29/03/2019	Scale: 1:10 - 1:50

[redacted]


PIANTA COPERTURA
Scala 1:50

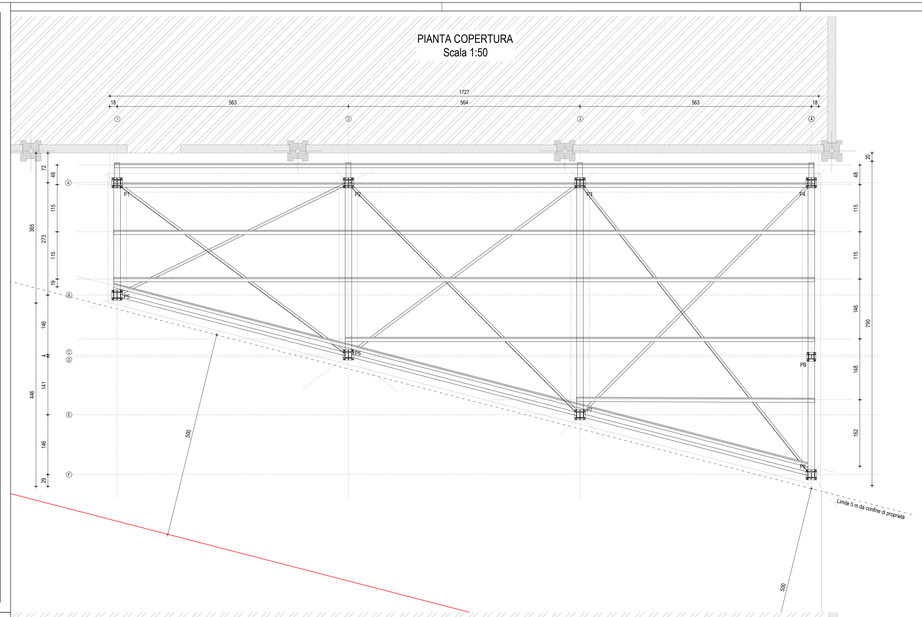


PIANTA BASE
Scala 1:50

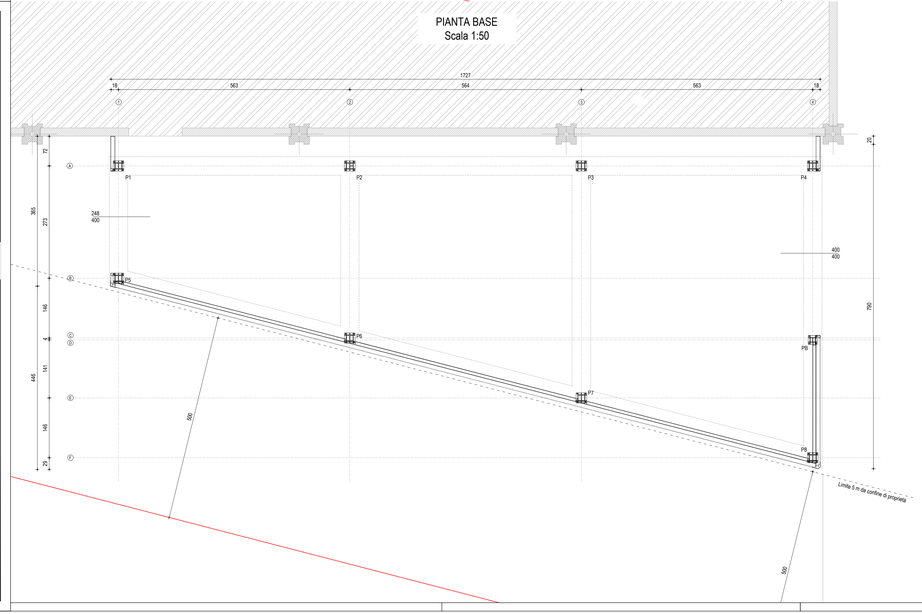


PROSPETTO FRONTALE
Scala 1:50

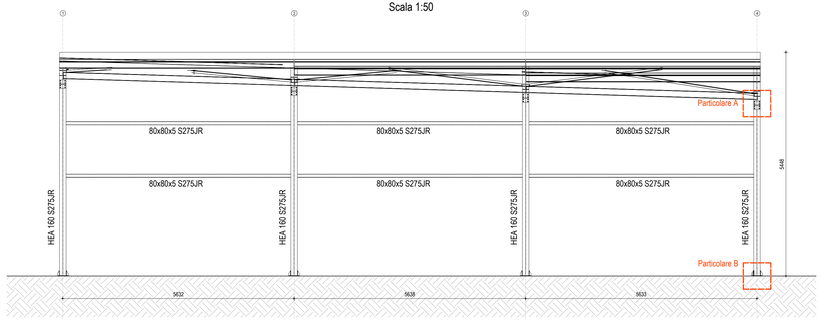


PROSPETTO FRONTALE
Scala 1:50

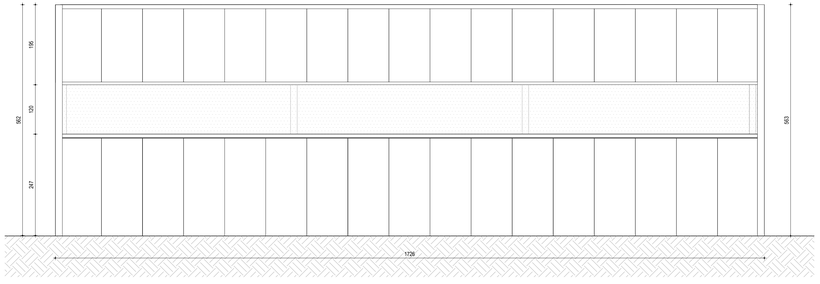

PROSPETTO LATERALE
Scala 1:50

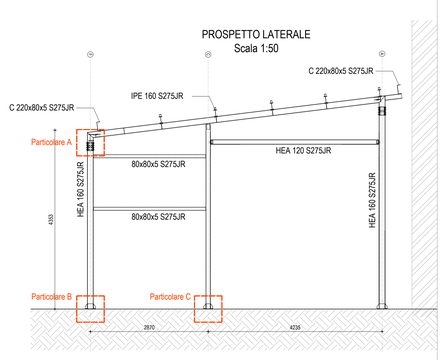


PROSPETTO LATERALE
Scala 1:50

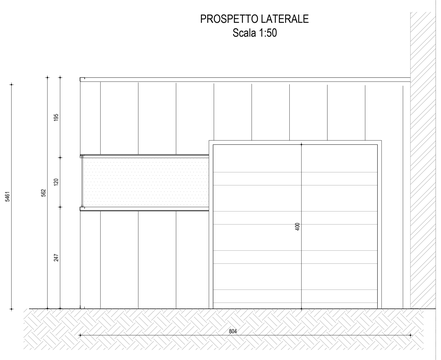


PARTICOLARE A
Scala 1:10
Spessore piastre 8 mm

Vista laterale

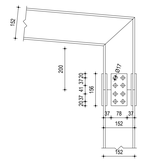



Vista frontale

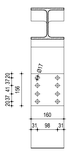


PARTICOLARE B
Scala 1:10

Trafondi Ø16 mm Vite cl. 8.8 Dadi 8 o 10
Profilo colonna: HEA 160
Materiale colonna: Acciaio S275
Materiale piast. Sotra e nervature: Acciaio S275
Spessore dei cordoni di saldatura 5 mm

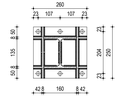

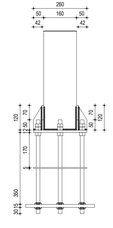

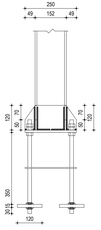

PARTICOLARE C
Scala 1:10

Trafondi Ø16 mm Vite cl. 8.8 Dadi 8 o 10
Profilo colonna: HEA 120
Materiale colonna: Acciaio S275
Materiale piast. Sotra e nervature: Acciaio S275
Spessore dei cordoni di saldatura 5 mm

