MATERIALI E PRESCRIZIONI

CALCESTRUZZO	FONDAZIONI MURI CONTRO TERRA	TRAVI - SOLETTE POGGIOLI - SCALE	PILASTRI-SETTI NUCLEI ASCENSORE
CLASSE DI RESISTENZA	C 25/30 R ck= 30 MPa	C 25/30 R ck= 30 MPa	C 25/30 R ck= 30 MPa
CLASSE DI ESPOSIZIONE	XC2	XC1	XC1
CLASSE DI CONSISTENZA (Slump)	S4	S4	S4
DIAMETRO MAX AGGREGATI	32 mm	22 mm	22 mm

	TIPO	f yk	f tk	f yd
ACCIAIO PER ARMATURE LENTE (6<Ø<40 mm)	B450C	> 450 MPa	> 540 MPa	> 391 MPa
ACCIAIO PER RETI ELETTROSALDATE (5<Ø<10 mm)	B450A	> 450 MPa	> 540 MPa	> 391 MPa

COPRIFERRO NOMINALE C nom			Chiusura staffe	Ancoraggio barre
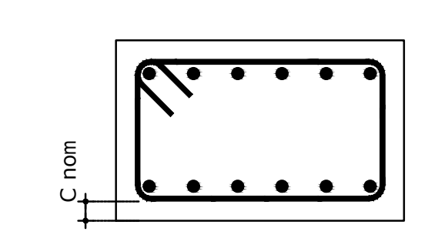 C nom	FONDAZIONI	40 mm	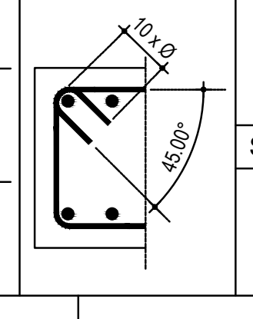 10 x Ø 45.00°	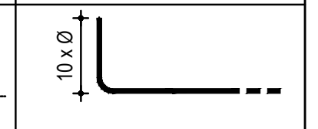 10 x Ø
	MURI CONTRO TERRA			Sovrapposizione barre
	TRAVI - SOLETTE	30 mm		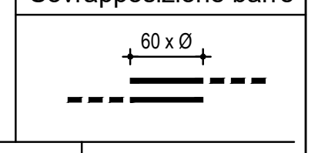 60 x Ø
	POGGIOLI - SCALE			
	PILASTRI - SETTI	30 mm		
	NUCLEI ASCENSORE			

DIAMETRO BARRA	Ø < 12	12 < Ø < 16	16 < Ø < 25	25 < Ø < 40
DIAMETRO DEL MANDRINO	4 x Ø	5 x Ø	8 x Ø	10 x Ø

NOTE:

COMUNE DI SIRMIONE PROVINCIA DI BRESCIA

Og[redacted]
[redacted]

[redacted]
[redacted]

PROGETTO STRUTTURE

Oggetto tavola
- Fondazioni
- Elevazione
- Particolari

Tav. n°	Revisione
01	00

Data	Scale
	1:25 - 1:10

Progettista
[redacted]

Pianta
scala 1:25

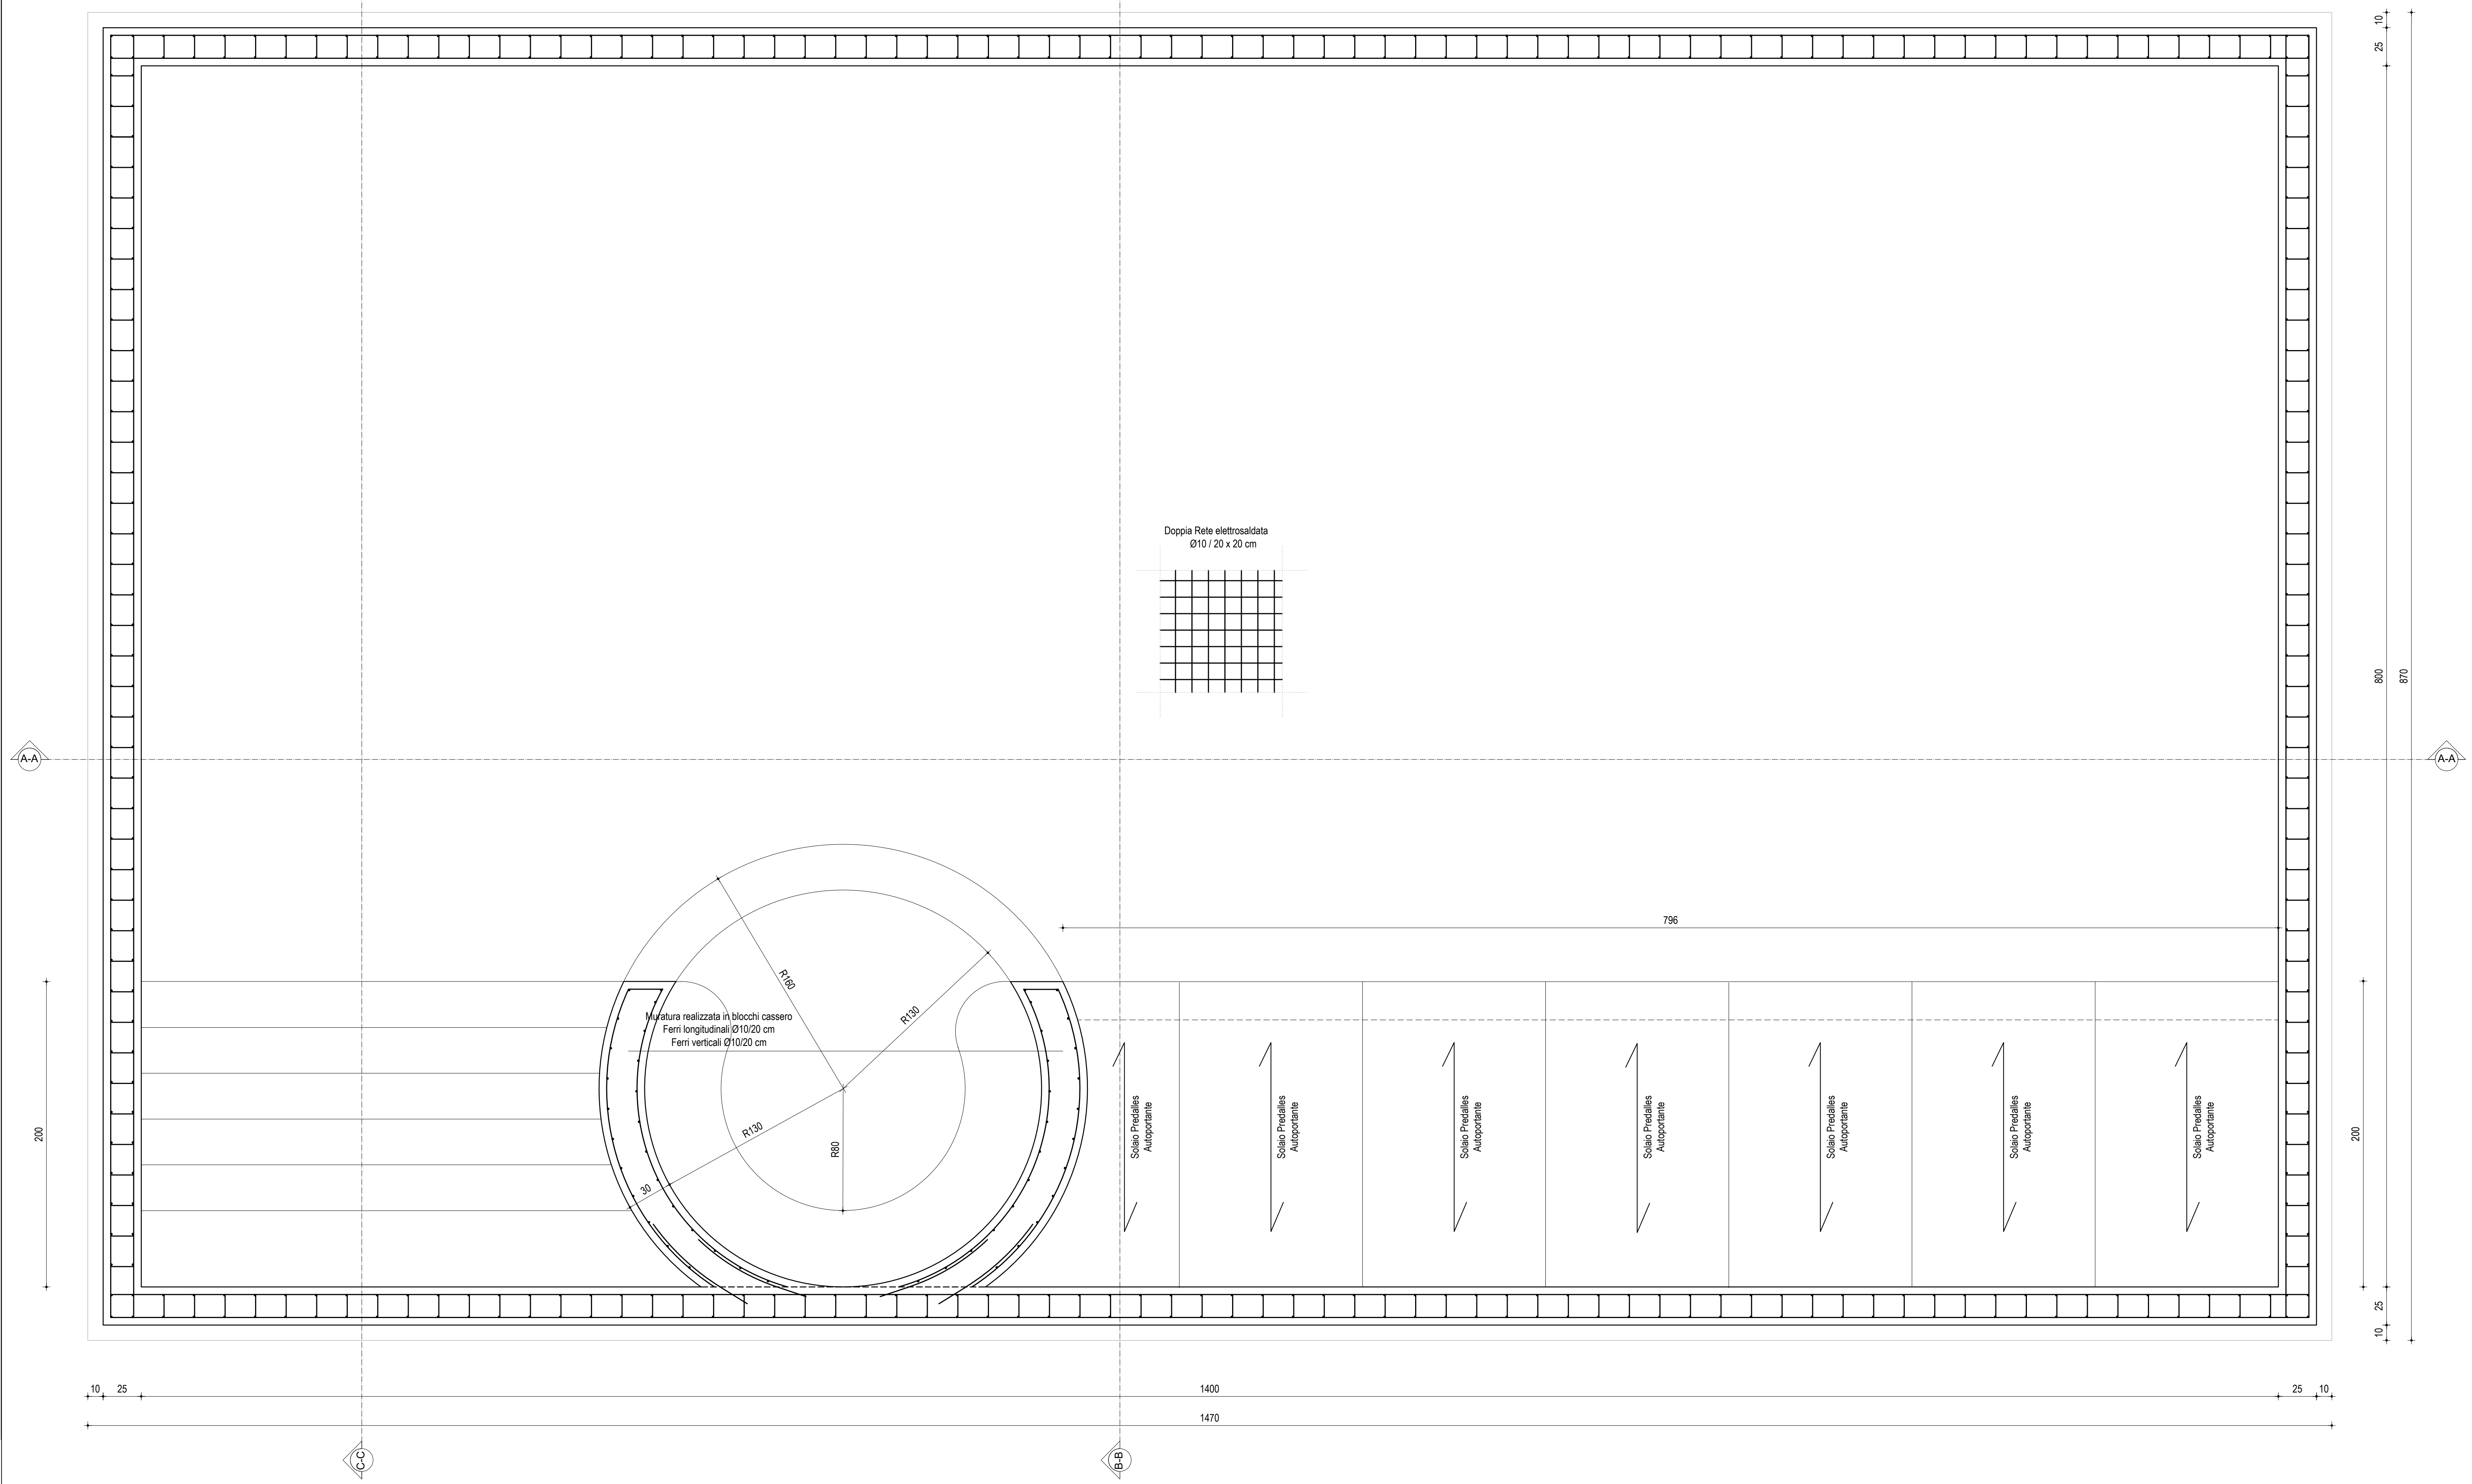
C-C
B-B
A-A
Doppia Rete elettrosaldata
Ø10 / 20 x 20 cm
796
Muratura realizzata in blocchi cassero
Ferri longitudinali Ø10/20 cm
Ferri verticali Ø10/20 cm
R160
R130
R130
R80
30
Solaio Predalles
Autoportante
200
800
870
10
25
1400
1470

Sezione B-B
scala 1:25

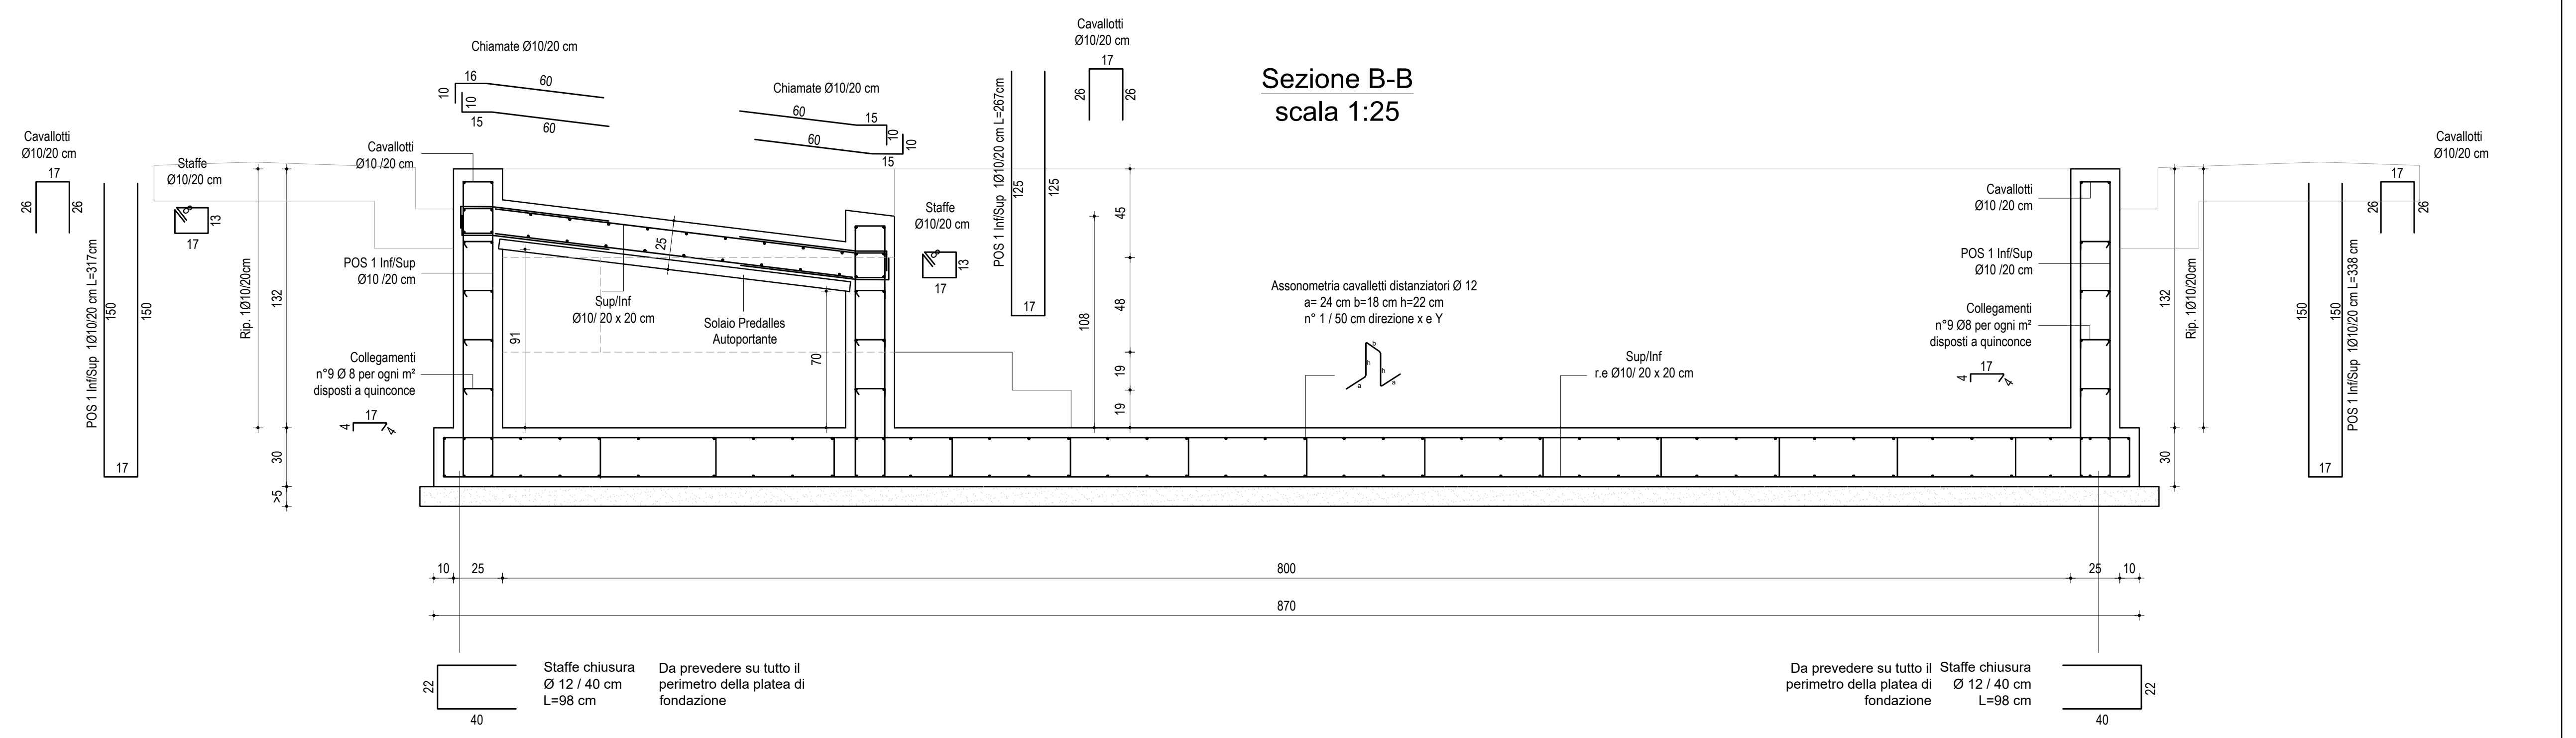

Sezione C-C
scala 1:25

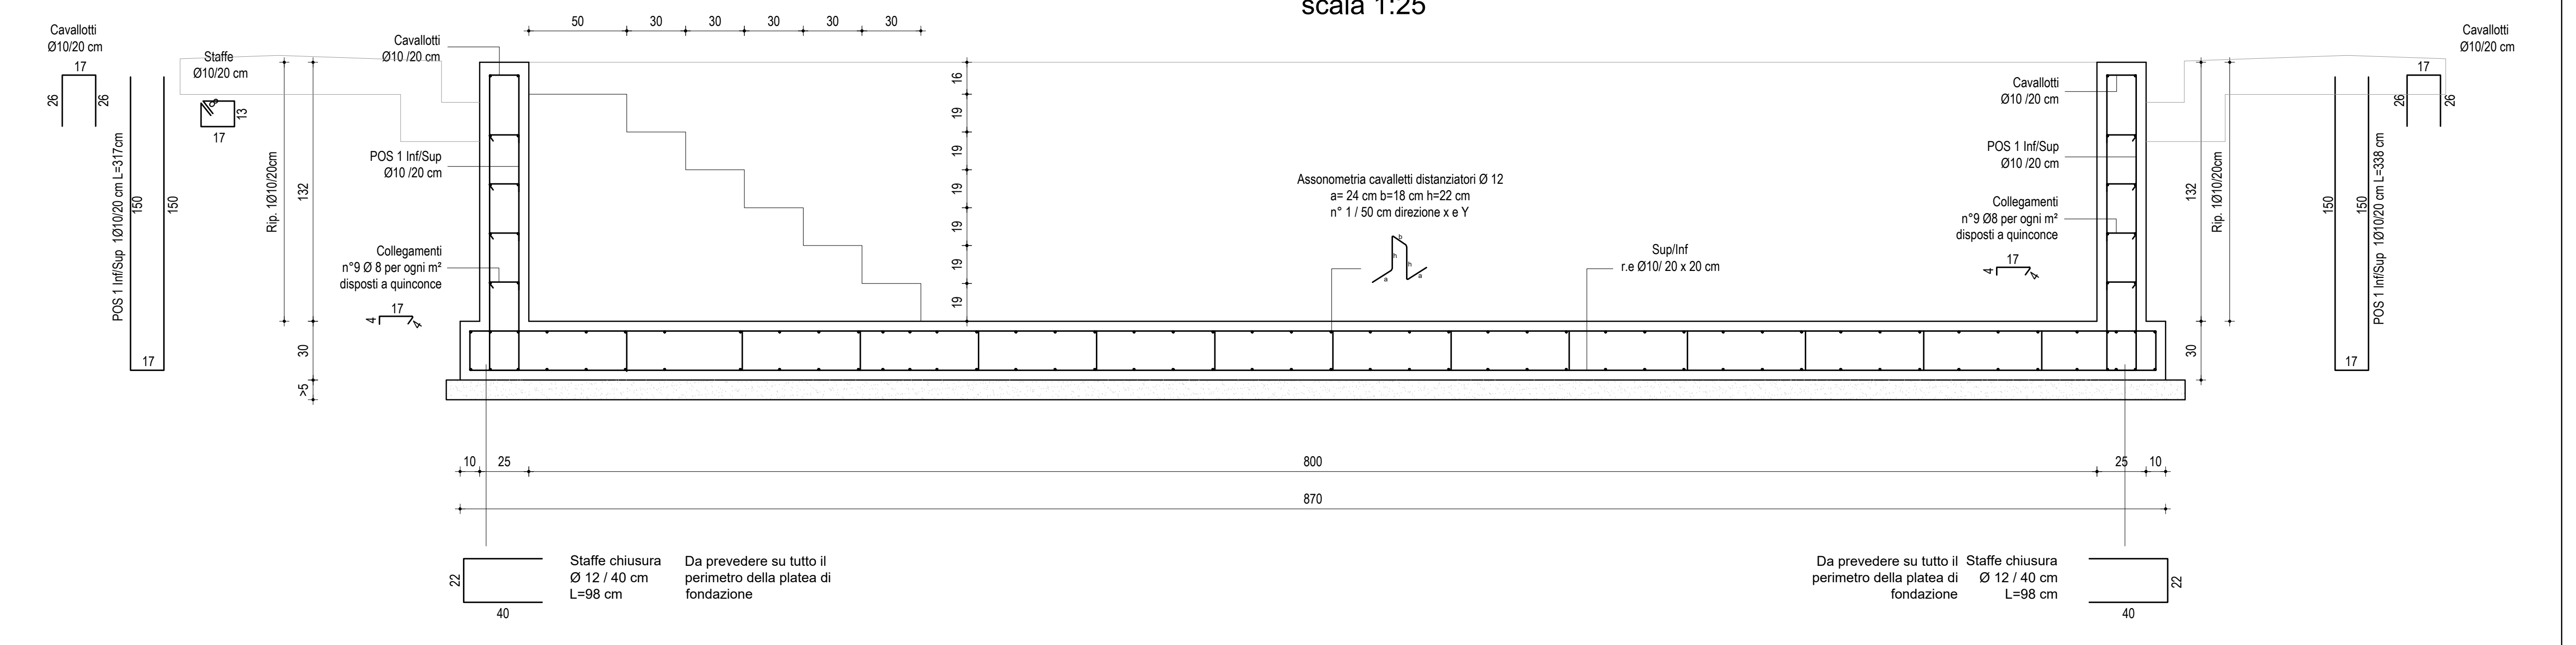

Sezione A-A
scala 1:25

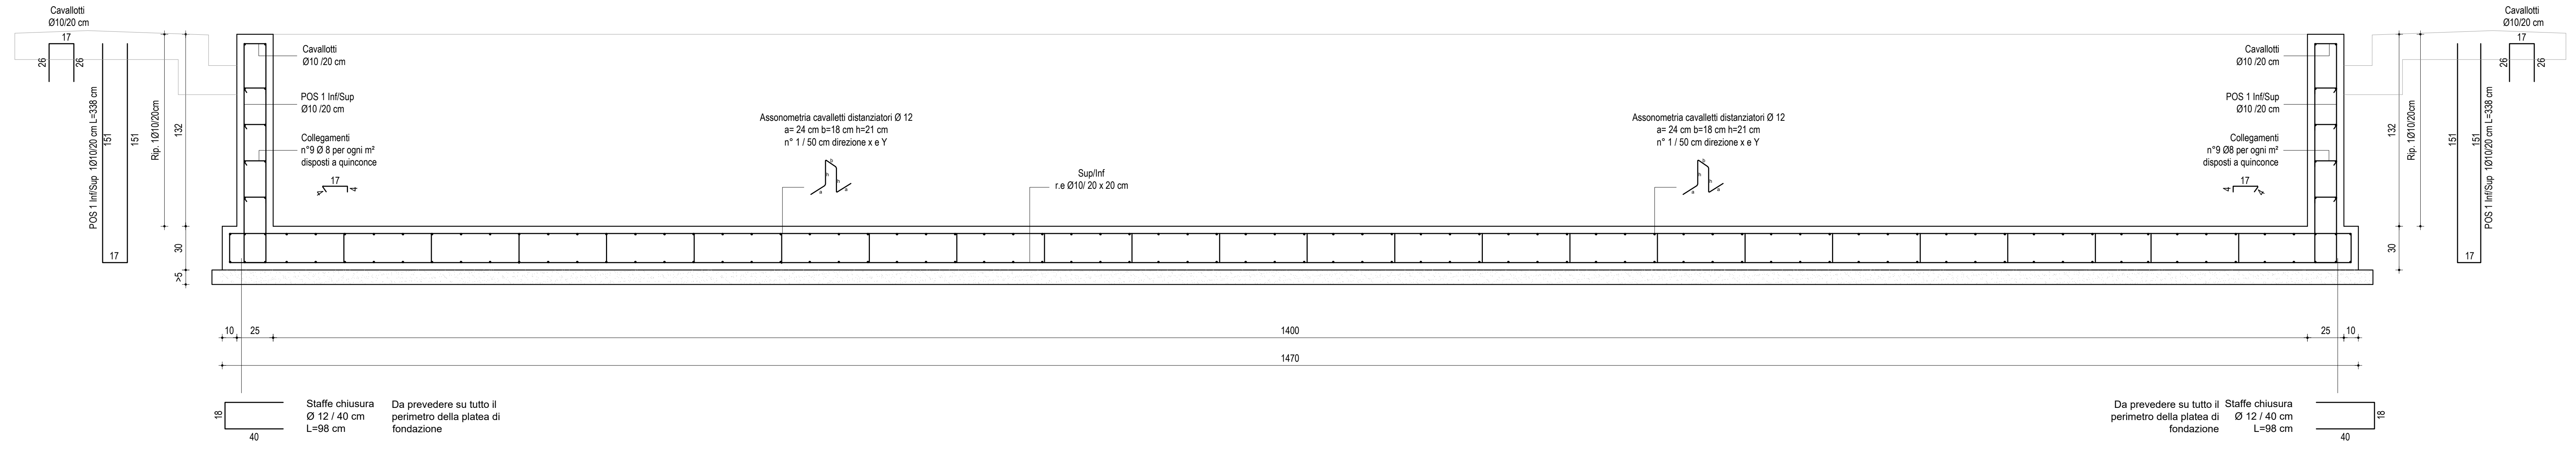

Particolare armatura d'angolo
scala 1: 25

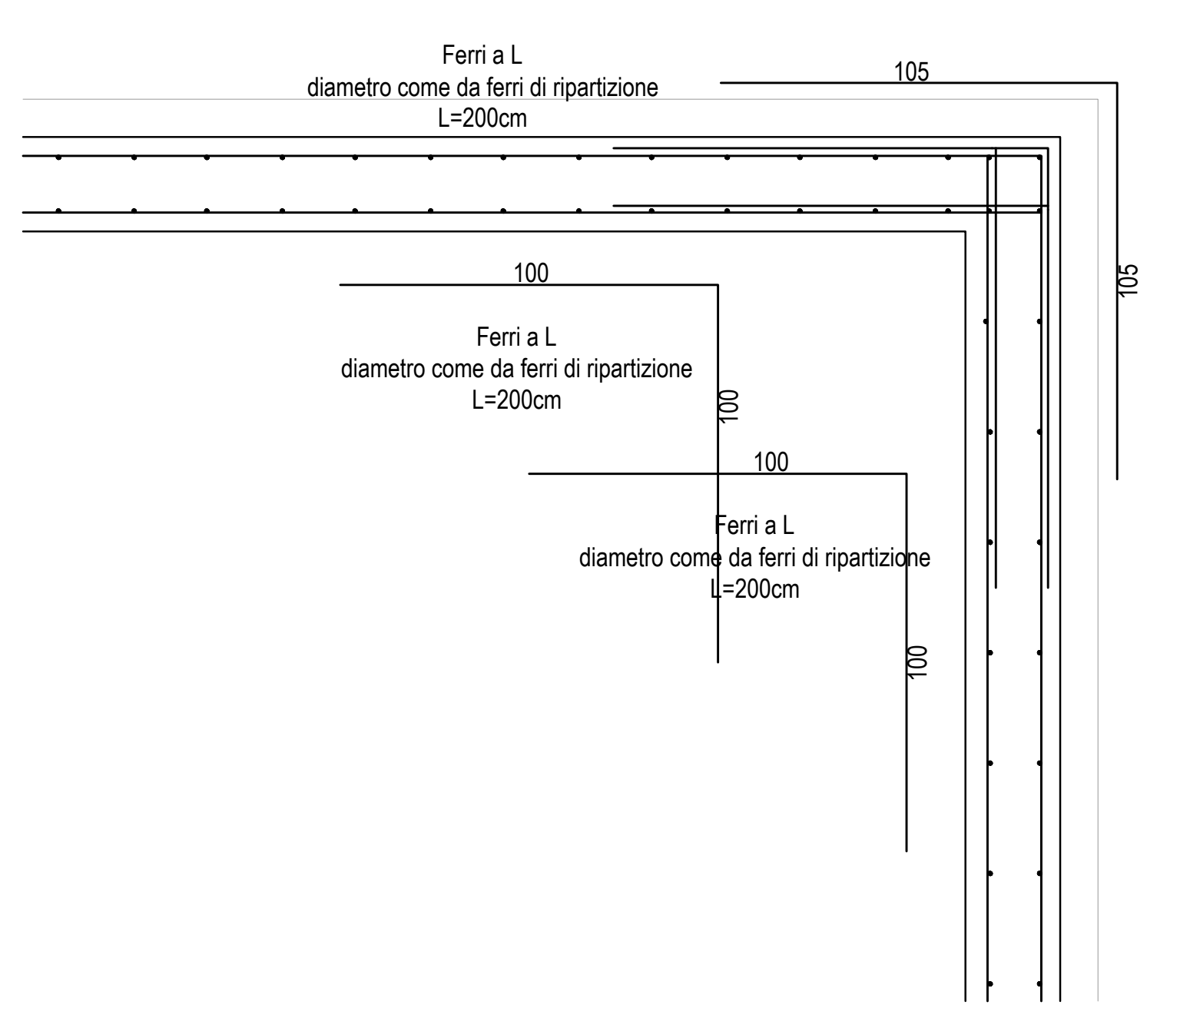
Ferri a L
diametro come da ferri di ripartizione
L=200cm
105
105
100
Ferri a L
diametro come da ferri di ripartizione
L=200cm
100
100
Ferri a L
diametro come da ferri di ripartizione
L=200cm
100

Particolare canalina
scala 1: 10