SETTO -S1-S5-
-scala 1:20-
Sezione A-A

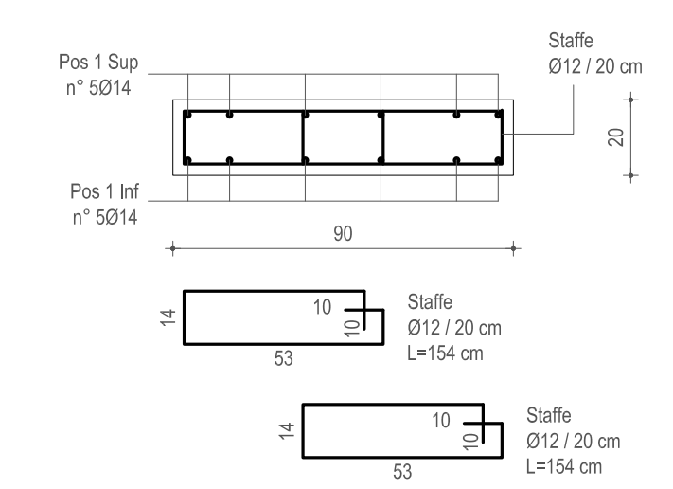

SETTO -S1-S5-
-scala 1:25-

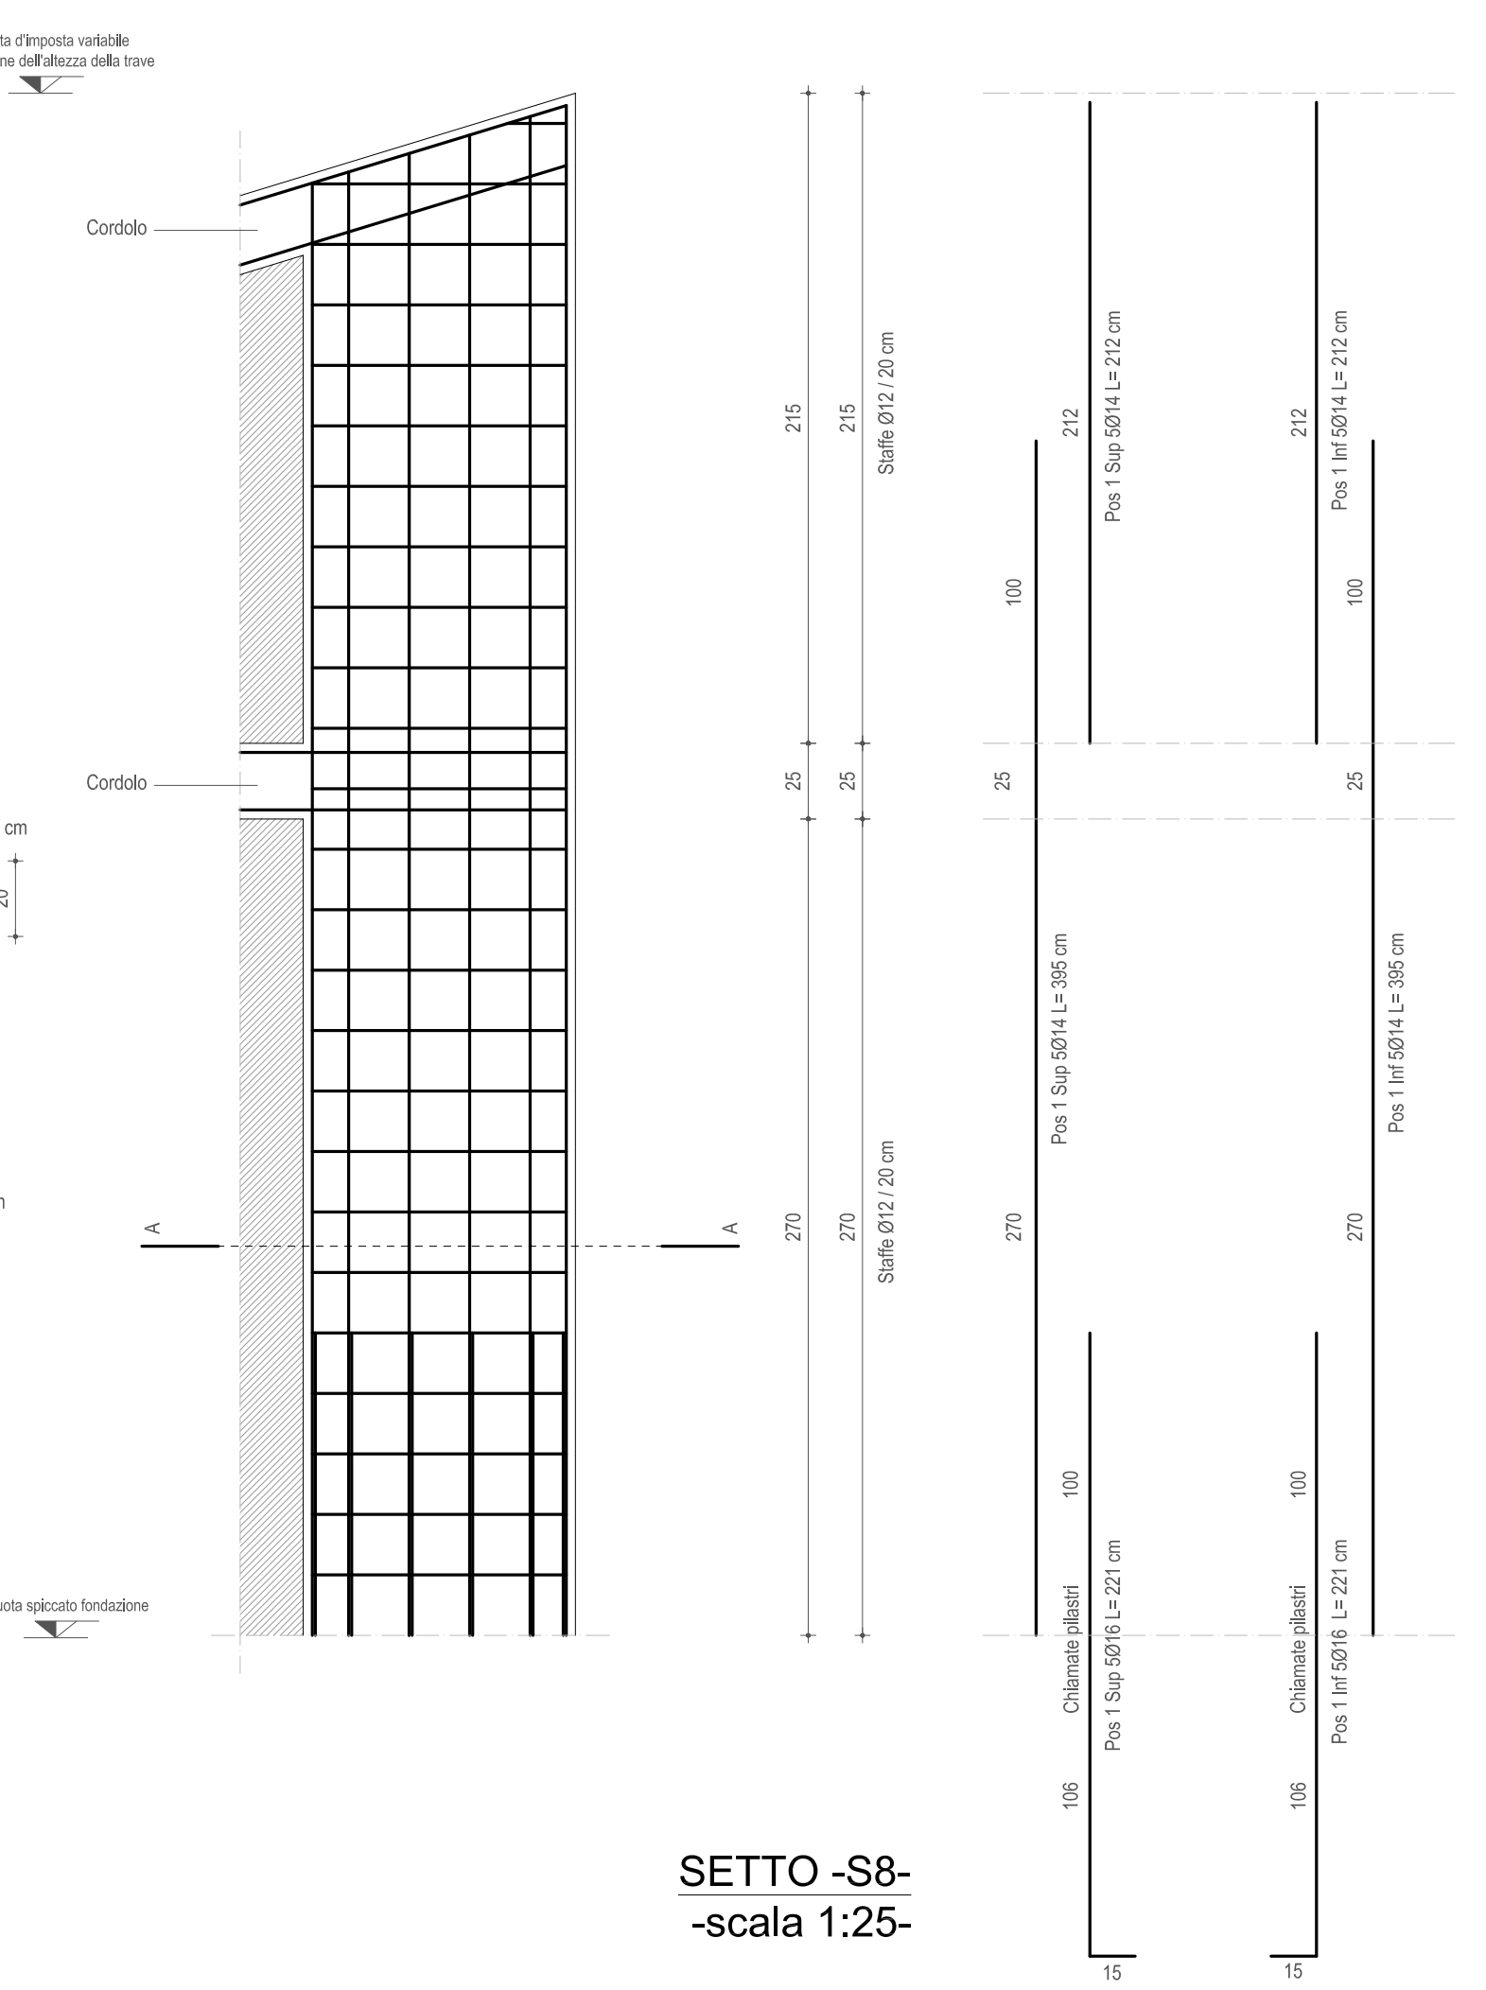

SETTO -S2-S3-S4-S9-S10-
-scala 1:20-
Sezione A-A

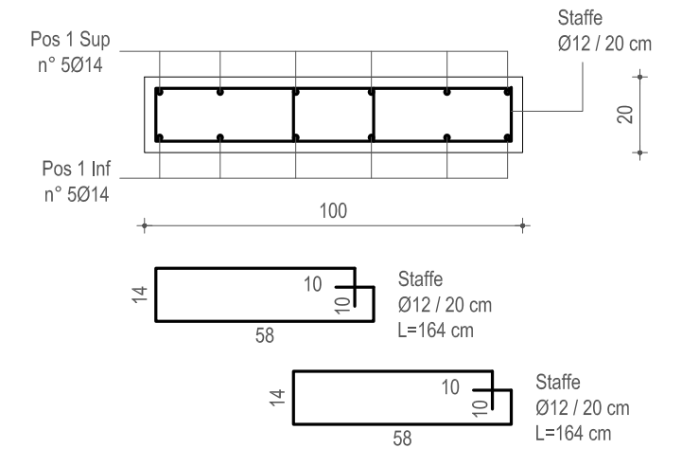

SETTO -S2-S3-S4-S9-S10-
-scala 1:25-

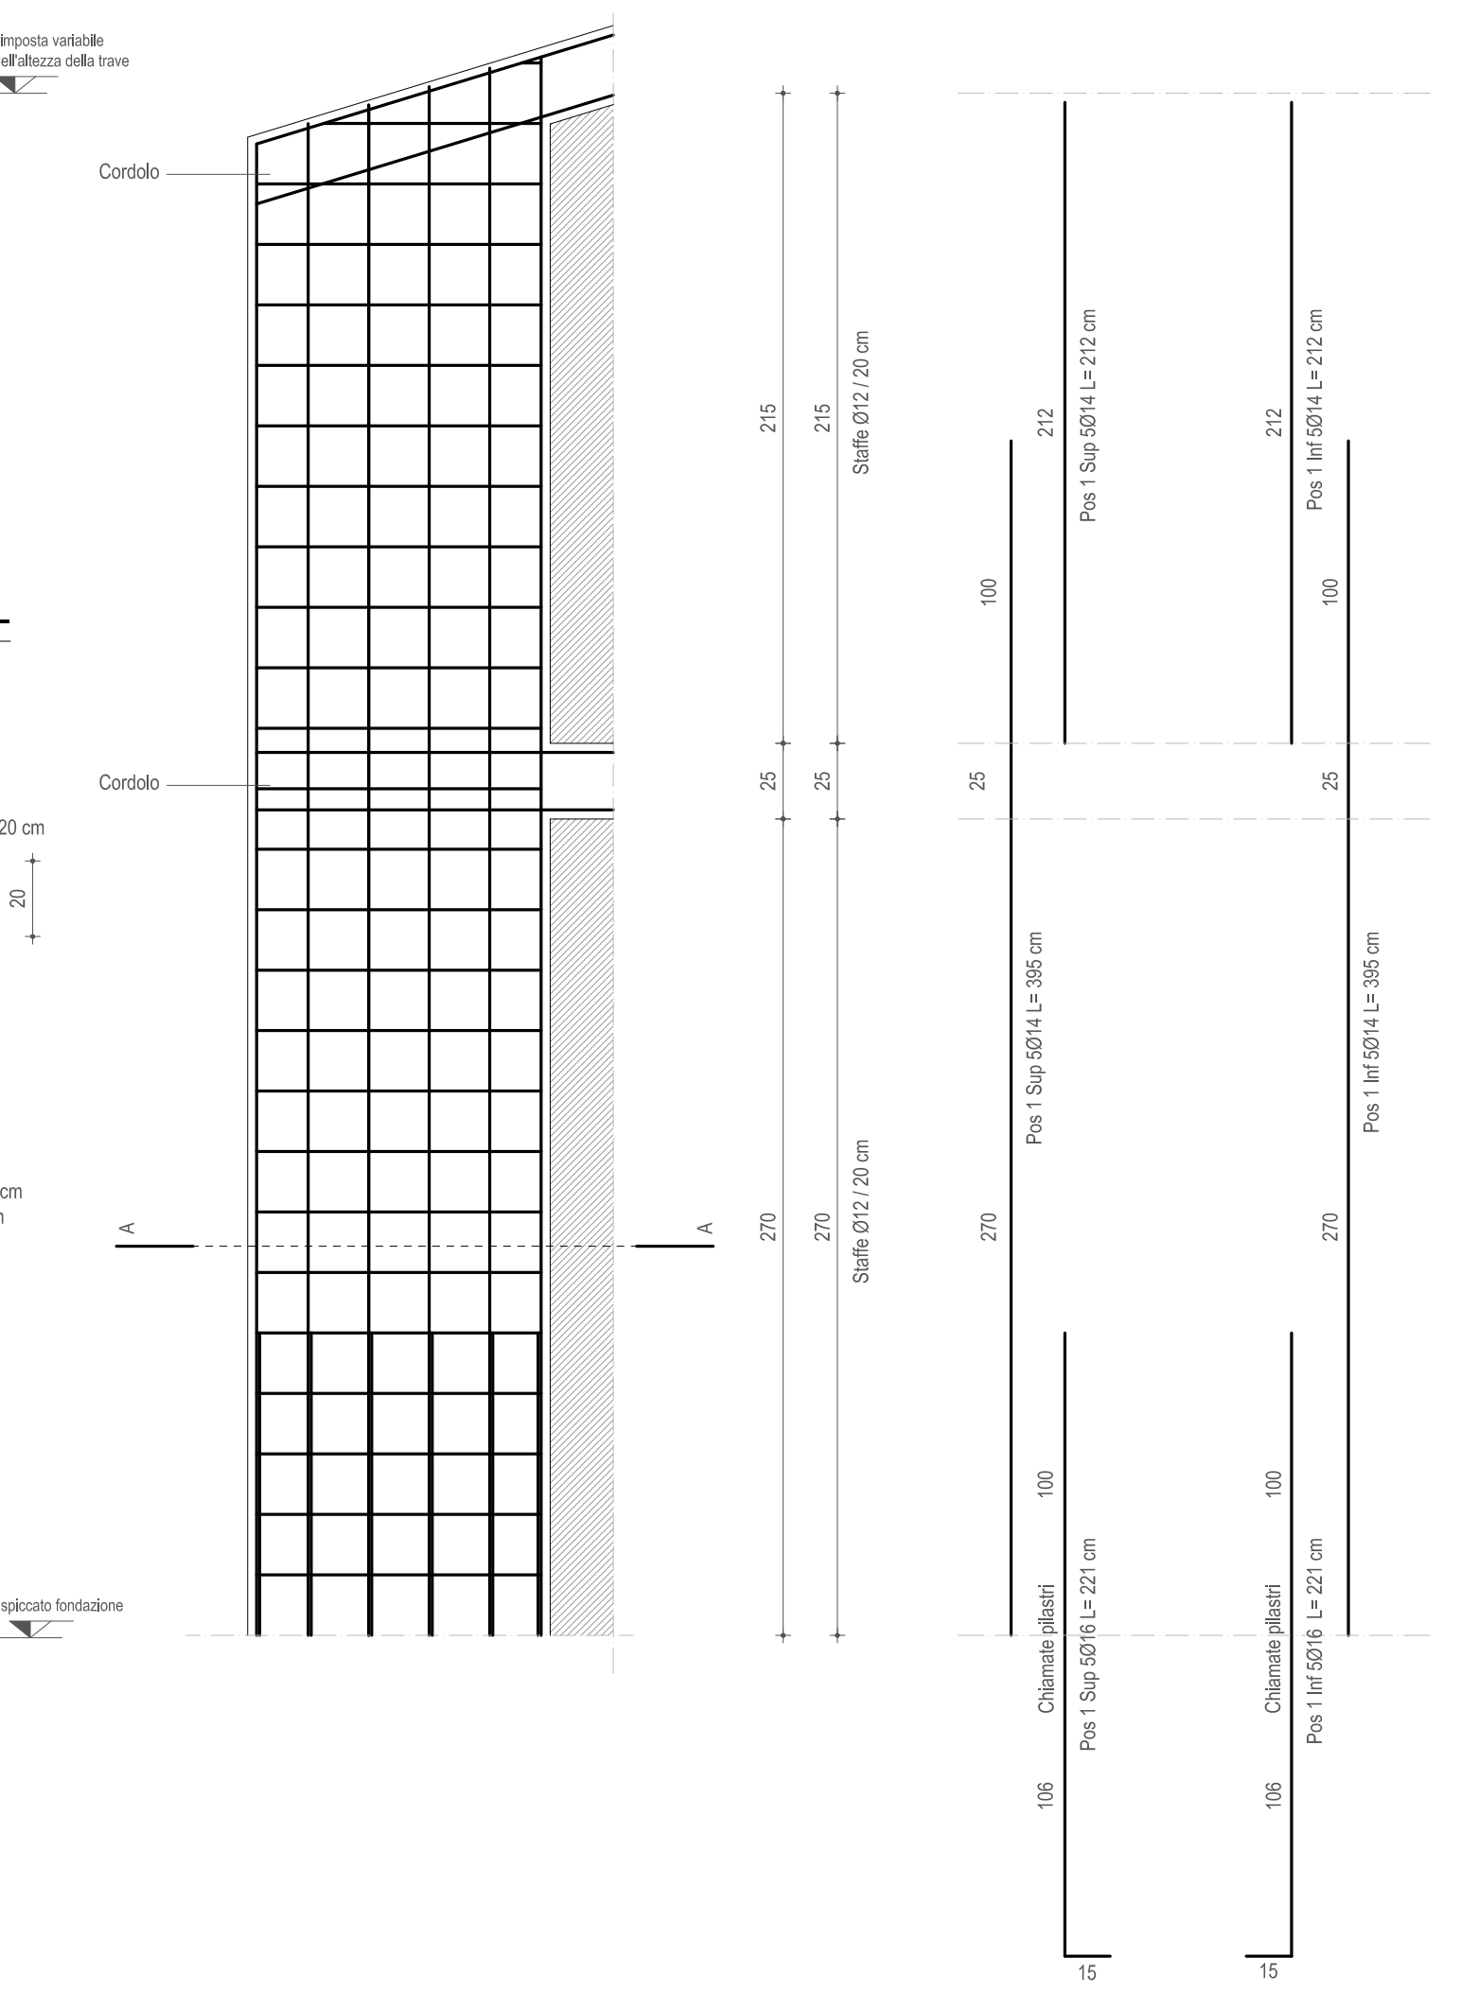

PILASTRO -S1-S5-
-scala 1:20-
Sezione A-A

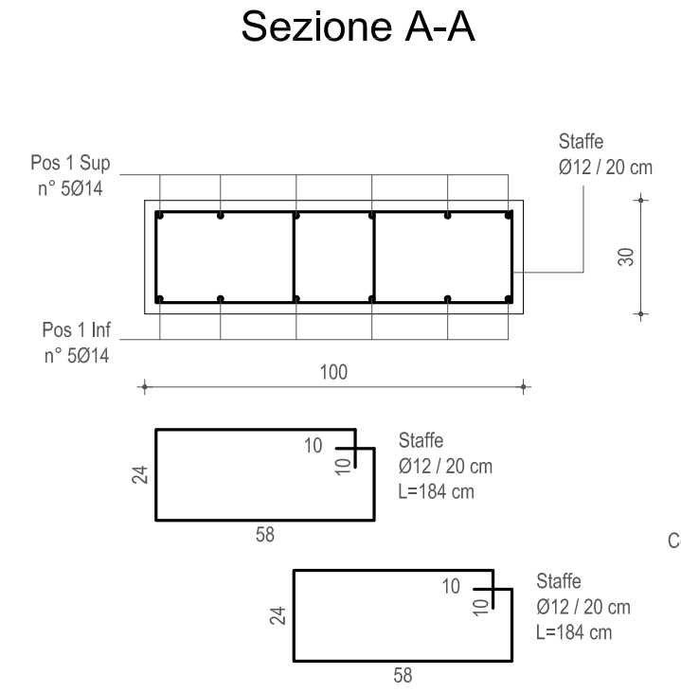

SETTO -S6-S7-
-scala 1:25-

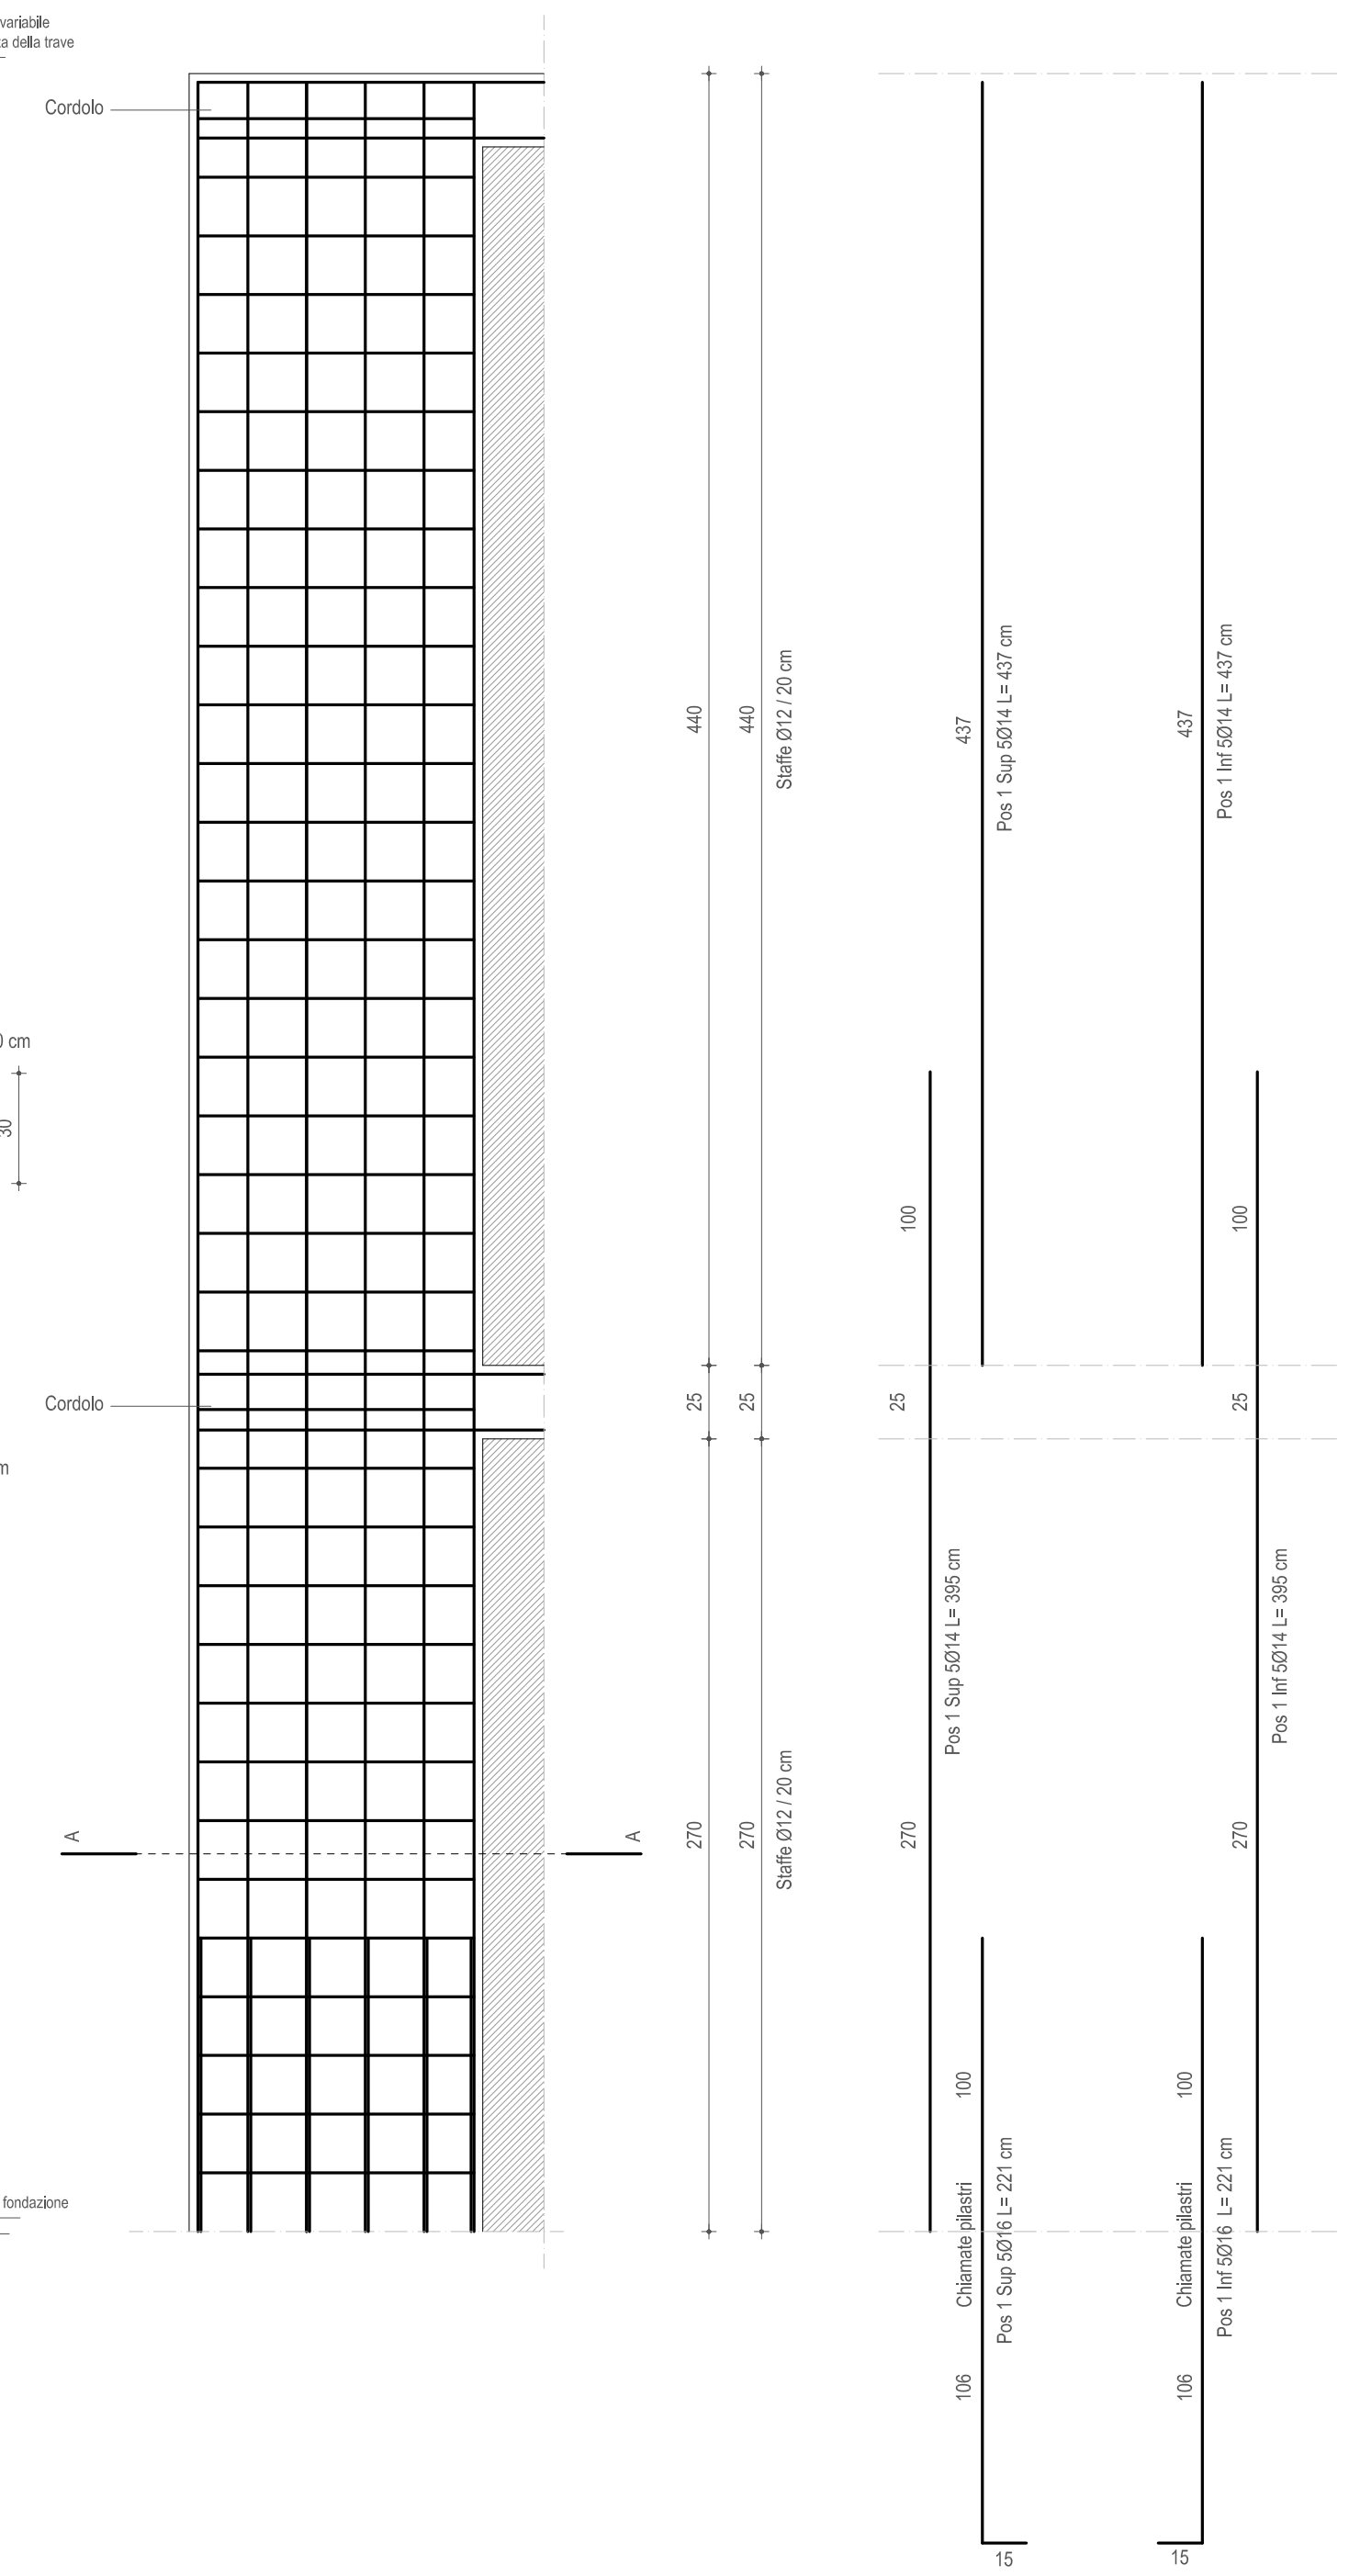

PILASTRO -P8-P9-P10-P11-P12-
-scala 1:20-
Sezione B-B

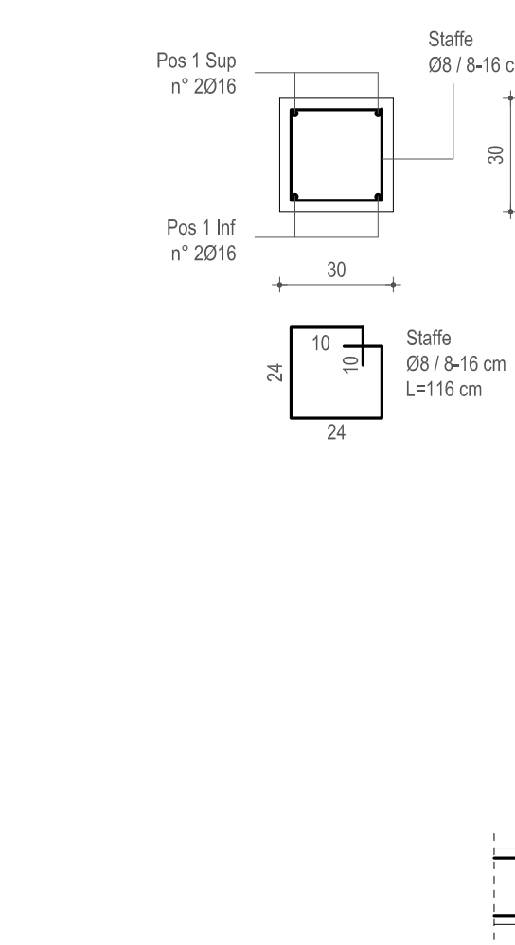

PILASTRO -P8-P9-P10-P11-P12-
-scala 1:20-
Sezione B-B

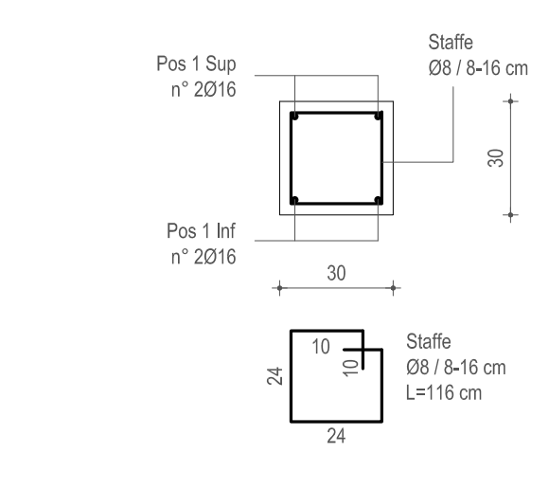

PILASTRO -P8-P9-P10-P11-P12-
-scala 1:25-

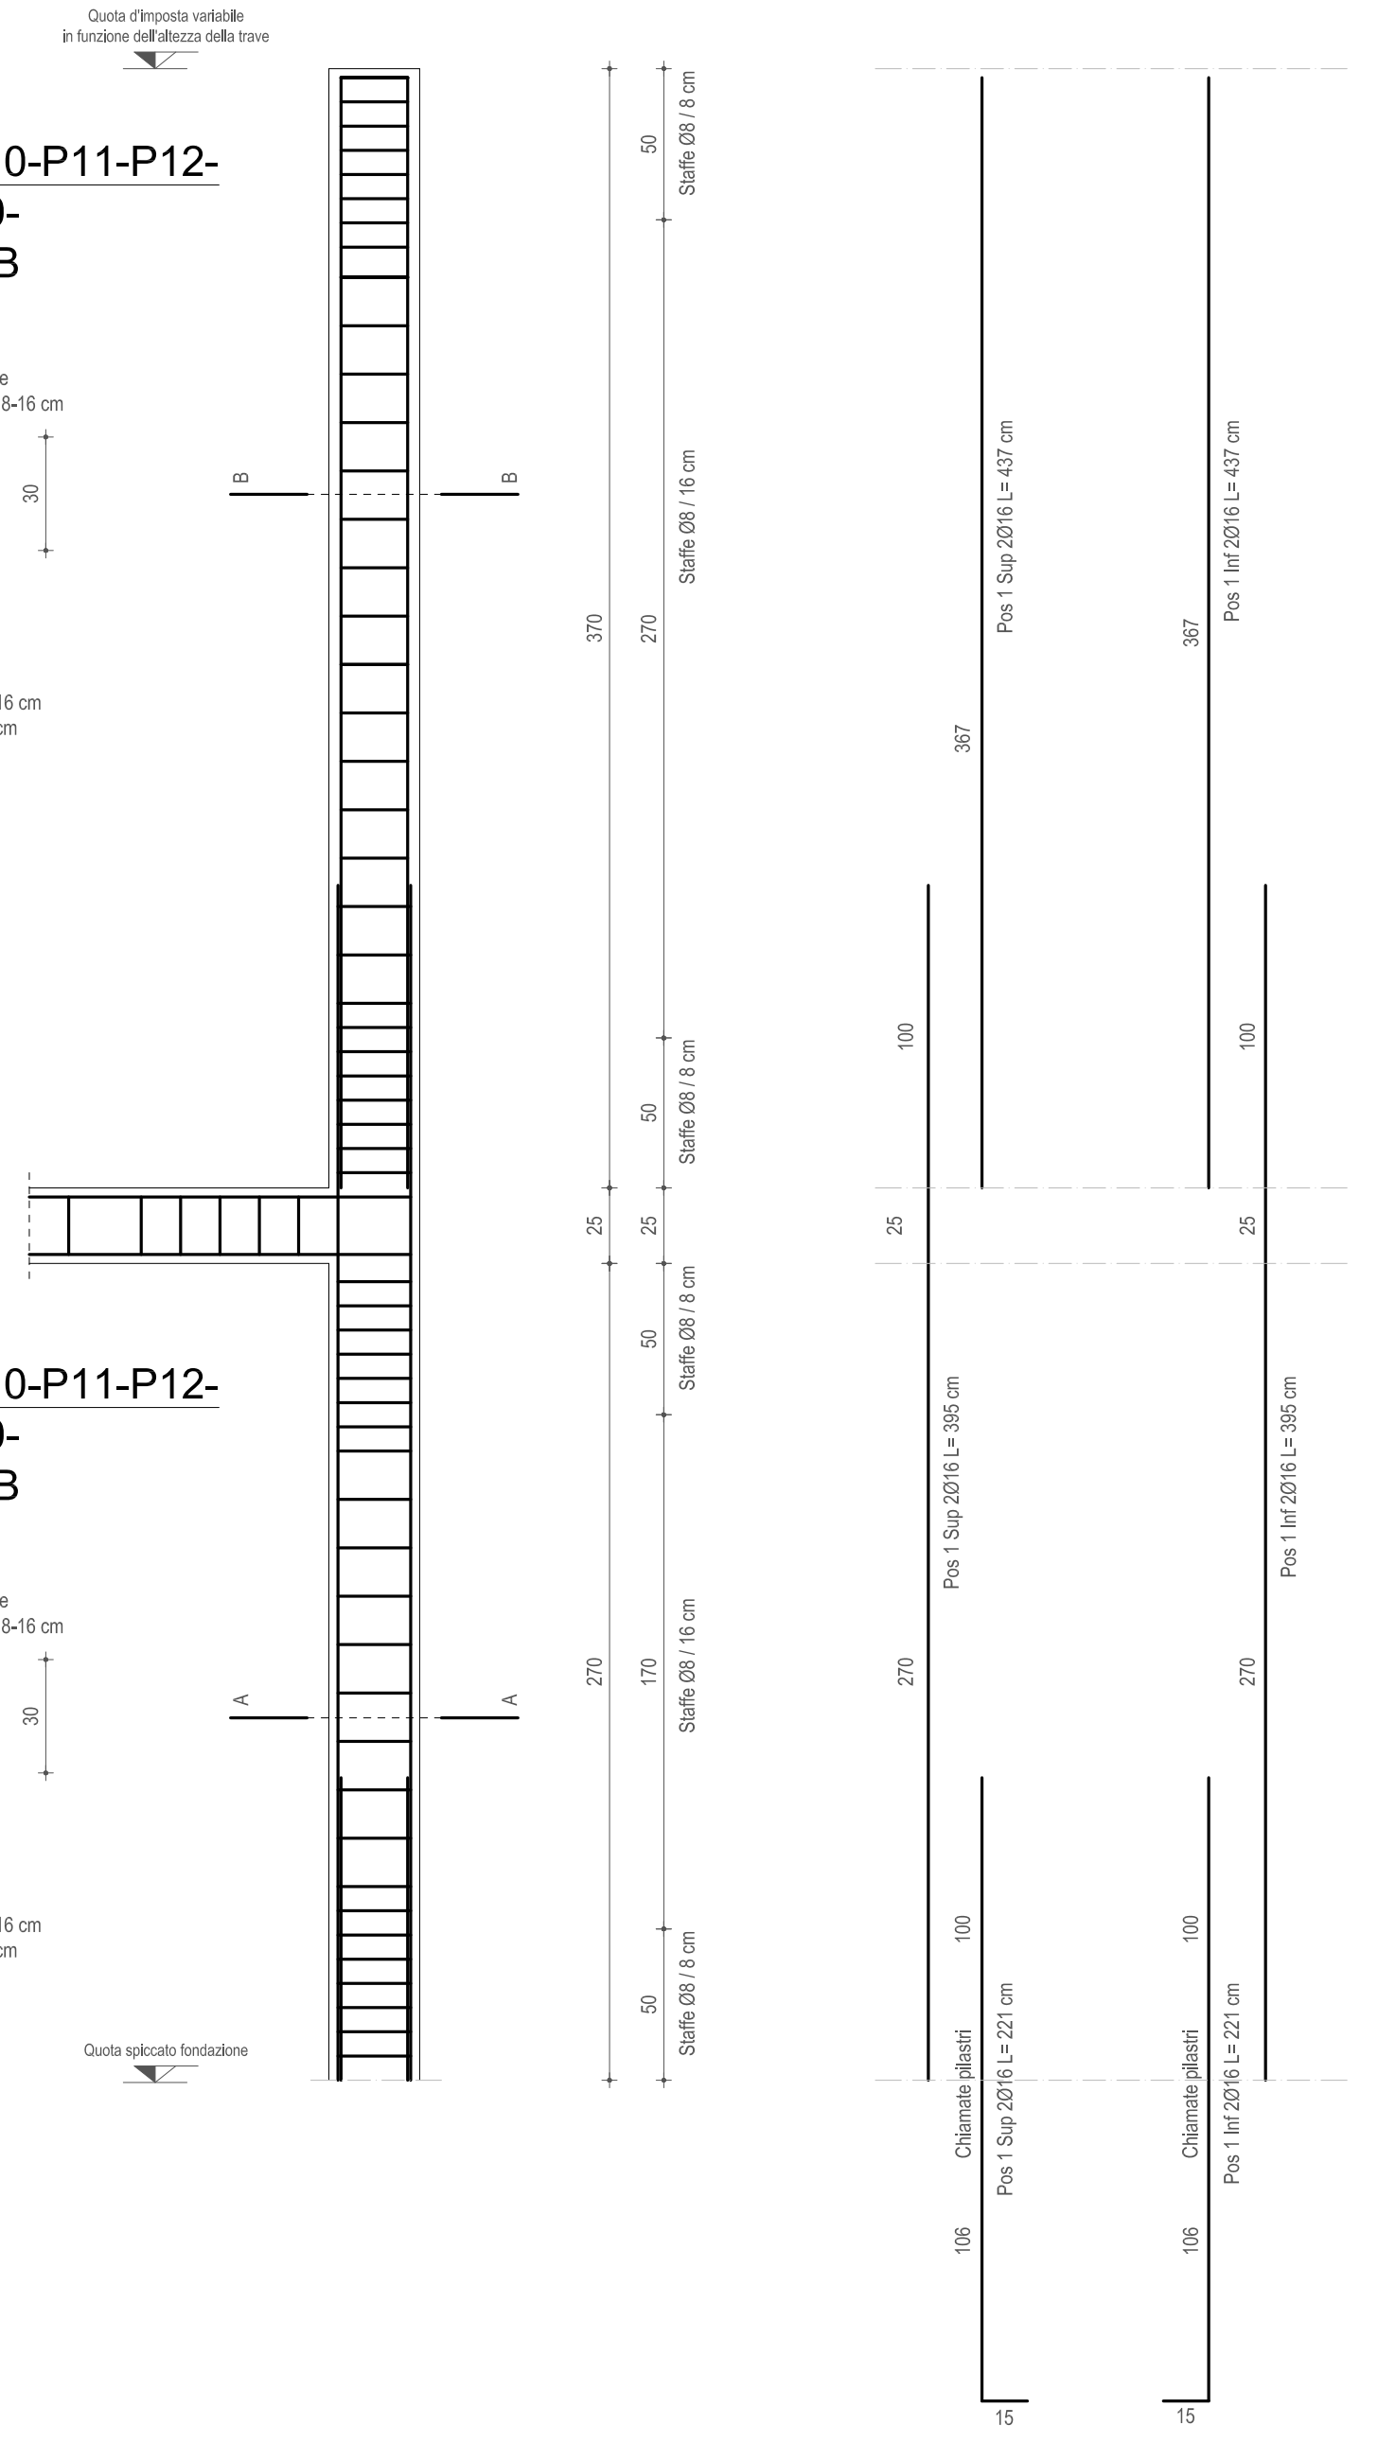

PILASTRO -P13-P14-
-scala 1:20-
Sezione B-B

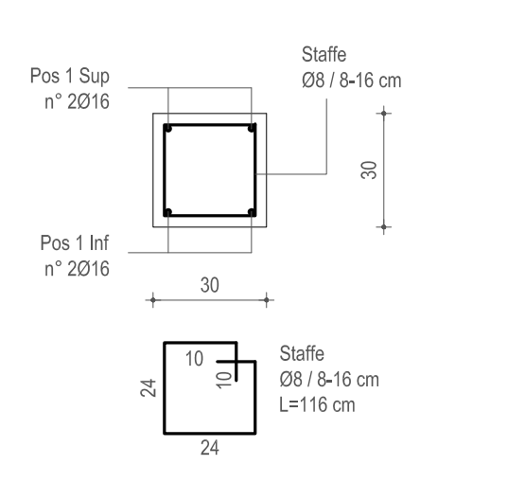

PILASTRO -P13-P14-
-scala 1:20-
Sezione A-A

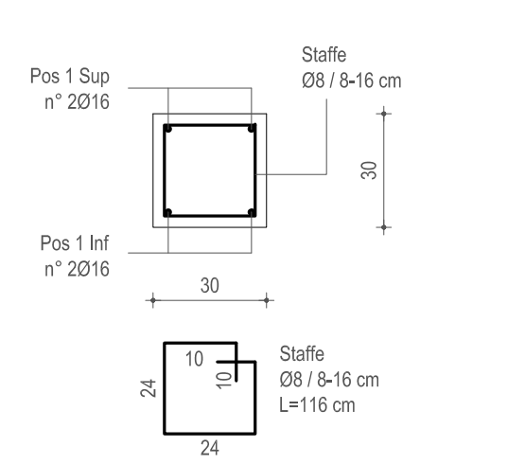

PILASTRO -P13-P14-
-scala 1:25-

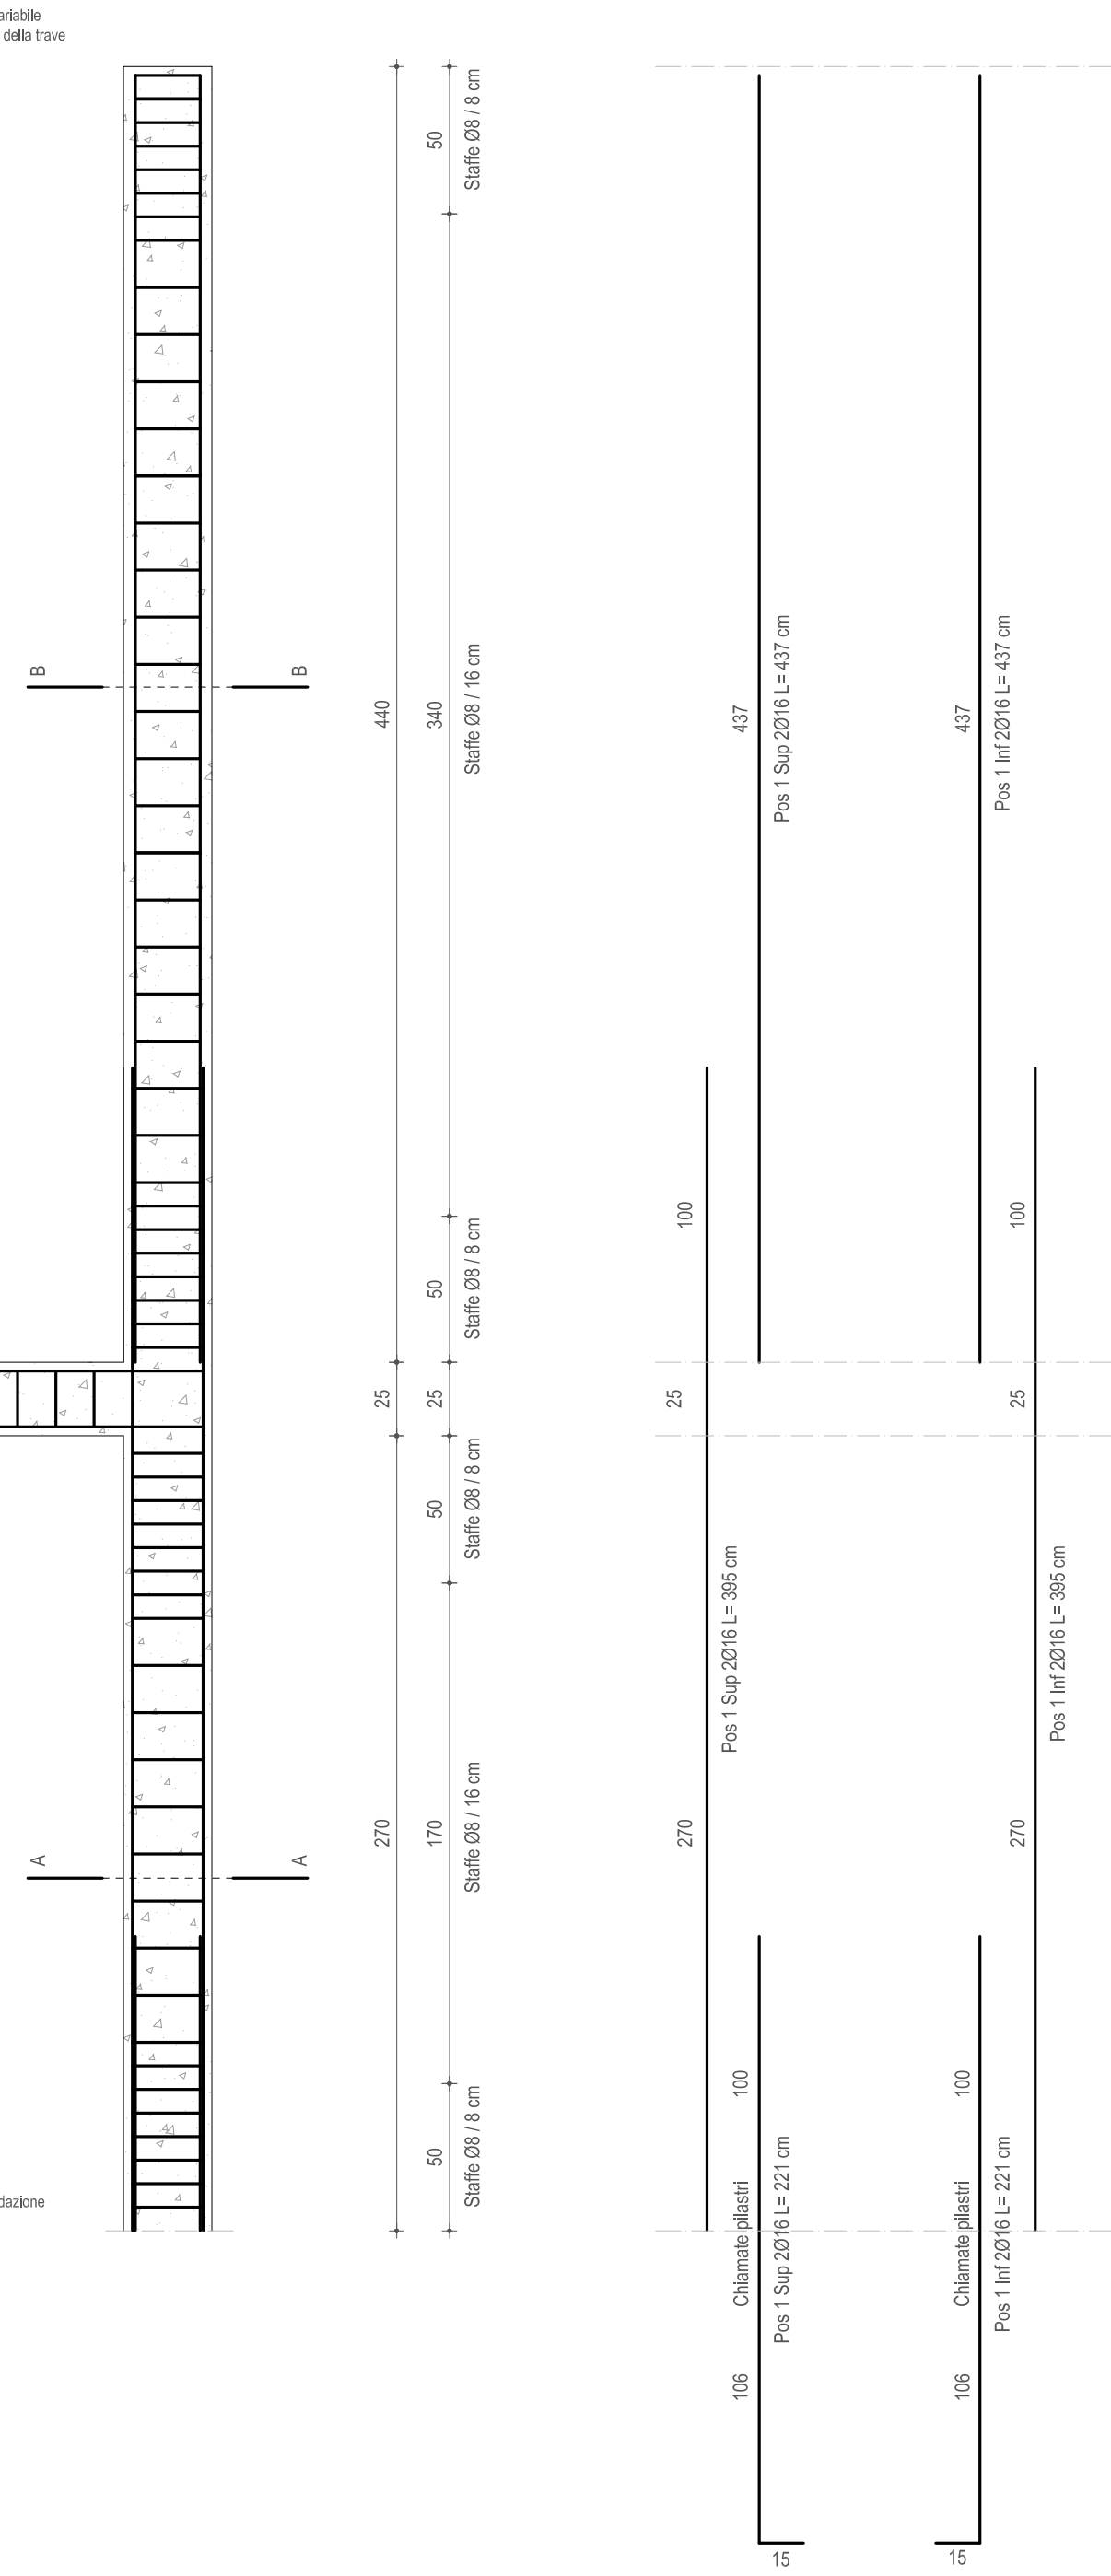

PIANTA COPERTURA -scala 1:100-

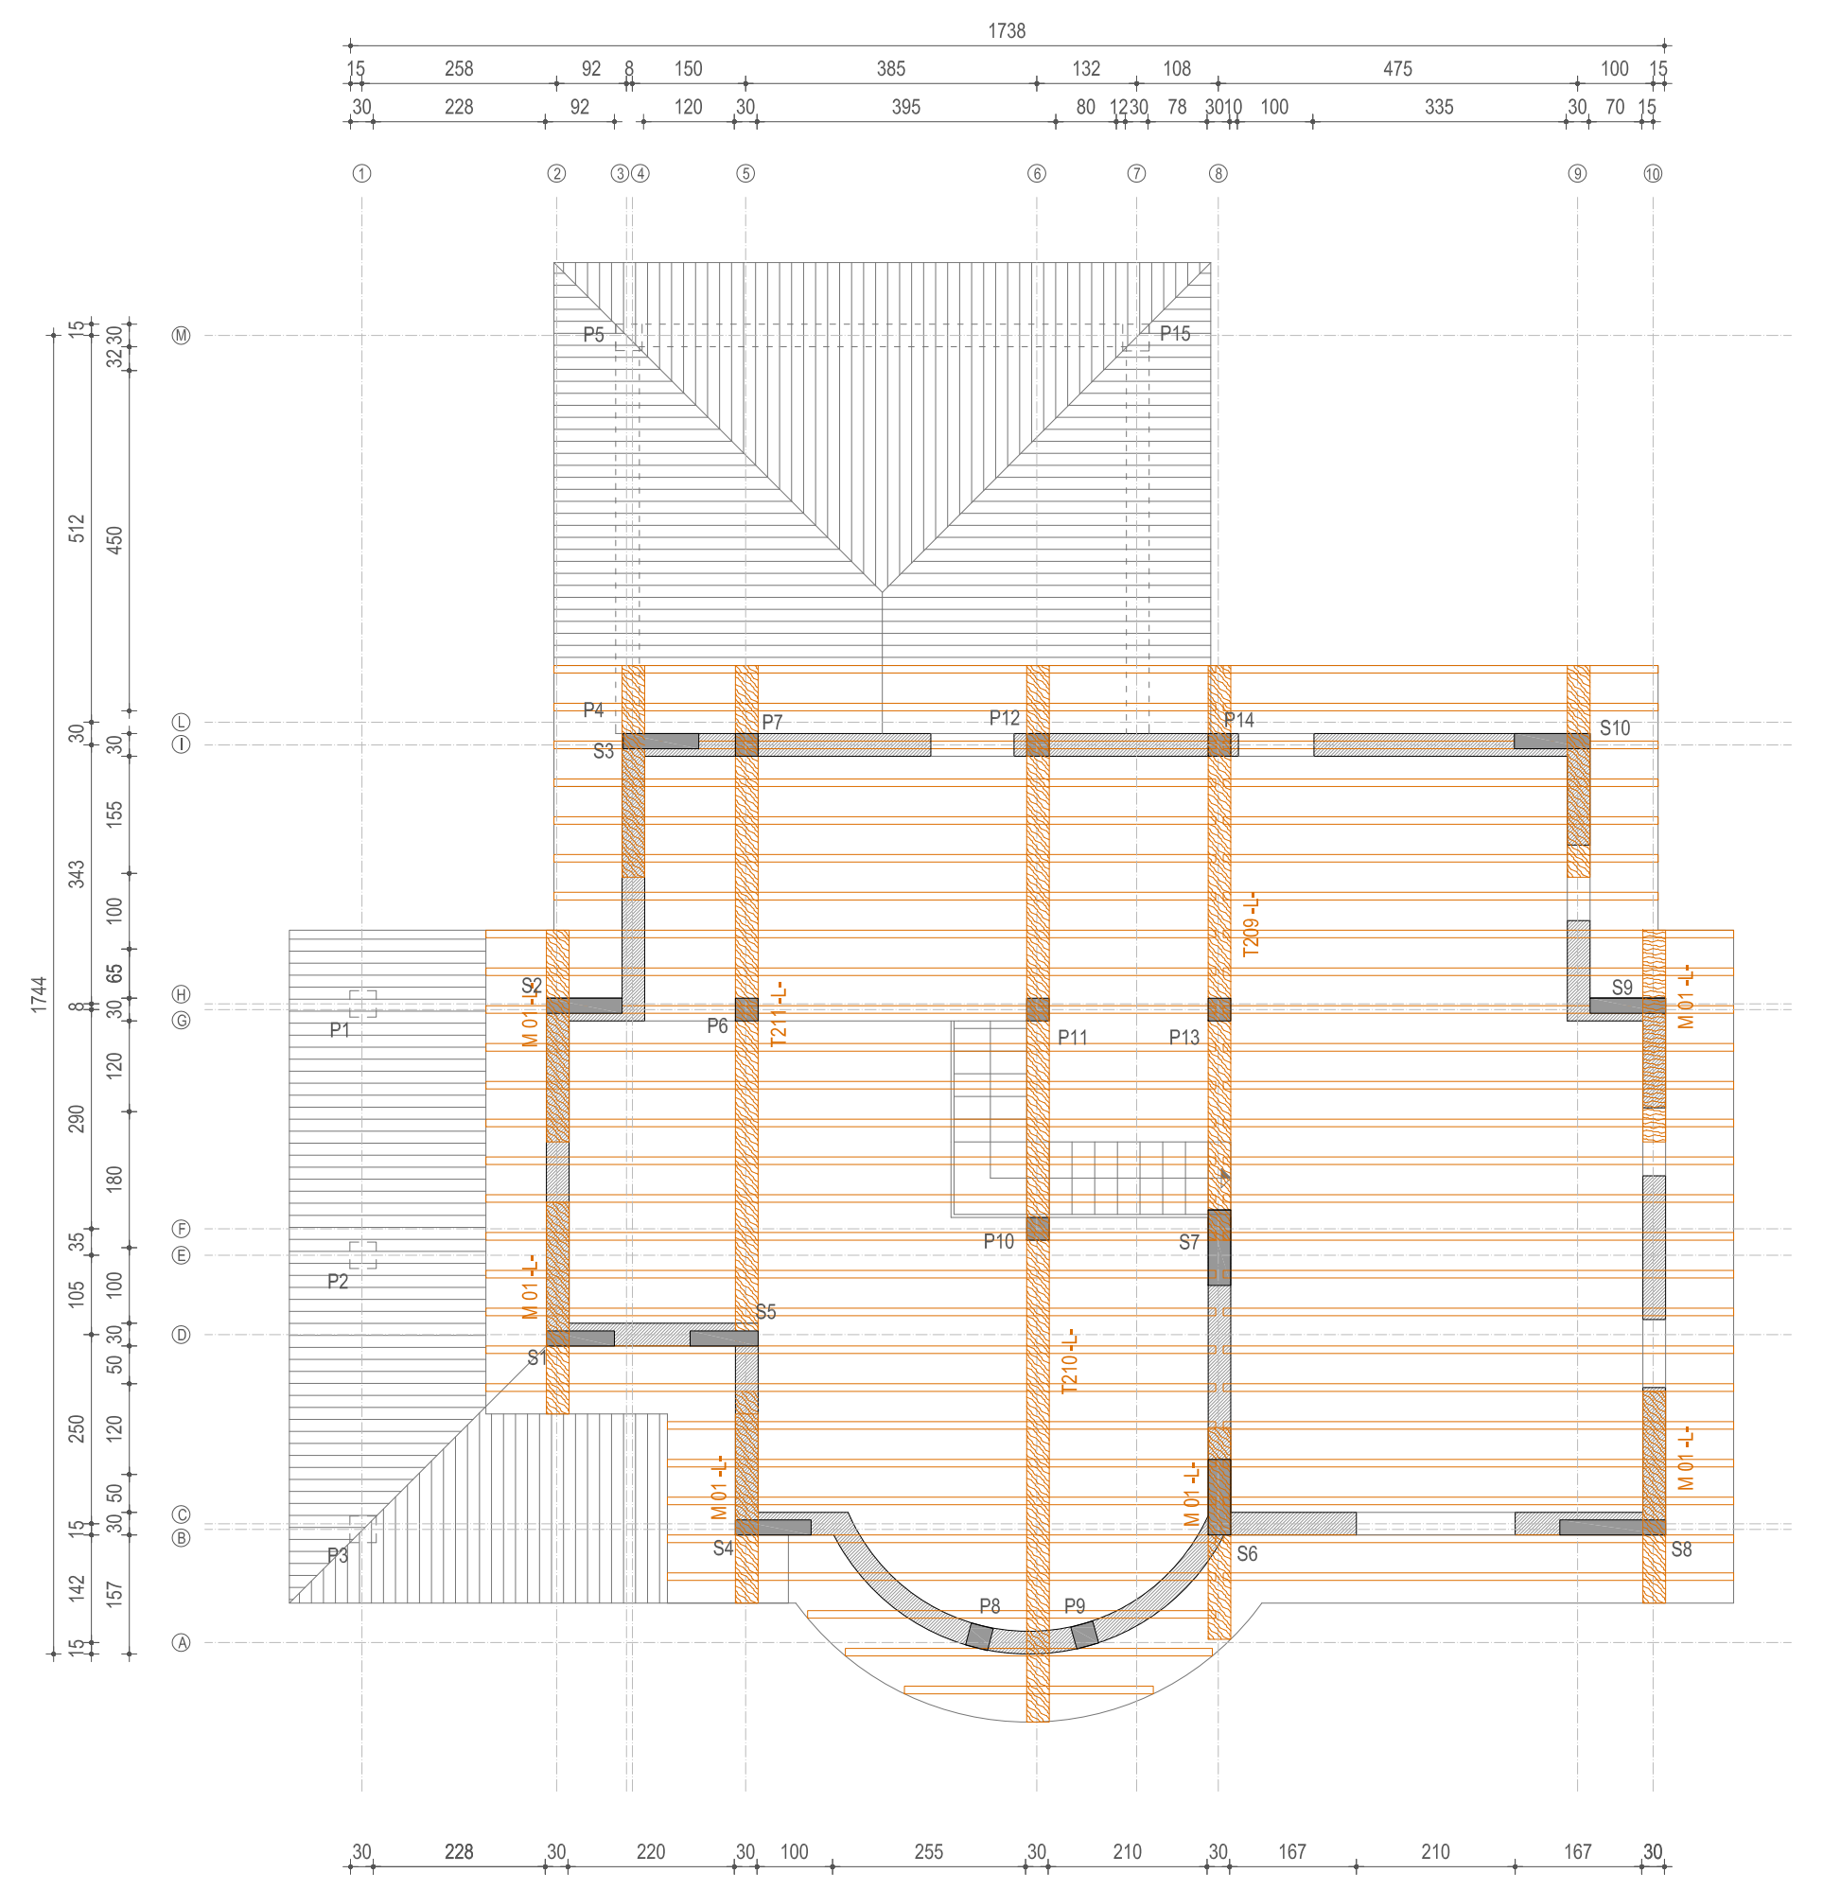

PIANTA PRIMO IMPALCATO -scala 1:100-

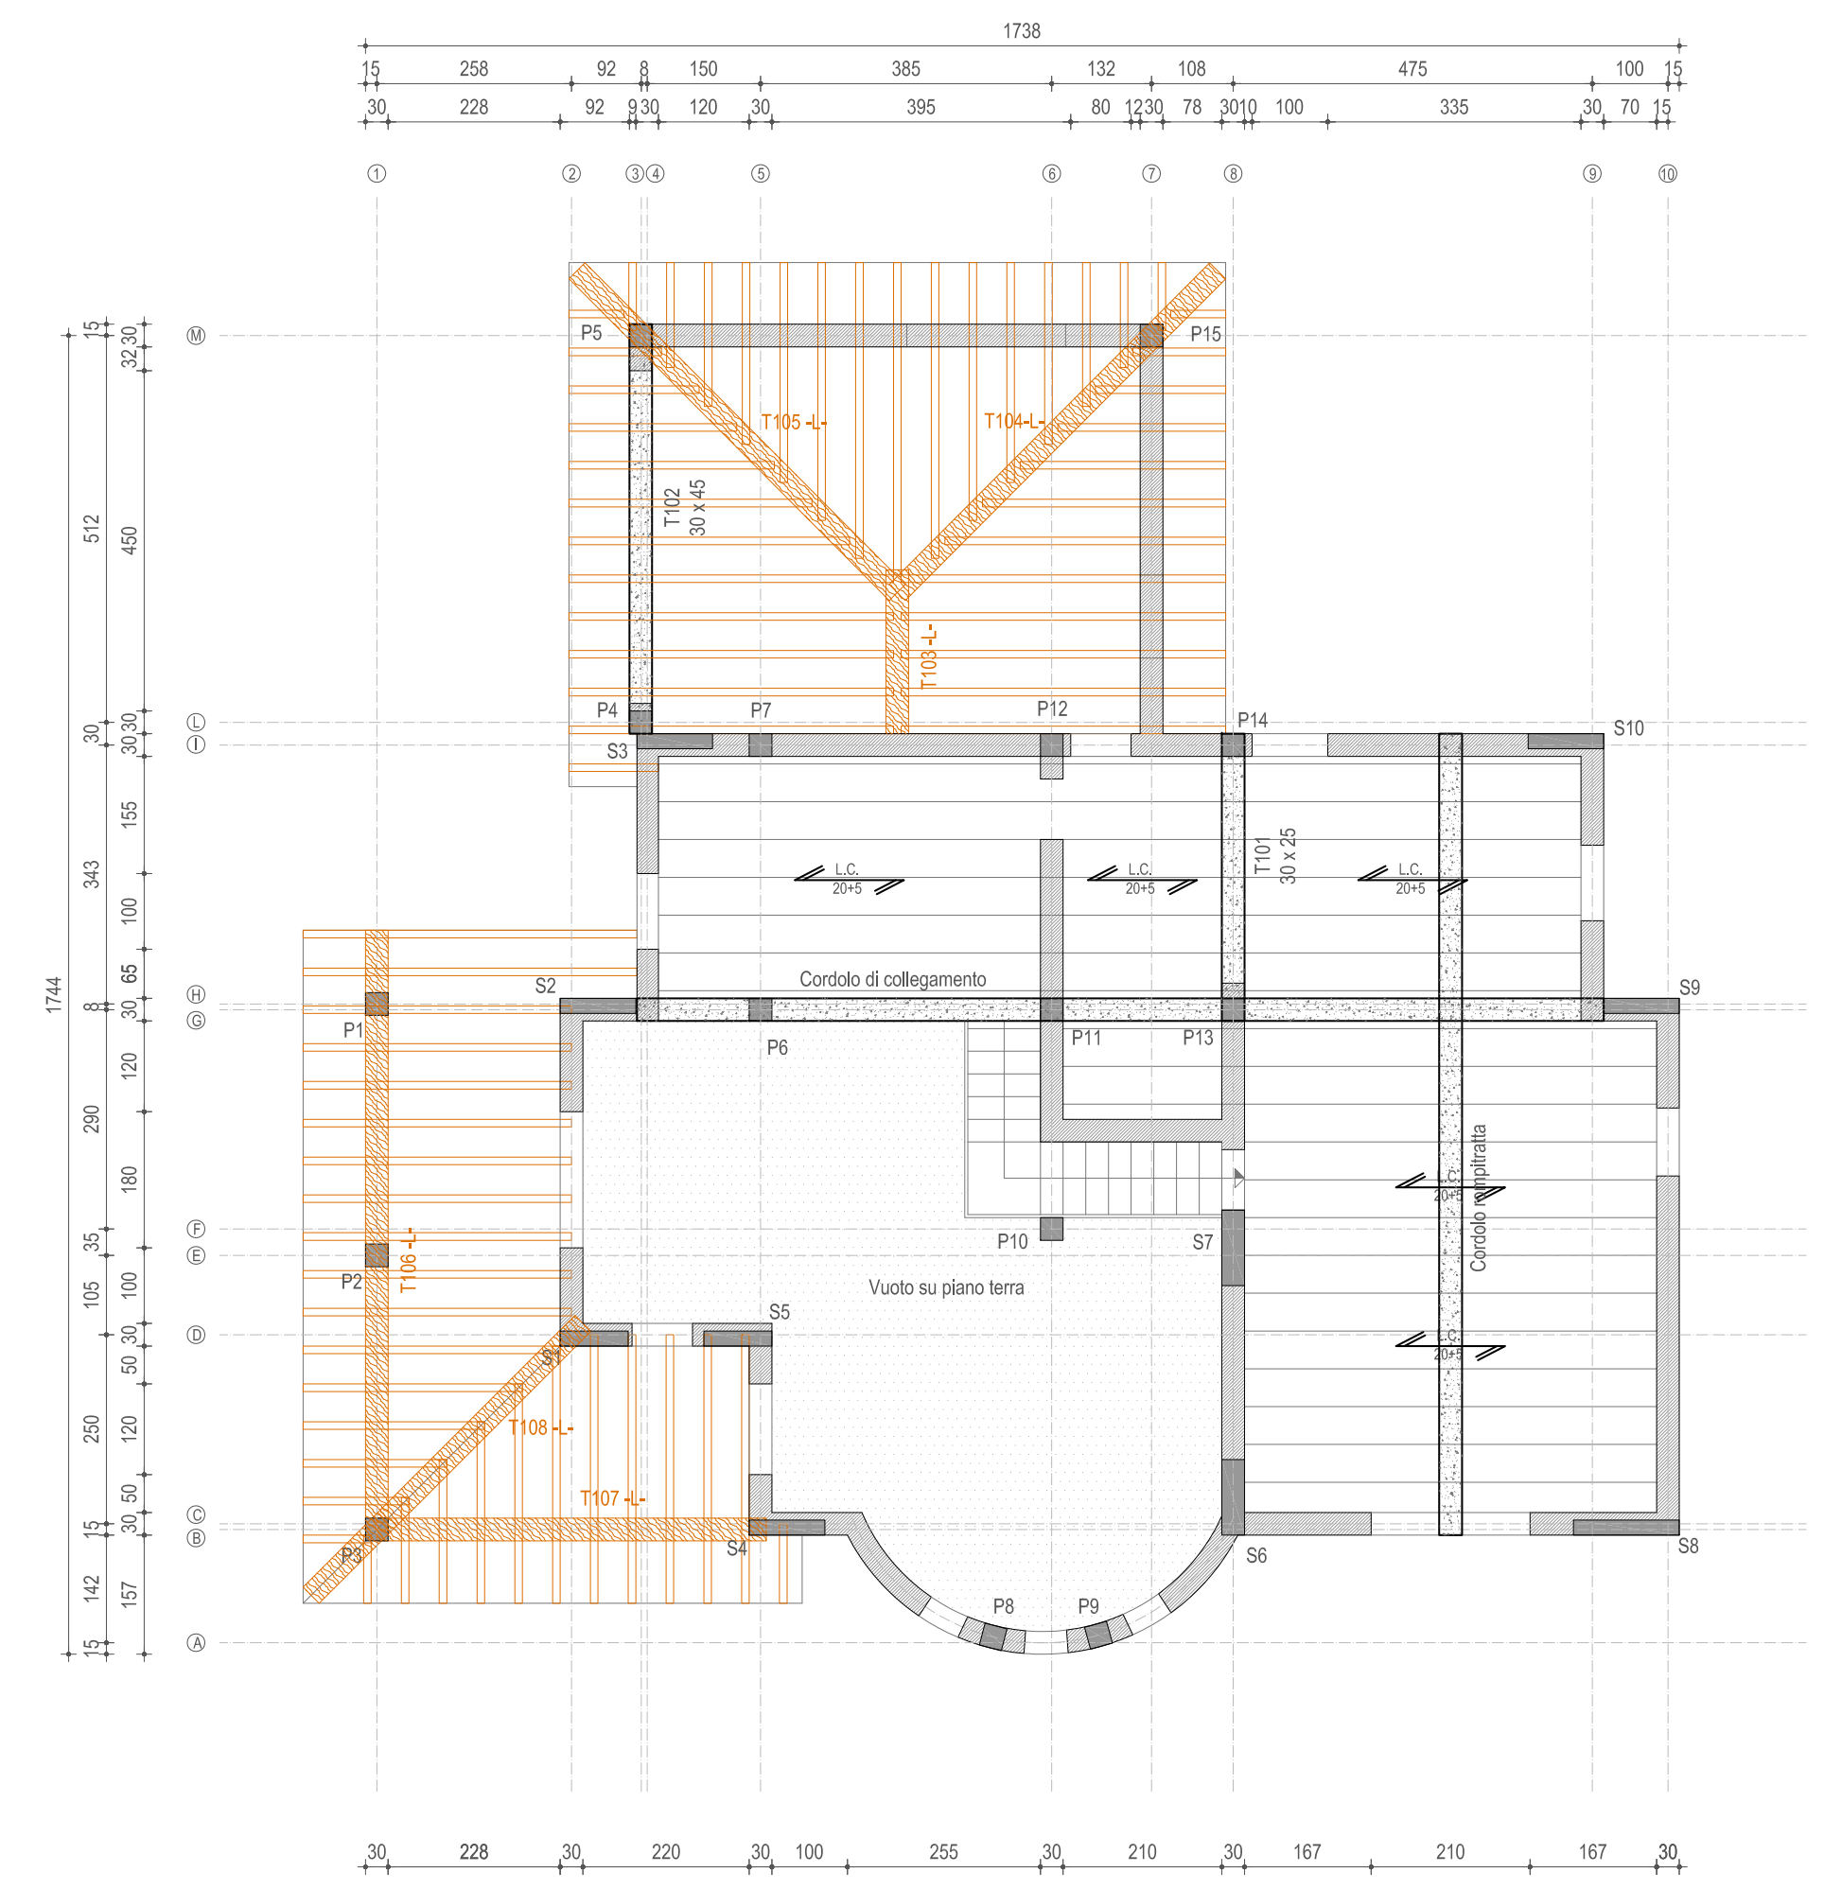

PARTICOLARE CORDOLO
-scala 1:20-

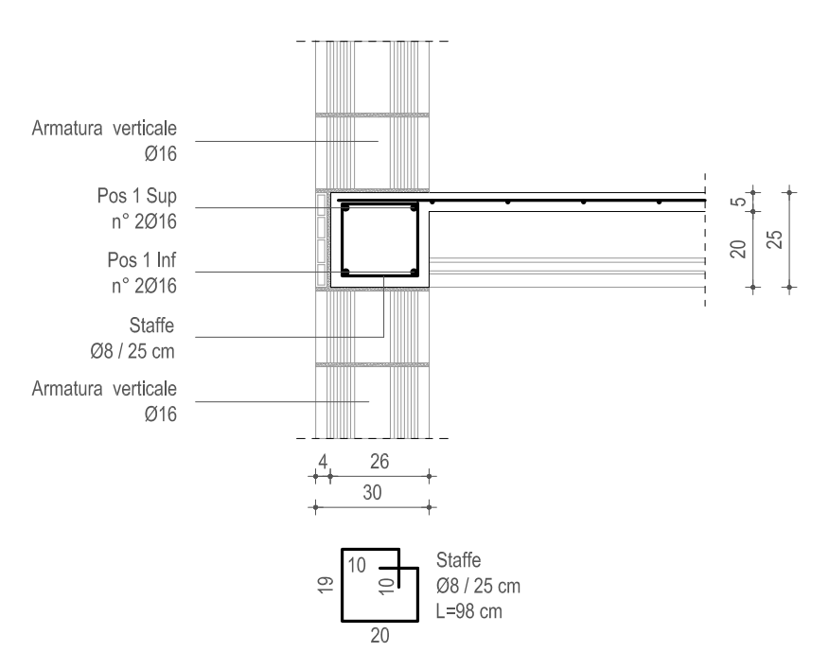

PARTICOLARE CORDOLO ROMPITRATTA
-scala 1:20-

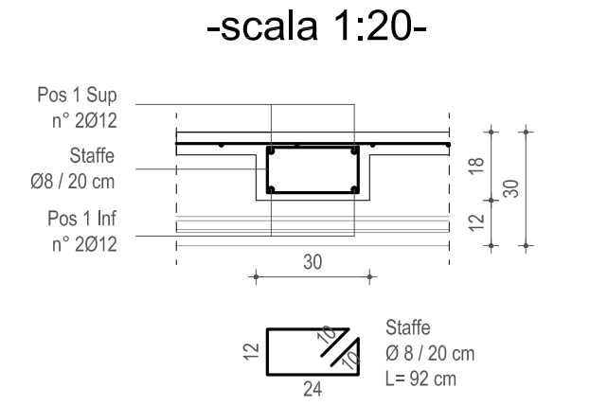

SETTO -S8-
-scala 1:25-

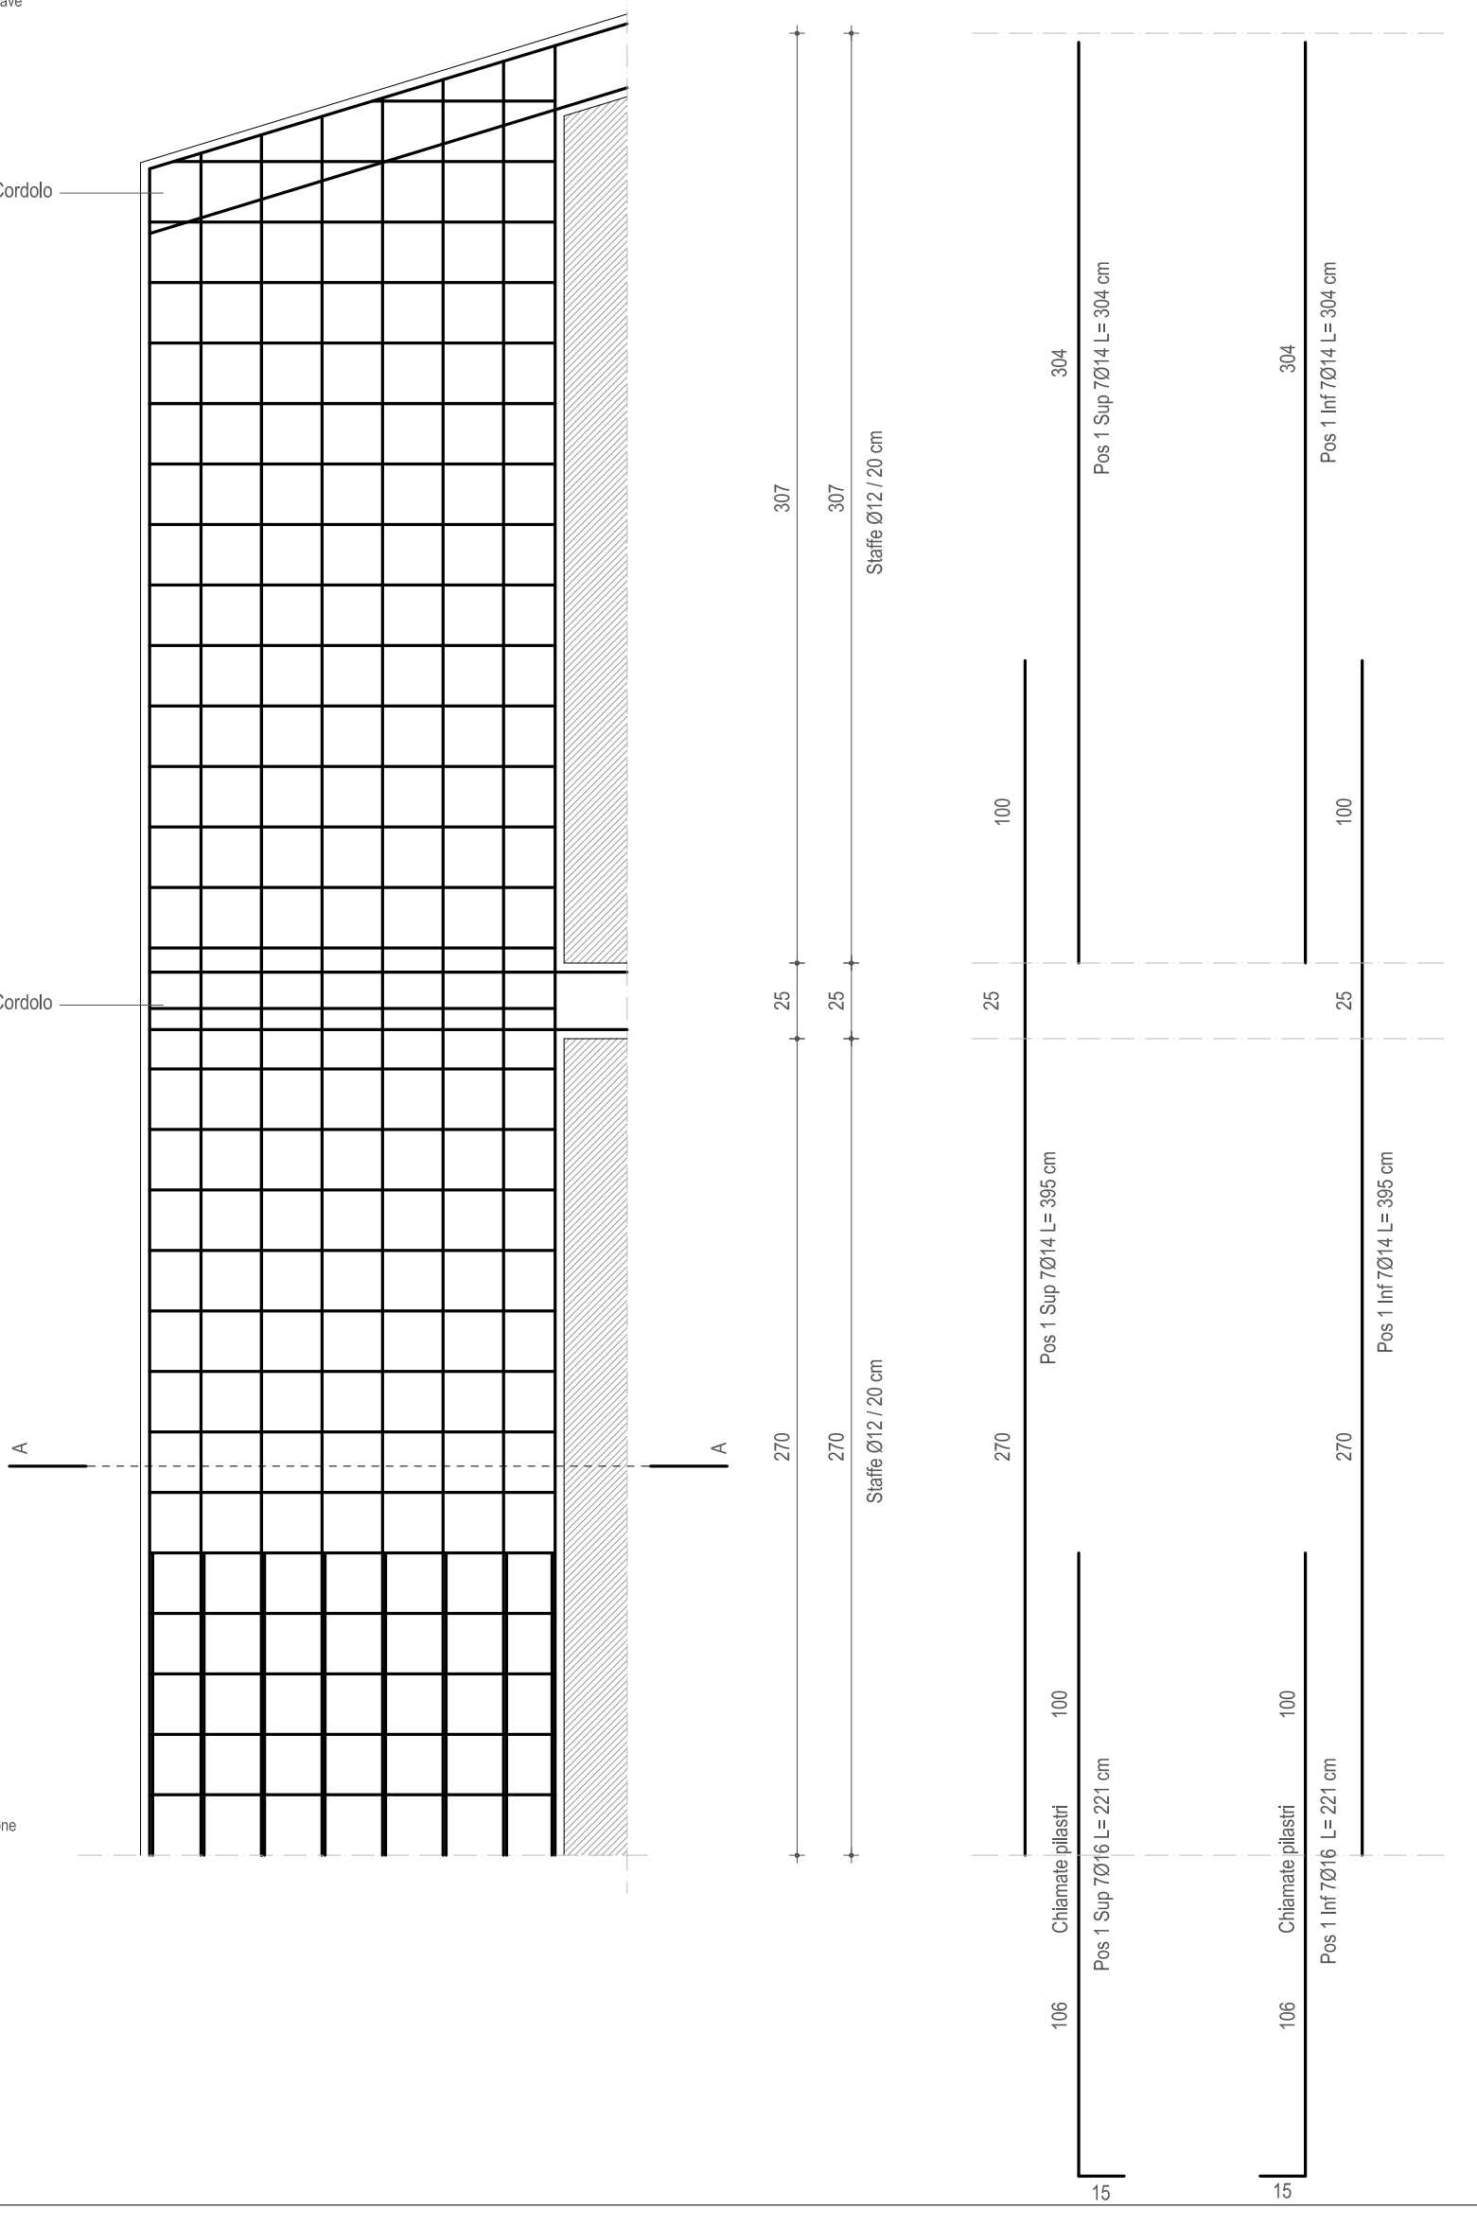

PILASTRO -S8-
-scala 1:20-
Sezione A-A

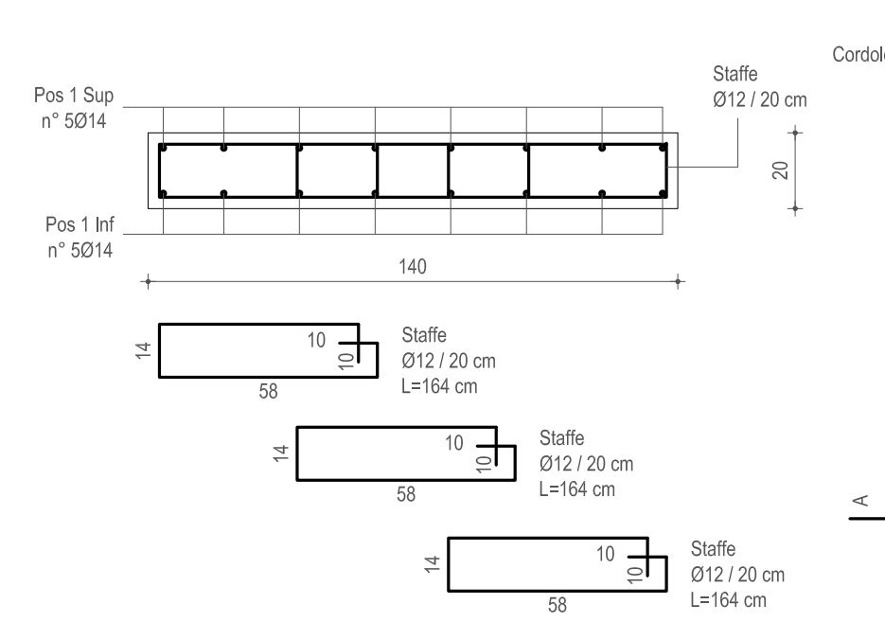

PILASTRO -P6-P7-
-scala 1:20-
Sezione B-B

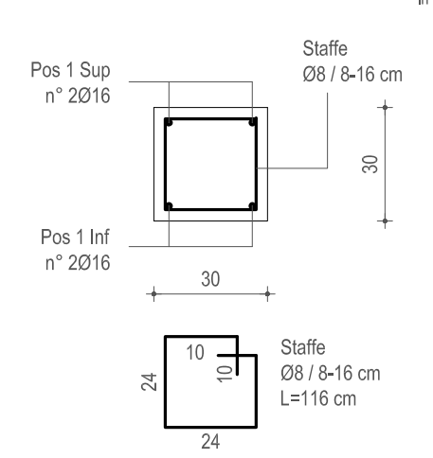

PILASTRO -P6-P7-
-scala 1:20-
Sezione A-A

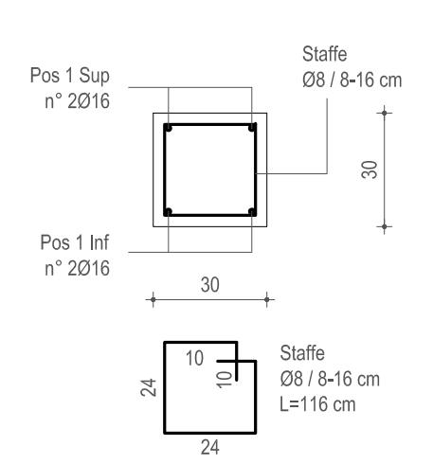

PILASTRO -P6-P7-
-scala 1:25-

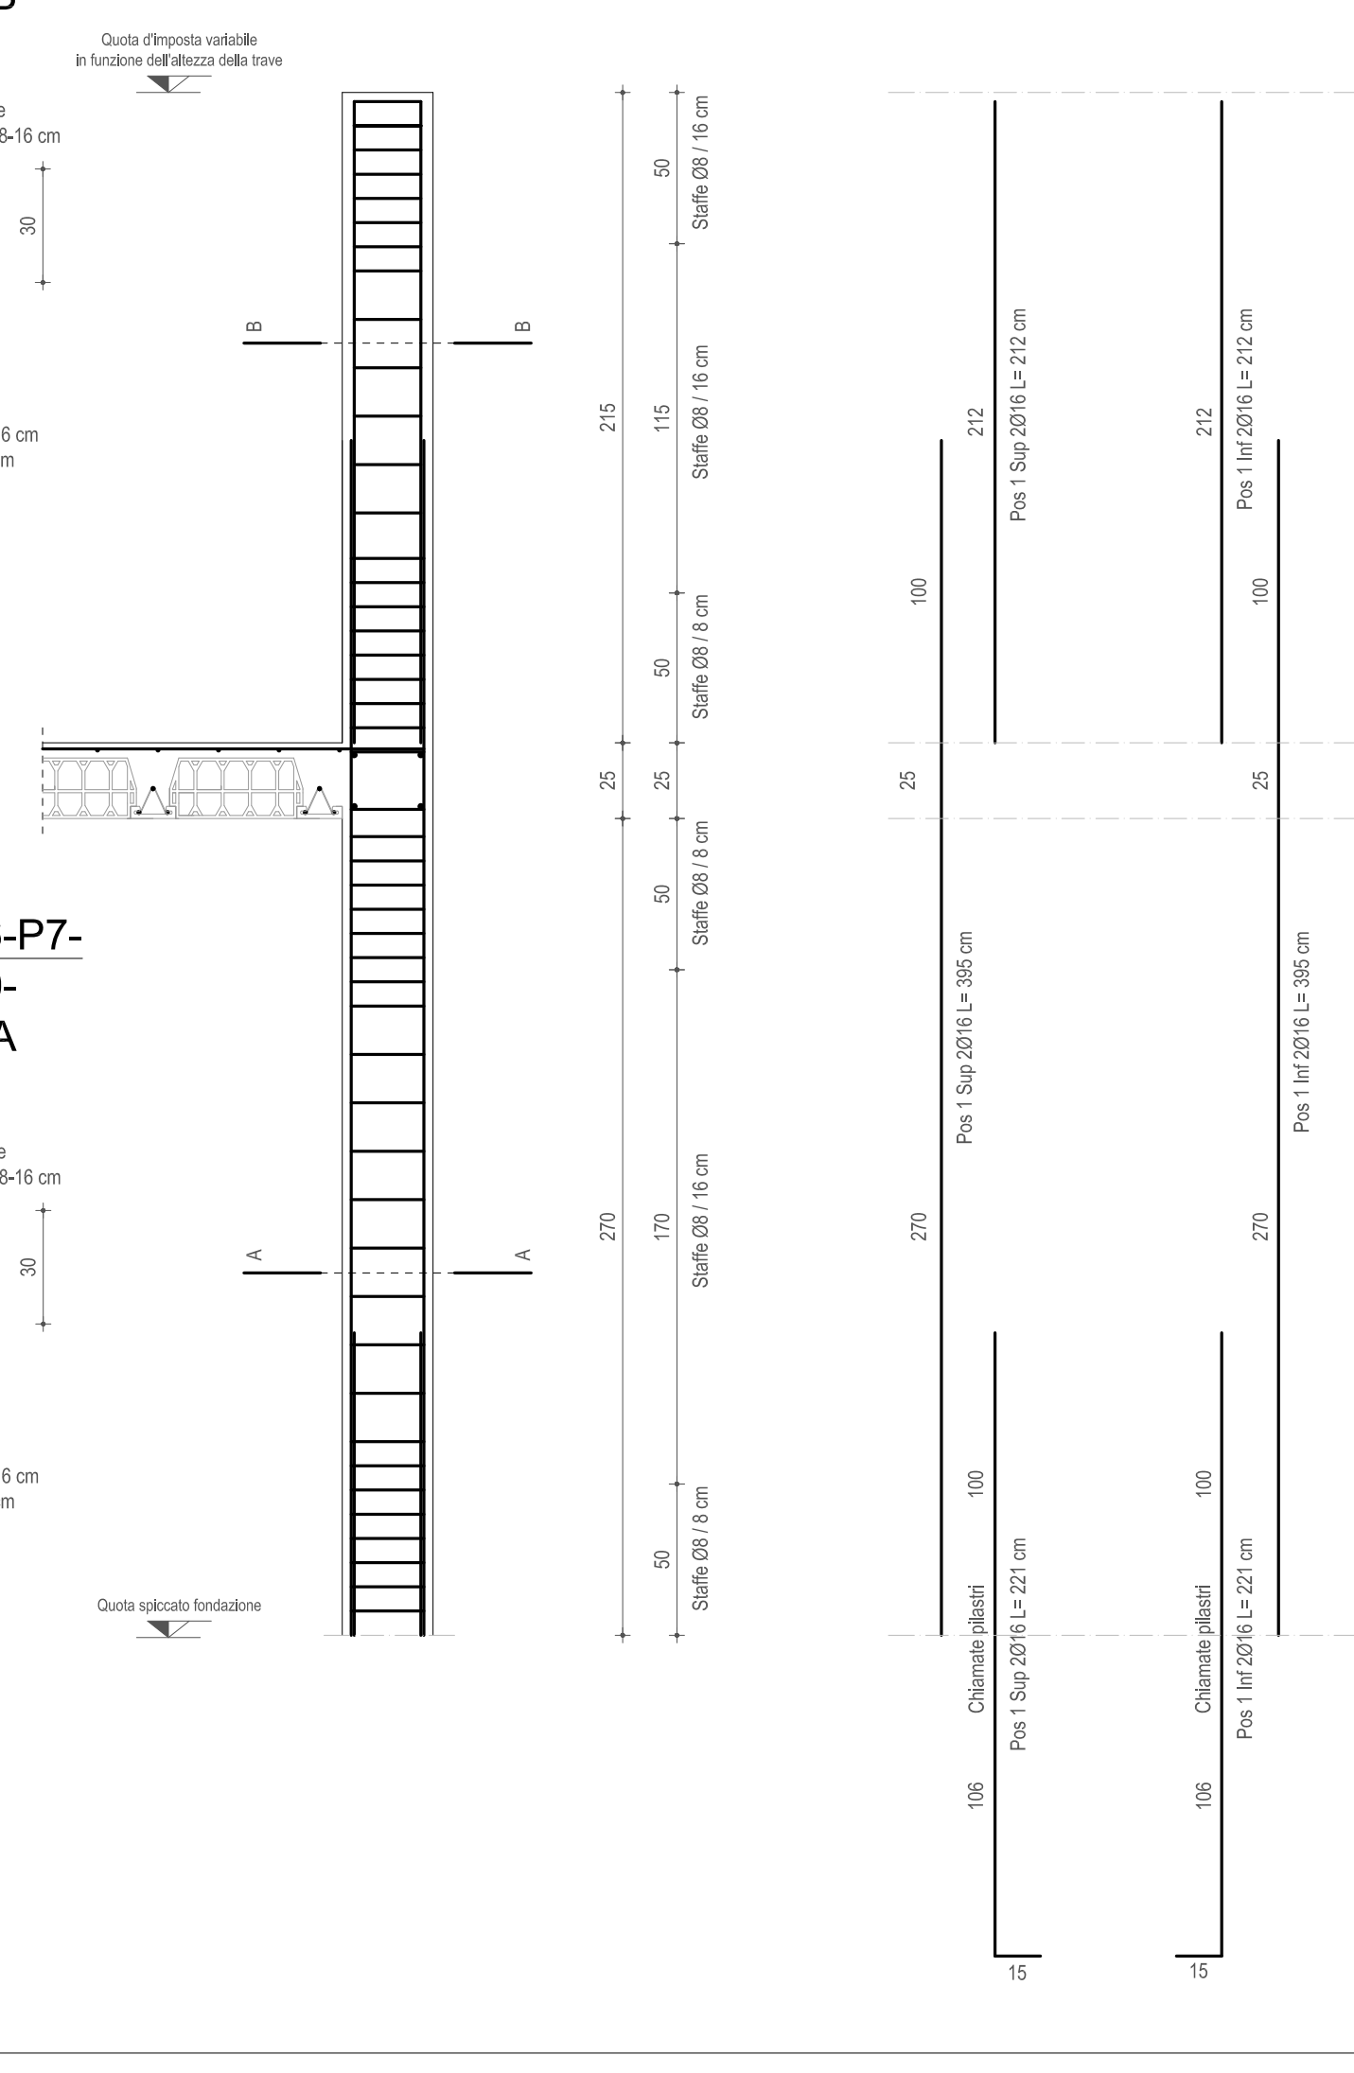

PILASTRO -P1-P2-P3-
-scala 1:20-
Sezione A-A

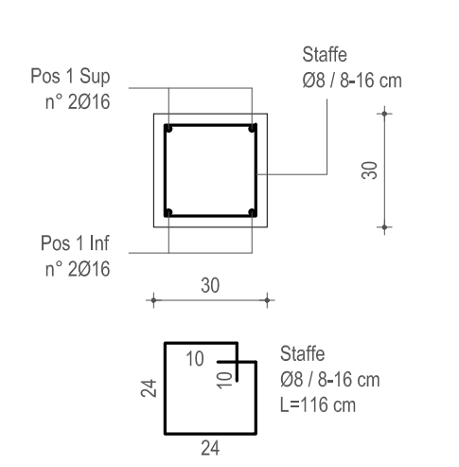

PILASTRO -P1-P2-P3-
-scala 1:25-

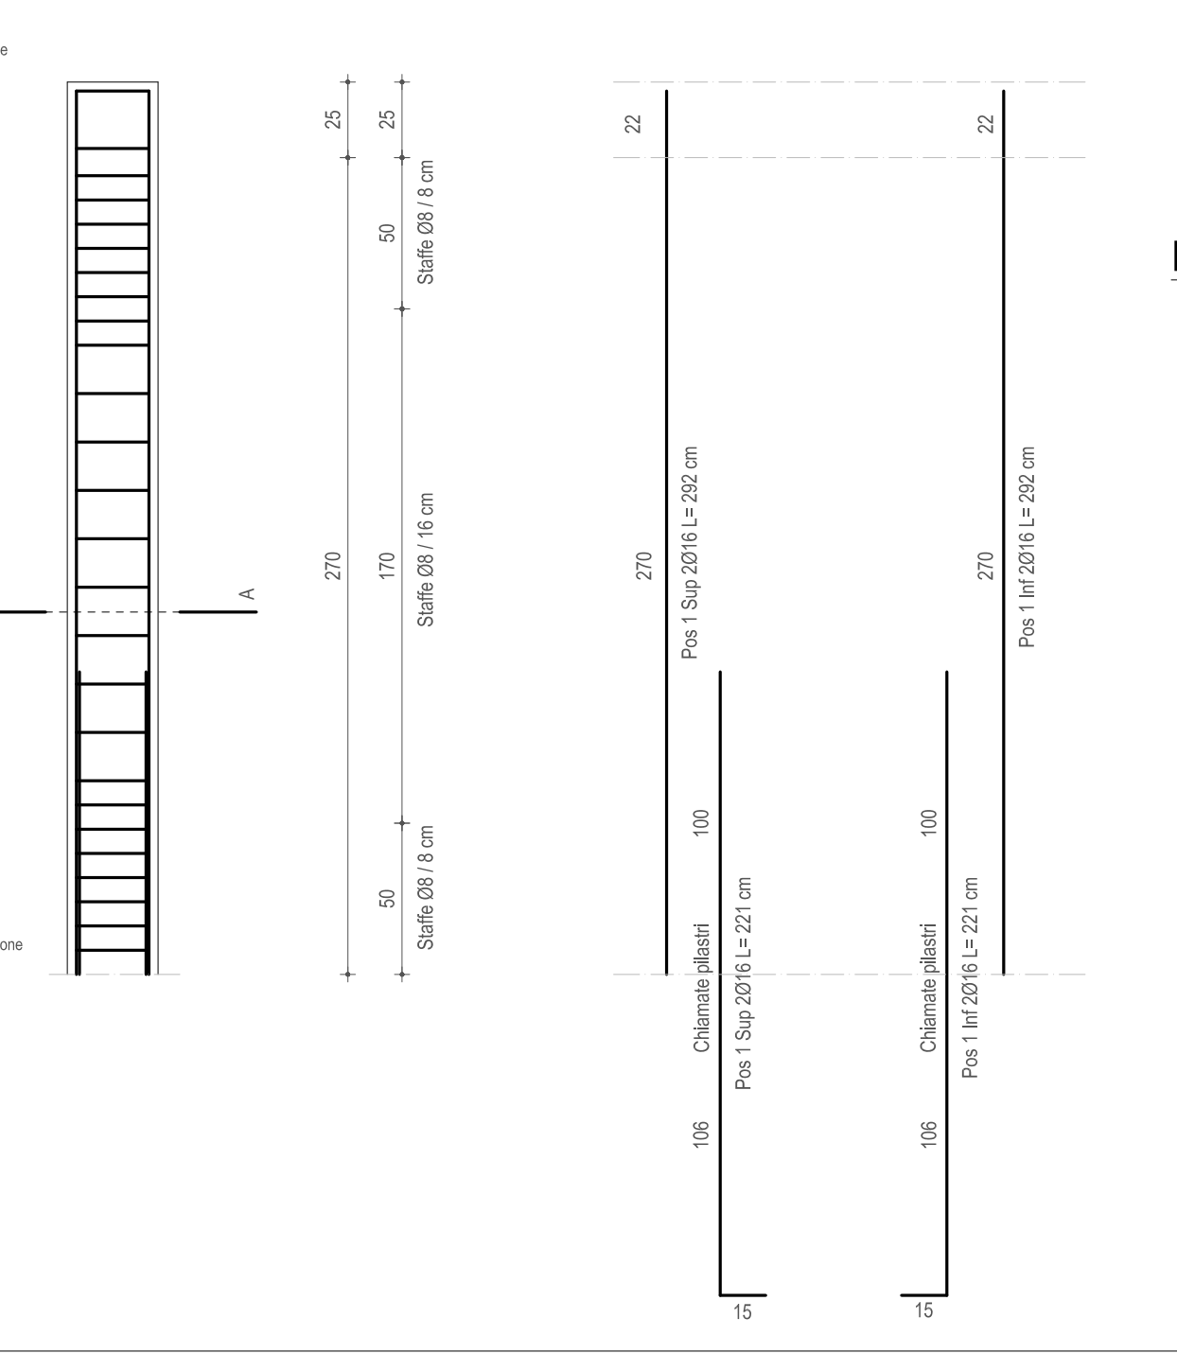

PILASTRO -P4-P5-P15-
-scala 1:20-
Sezione A-A

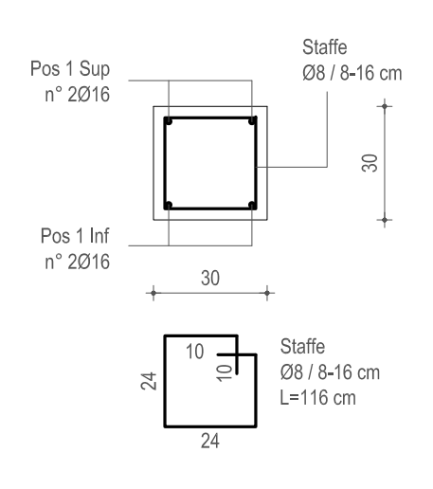

PILASTRO -P4-P5-P15-
-scala 1:25-

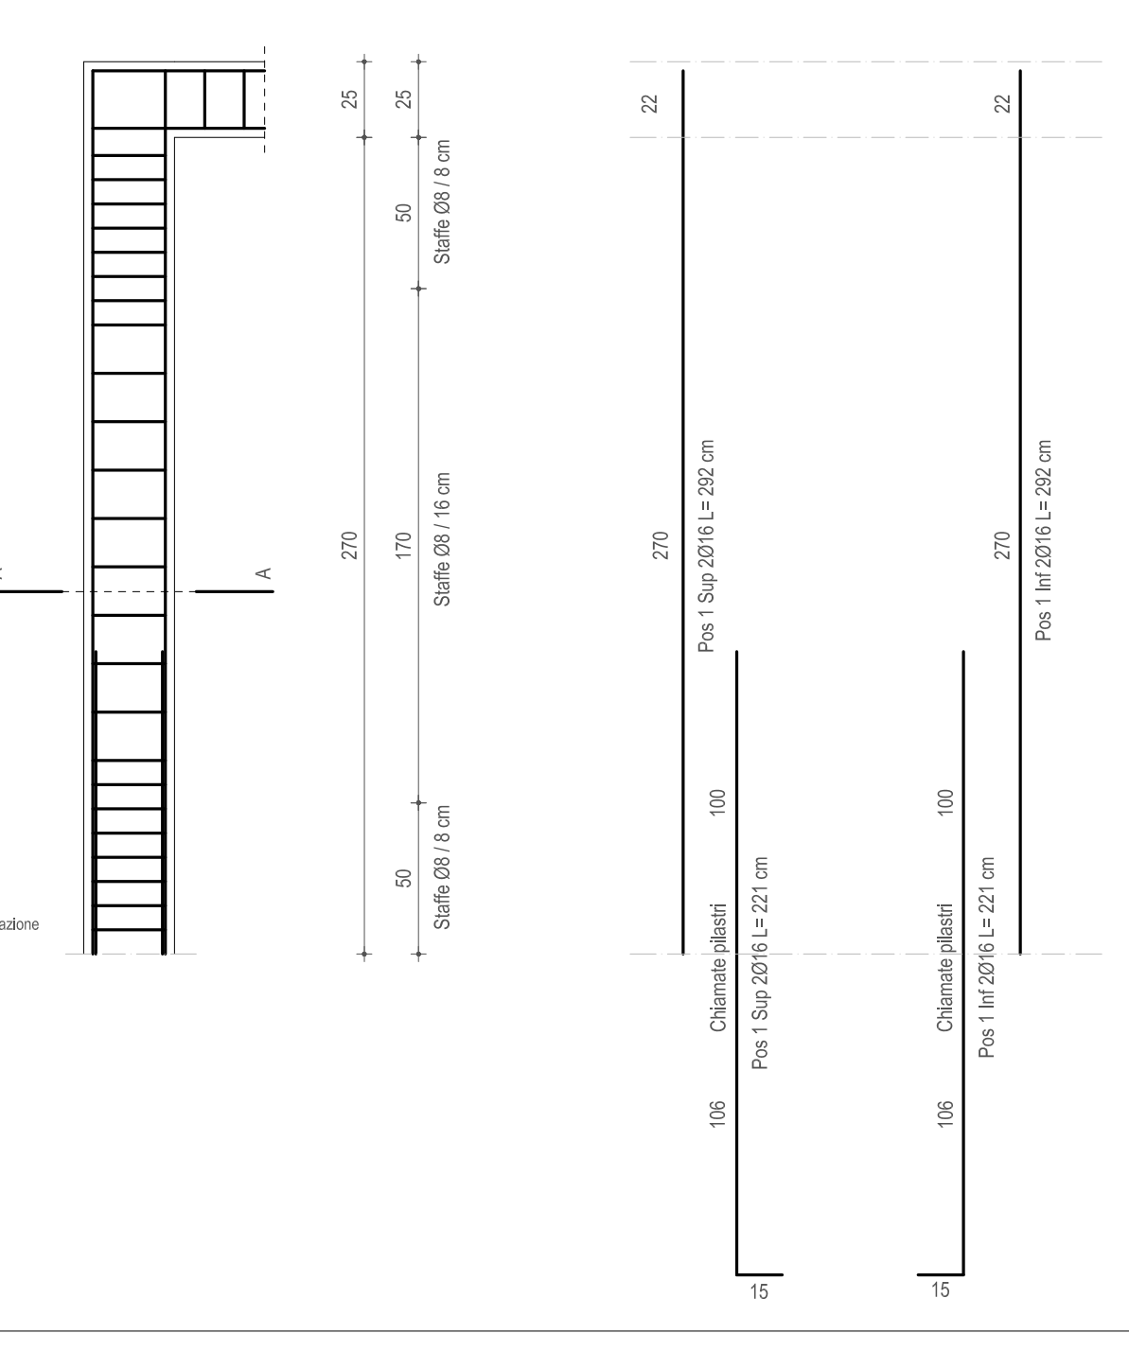

TRAVE -T102-
-scala 1:25-

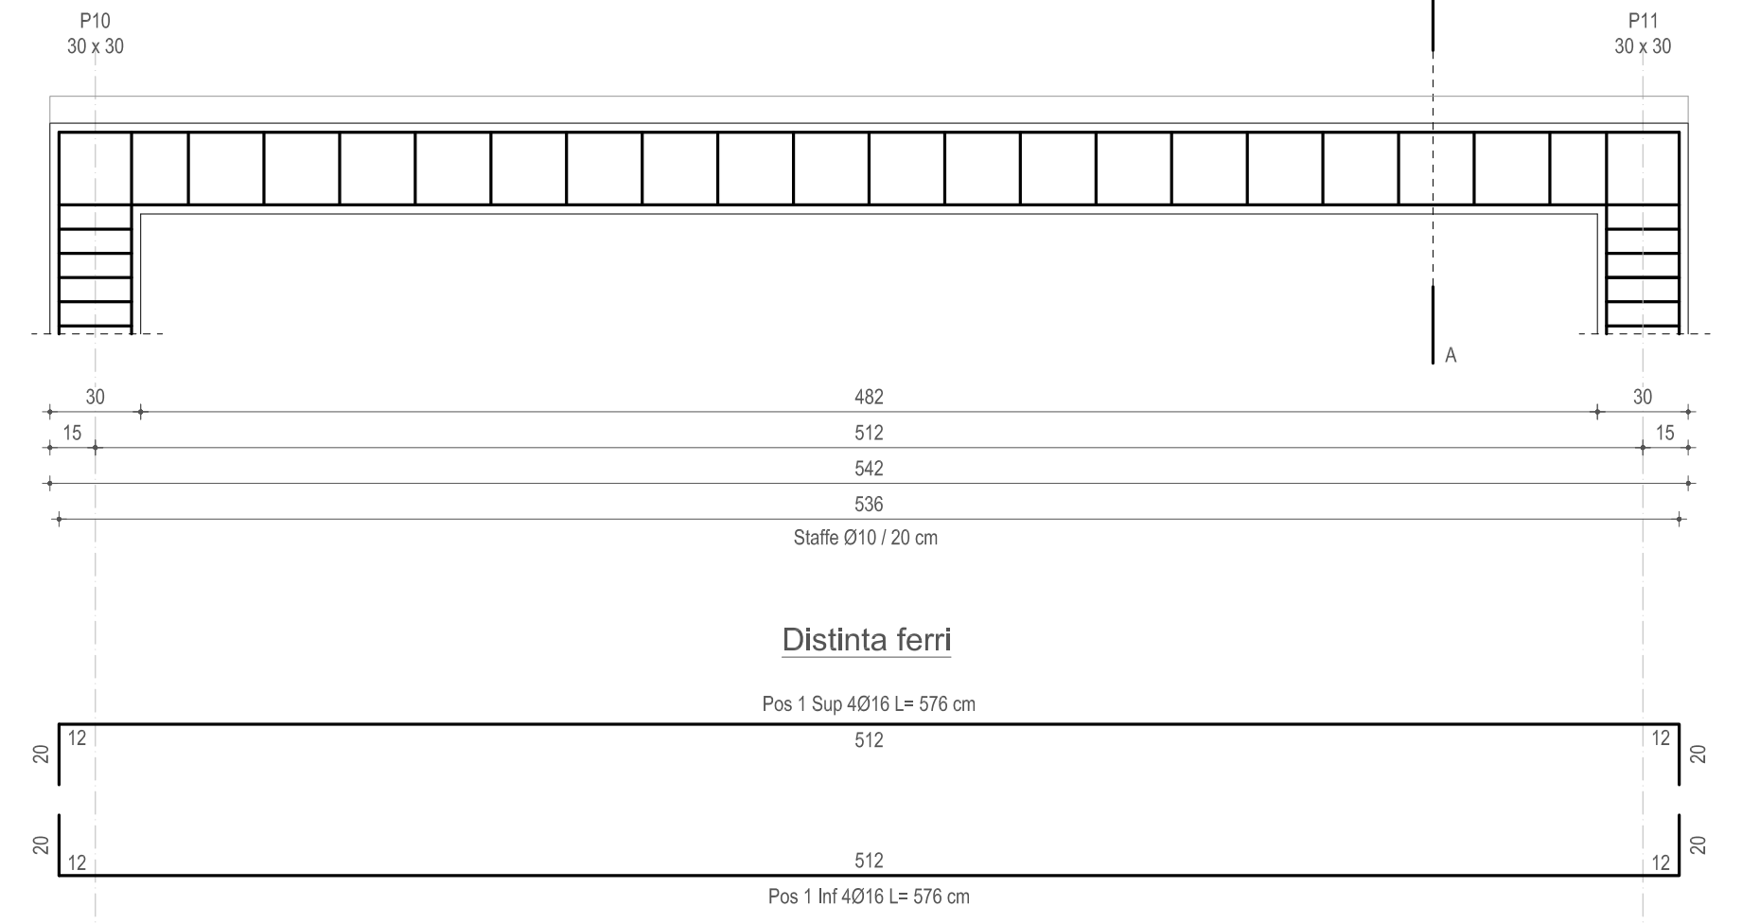

TRAVE -T102-
-scala 1:20-
Sezione A-A

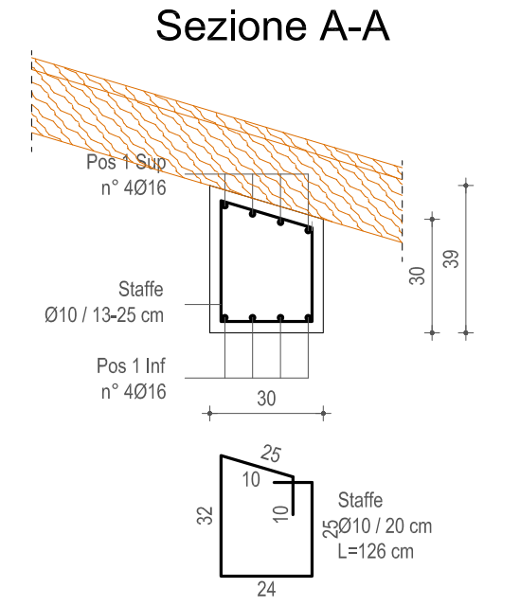

TRAVE -T101-
-scala 1:25-

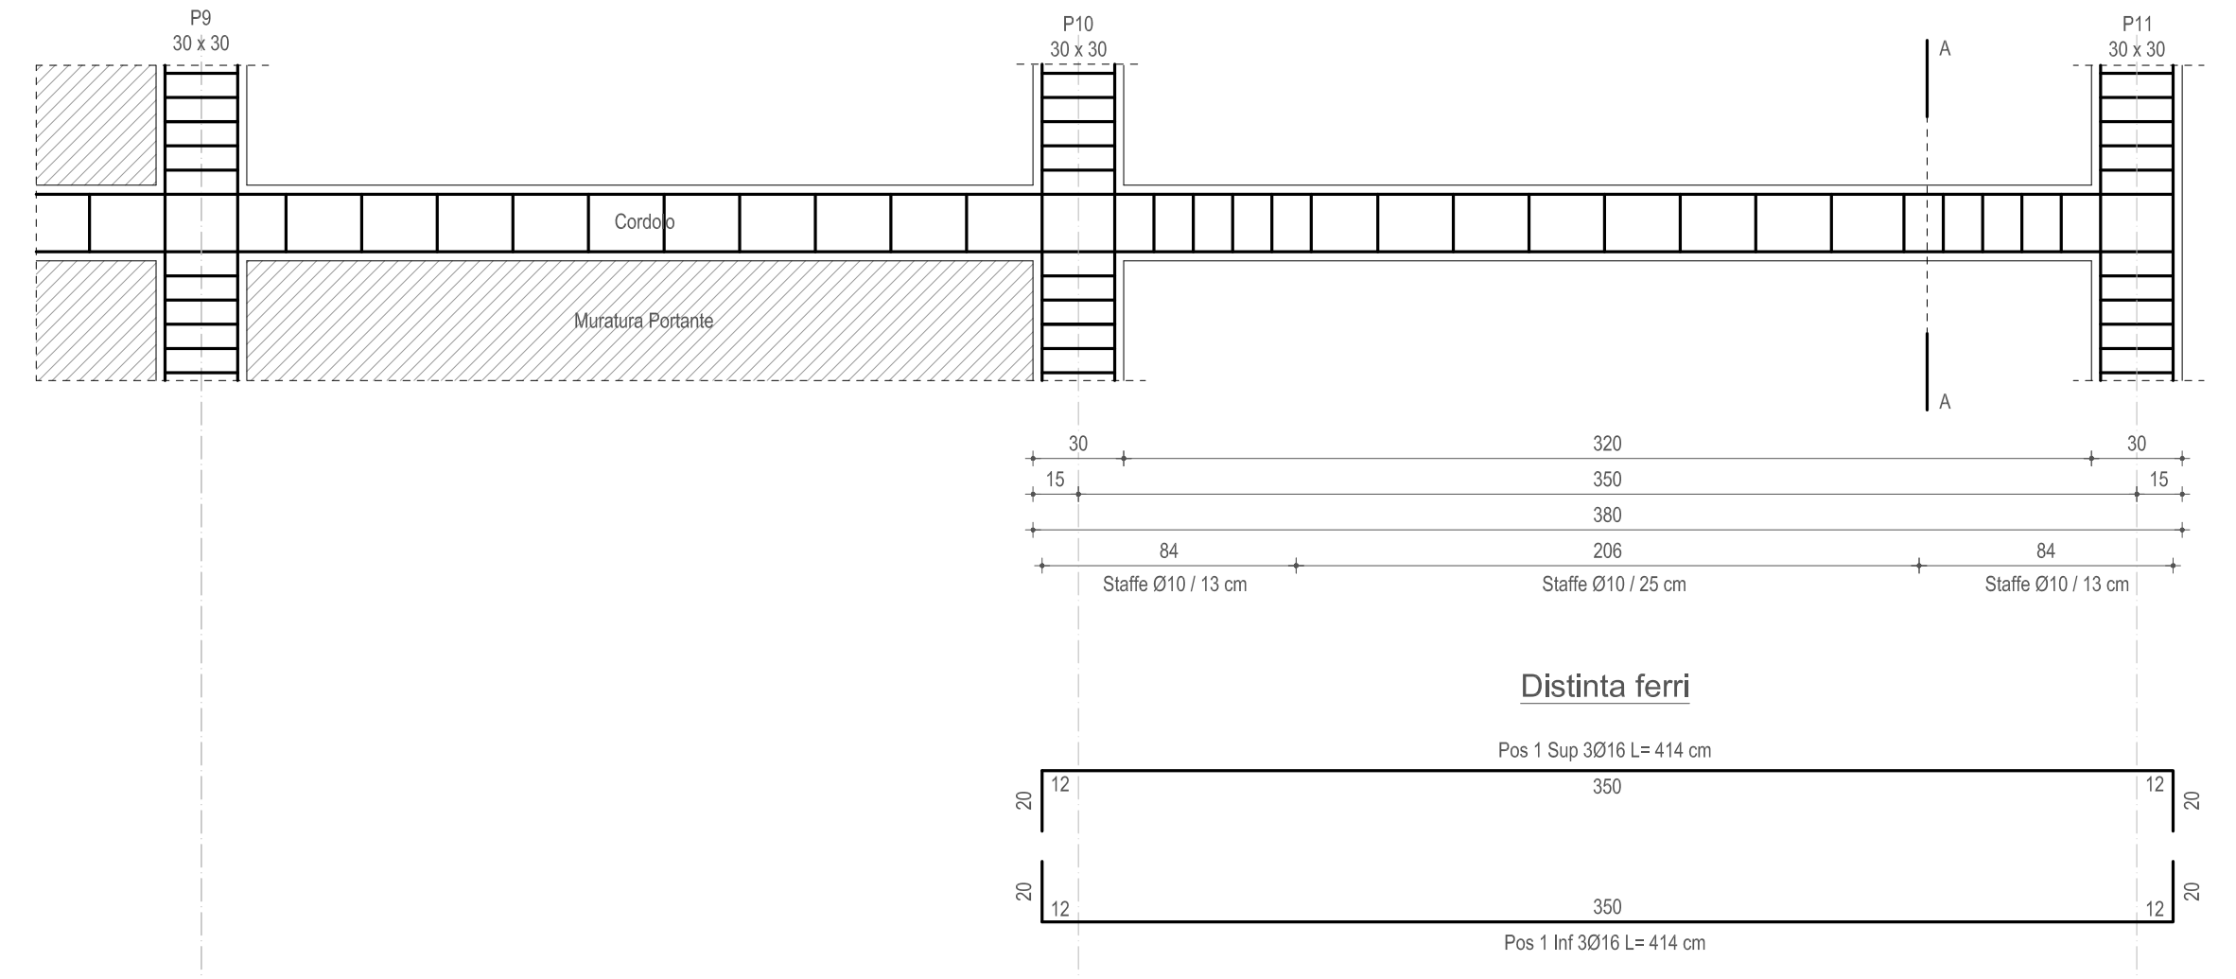

TRAVE -T101-
-scala 1:20-
Sezione A-A

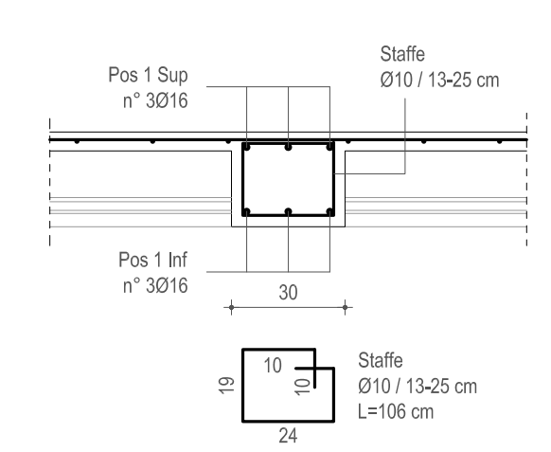

MATERIALI E PRESCRIZIONI

MATERIALI PRESCRITTI:

- Calcestruzzo per opere di: Fondazioni
  - Classe di resistenza : C25/30 (Rck 30)
  - Condizioni ambientali: Strutture completamente interrate in terreno permeabile
  - Classe di esposizione : XC2
  - Rapporto massimo acqua/cemento: 0,60
  - Classe di consistenza: S3 (Plastica)
  - Diametro massimo degli aggregati: 16 mm
- Calcestruzzo per opere di: Elevazione e Solai
  - Classe di resistenza : C25/30 (Rck 30)
  - Condizioni ambientali: Strutture interne di edifici non industriali con umidità bassa
  - Classe di esposizione : XC1
  - Rapporto massimo acqua/cemento: 0,60
  - Classe di consistenza: S3 (Plastica)
  - Diametro massimo degli aggregati: 16 mm
- Acciaio per tutte le strutture: B450 C controllato

PRESCRIZIONE

Tutte le misure dovranno essere controllate in cantiere confrontandole con quelle del progetto architettonico e confermate dalla direzione lavori

---

COMUNE DI RODIGO PROVINCIA DI MANTOVA

Oggetto

PROGETTO PER LA REALIZZAZIONE DI CASA UNIFAMIGLIARE.

[redacted]

Oggetto tavola
- Disegni esecutivi:
  Primo Impalcato
  Copertura
  Pilastri
  Setti

Denuncia C.A.

Tav. n° 2	Variante
Data	Scale 1:100, 1:25, 1:20

[redacted]