


FONDAZIONE CONTINUA -TIPO 1- FC-T1- -scala 1:20-

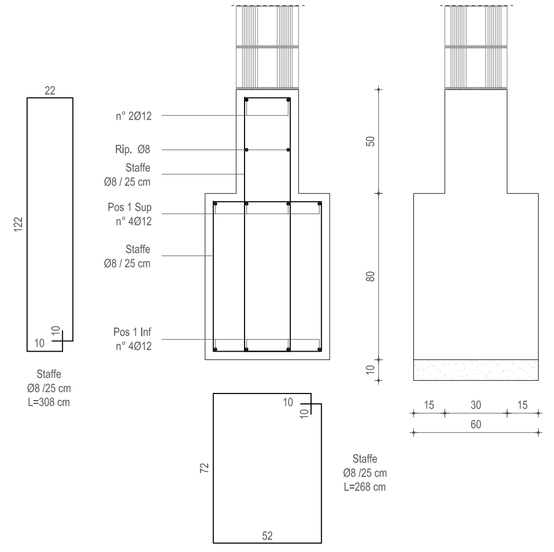


PARTICOLARE CHIAMATE PILASTRI -scala 1:20-

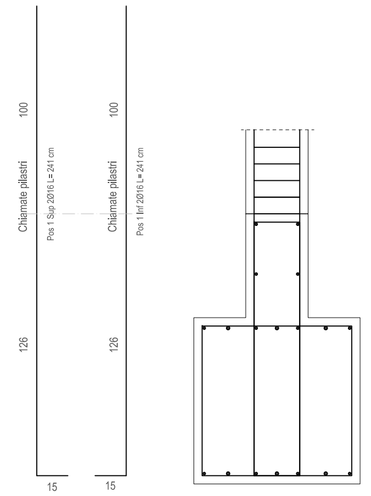


PILASTRO -scala 1:20- Sezione di base

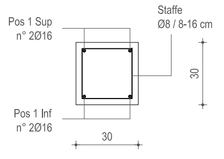


PARTICOLARE CHIAMATE SETTI s=20 cm -scala 1:20-

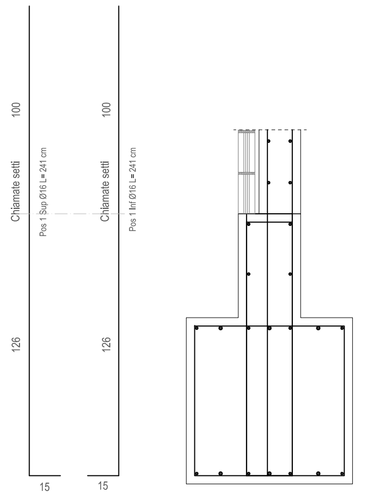


SETTO s =20 cm -scala 1:20- Sezione di base

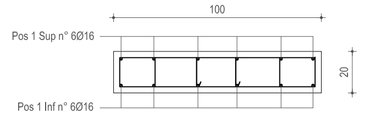


PARTICOLARE CHIAMATE SETTI s=30 cm -scala 1:20-

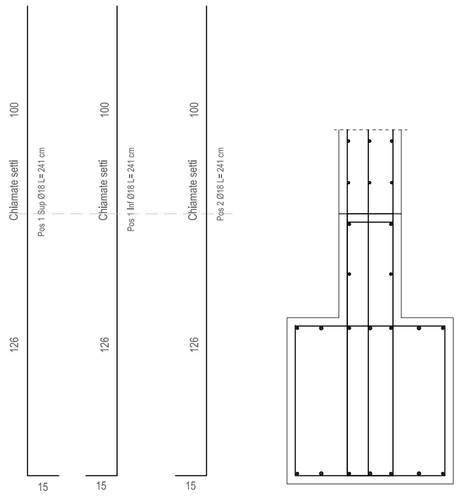


SETTO s =30 cm -scala 1:20- Sezione di base

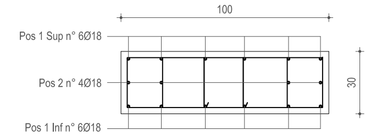


PIANTA FONDAZIONI -scala 1:100-

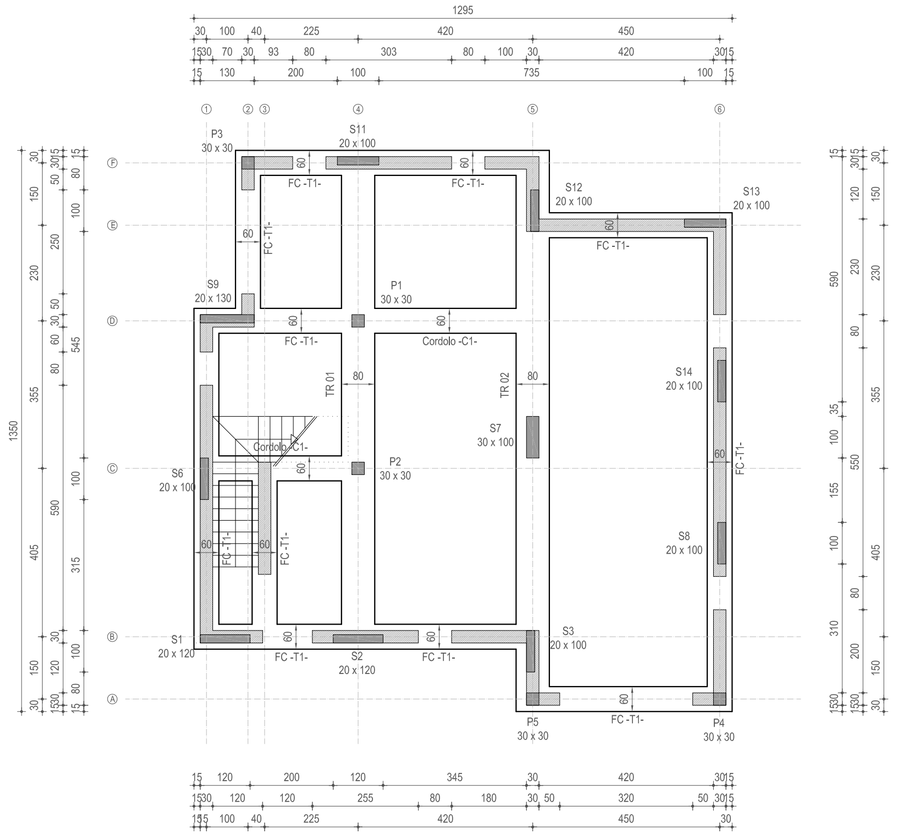


TRAVE ROVESCIA -TR 1- -scala 1:20-

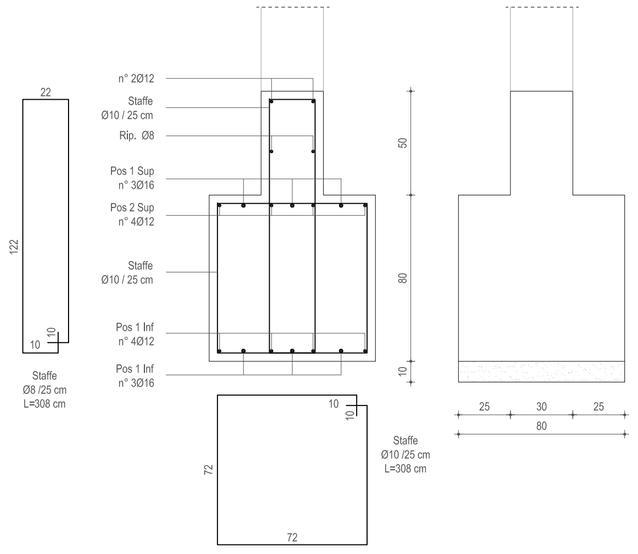


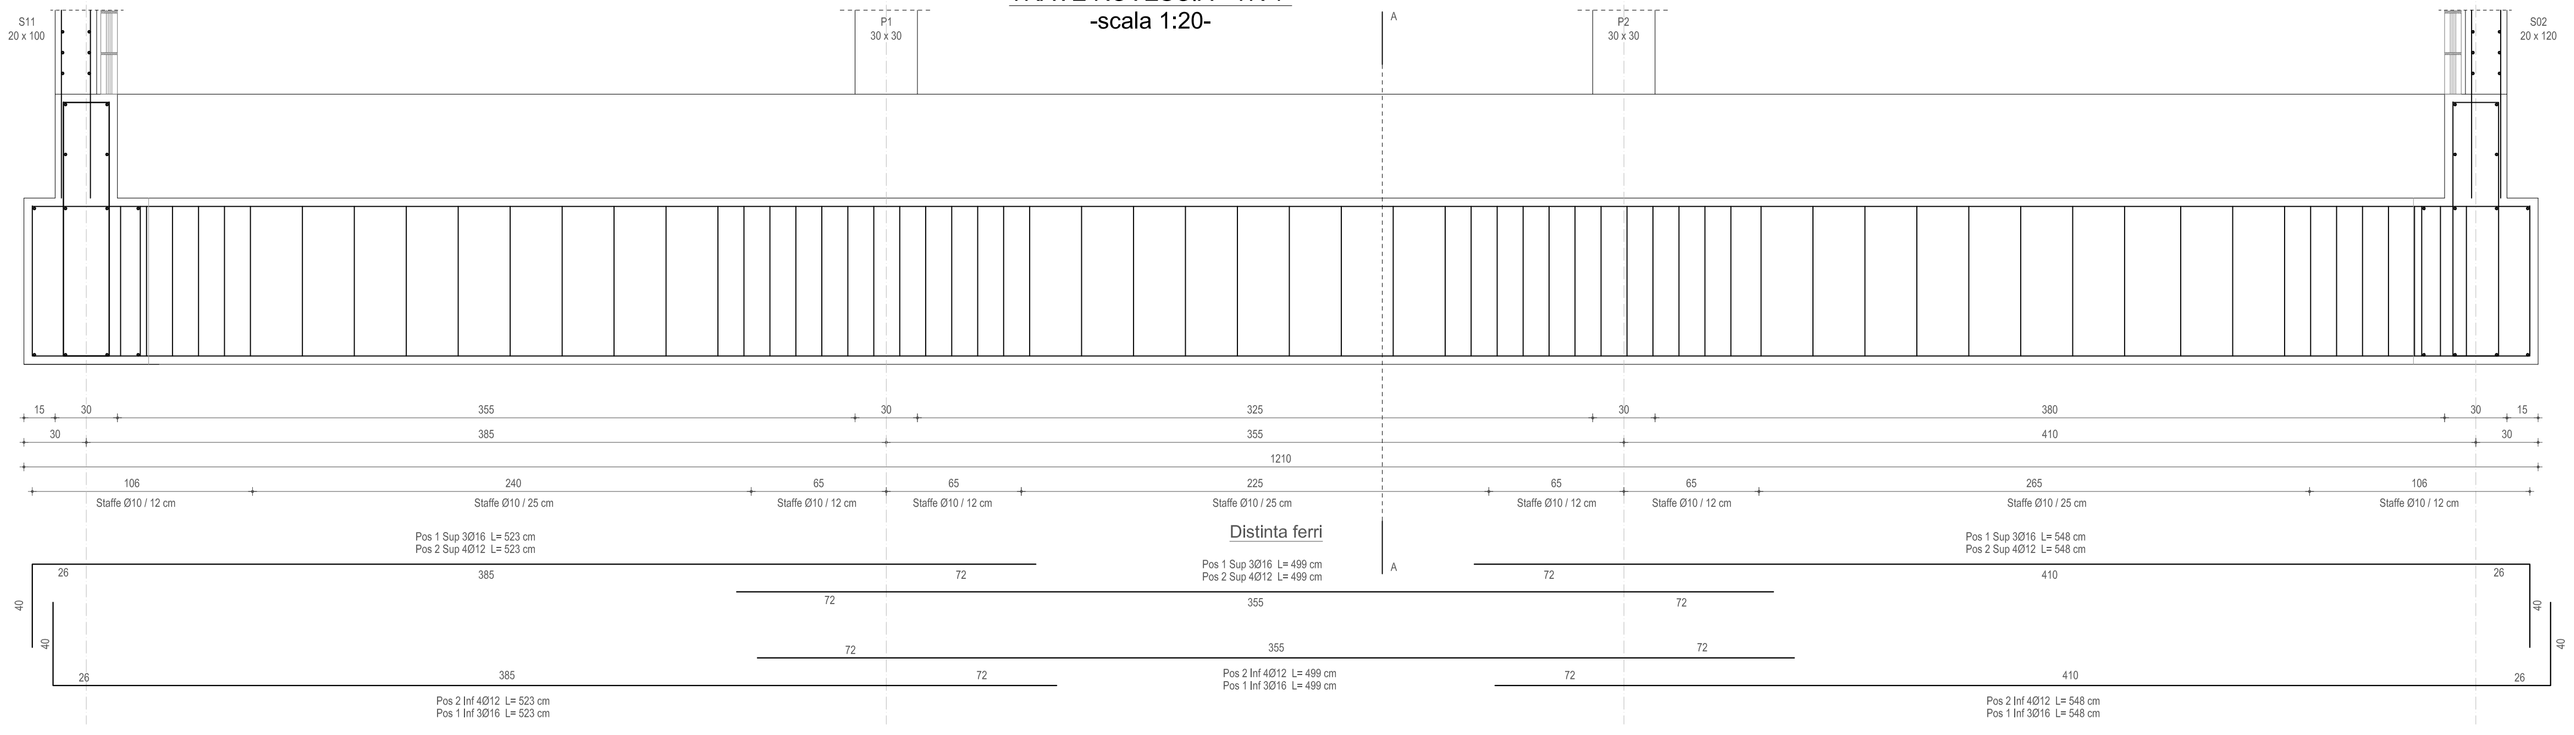

TRAVE ROVESCIA -TR 1- -scala 1:20- Sezione A-A

TRAVE ROVESCIA -TR 2- -scala 1:20-

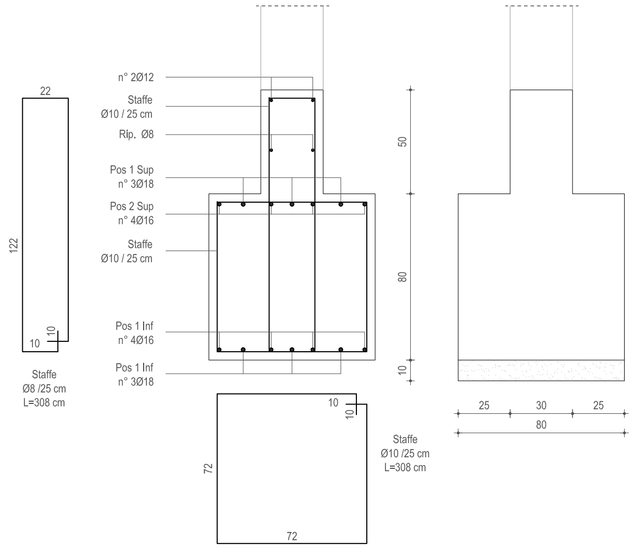

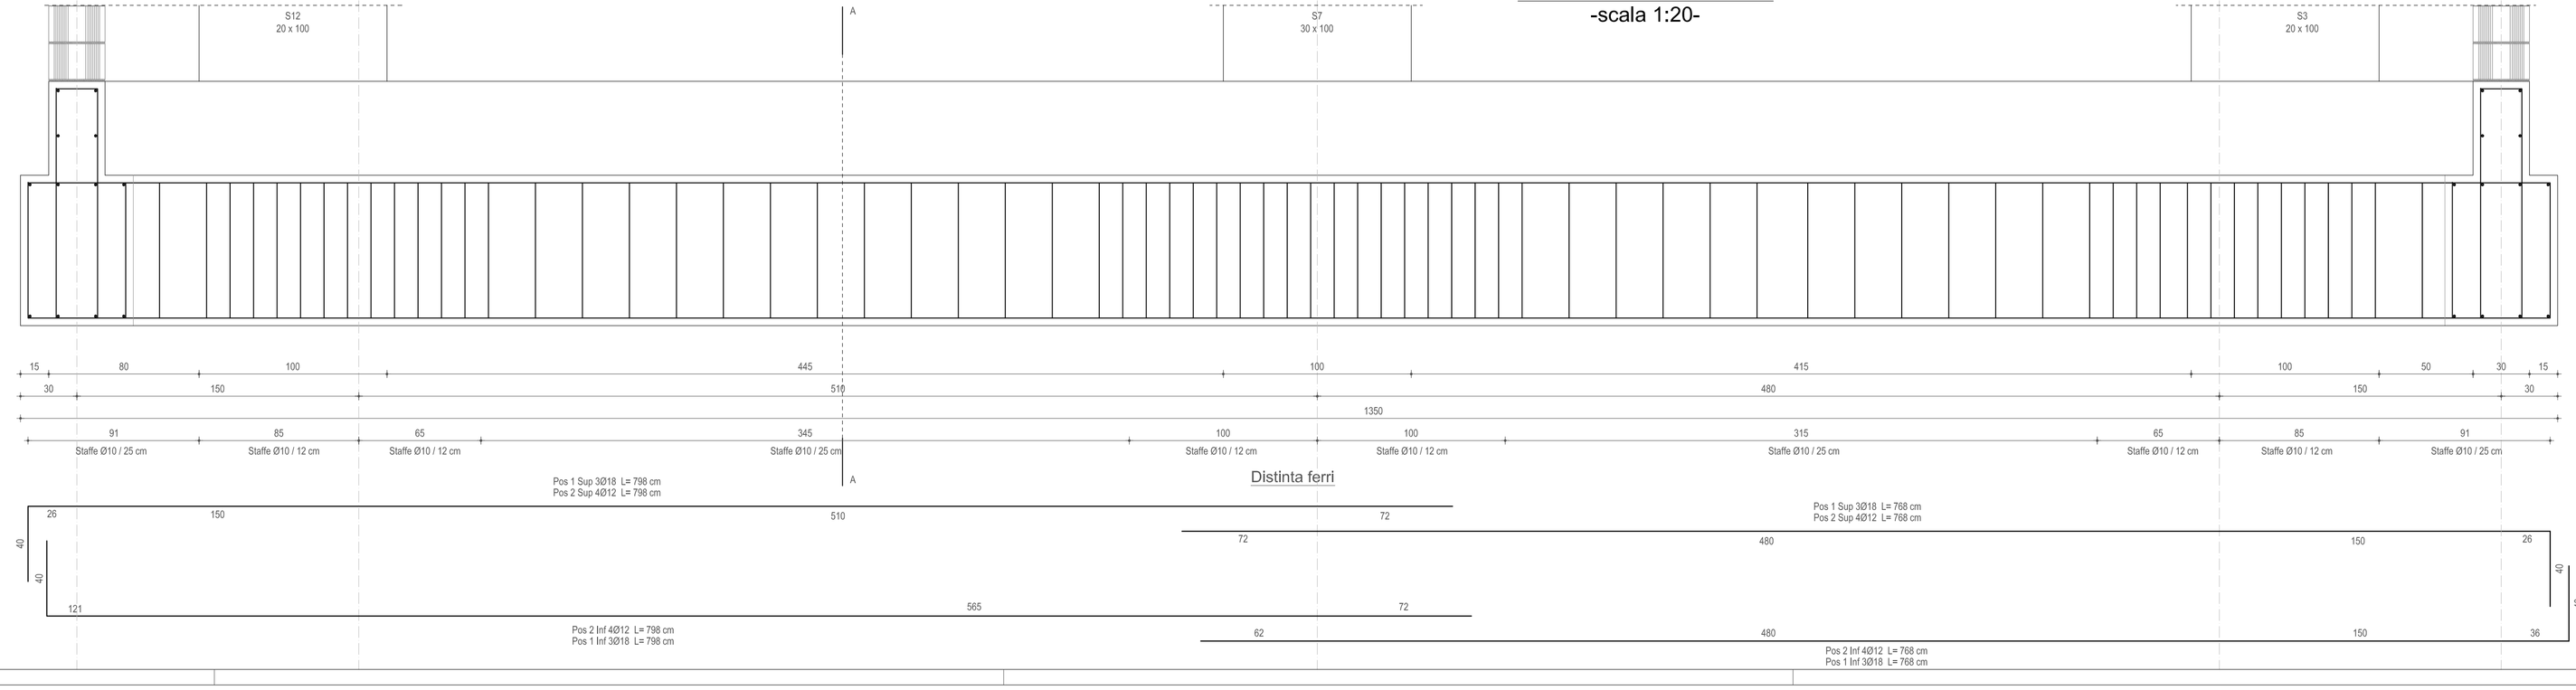

TRAVE ROVESCIA -TR 2- -scala 1:20- Sezione A-A

MATERIALI E PRESCRIZIONI

MATERIALI PRESCRITTI:

- Calcestruzzo per opere di: Fondazioni
  - Classe di resistenza : C25/30 (Rck 30)
  - Condizioni ambientali: Strutture completamente interrate in terreno permeabile
  - Classe di esposizione : XC2
  - Rapporto massimo acqua/cemento: 0,60
  - Classe di consistenza: S3 (Plastica)
  - Diametro massimo degli aggregati: 16 mm
- Calcestruzzo per opere di: Elevazione e Solai misti laterizio-c.a.
  - Classe di resistenza : C25/30 (Rck 30)
  - Condizioni ambientali: Strutture interne di edifici non industriali con umidità bassa
  - Classe di esposizione : XC1
  - Rapporto massimo acqua/cemento: 0,60
  - Classe di consistenza: S3 (Plastica)
  - Diametro massimo degli aggregati: 16 mm
- Calcestruzzo per opere di: Solette piene in C.A.
  - Classe di resistenza : C28/35 (Rck 35)
  - Condizioni ambientali: Strutture interne di edifici non industriali con umidità bassa
  - Classe di esposizione : XC1
  - Rapporto massimo acqua/cemento: 0,60
  - Classe di consistenza: S3 (Plastica)
  - Diametro massimo degli aggregati: 16 mm
- Acciaio per tutte le strutture: B450 C controllato

PRESCRIZIONE

Tutte le misure dovranno essere controllate in cantiere confrontandole con quelle del progetto architettonico e confermate dalla direzione lavori

COMUNE DI RODIGO PROVINCIA DI MANTOVA

Oggetto

[redacted]

Fondazioni

Tav. n° 1

Variante

Data

Scale 1:100, 1:20

[redacted]