TRAVE SCALA
Rampa n°1
-scala 1:20-

TRAVE SCALA
Rampa n°1
-scala 1:20-
Sezione B-B

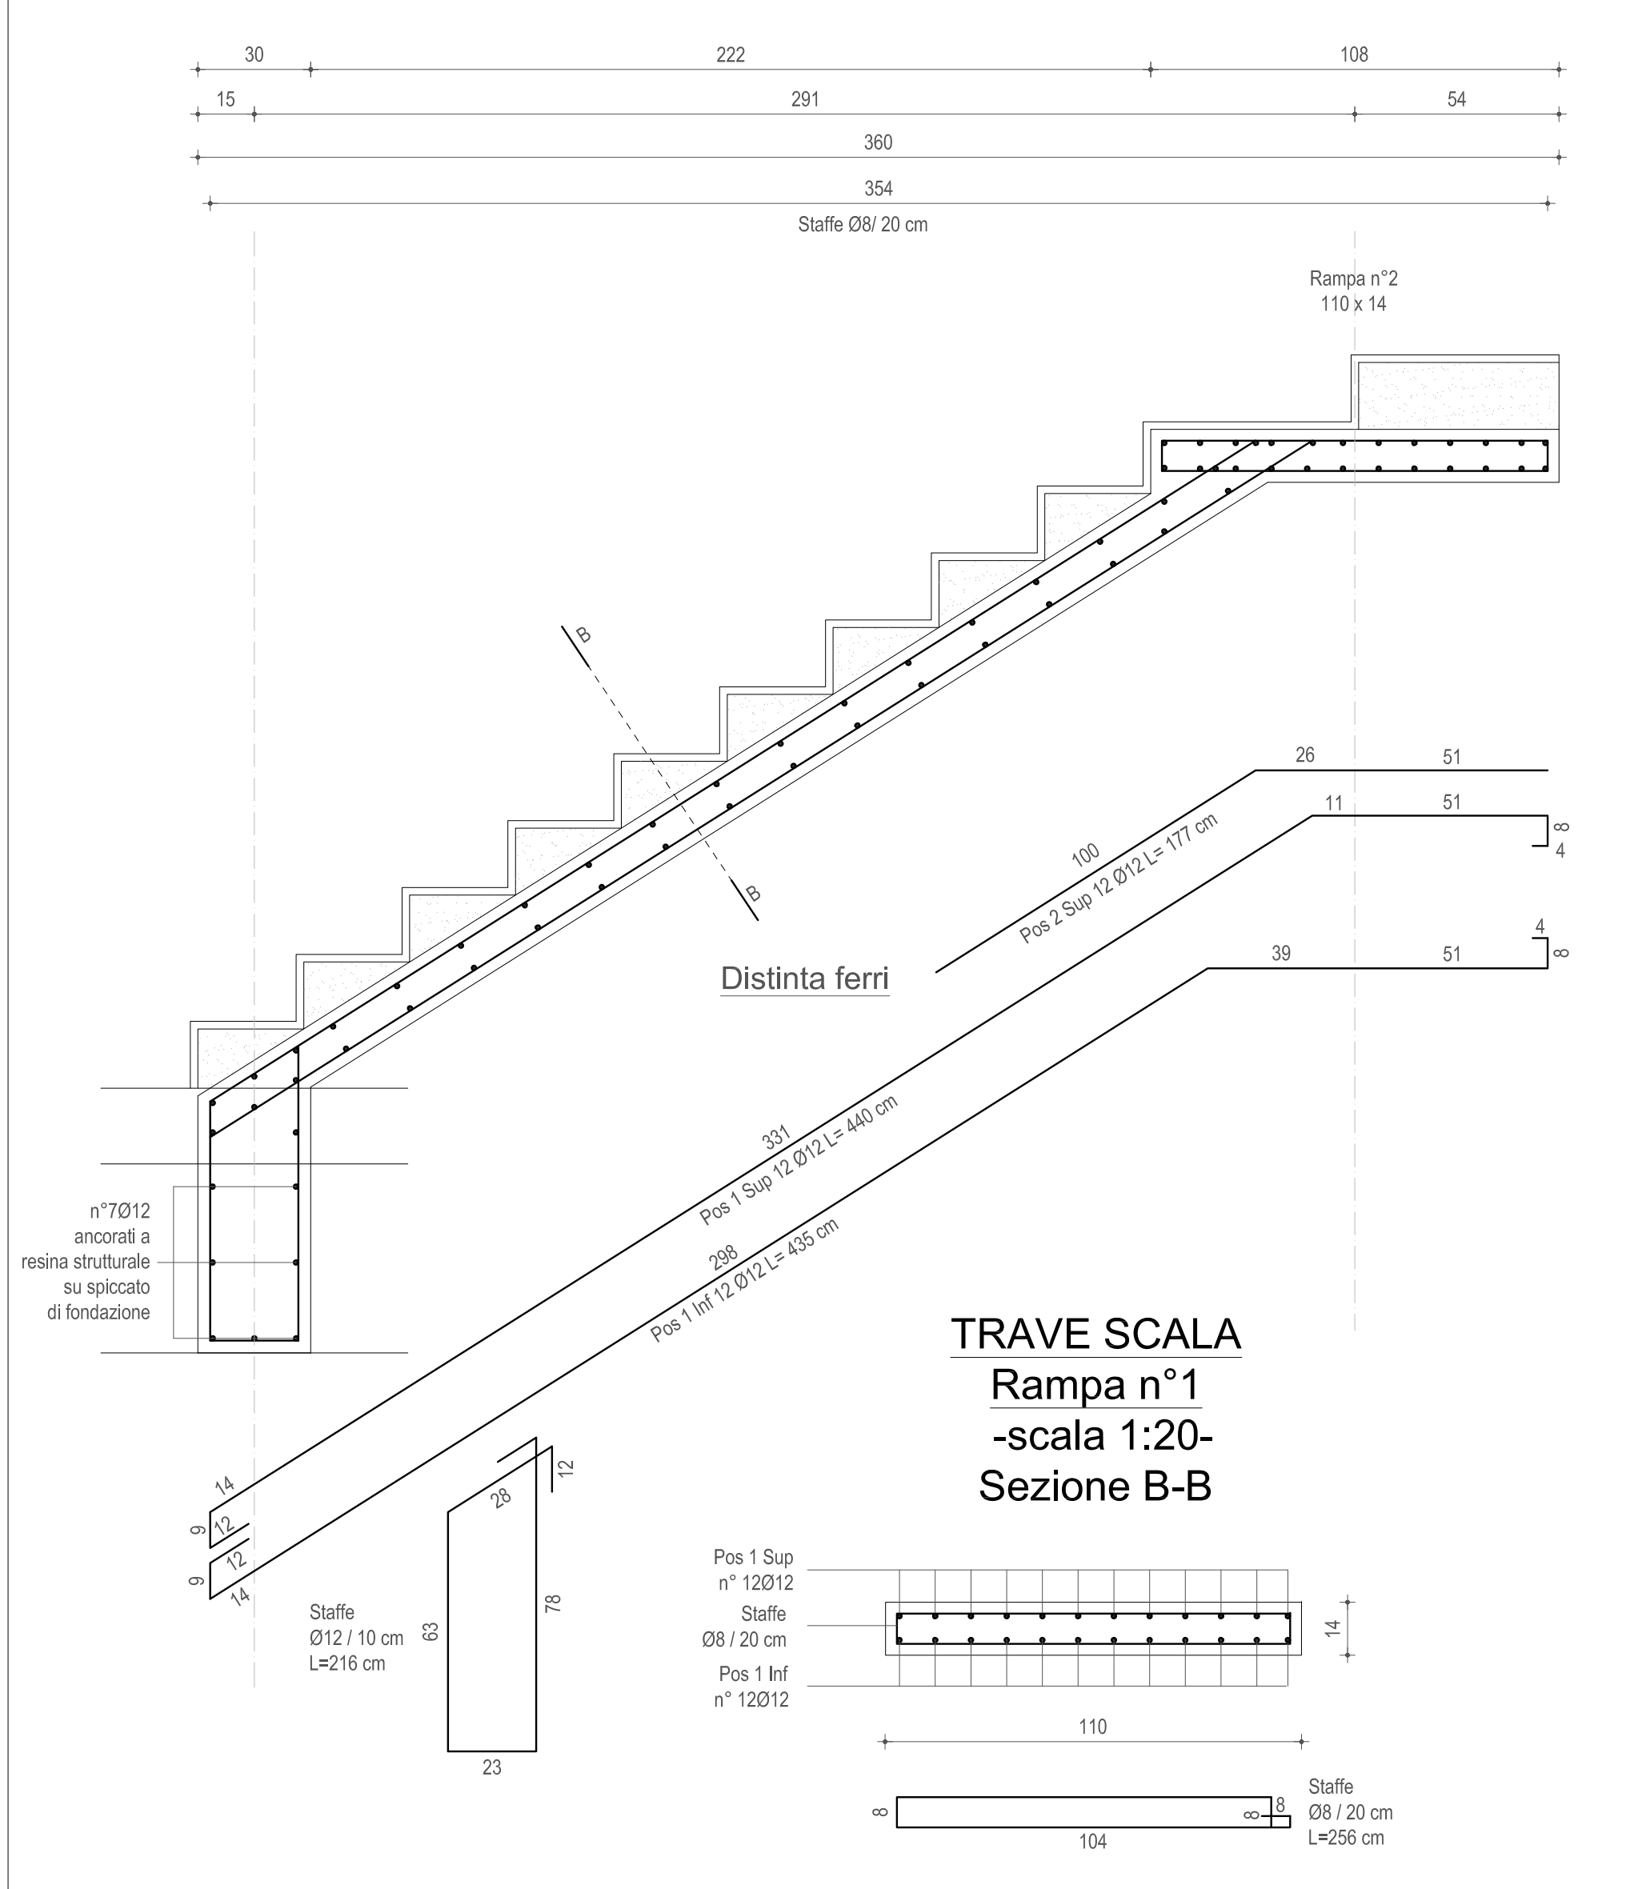

TRAVE SCALA
Rampa n°2
-scala 1:20-

TRAVE SCALA
Rampa n°2
-scala 1:20-
Sezione B-B

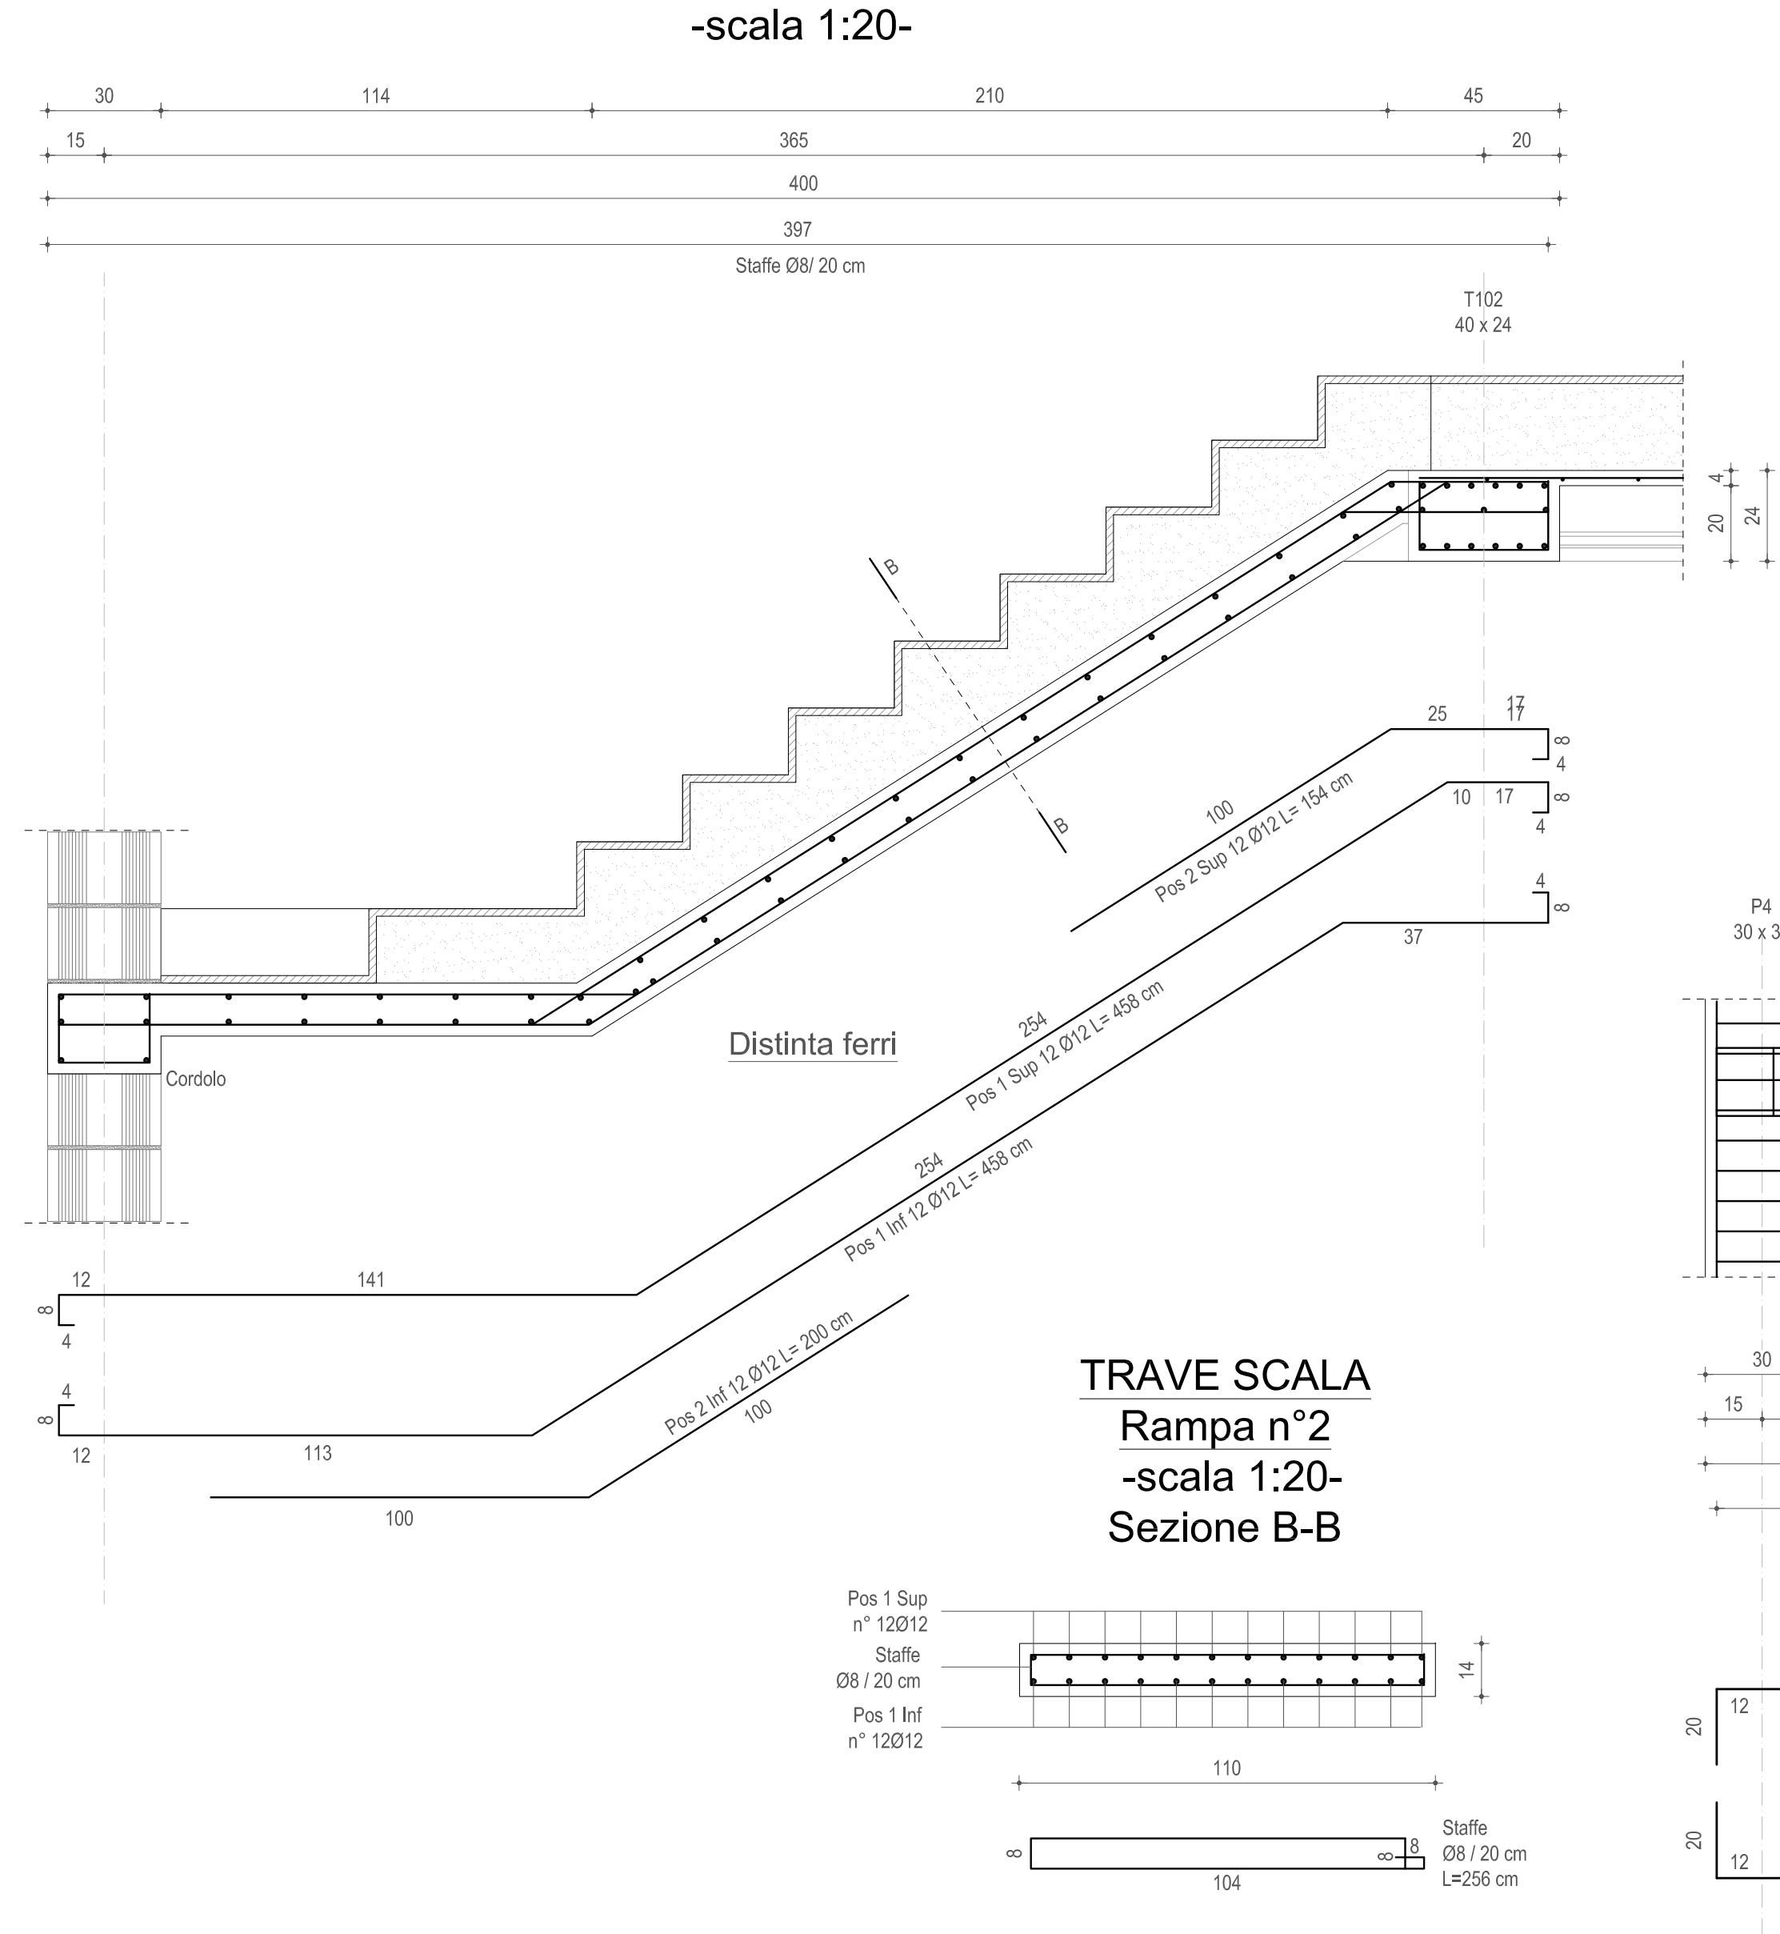

TRAVE -M 01 -
-scala 1:20-

TRAVE -M 01 -
-scala 1:20-
Sezione A-A

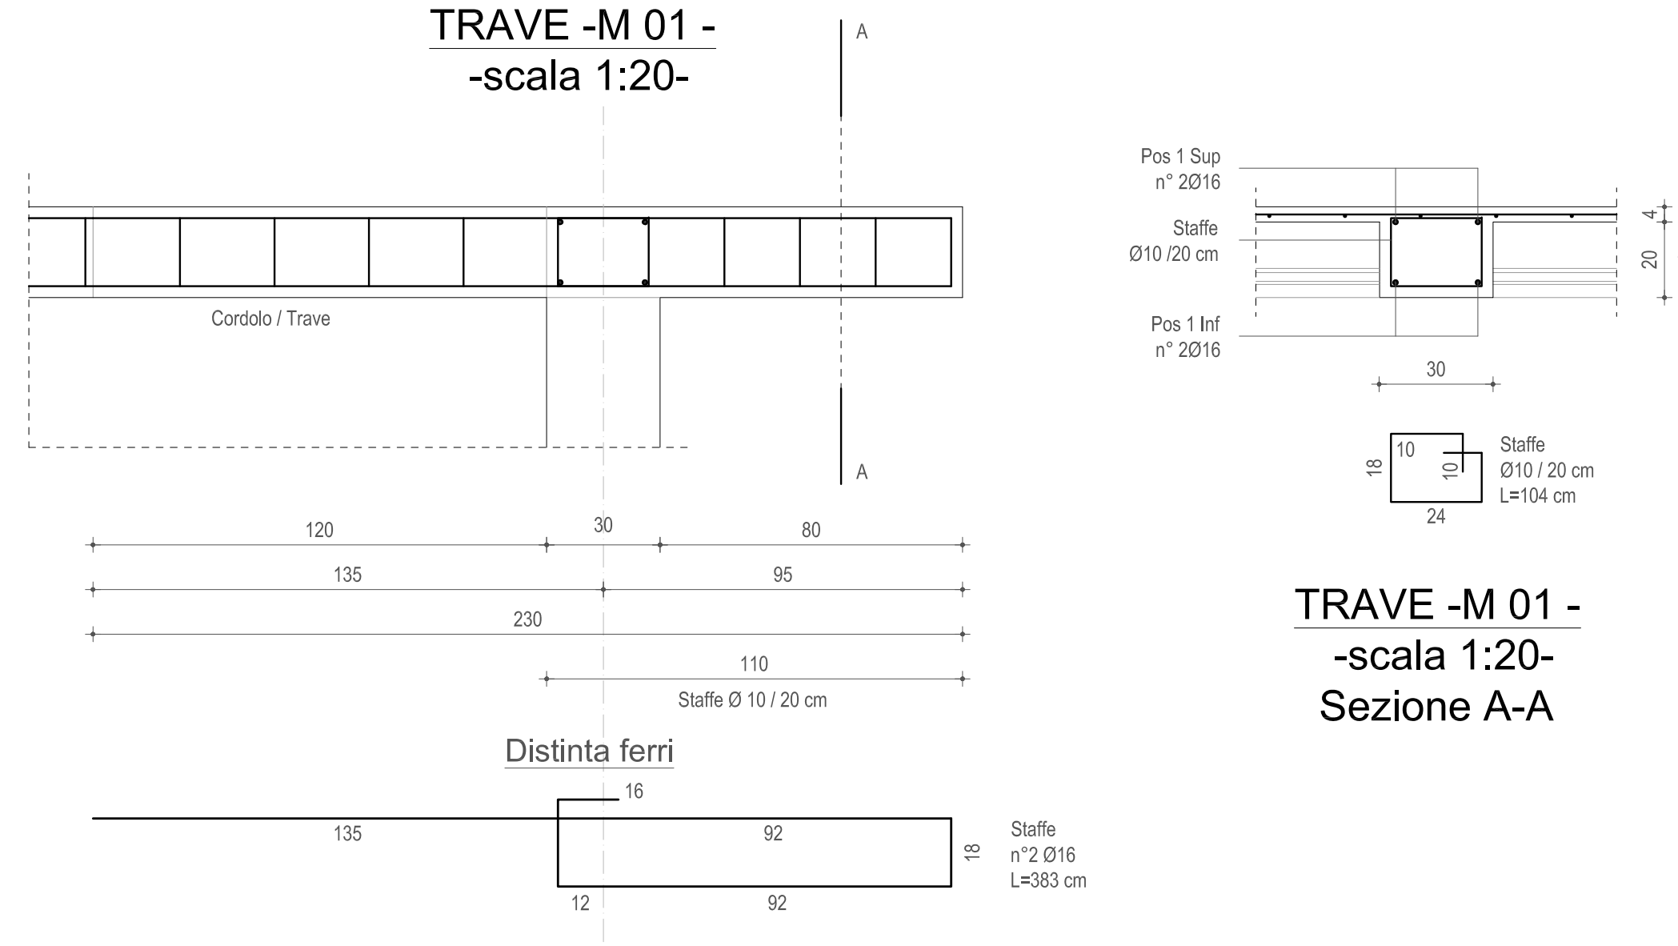

PARTICOLARE ANGOLO CORDOLO
Pianta
-scala 1:20-

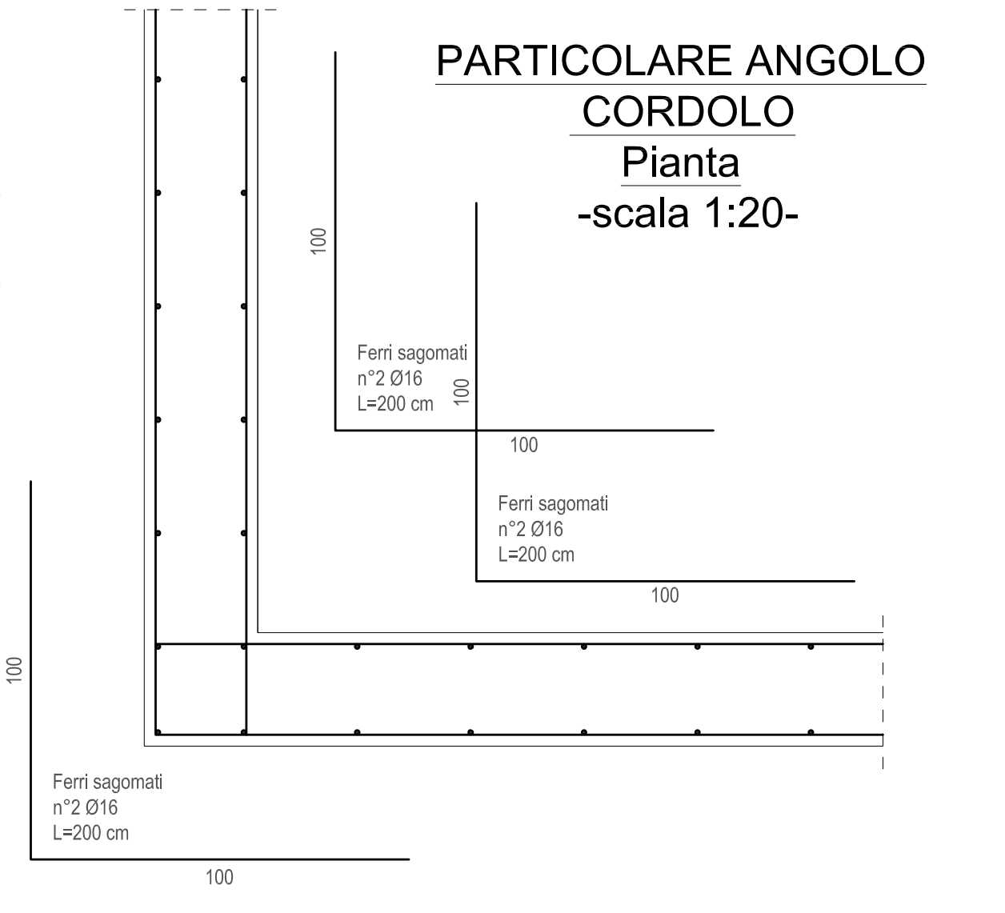

PARTICOLARE INCROCIO CORDOLO
Pianta
-scala 1:20-

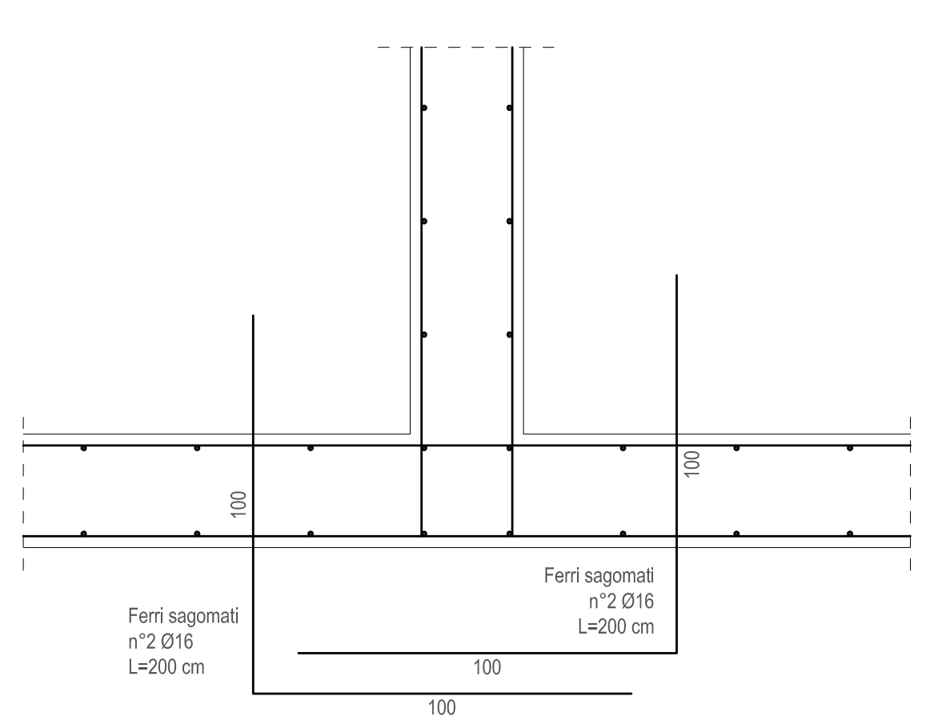

PARTICOLARE CORDOLO
-scala 1:20-

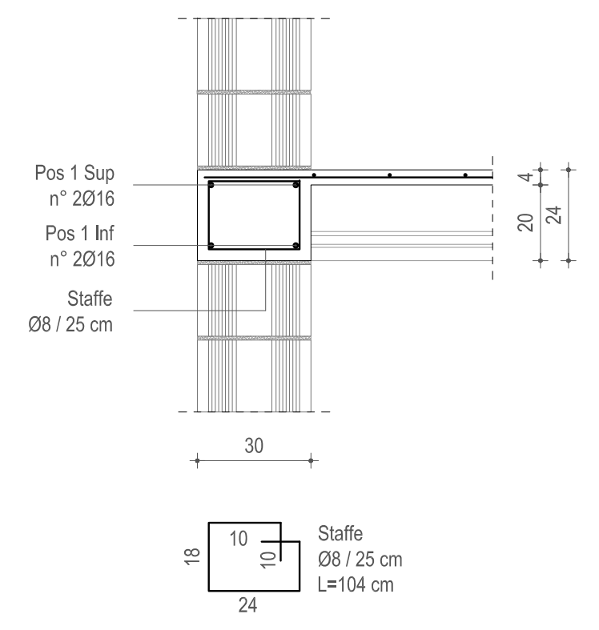

SOLETTA -N -
Sezione trasversale
-scala 1:20-

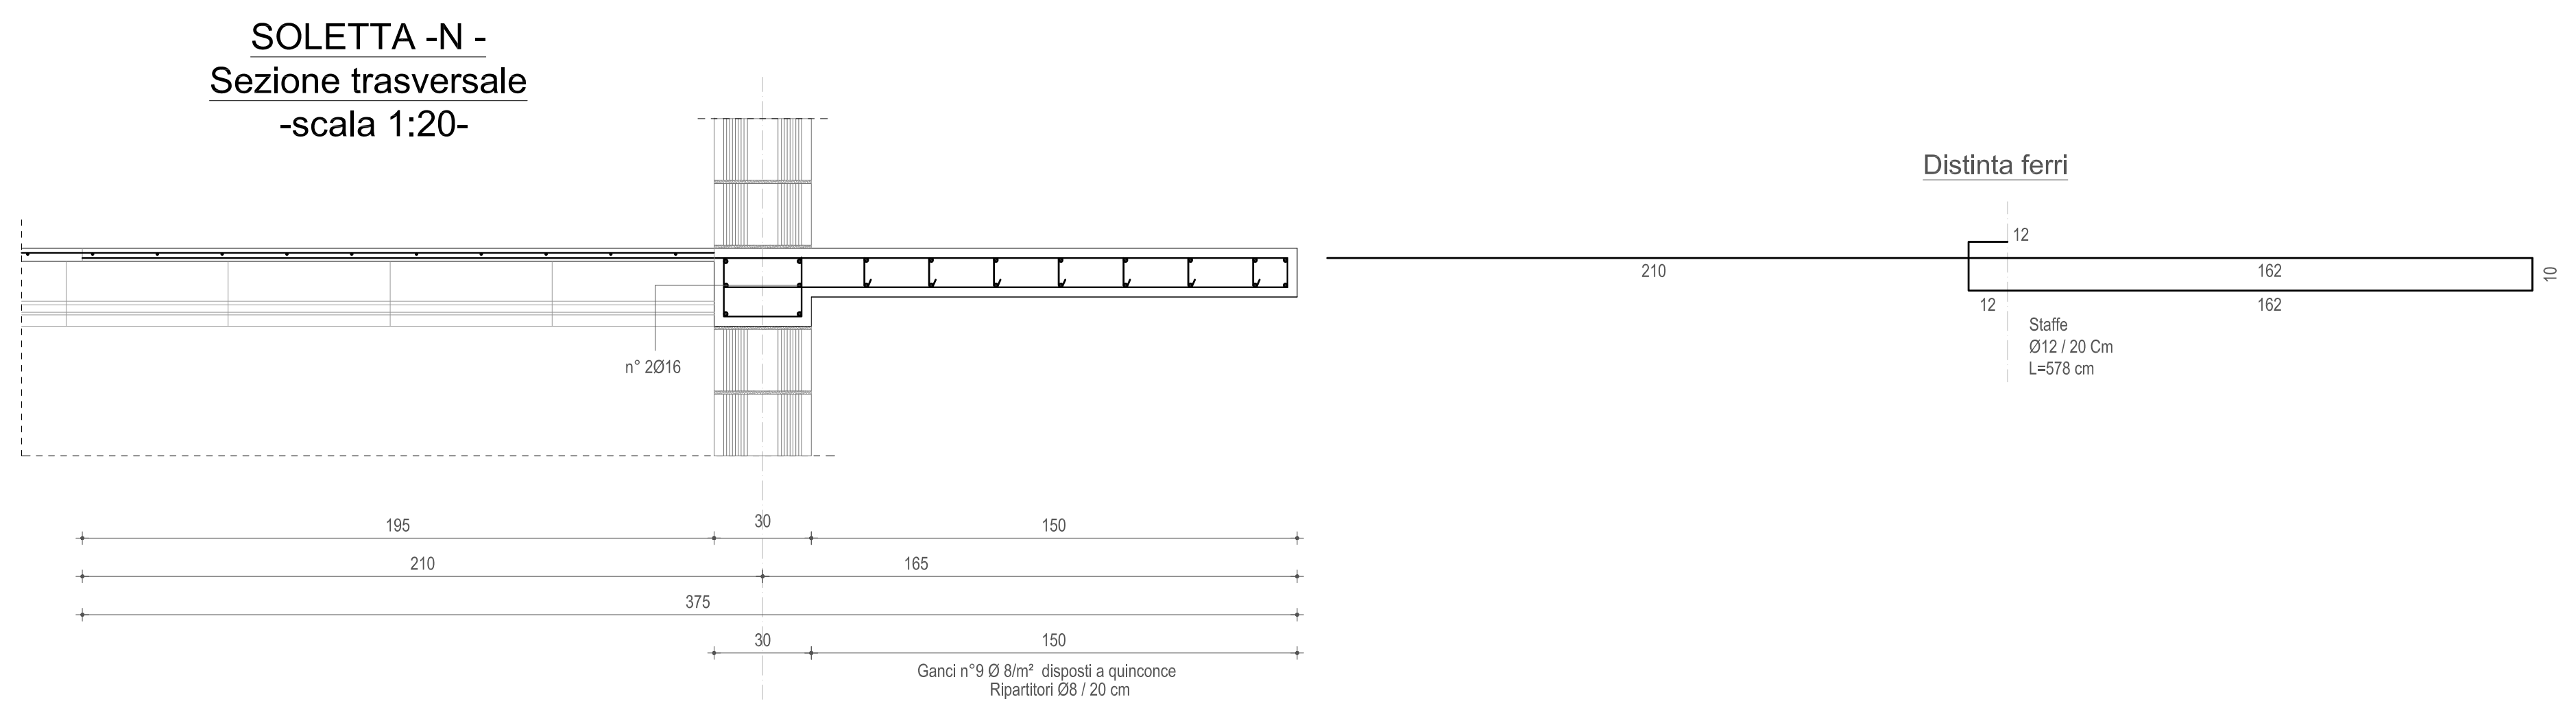

SOLETTA -N -
Sezione longitudinale
-scala 1:20-
n.b. Per soletta d'angolo

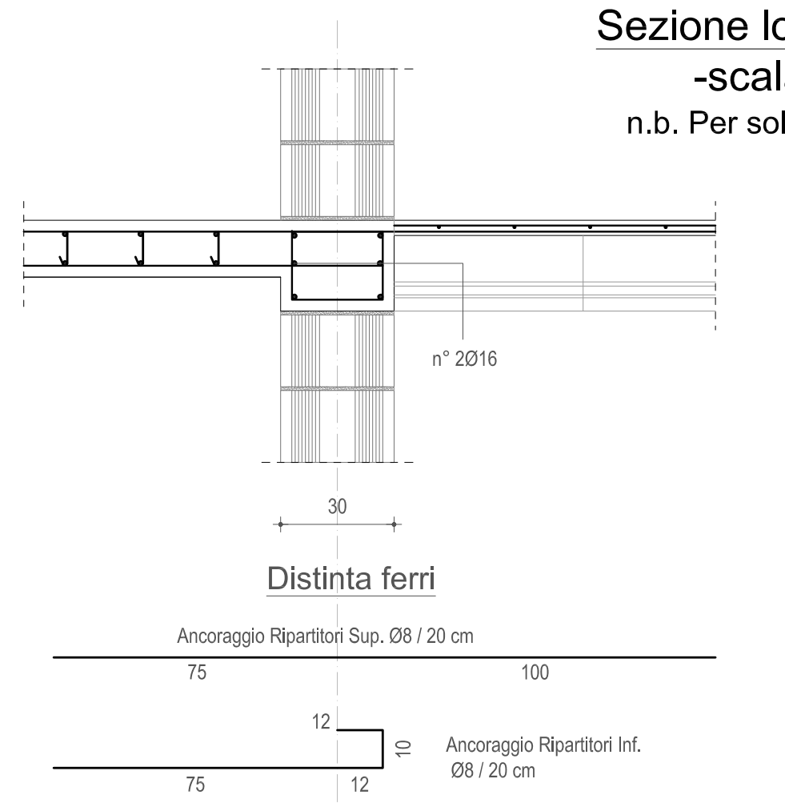

PIANTA IMPALCATO DI COPERTURA -scala 1:100-

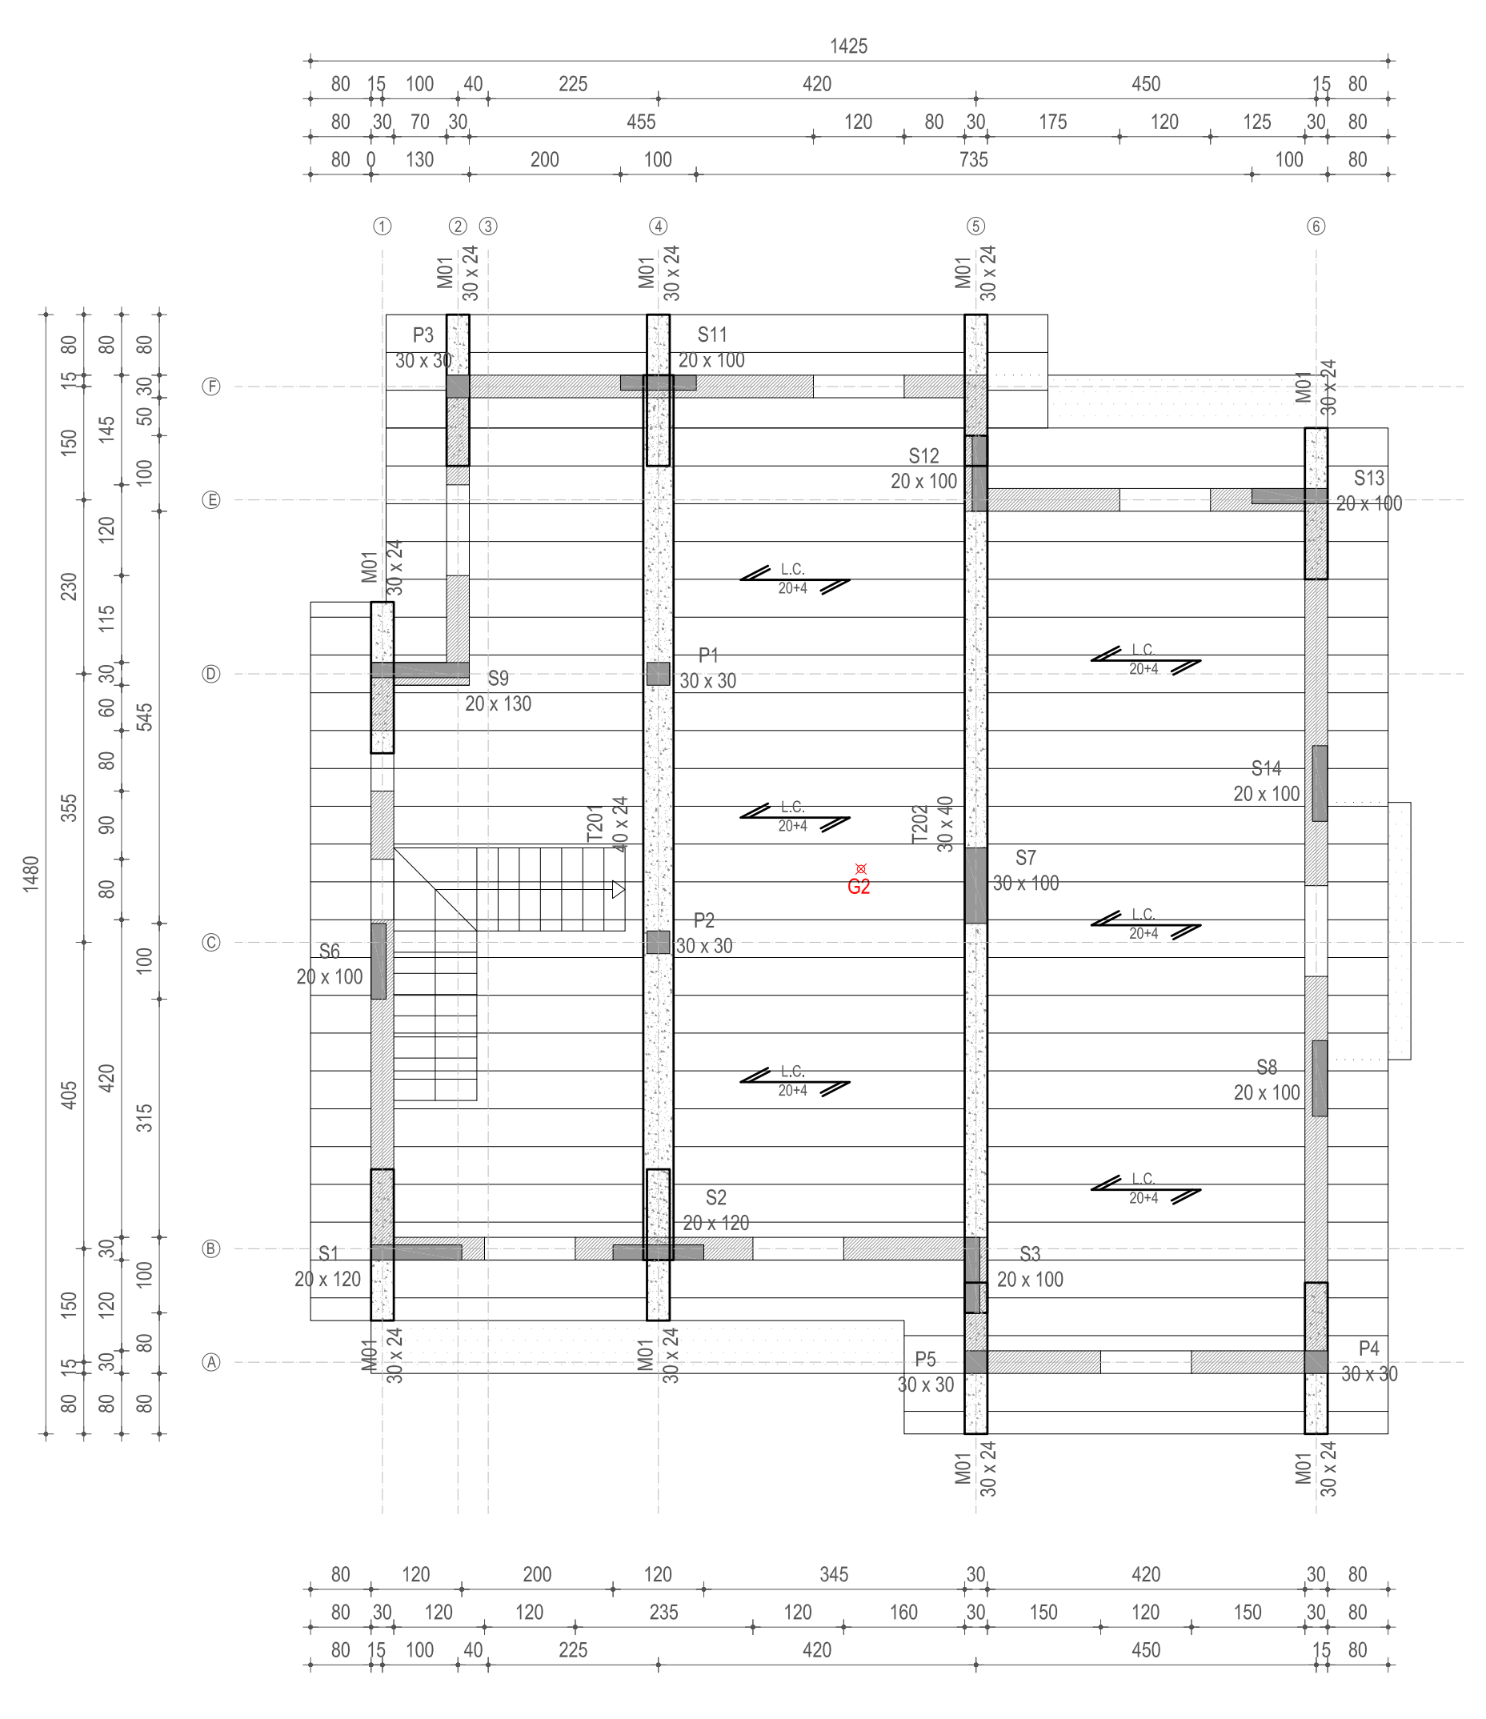

PIANTA PRIMO IMPALCATO -scala 1:100-

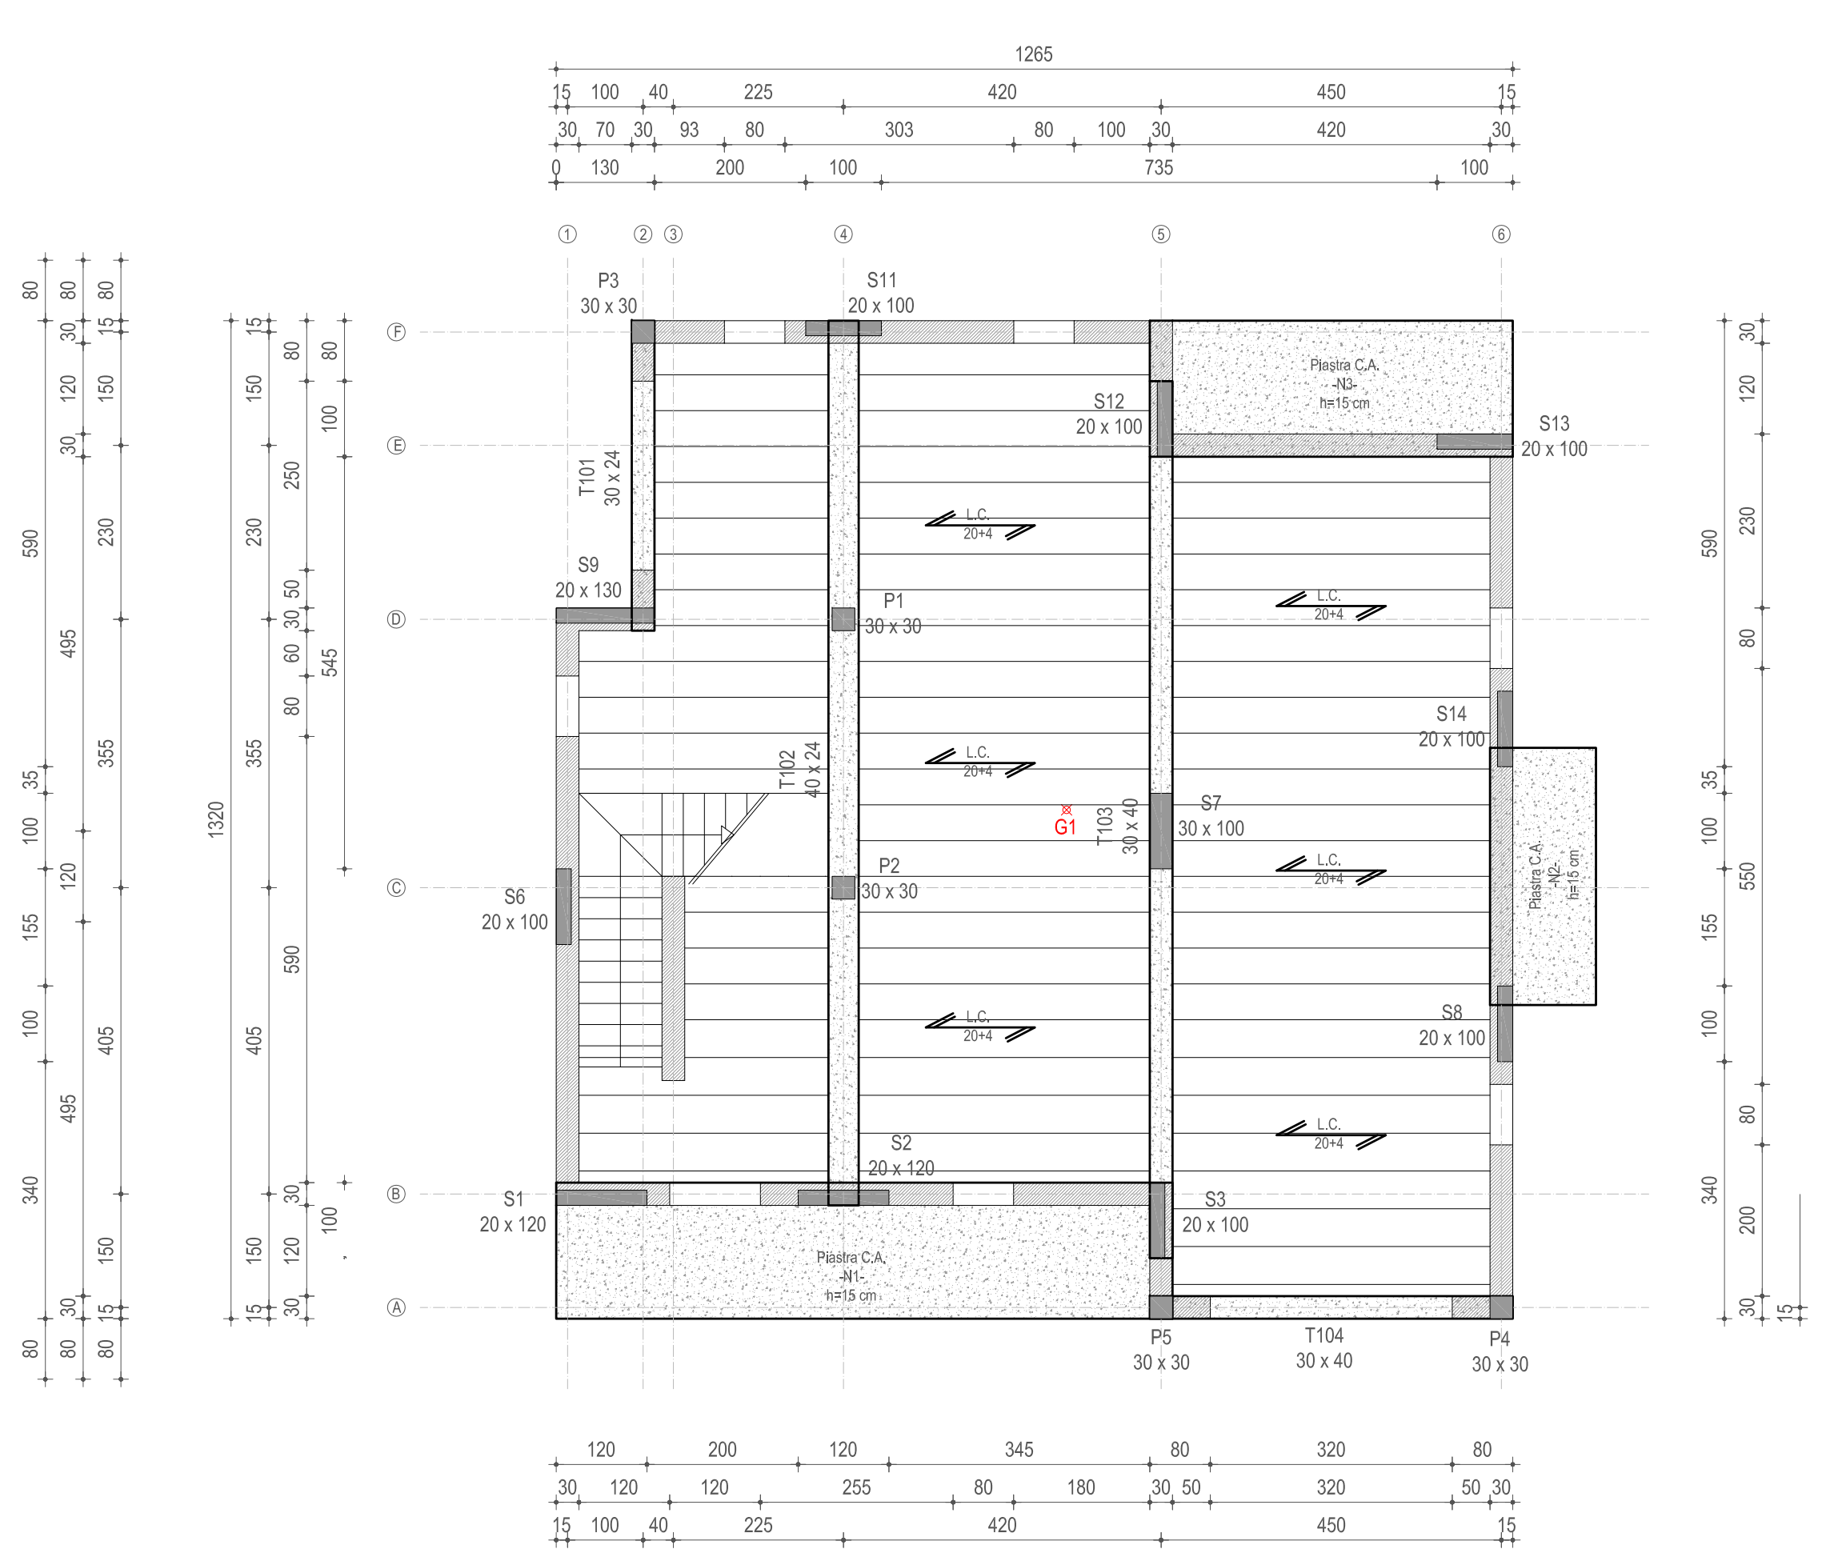

TRAVE -T101 -
-scala 1:20-

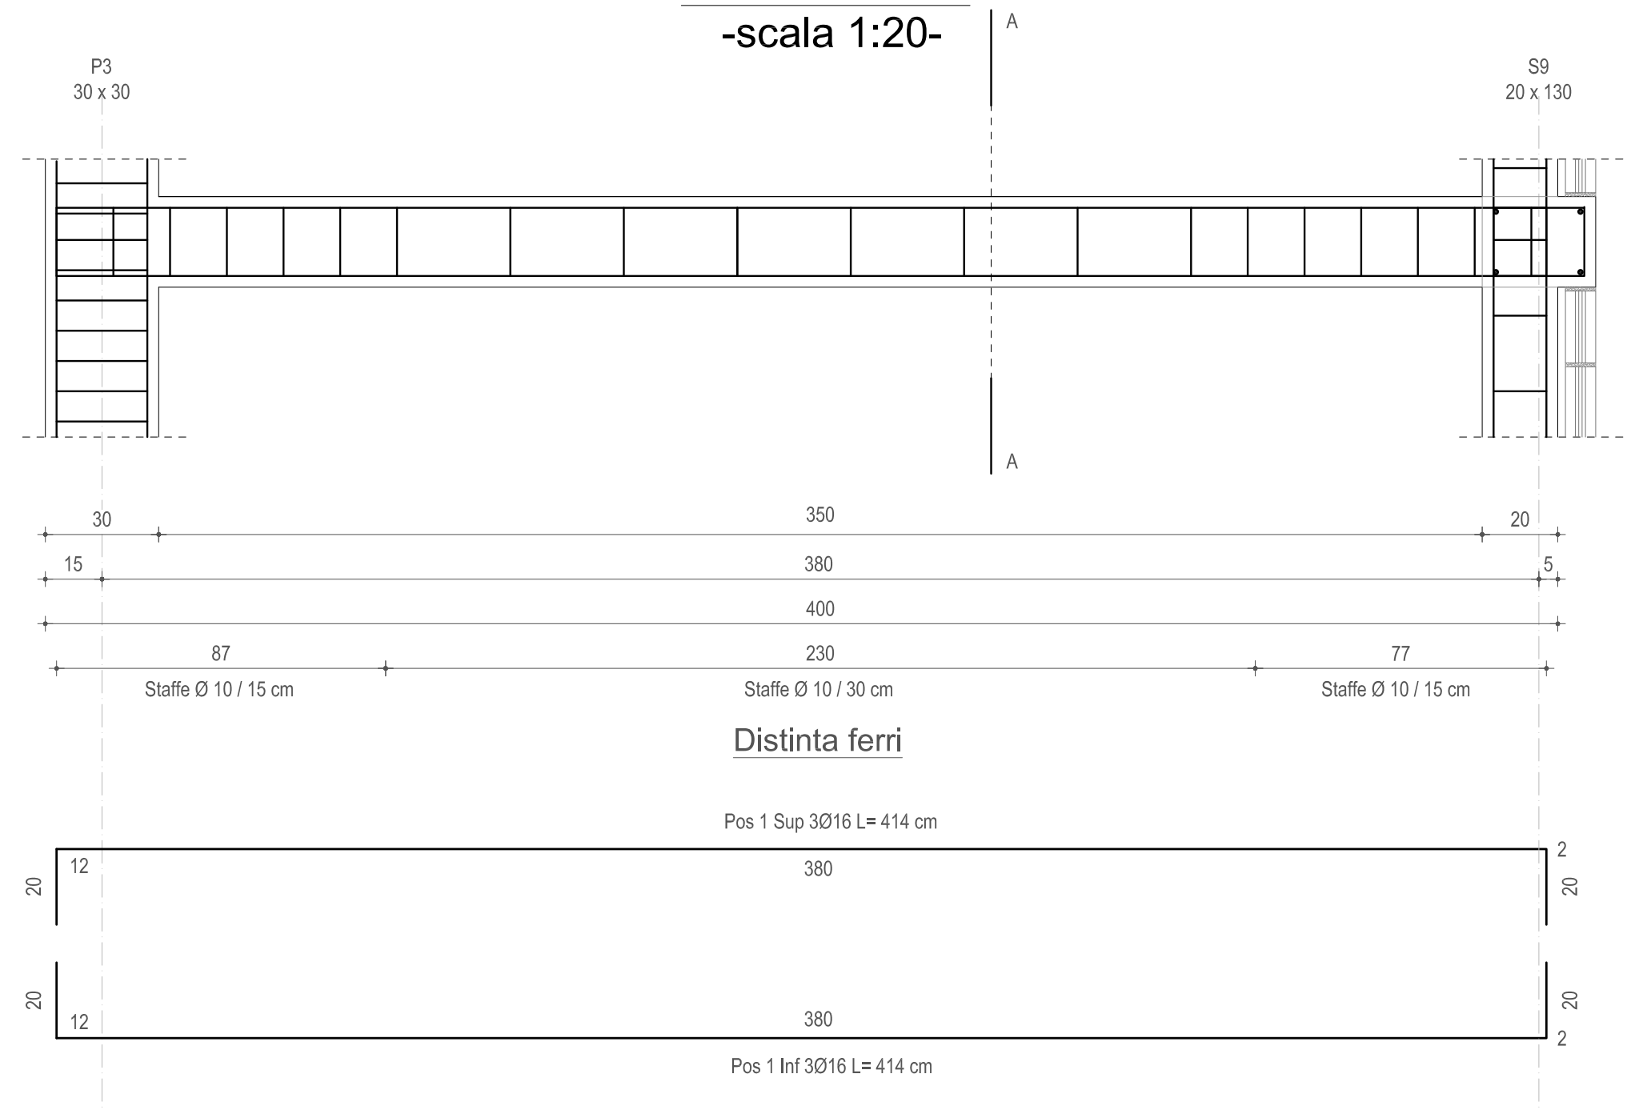

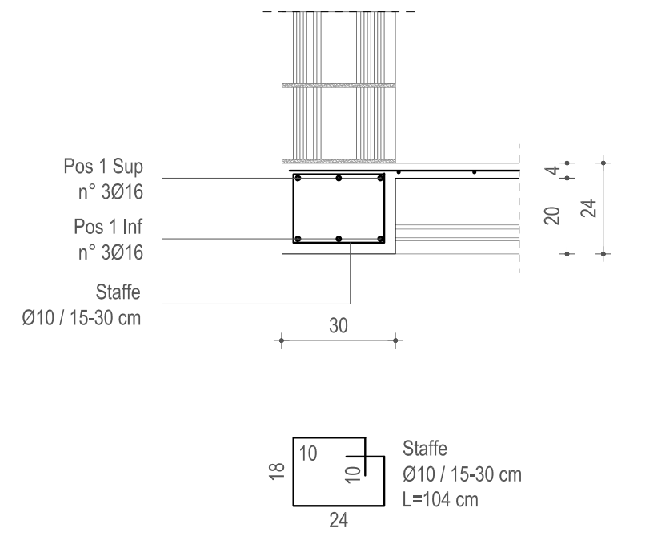

TRAVE -T101 -
-scala 1:20-
Sezione A-A

TRAVE -T102 -T201-
-scala 1:20-

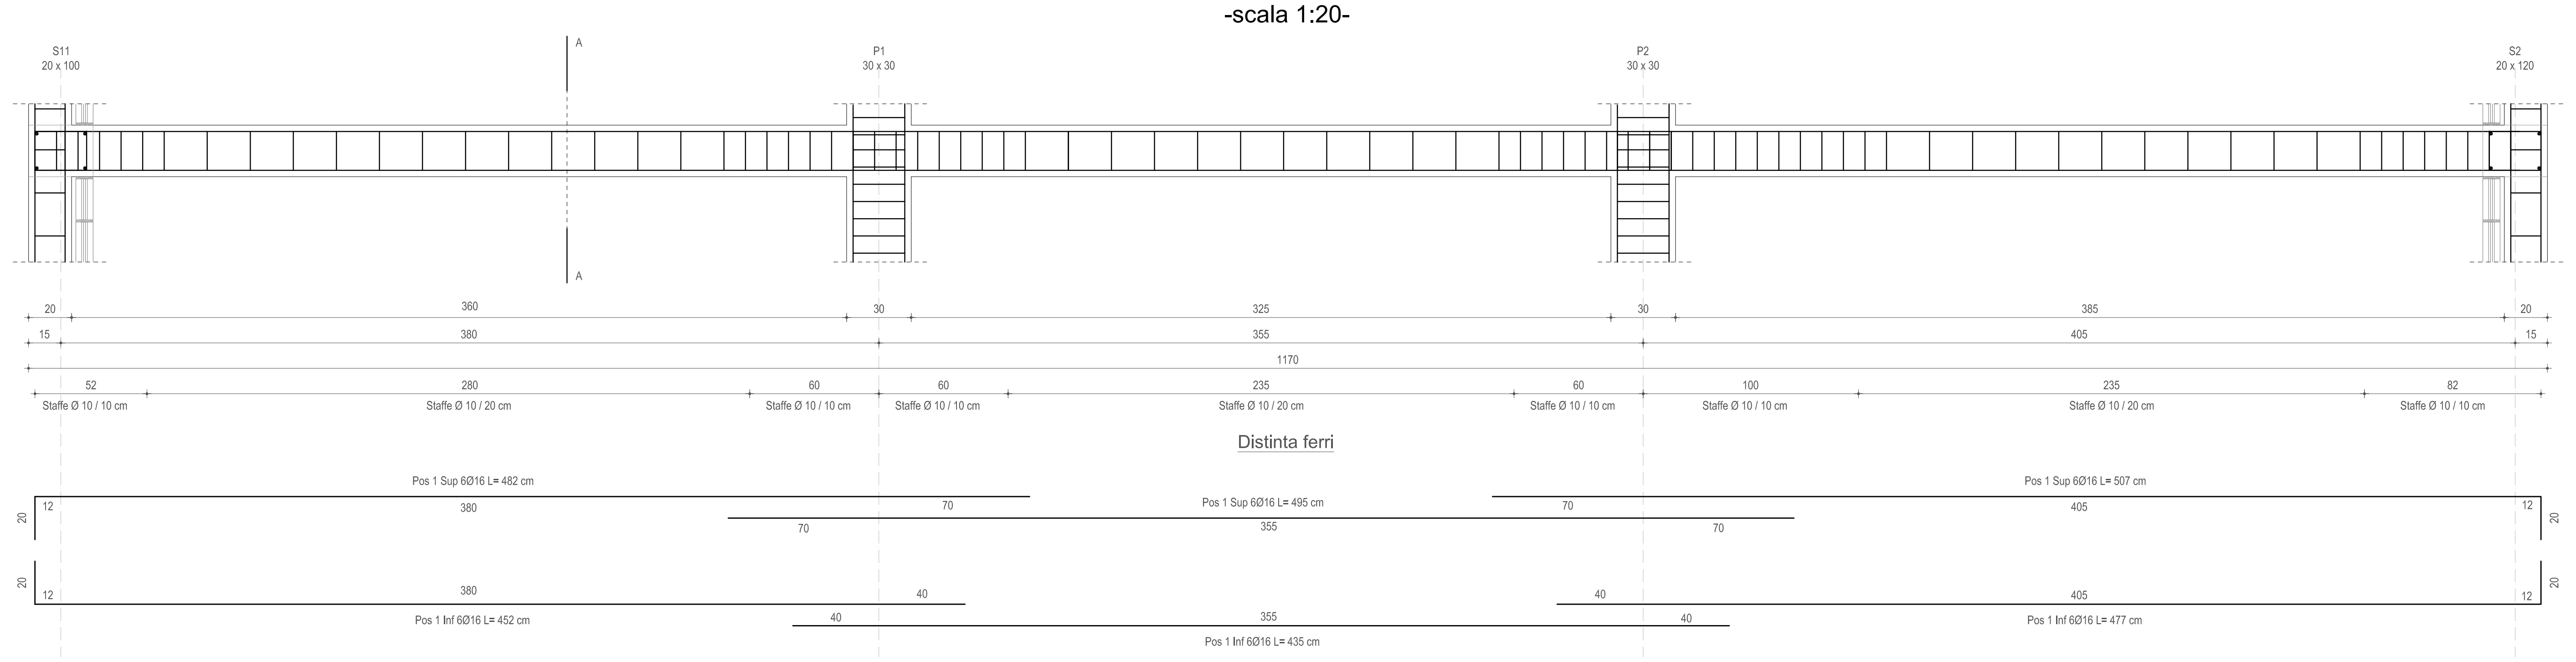

TRAVE -T102 -T201-
-scala 1:20-
Sezione A-A

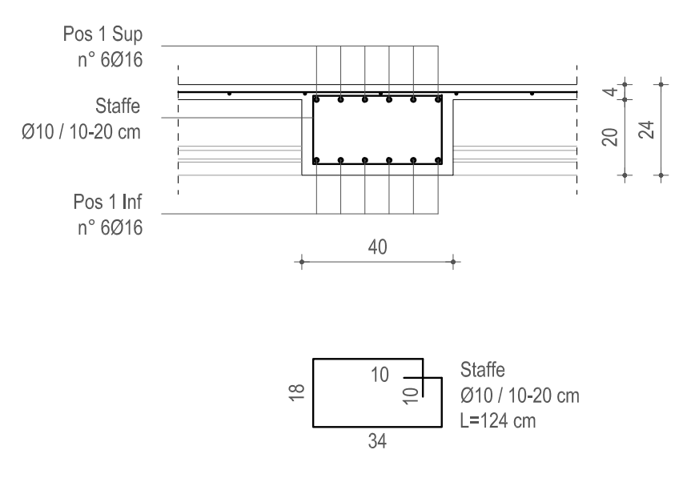

TRAVE -T104 -
-scala 1:20-

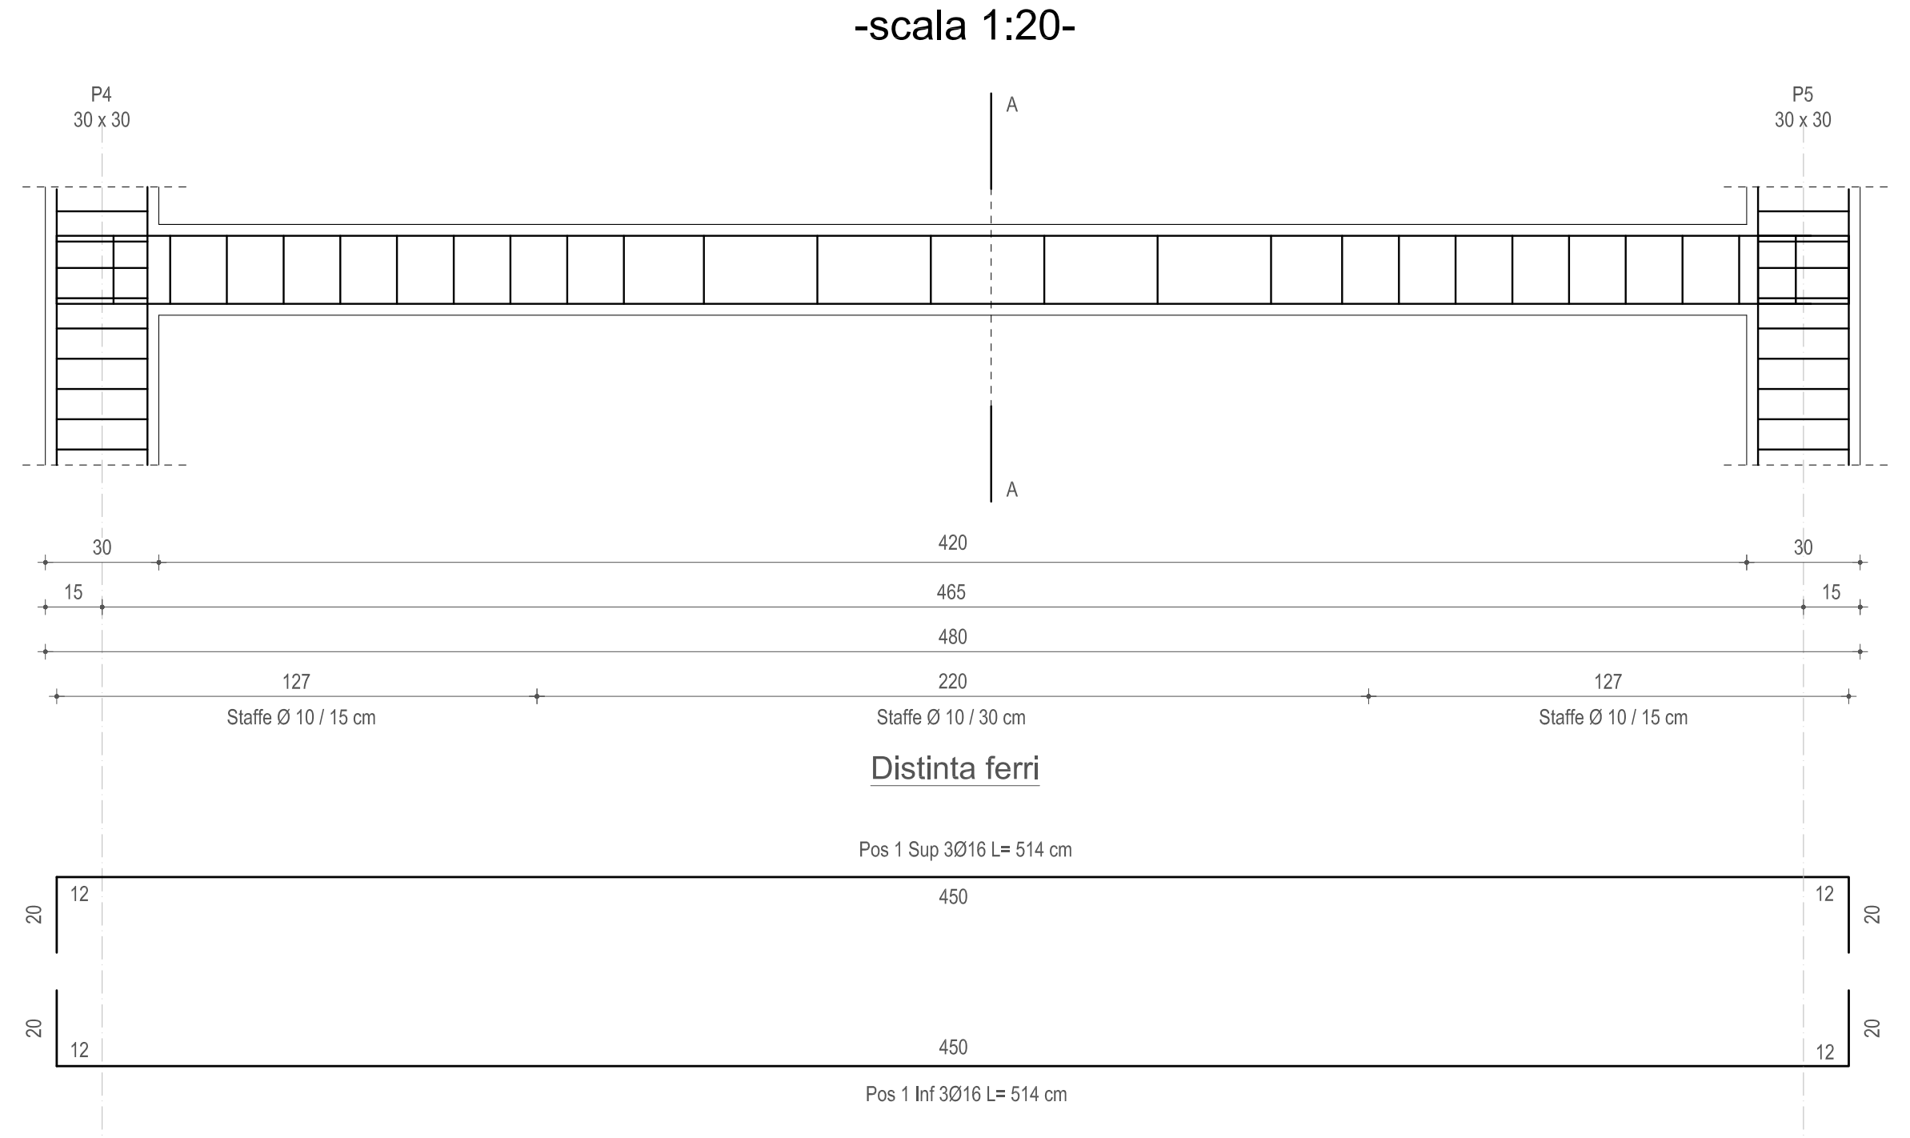

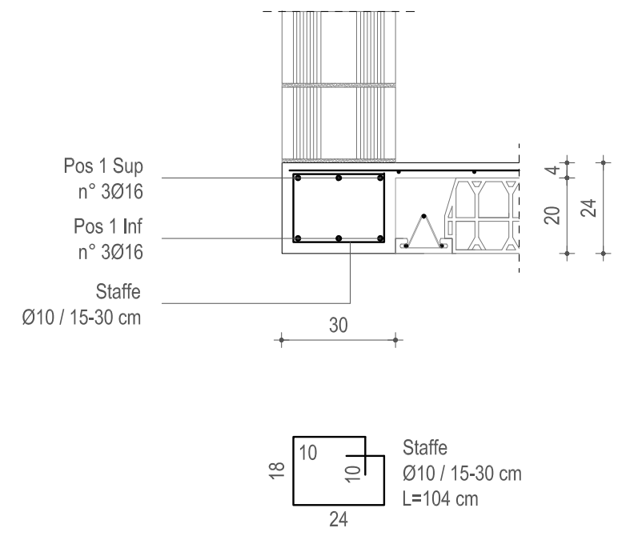

TRAVE -T104 -
-scala 1:20-
Sezione A-A

TRAVE -T103 -T202-
-scala 1:20-

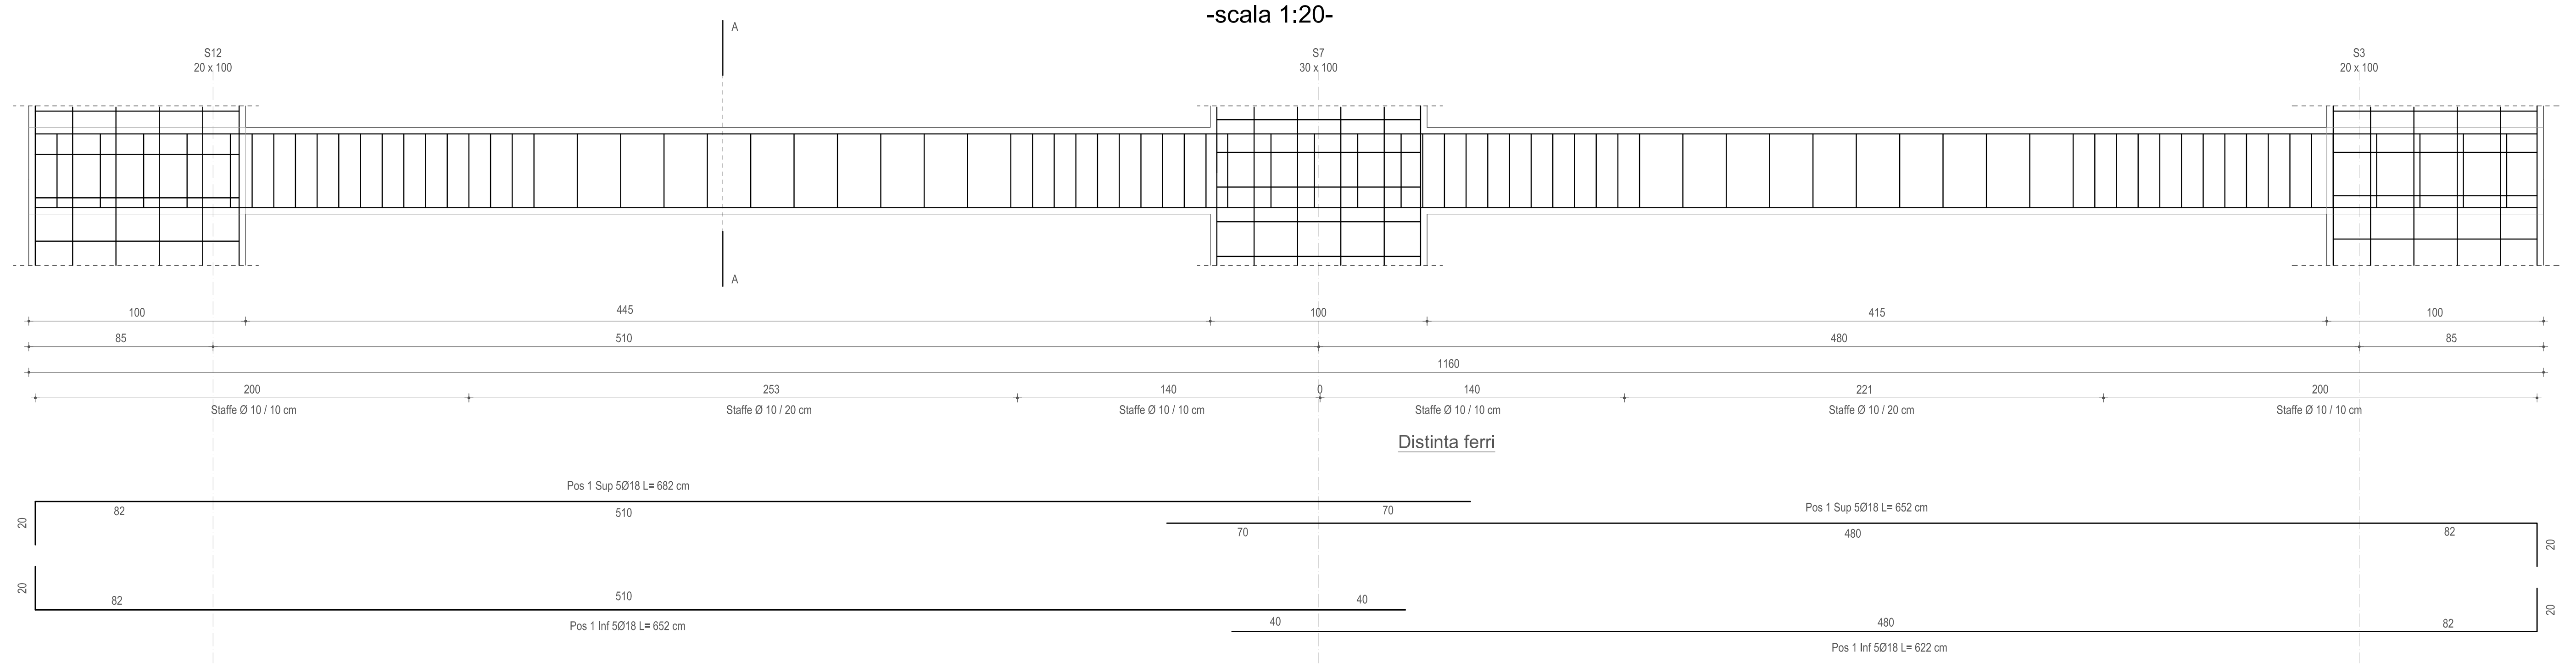

TRAVE -T103 -
-scala 1:20-
Sezione A-A

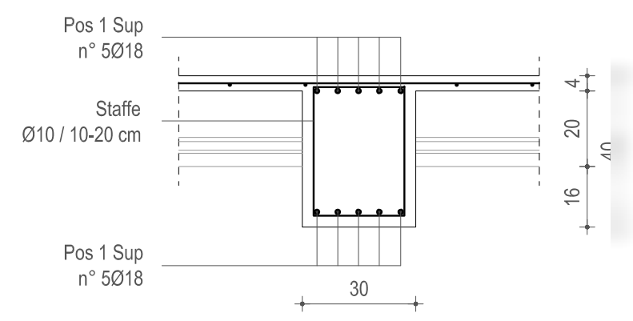

TRAVE -T202 -
-scala 1:20-
Sezione A-A

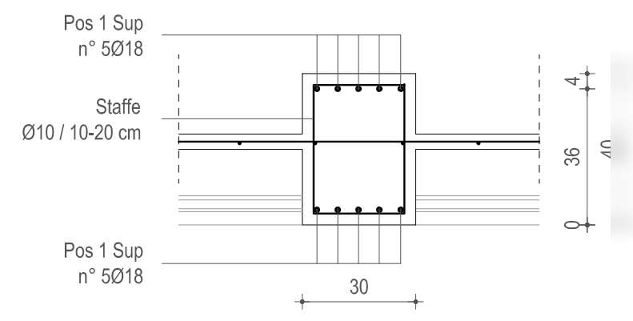

MATERIALI E PRESCRIZIONI

MATERIALI PRESCRITTI:

- Calcestruzzo per opere di: Fondazioni

  - Classe di resistenza : C25/30 (Rck 30)
  - Condizioni ambientali: Strutture completamente interrate in terreno permeabile
  - Classe di esposizione : XC2
  - Rapporto massimo acqua/cemento: 0,60
  - Classe di consistenza: S3 (Plastica)
  - Diametro massimo degli aggregati: 16 mm

- Calcestruzzo per opere di: Elevazione e Solai misti laterizio-c.a.
  - Classe di resistenza : C25/30 (Rck 30)
  - Condizioni ambientali: Strutture interne di edifici non industriali con umidità bassa
  - Classe di esposizione : XC1
  - Rapporto massimo acqua/cemento: 0,60
  - Classe di consistenza: S3 (Plastica)
  - Diametro massimo degli aggregati: 16 mm

- Calcestruzzo per opere di: Solette piene in C.A.

  - Classe di resistenza : C25/30 (Rck 30)
  - Condizioni ambientali: Strutture interne di edifici non industriali con umidità bassa
  - Classe di esposizione : XC1
  - Rapporto massimo acqua/cemento: 0,60
  - Classe di consistenza: S3 (Plastica)
  - Diametro massimo degli aggregati: 16 mm

- Acciaio per tutte le strutture: B450 C controllato

PRESCRIZIONE

Tutte le misure dovranno essere controllate in cantiere confrontandole con quelle del progetto architettonico e confermate dalla direzione lavori

COMUNE DI RODIGO PROVINCIA DI MANTOVA

[redacted]

- Disegni esecutivi:
  Primo impalcato
  Impalcato di copertura
  Travi

Denuncia C.A.

Tav. n° 2	Variante
Data	Scale 1:100, 1:20

[redacted]

aboratori