SETTO 30 x 100
-scala 1:20-

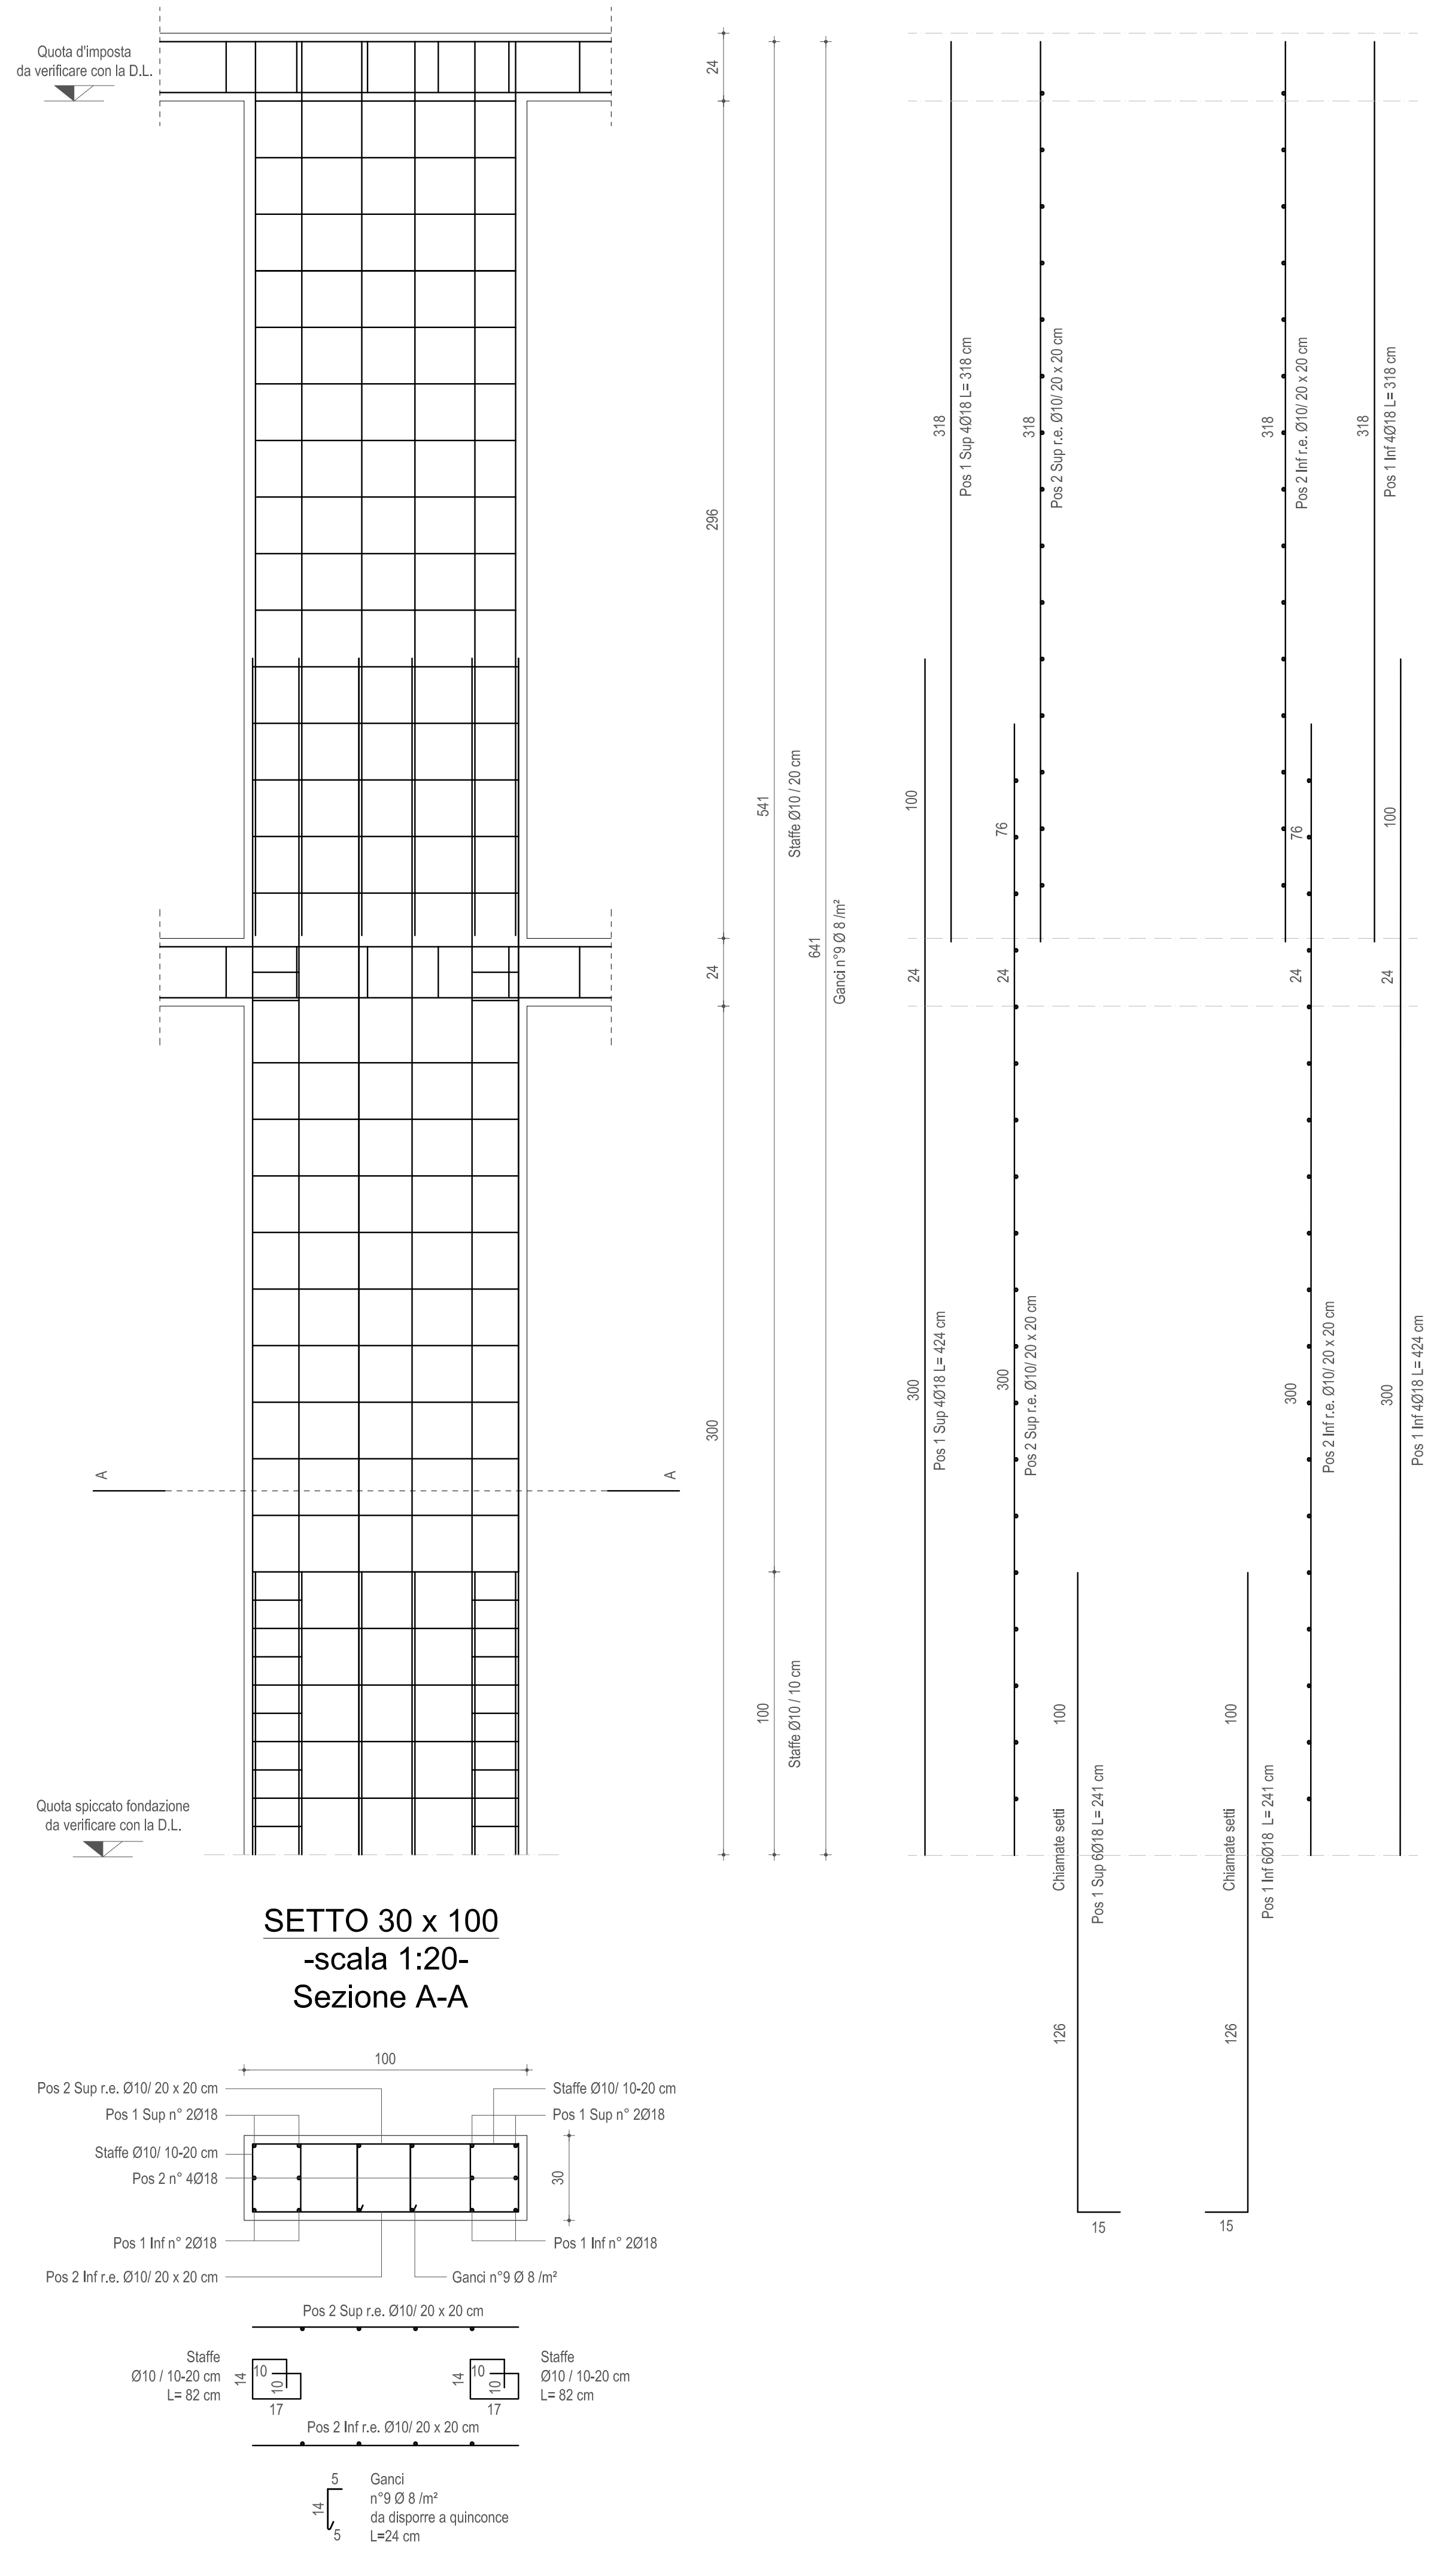

SETTO 30 x 100
-scala 1:20-
Sezione A-A

SETTO 20 x 130
-scala 1:20-

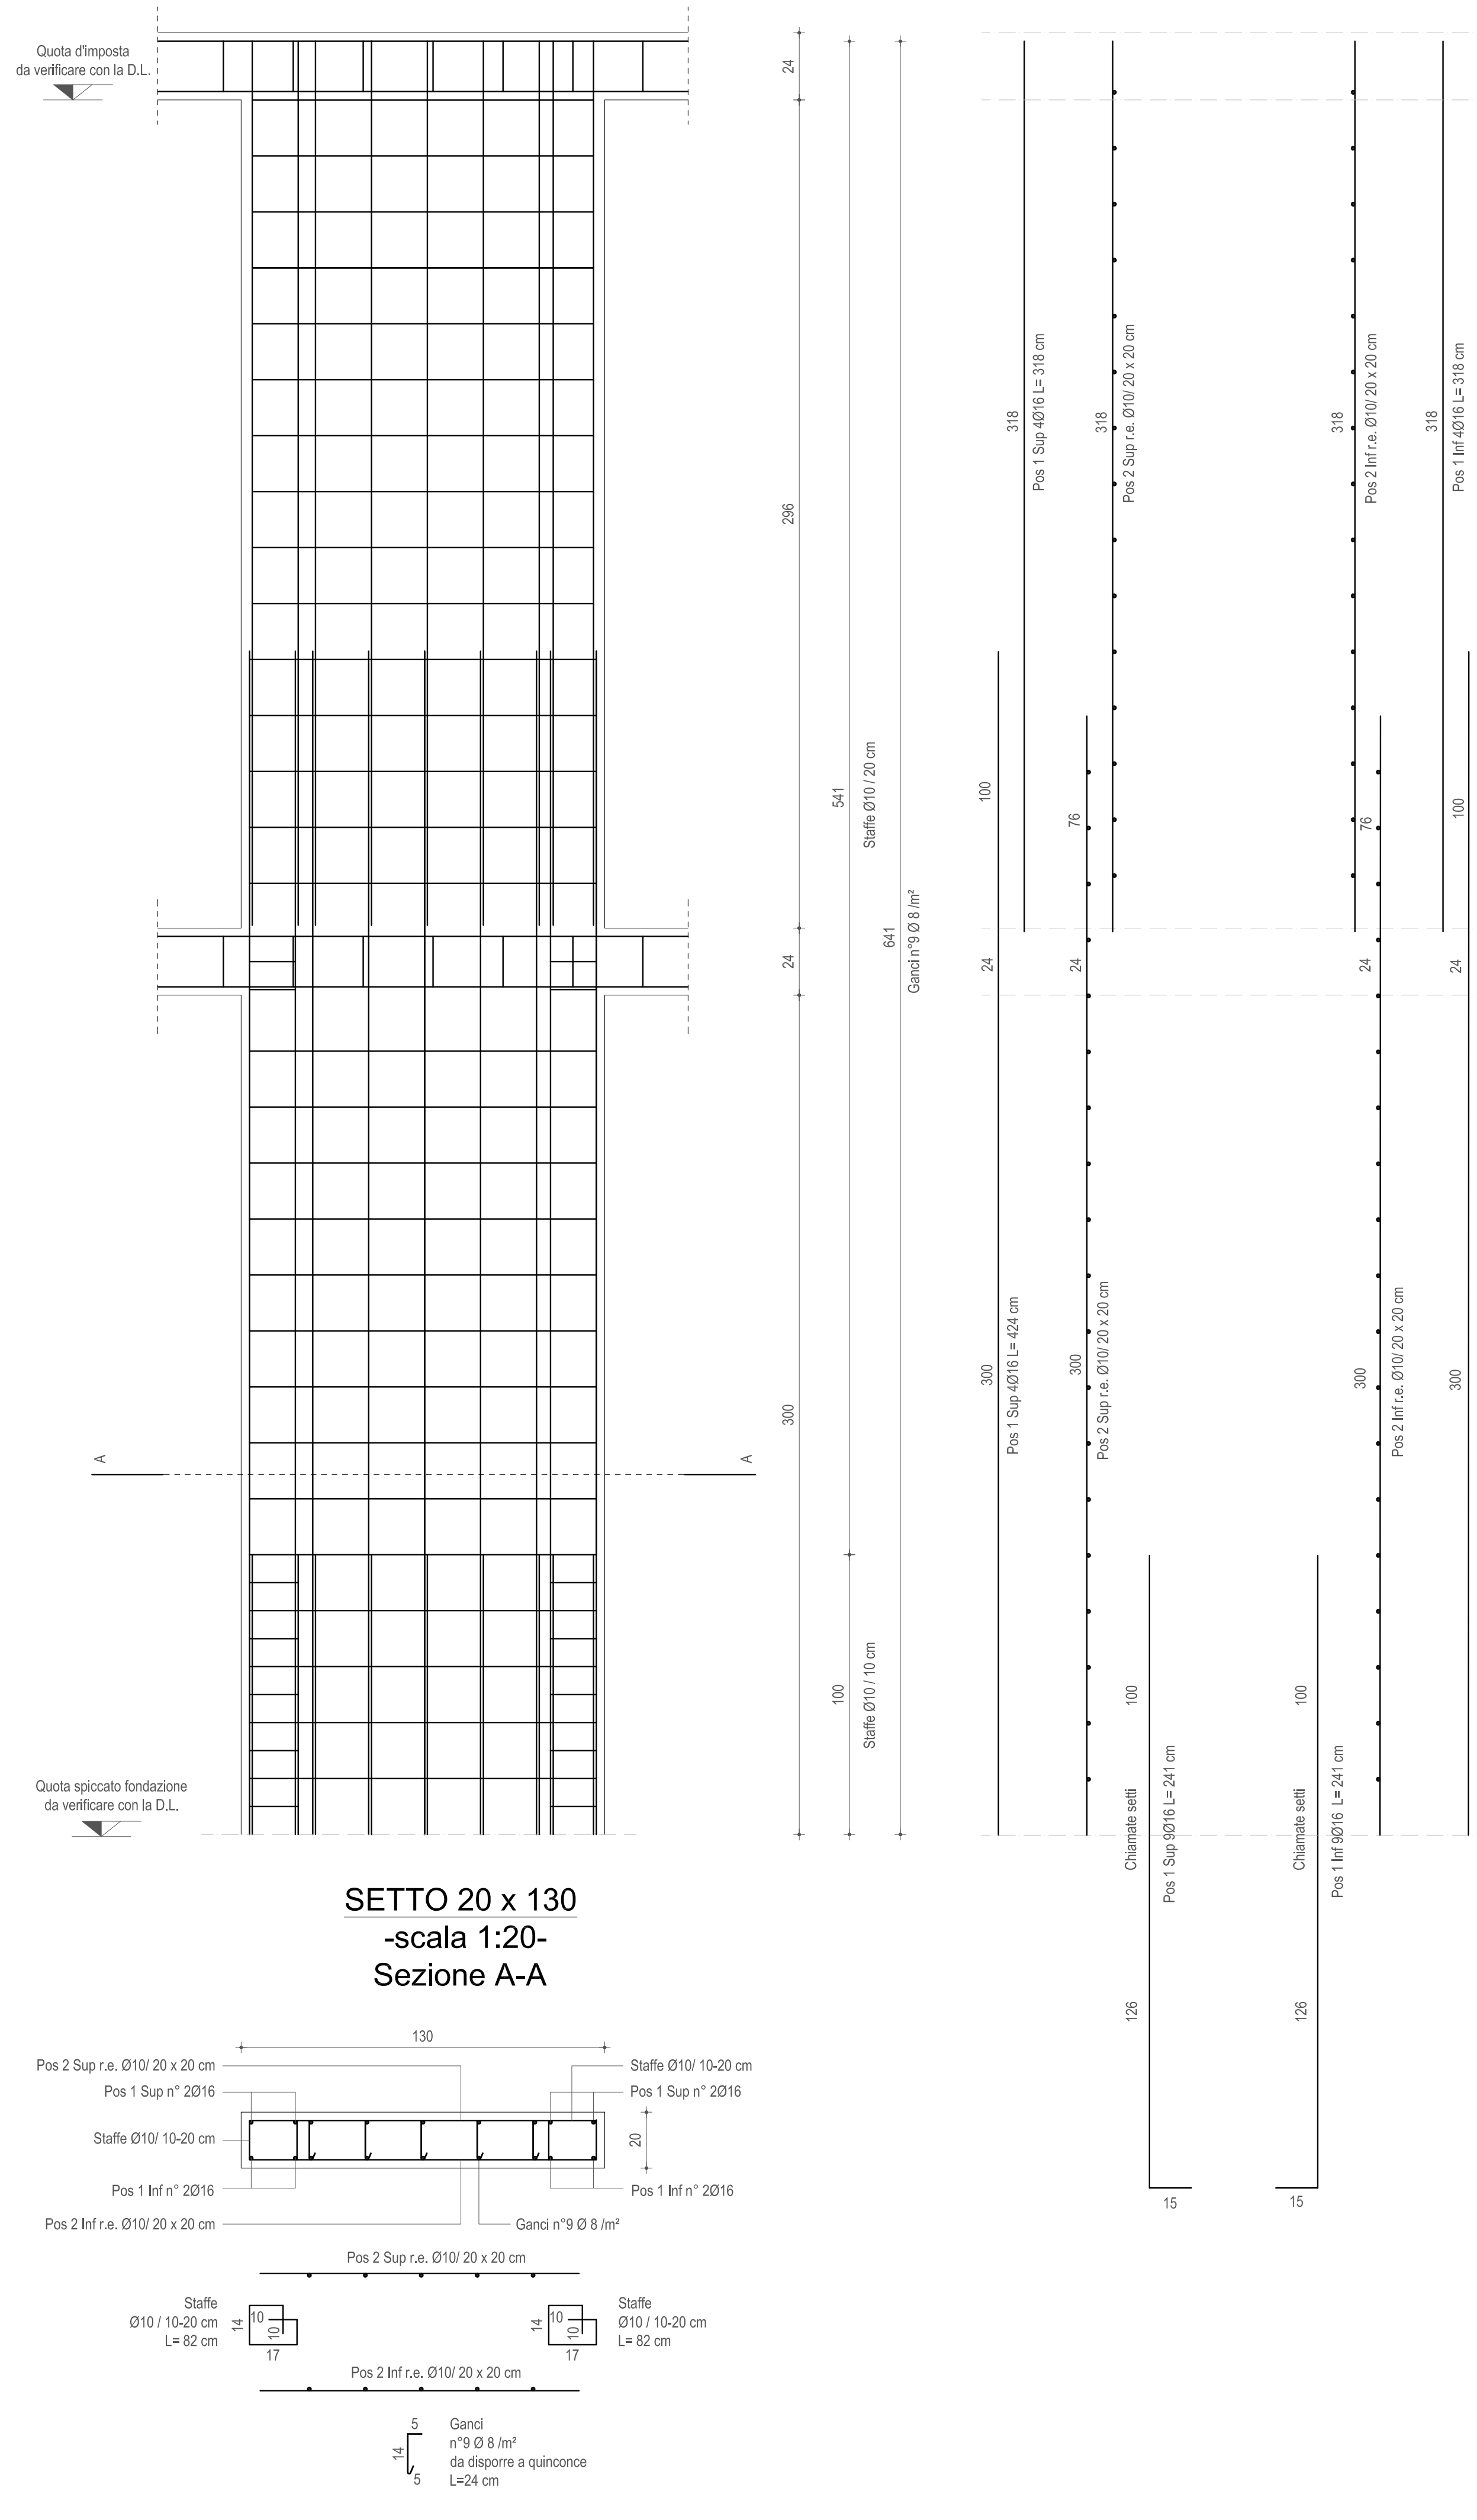

SETTO 20 x 130
-scala 1:20-
Sezione A-A

SETTO 20 x 120
-scala 1:20-

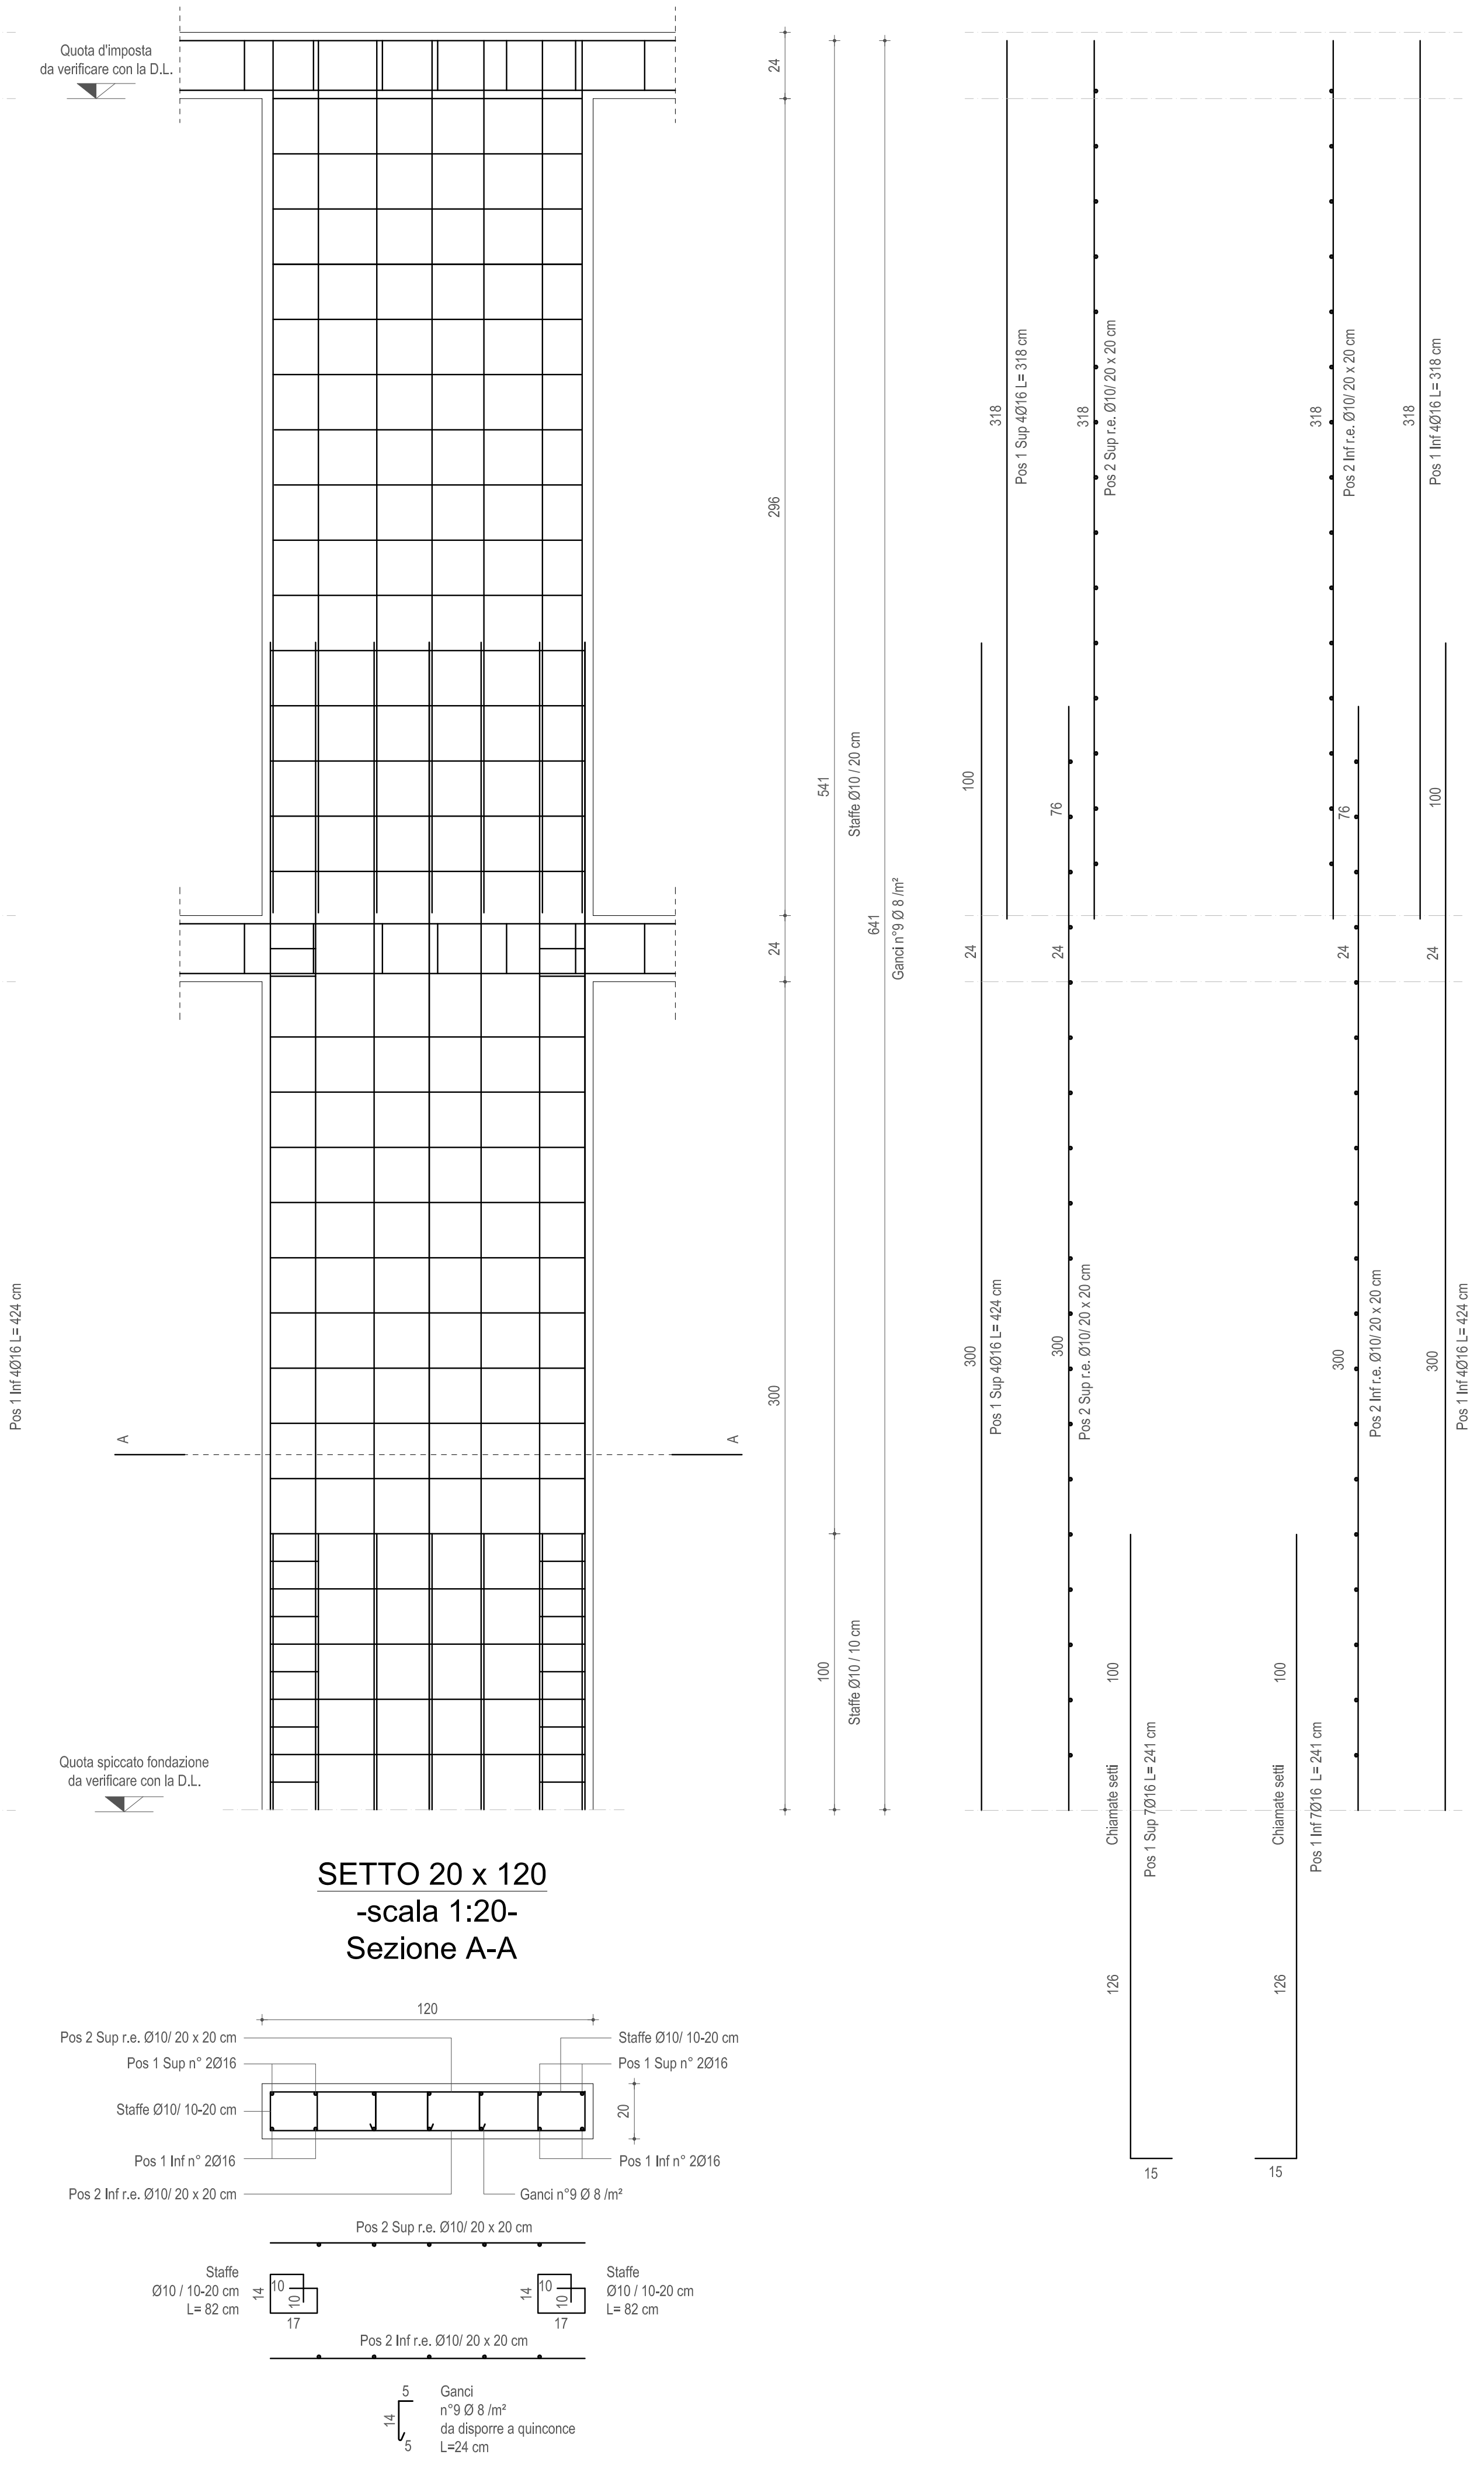

SETTO 20 x 120
-scala 1:20-
Sezione A-A

SETTO 20 x 100
-scala 1:20-

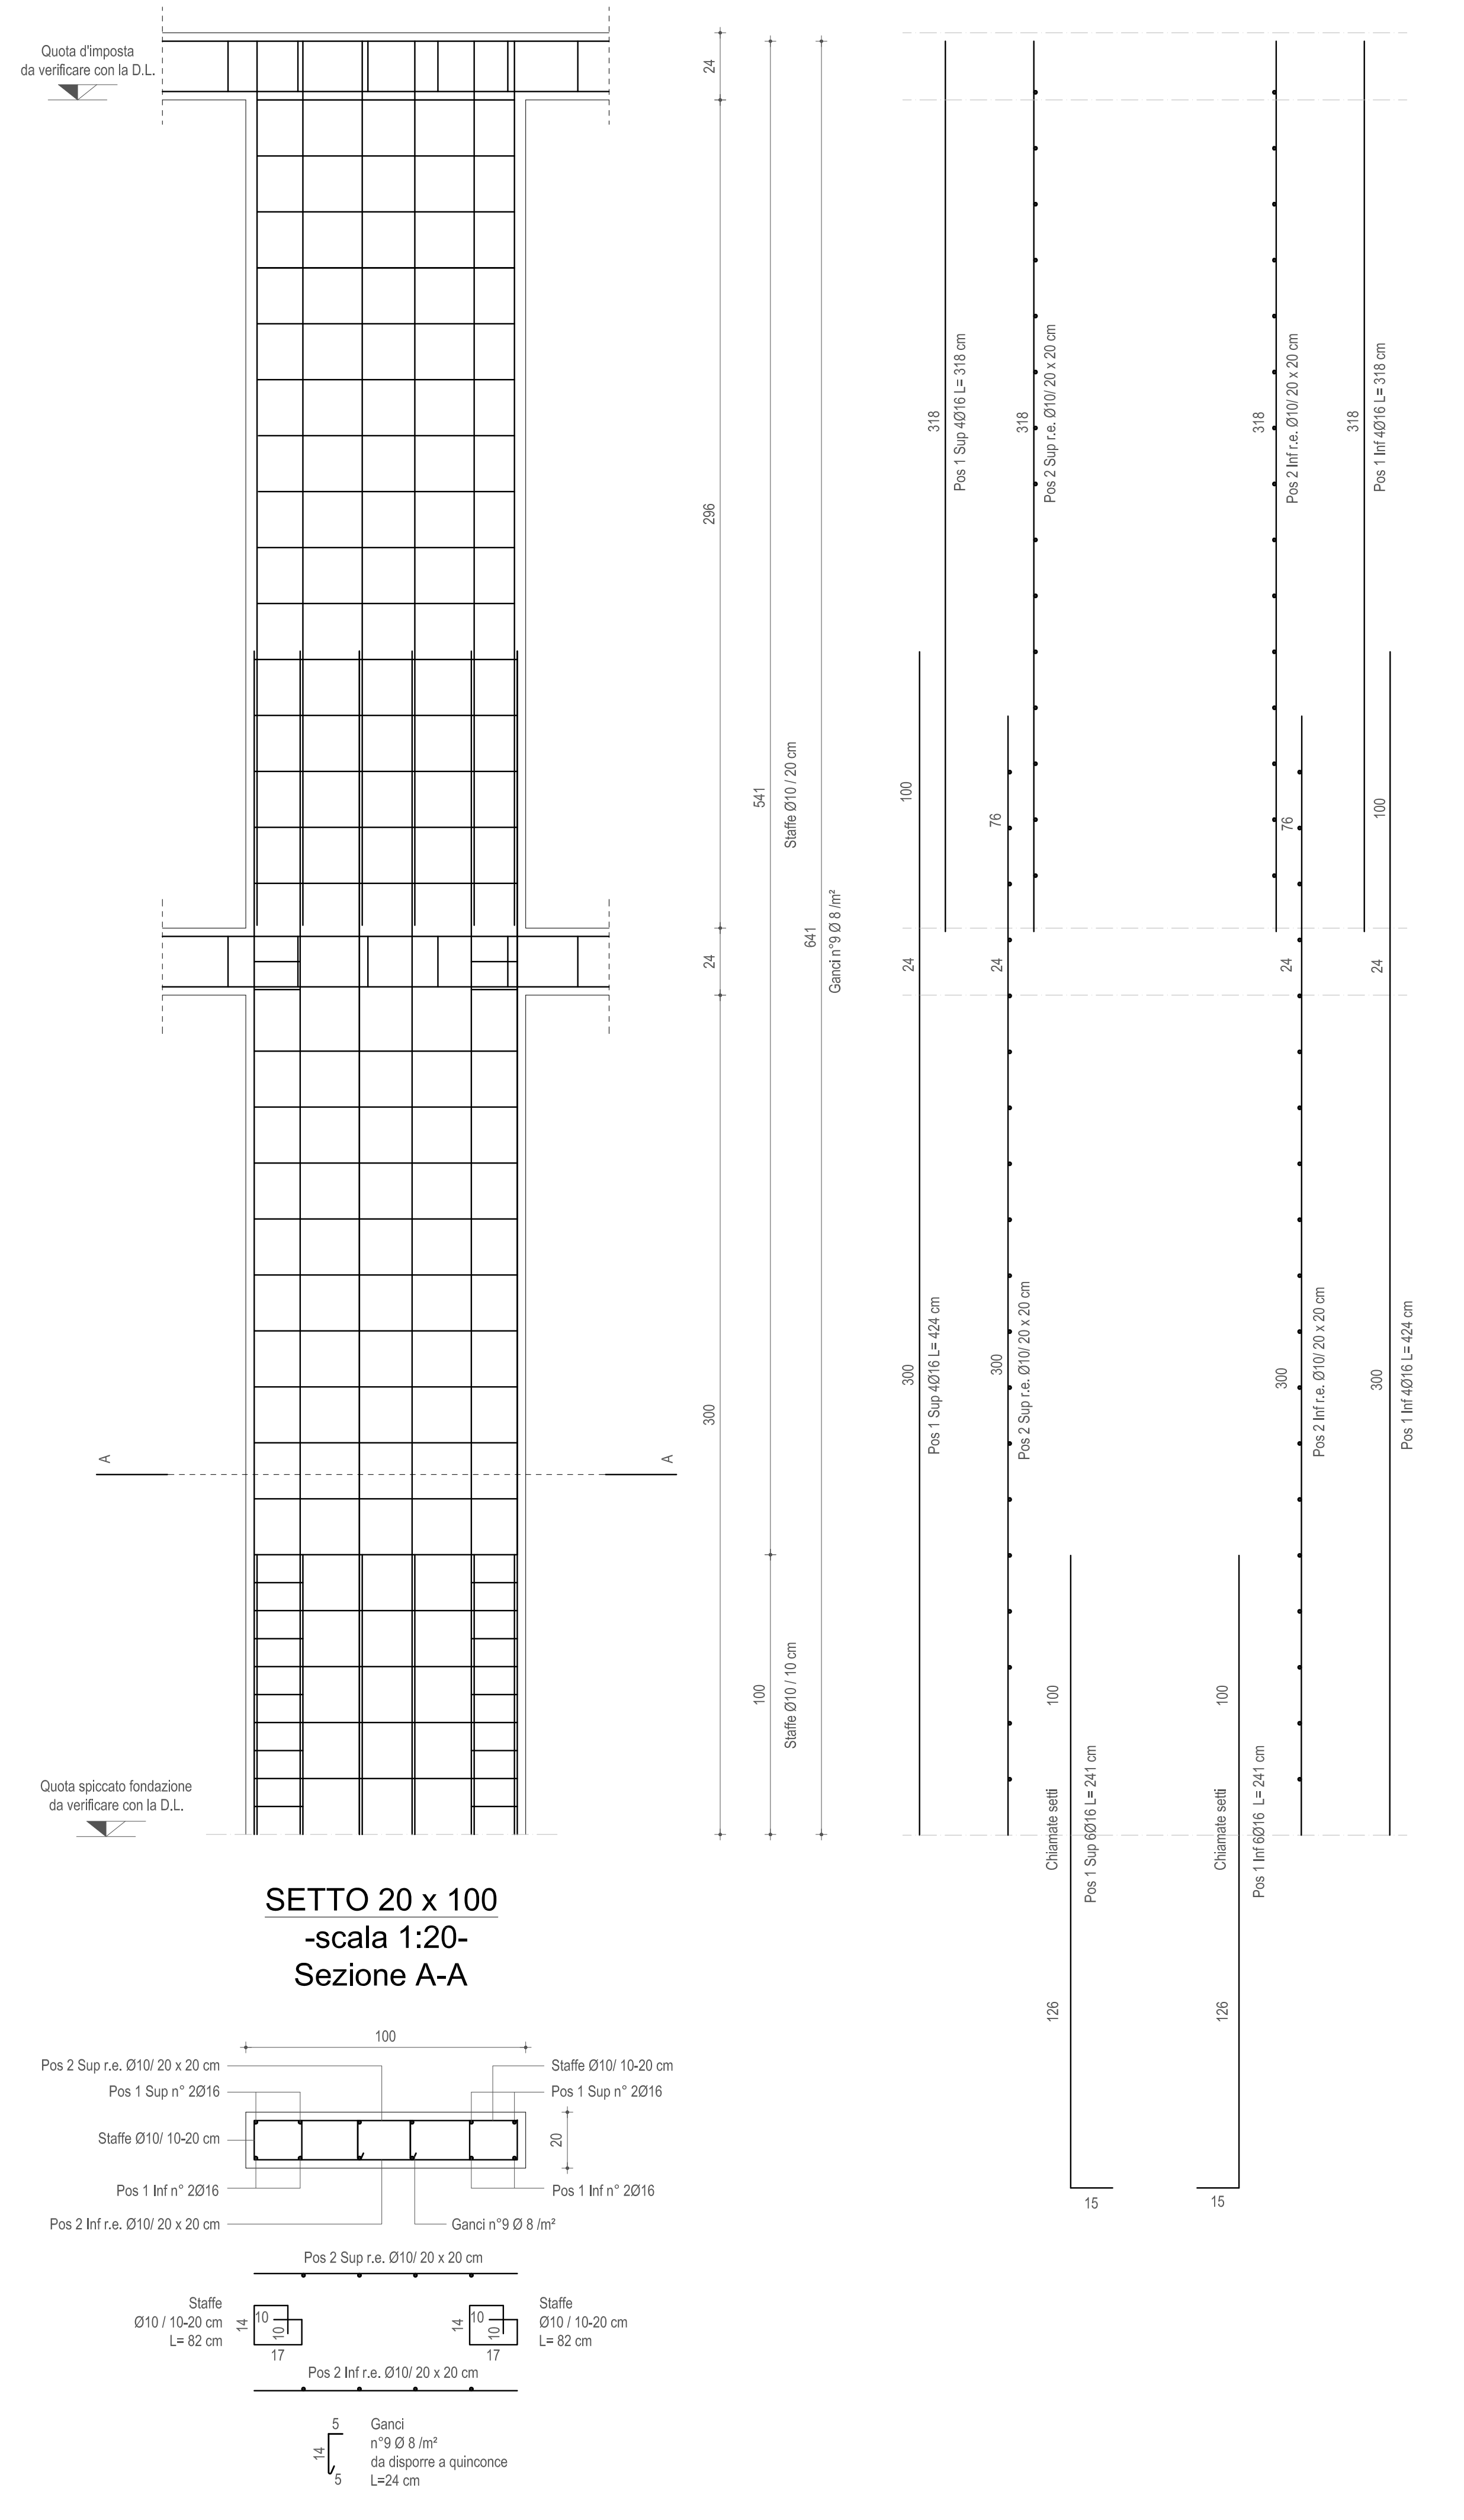

SETTO 20 x 100
-scala 1:20-
Sezione A-A

PILASTRO TIPO
-scala 1:20-

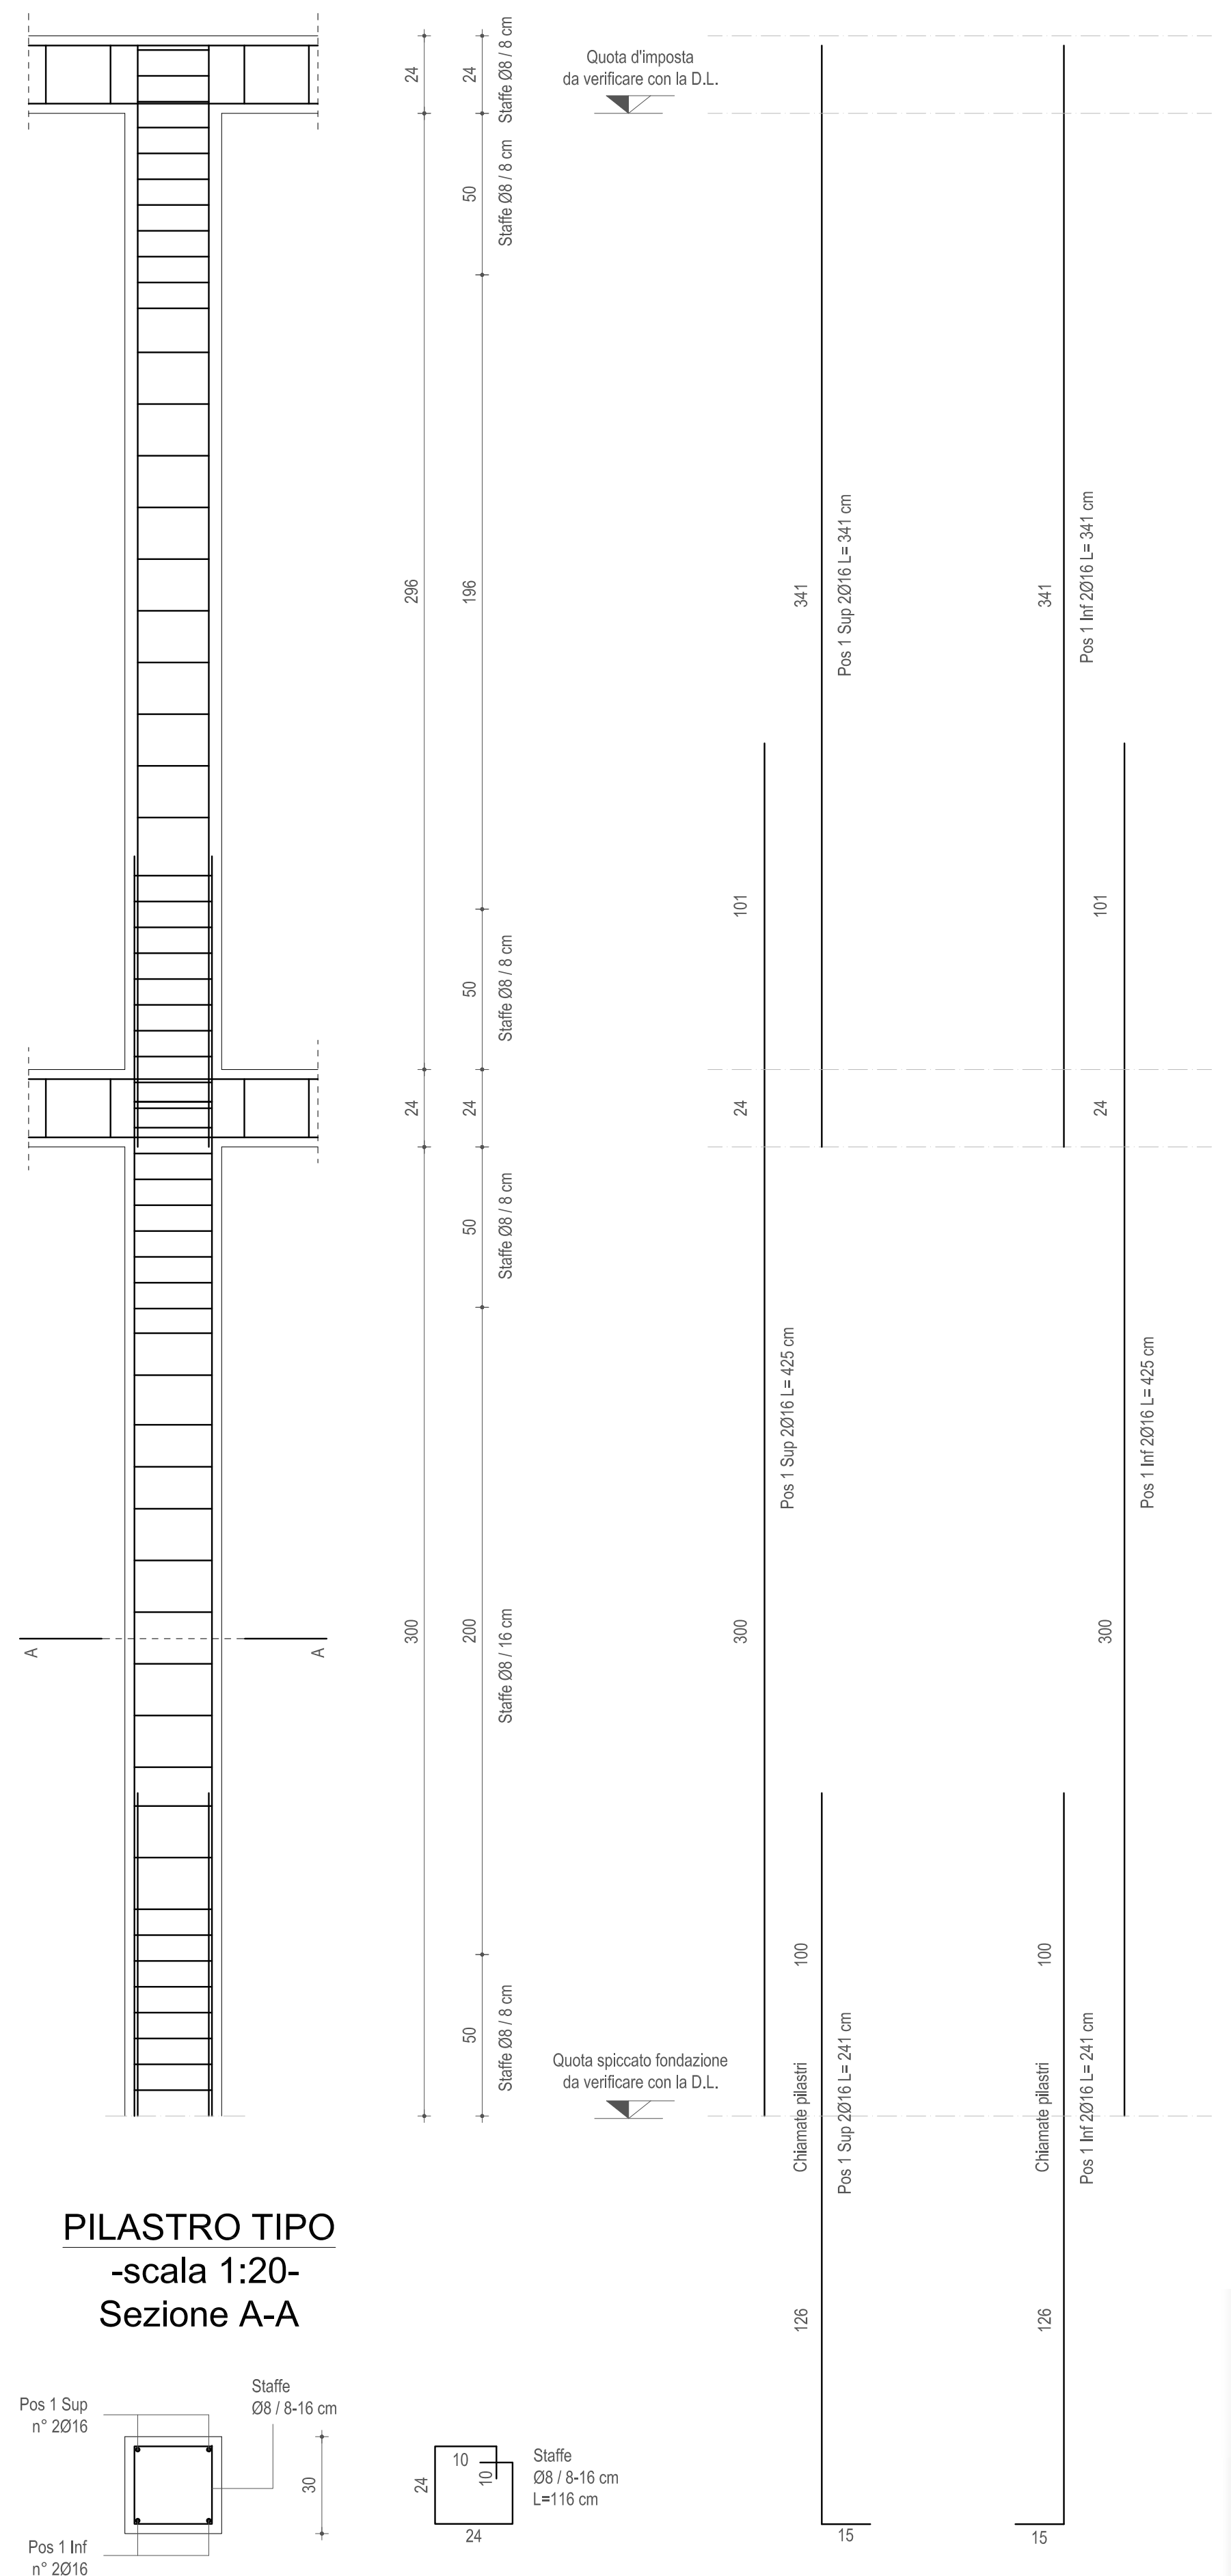

PILASTRO TIPO
-scala 1:20-
Sezione A-A

MATERIALI E PRESCRIZIONI

MATERIALI PRESCRITTI:

- Calcestruzzo per opere di: Fondazioni

  - Classe di resistenza : C25/30 (Rck 30)
  - Condizioni ambientali: Strutture completamente interrate in terreno permeabile
  - Classe di esposizione : XC2
  - Rapporto massimo acqua/cemento: 0,60
  - Classe di consistenza: S3 (Plastica)
  - Diametro massimo degli aggregati: 16 mm

- Calcestruzzo per opere di: Elevazione e Solai misti laterizio-c.a.
  - Classe di resistenza : C25/30 (Rck 30)
  - Condizioni ambientali: Strutture interne di edifici non industriali con umidità bassa
  - Classe di esposizione : XC1
  - Rapporto massimo acqua/cemento: 0,60
  - Classe di consistenza: S3 (Plastica)
  - Diametro massimo degli aggregati: 16 mm

- Calcestruzzo per opere di: Solette piene in C.A.

  - Classe di resistenza : C25/30 (Rck 30)
  - Condizioni ambientali: Strutture interne di edifici non industriali con umidità bassa
  - Classe di esposizione : XC1
  - Rapporto massimo acqua/cemento: 0,60
  - Classe di consistenza: S3 (Plastica)
  - Diametro massimo degli aggregati: 16 mm

- Acciaio per tutte le strutture: B450 C controllato

PRESCRIZIONE

Tutte le misure dovranno essere controllate in cantiere confrontandole con quelle del progetto architettonico e confermate dalla direzione lavori

COMUNE DI RODIGO PROVINCIA DI MANTOVA

[redacted]

- Disegni esecutivi:
  Setti
  Pilastri

Denuncia C.A.

Tav. n° 3	Variante
Data	Scale 1:100, 1:20

[redacted]