MATERIALI E PRESCRIZIONI

MATERIALI PRESCRITTI:

- Calcestruzzo per opere di: Fondazioni

  - Classe di resistenza : C25/30 (Rck 30)
  - Condizioni ambientali: Strutture completamente interrate in terreno permeabile
  - Classe di esposizione : XC2
  - Rapporto massimo acqua/cemento: 0,60
  - Classe di consistenza: S3 (Plastica)
  - Diametro massimo degli aggregati: 16 mm

- Calcestruzzo per opere di: Elevazione Travi e Solai misti laterizio-c.a.
  - Classe di resistenza : C25/30 (Rck 30)
  - Condizioni ambientali: Strutture interne di edifici non industriali con umidità bassa
  - Classe di esposizione : XC1
  - Rapporto massimo acqua/cemento: 0,60
  - Classe di consistenza: S3 (Plastica)
  - Diametro massimo degli aggregati: 16 mm

- Calcestruzzo per opere di: Solette piene in C.A.

  - Classe di resistenza : C25/30 (Rck 30)
  - Condizioni ambientali: Strutture interne di edifici non industriali con umidità bassa
  - Classe di esposizione : XC1
  - Rapporto massimo acqua/cemento: 0,60
  - Classe di consistenza: S3 (Plastica)
  - Diametro massimo degli aggregati: 16 mm

- Acciaio per tutte le strutture: B450 C controllato

- Blocchi semipieni in laterizio per muratura armata con $f_{bk} > 8$ N/mm² e $\bar{f}_{bk} > 1,5$ N/mm²

- Malta per allettamento di classe >M5 ($f_m > 5$ N/mm²)

PRESCRIZIONE

- Prevedere giunti di allettamento verticali ed orizzontali pieni e di spessore non inferiore a 1 cm

-Tutte le misure dovranno essere controllate in cantiere confrontandole con quelle del progetto architettonico e confermate dalla direzione lavori

COMUNE DI MARMIROLO — PROVINCIA DI MANTOVA

REV.	DESCRIZIONE	REDATO		VERIFICATO	
0	Consegna	Ing. Dario Donelli	05/12/2012		
1	Integrazione	Ing. Dario Donelli	12/12/2012		

Oggetto

[redacted]

Oggetto tavola

- Disegni esecutivi: Fondazioni

Denuncia C.A.

Tav. n° 1


Variante

Data


Scale 1:100, 1:20

Collaboratori


Trave rovescia -TR 02-
Sezione A-A
-scala 1:20-

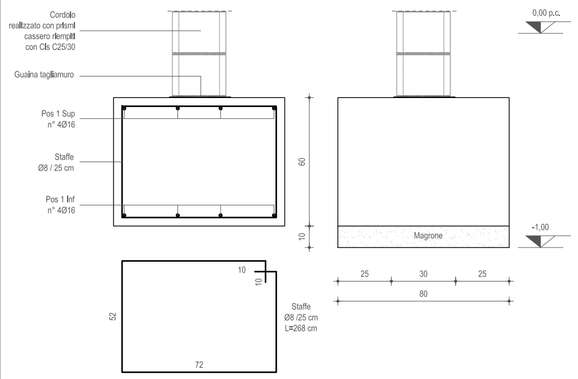


Trave rovescia -TR 02-
-scala 1:20-

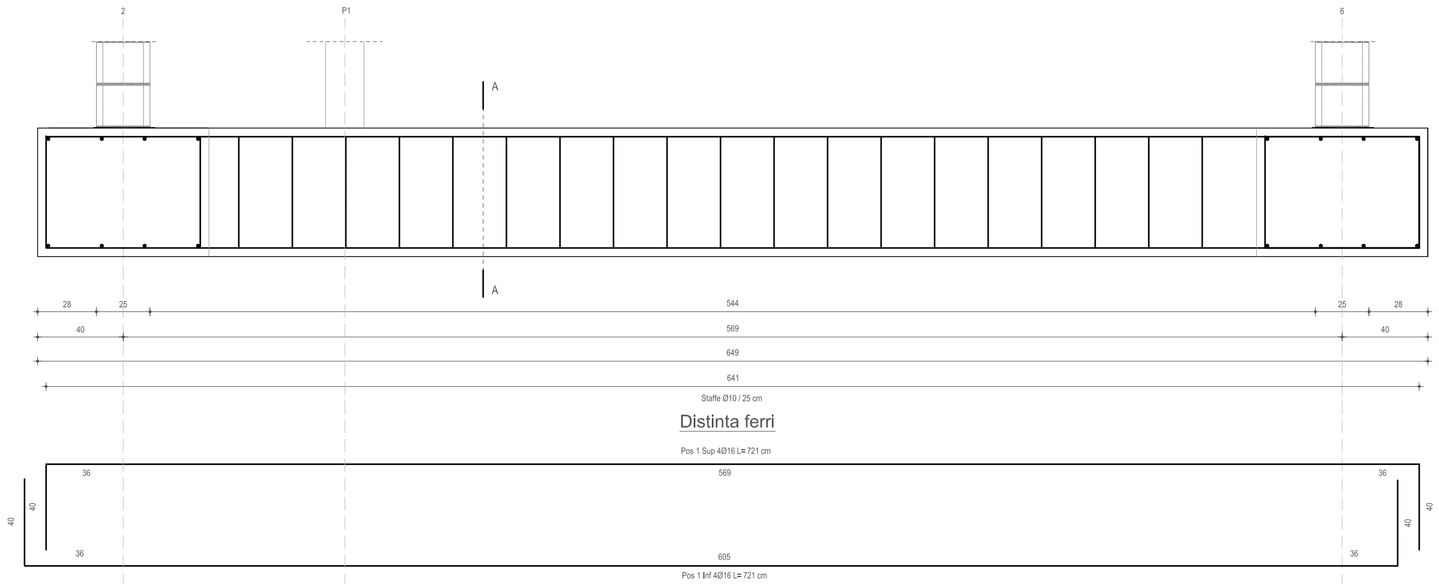


Trave rovescia -TR 01-
Sezione A-A
-scala 1:20-

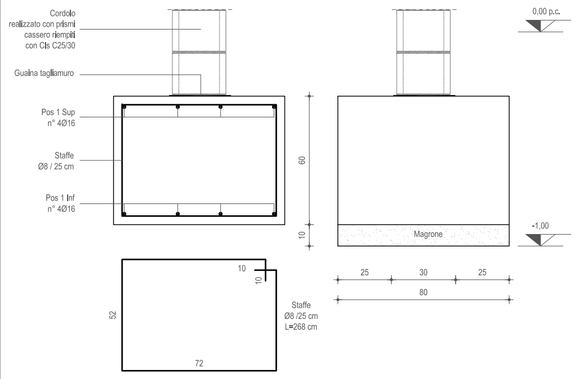


Trave rovescia -TR 01-
-scala 1:20-

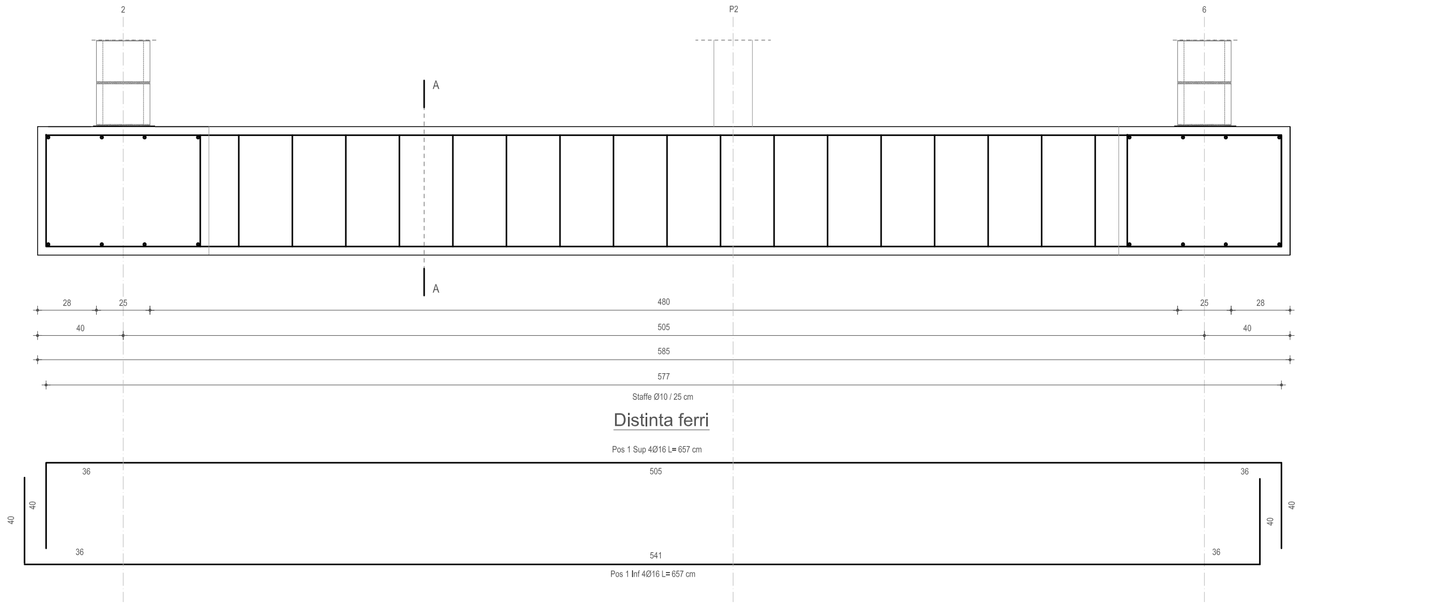


Pianta fondazioni -scala 1:100-

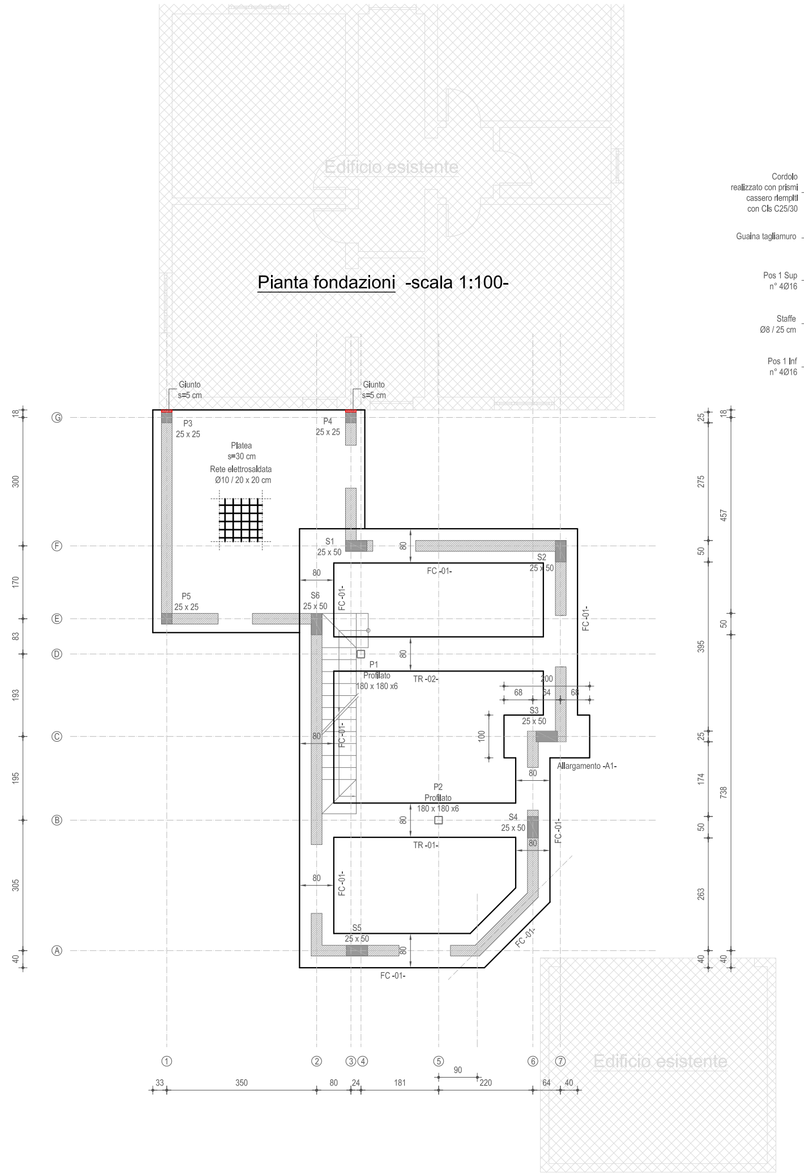


Fondazione continua -Tipo 1-
FC-T1-
-scala 1:20-

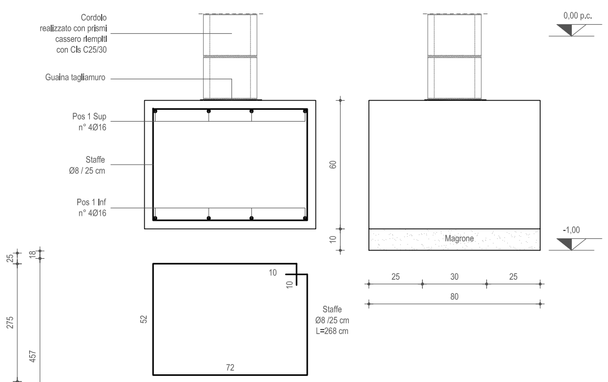

Allargamento -A1-
-scala 1:20-

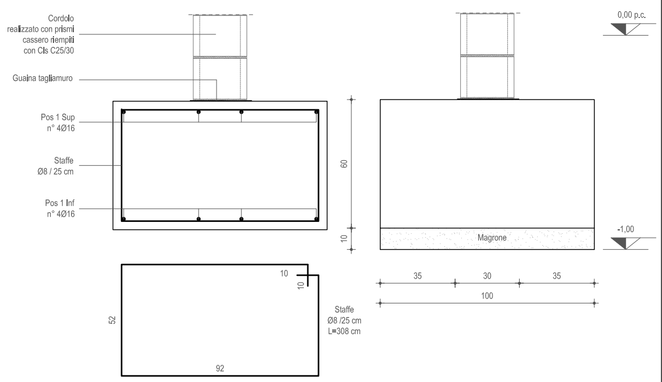

Particolare chiamate pilastri
25 x 50
-scala 1:20-

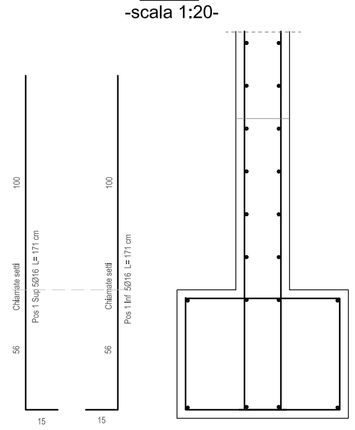

Particolare chiamate pilastri
25 x 25
-scala 1:20-

