MATERIALI E PRESCRIZIONI

MATERIALI PRESCRITTI:

- Calcestruzzo per opere di: Fondazioni

  - Classe di resistenza : C25/30 (Rck 30)
  - Condizioni ambientali: Strutture completamente interrate in terreno permeabile
  - Classe di esposizione : XC2
  - Rapporto massimo acqua/cemento: 0,60
  - Classe di consistenza: S3 (Plastica)
  - Diametro massimo degli aggregati: 16 mm

- Calcestruzzo per opere di: Elevazione Travi e Solai misti legno-c.a.
  - Classe di resistenza : C25/30 (Rck 30)
  - Condizioni ambientali: Strutture interne di edifici non industriali con umidità bassa
  - Classe di esposizione : XC1
  - Rapporto massimo acqua/cemento: 0,60
  - Classe di consistenza: S3 (Plastica)
  - Diametro massimo degli aggregati: 16 mm

- Calcestruzzo per opere di: Solette piene in C.A.

  - Classe di resistenza : C25/30 (Rck 30)
  - Condizioni ambientali: Strutture interne di edifici non industriali con umidità bassa
  - Classe di esposizione : XC1
  - Rapporto massimo acqua/cemento: 0,60
  - Classe di consistenza: S3 (Plastica)
  - Diametro massimo degli aggregati: 16 mm

- Acciaio per tutte le strutture: B450 C controllato

- Blocchi semipieni in laterizio per muratura armata con f_{bk} > 8 N/mm² e $\bar{f}_{bk}$ > 1,5 N/mm²

- Malta per allettamento di classe >M5 (f_m > 5 N/mm²)

PRESCRIZIONE

- Prevedere giunti di allettamento verticali ed orizzontali pieni e di spessore non inferiore a 1 cm

-Tutte le misure dovranno essere controllate in cantiere confrontandole con quelle del progetto architettonico e confermate dalla direzione lavori

COMUNE DI MARMIROLO — PROVINCIA DI MANTOVA

REV.	DESCRIZIONE	REDATO		VERIFICATO	
0	Consegna	Ing. Dario Donelli	05/12/2012		
1	Integrazione	Ing. Dario Donelli	12/12/2012		

Oggetto

Oggetto tavola

- Disegni esecutivi:
  Travi e Solai

Denuncia C.A.

Tav. n° 3


Variante

Data


Scale 1:100, 1:20, 1:10

Collaboratori

Pianta primo impalcato -scala 1:100-

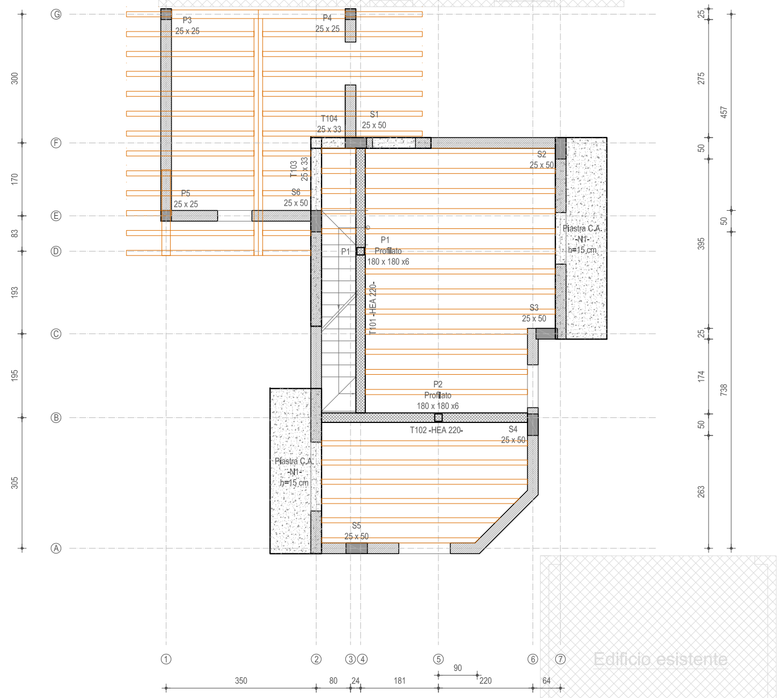


Particolare angolo cordolo
Pianta
-scala 1:20-

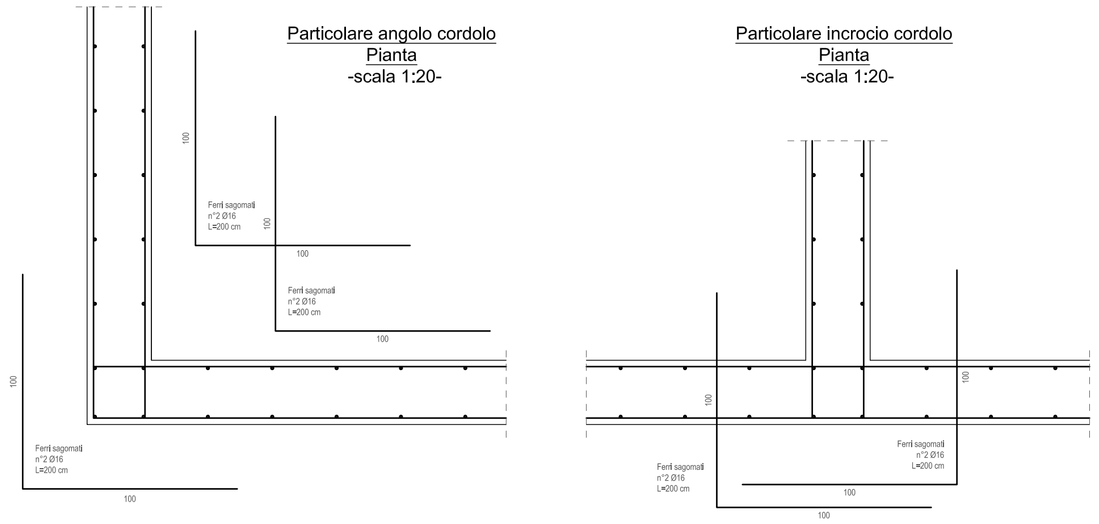


Particolare incrocio cordolo
Pianta
-scala 1:20-


Particolare appoggio
Trave-Cordolo
-scala 1:20-

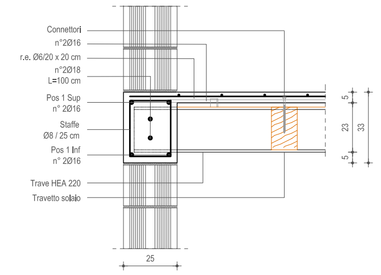


Particolare appoggio
Trave-Pilastro
-scala 1:20-

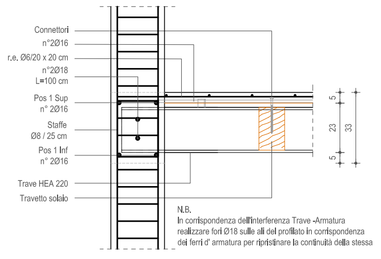

Particolare trave
-scala 1:20-

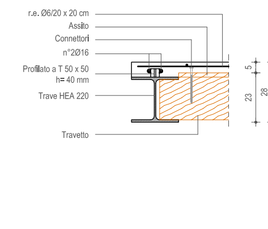


Soletta -N1 -
Sezione trasversale
-scala 1:20-

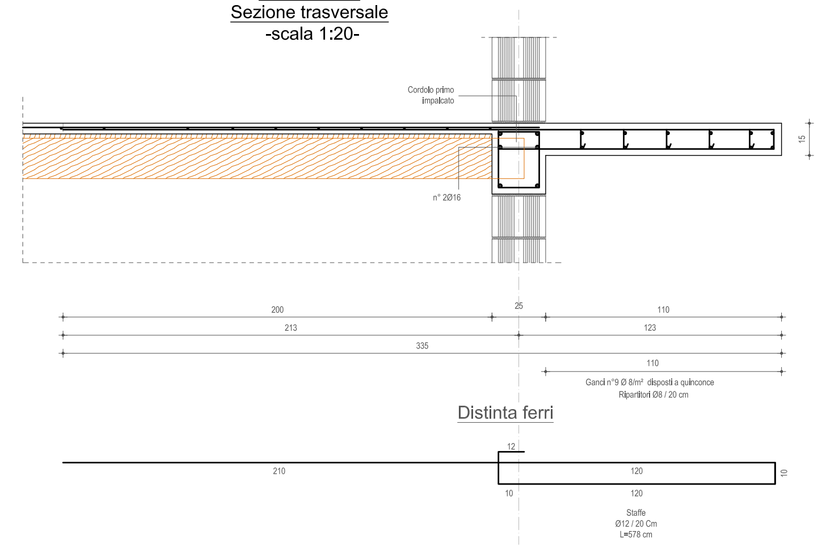


Distinta ferri


Particolare Pilastro Acciaio
Base
-scala 1:10-

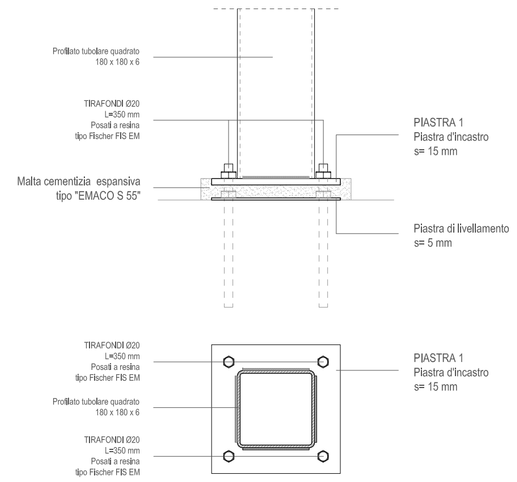


Particolare Pilastro Acciaio
Pilastro - Trave
-scala 1:10-

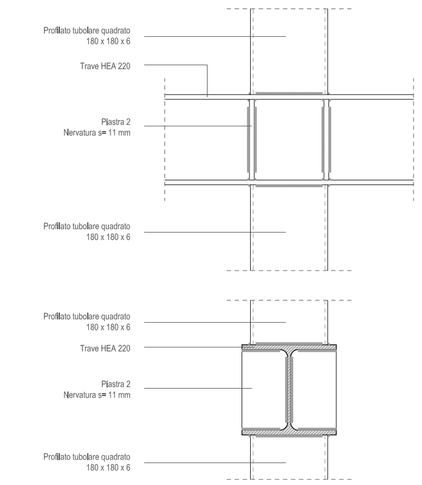


Piastra 1
-scala 1:10-

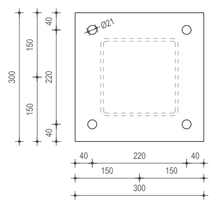


Piastra 2
-scala 1:10-

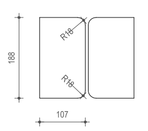


Pianta copertura -scala 1:100-

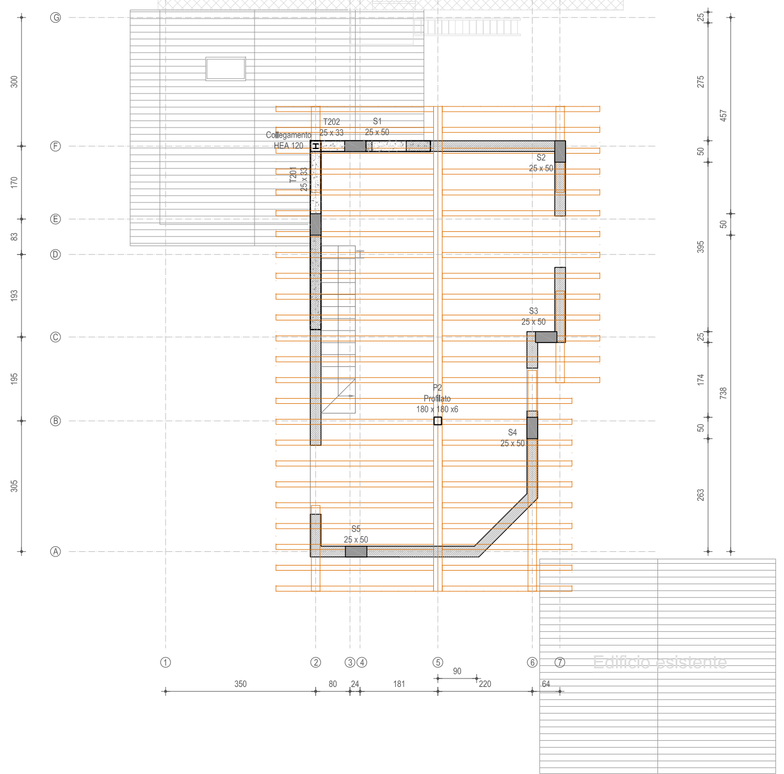

Trave -T103
-scala 1:20-

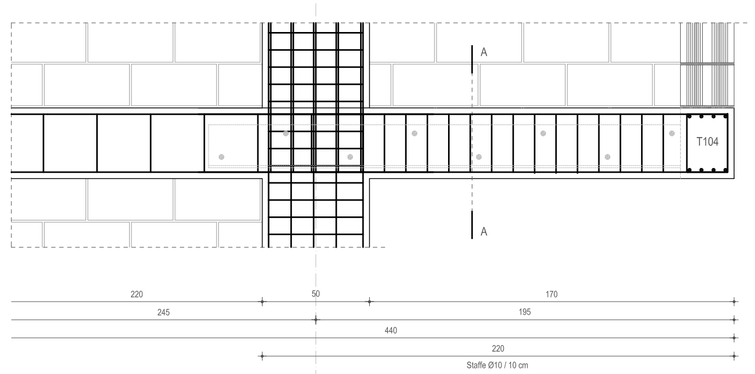


Trave -T103
-scala 1:20-
Sezione A-A

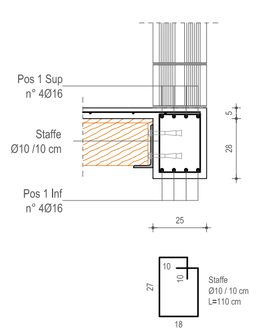


Distinta ferri




Trave -T104
-scala 1:20-

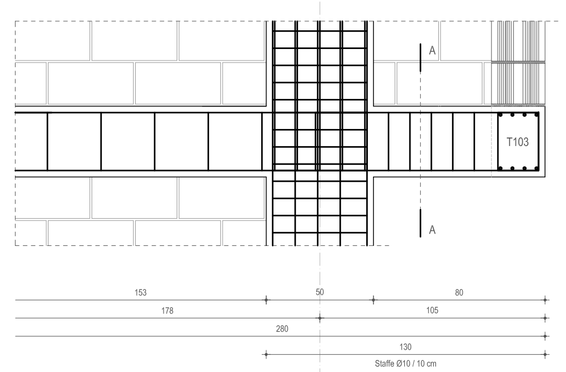


Trave -T104
-scala 1:20-
Sezione A-A

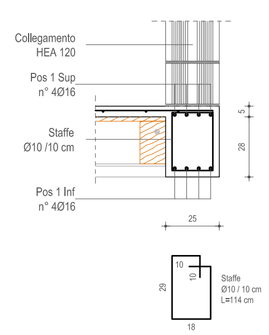


Distinta ferri

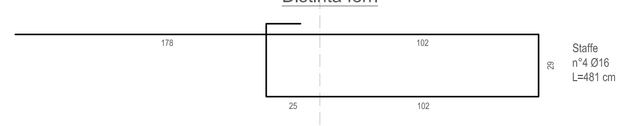


Trave -T201
-scala 1:20-

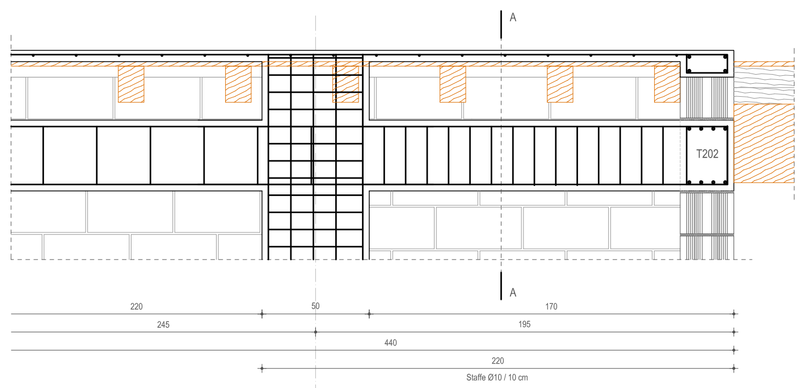


Trave -T201
-scala 1:20-
Sezione A-A

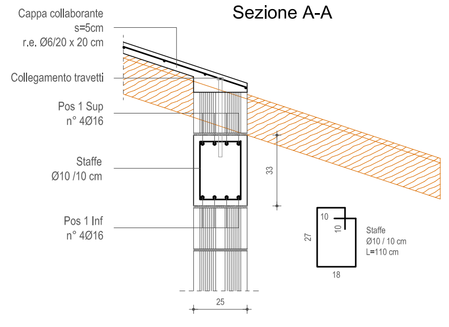


Distinta ferri

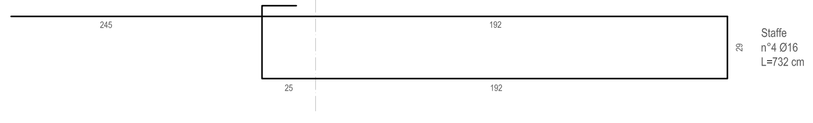

Trave -T202
-scala 1:20-

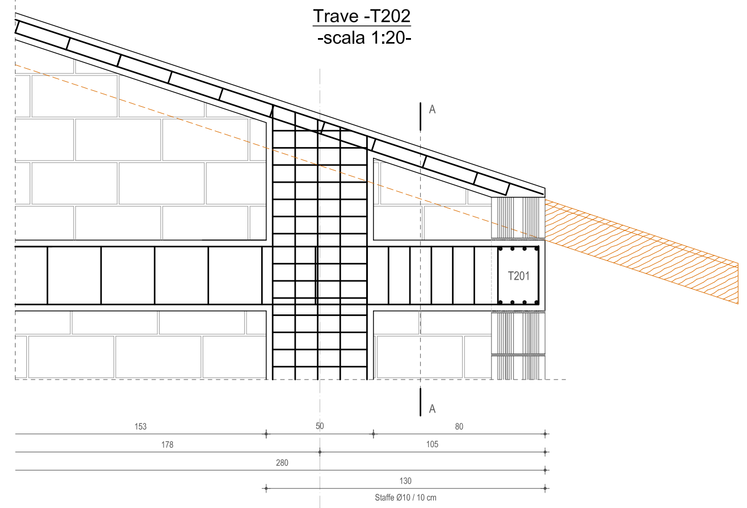

Trave -T202
-scala 1:20-
Sezione A-A

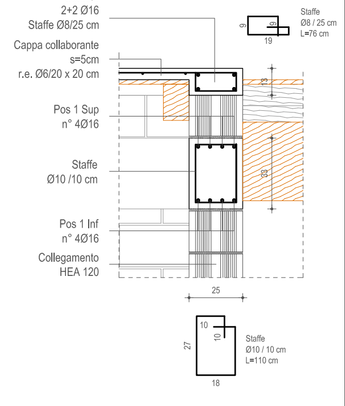

Distinta ferri

