TRAVE ROVESCIA -TR 1-
-scala 1:20-

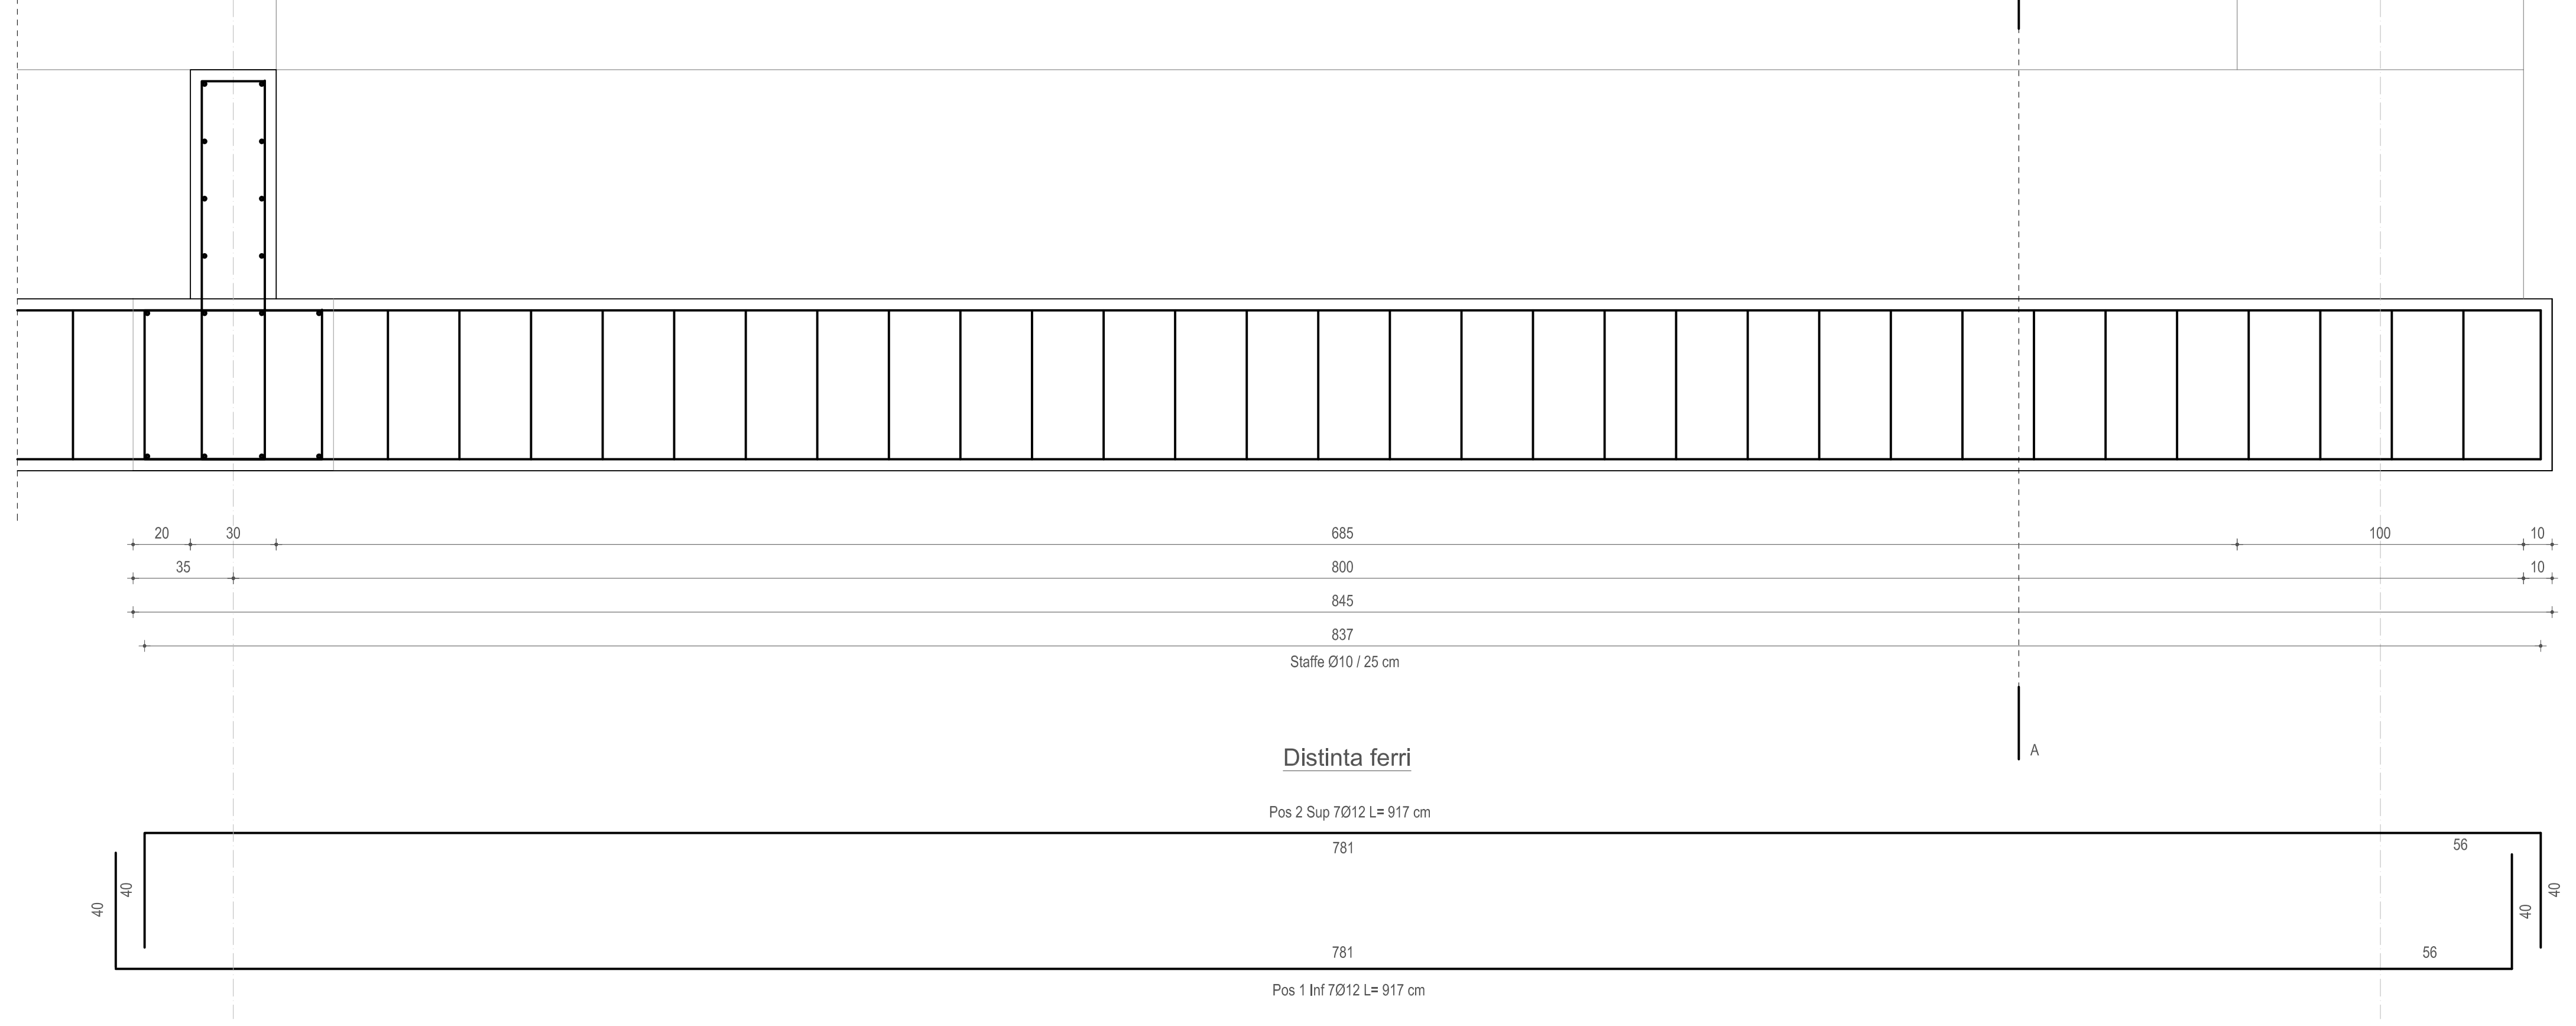

TRAVE ROVESCIA -TR 1-
-scala 1:20-
Sezione A-A

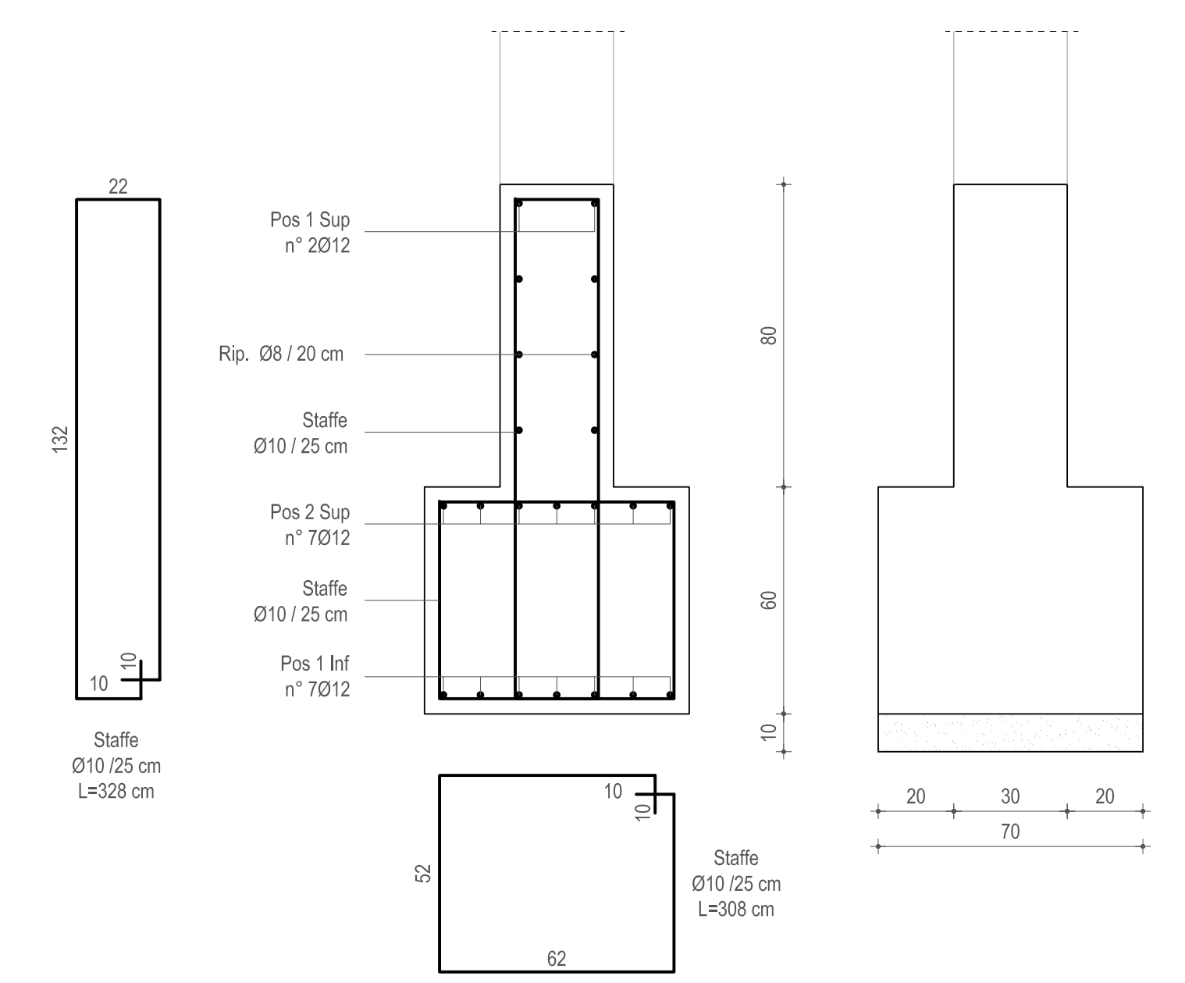

FONDAZIONE CONTINUA -TIPO 1-
FC-T1-
-scala 1:20-

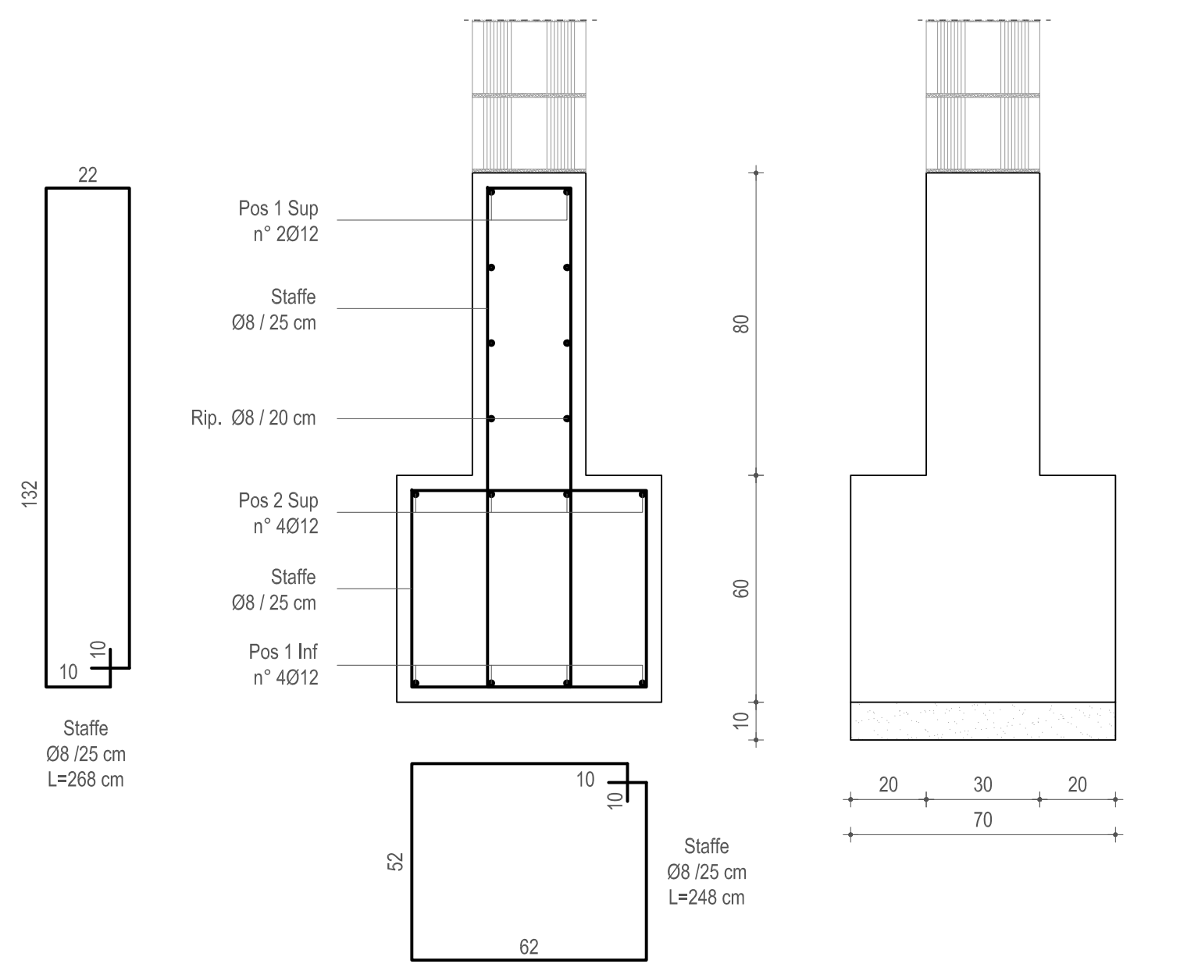

PIANTA FONDAZIONI -scala 1:100-

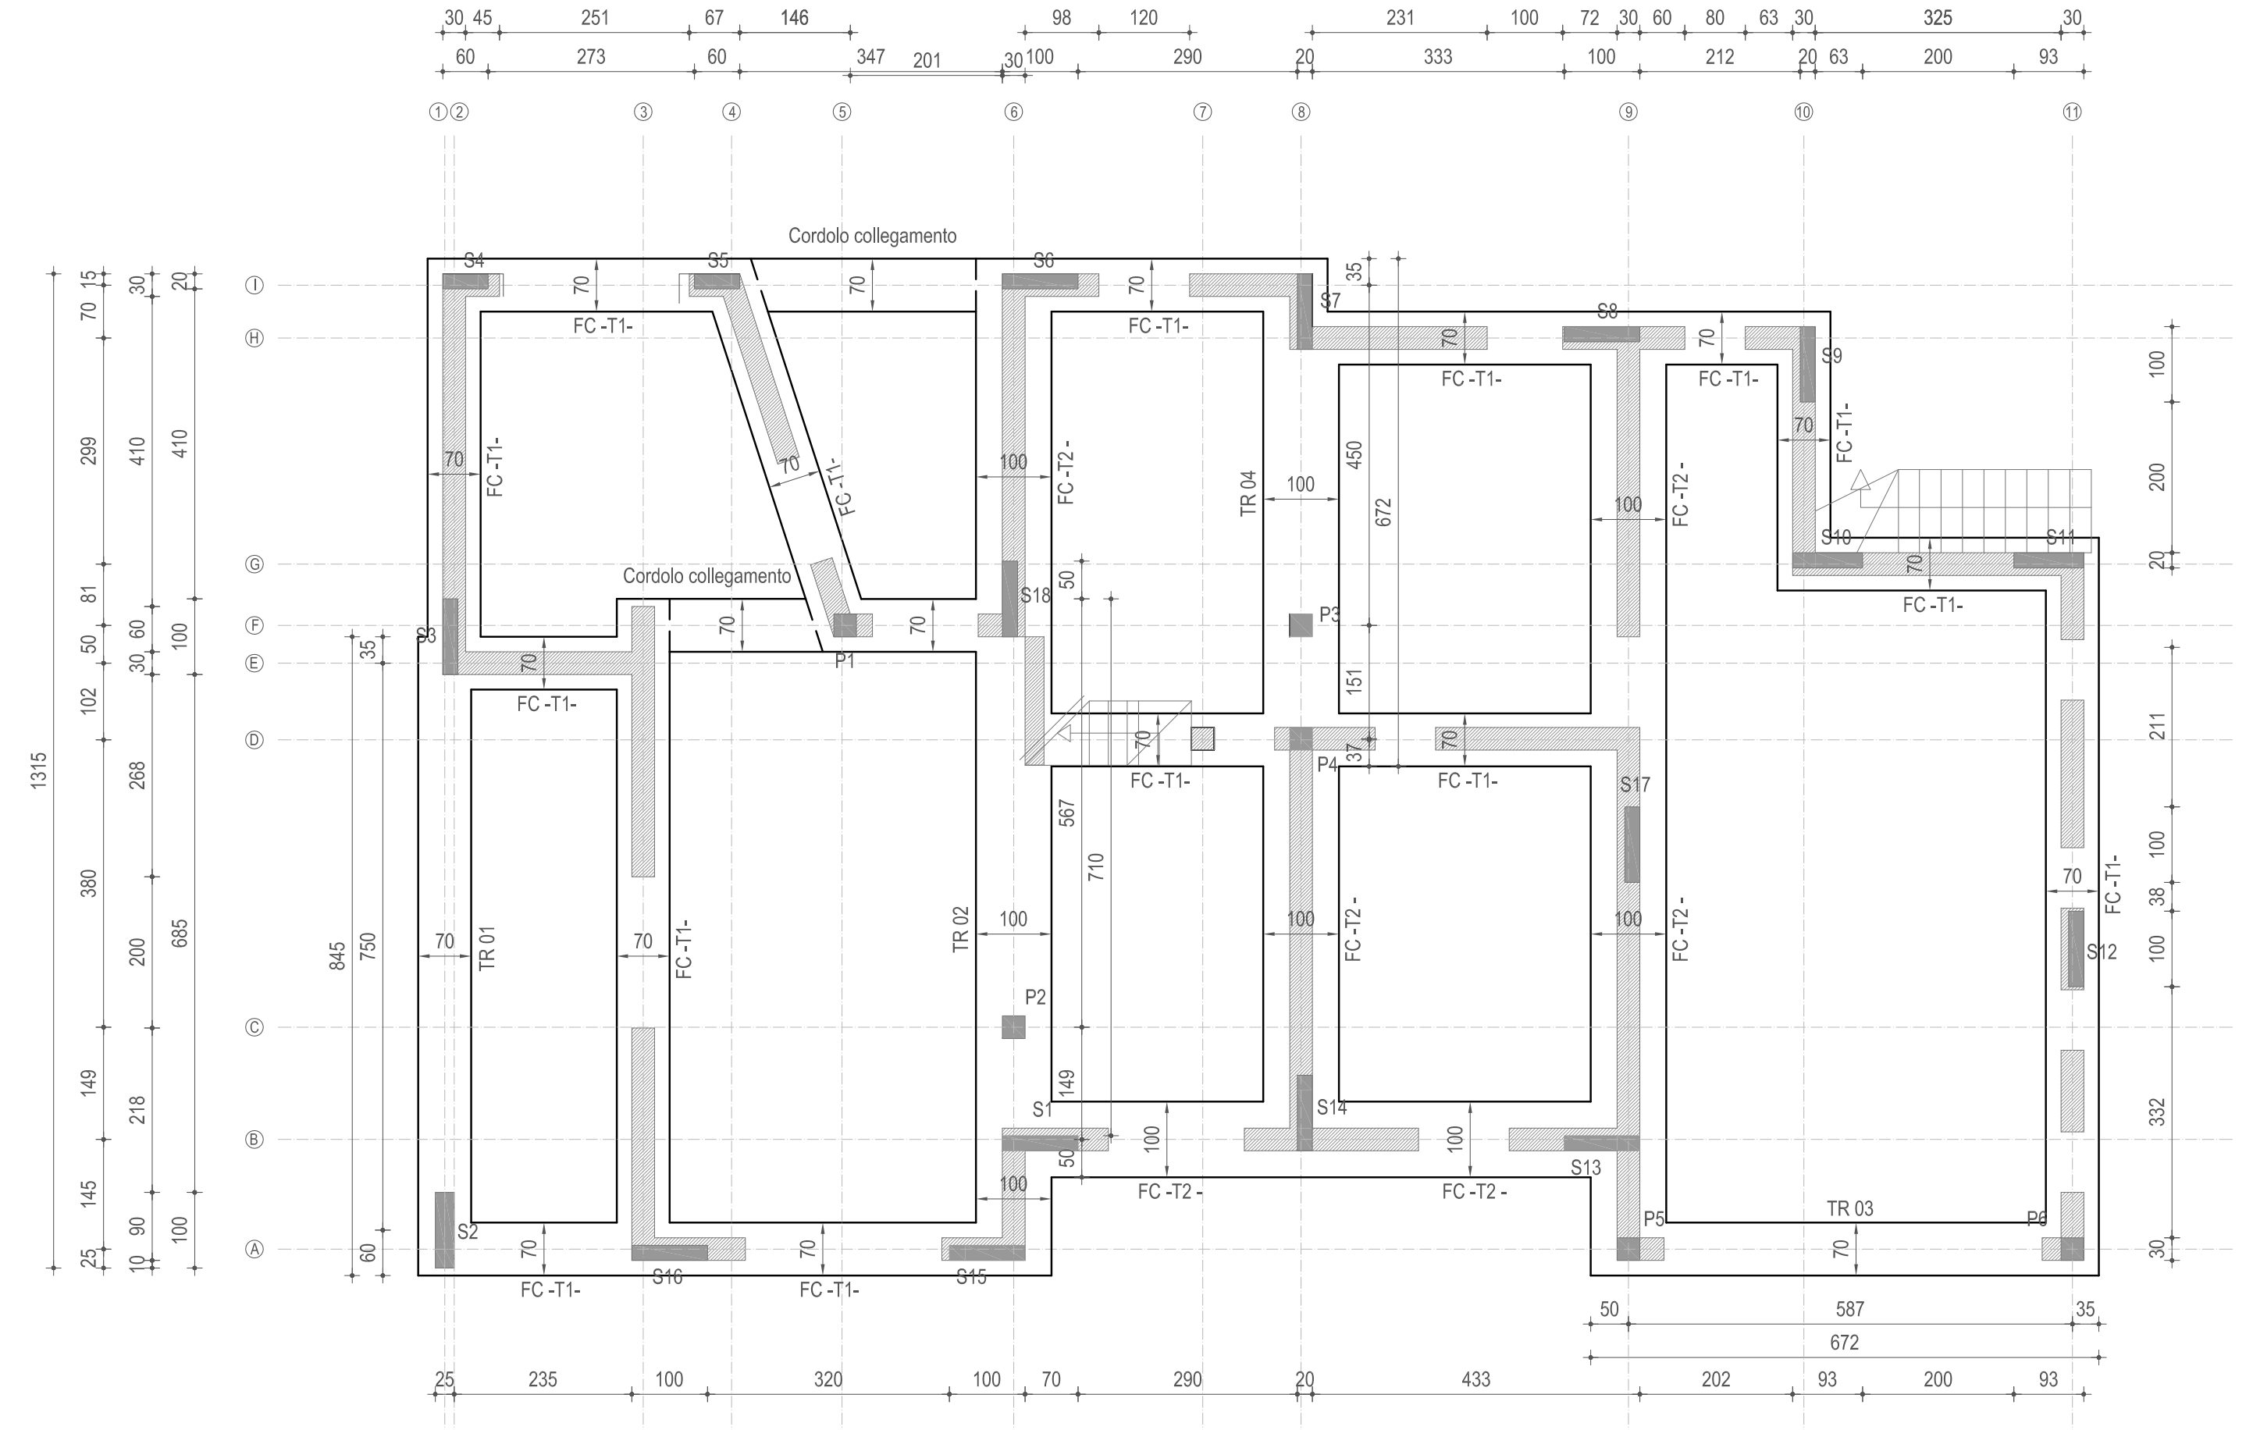

TRAVE ROVESCIA -TR 2-
-scala 1:20-

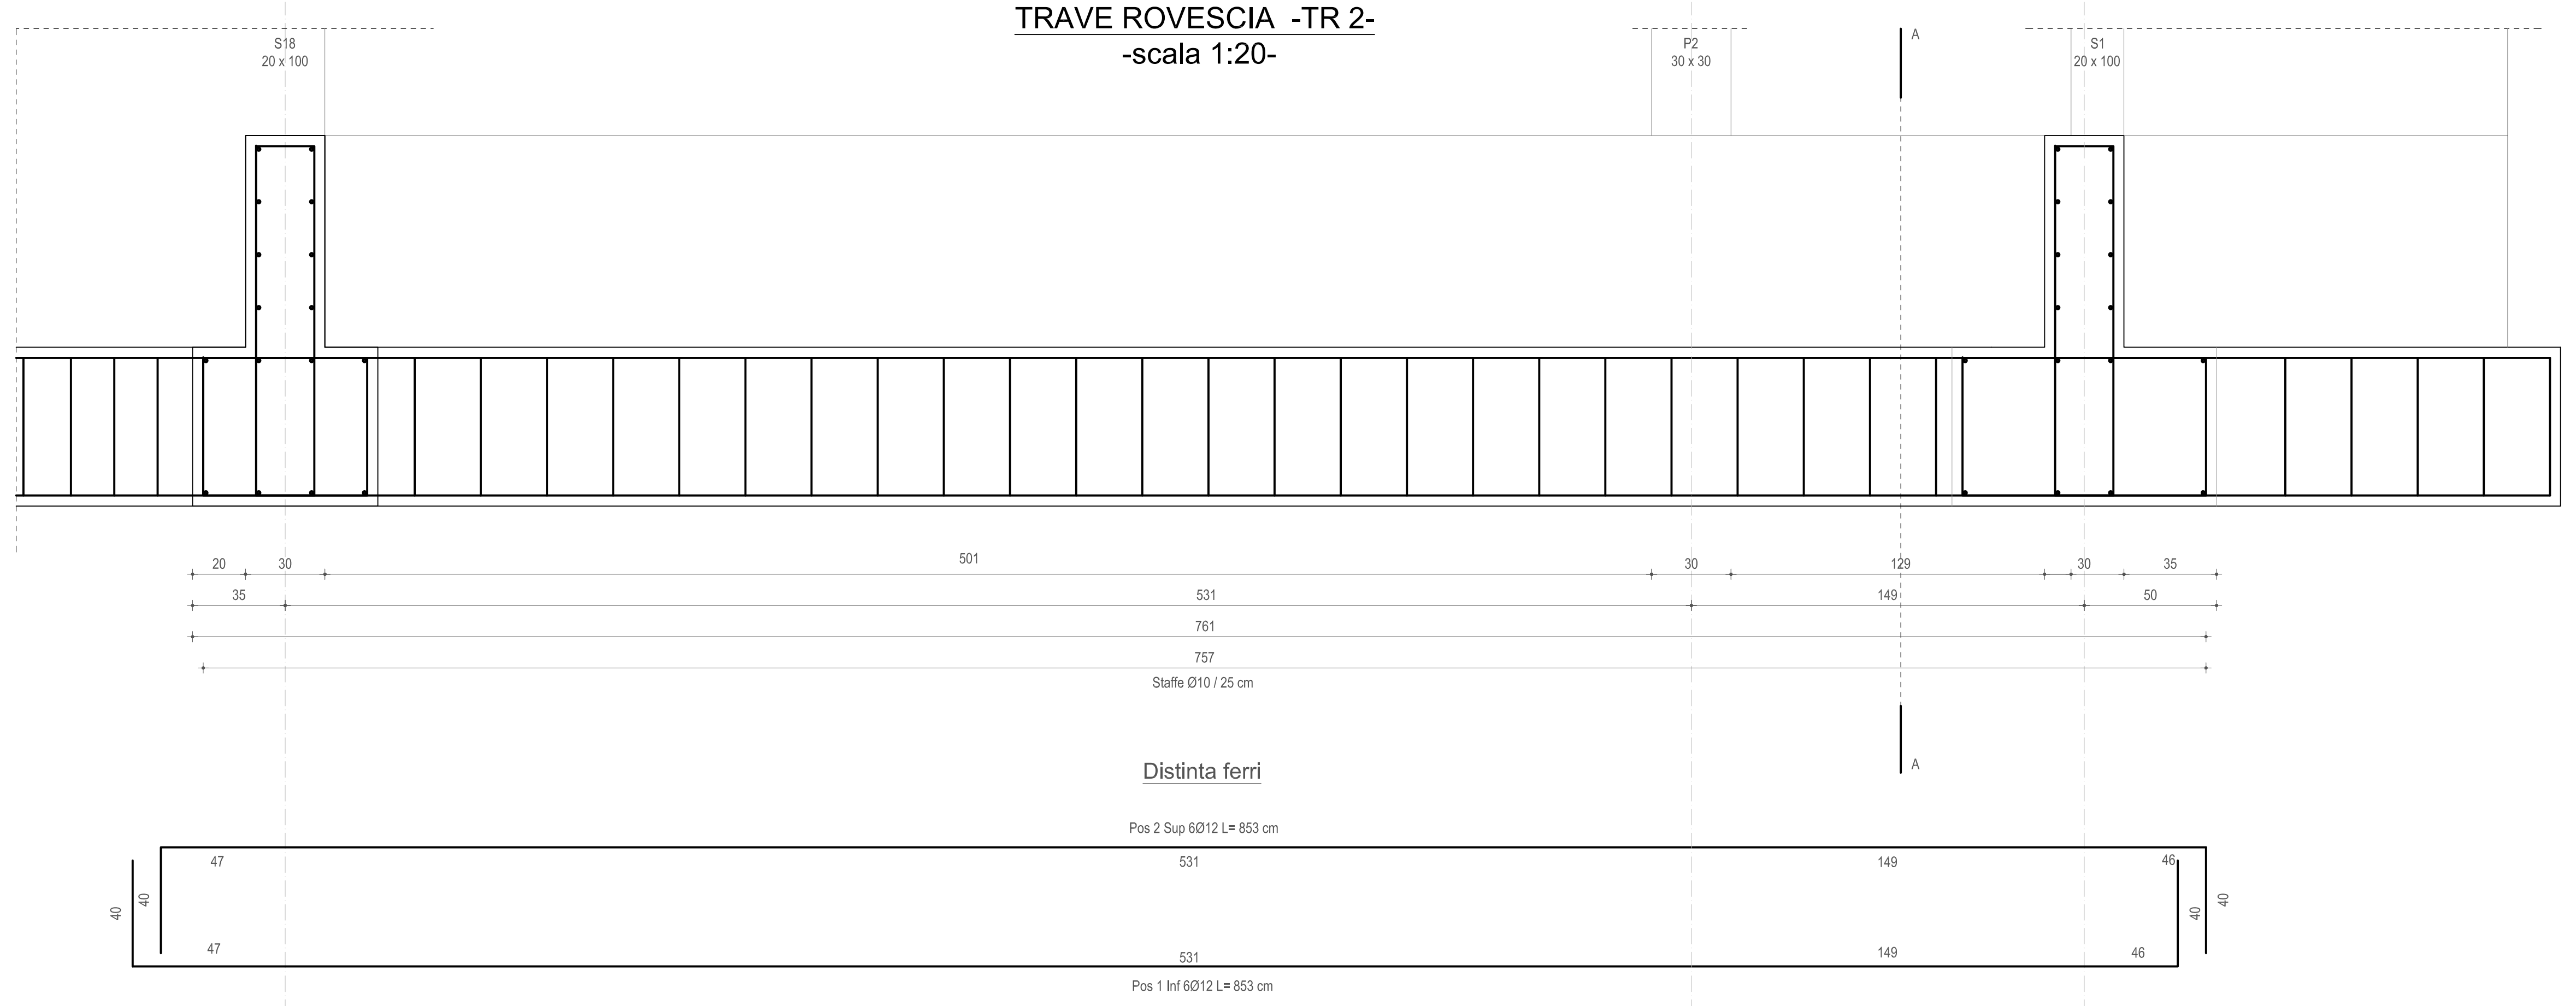

TRAVE ROVESCIA -TR 2-
-scala 1:20-
Sezione A-A

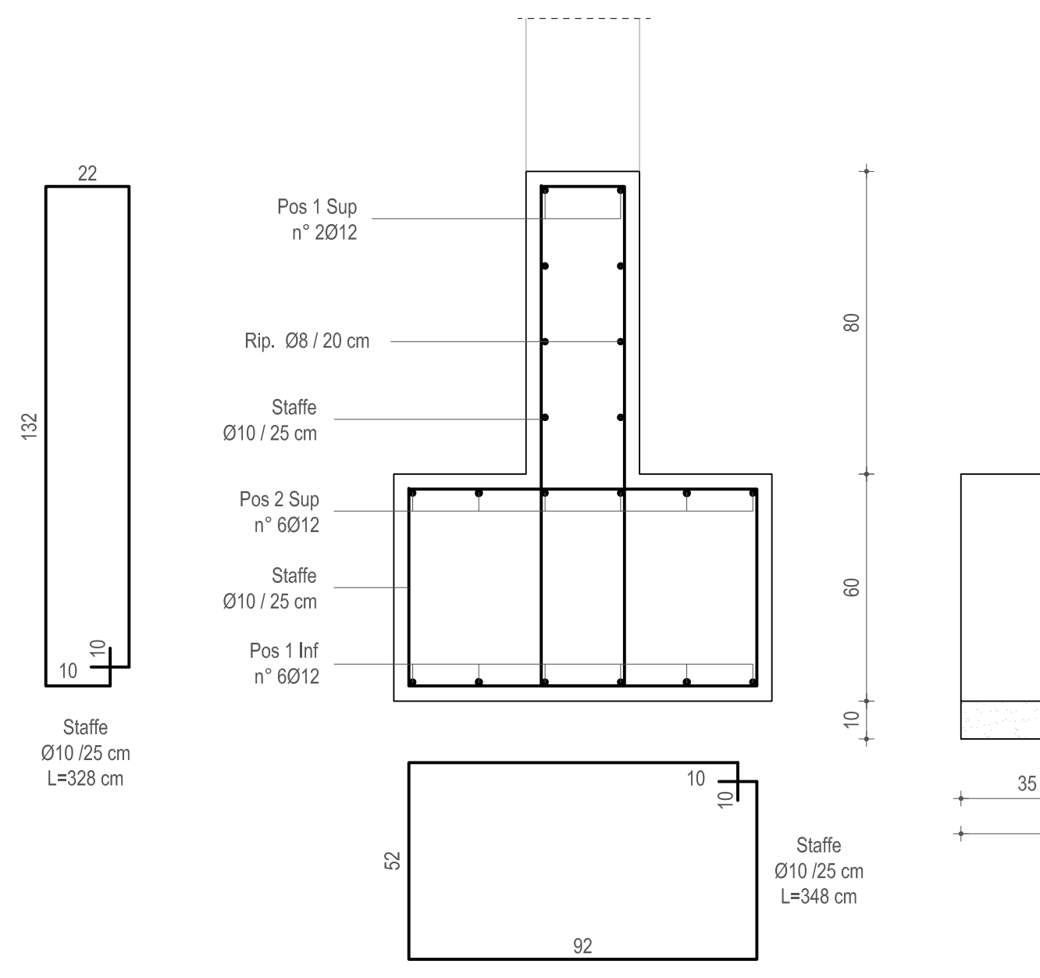

FONDAZIONE CONTINUA -TIPO 2-
FC-T2-
-scala 1:20-

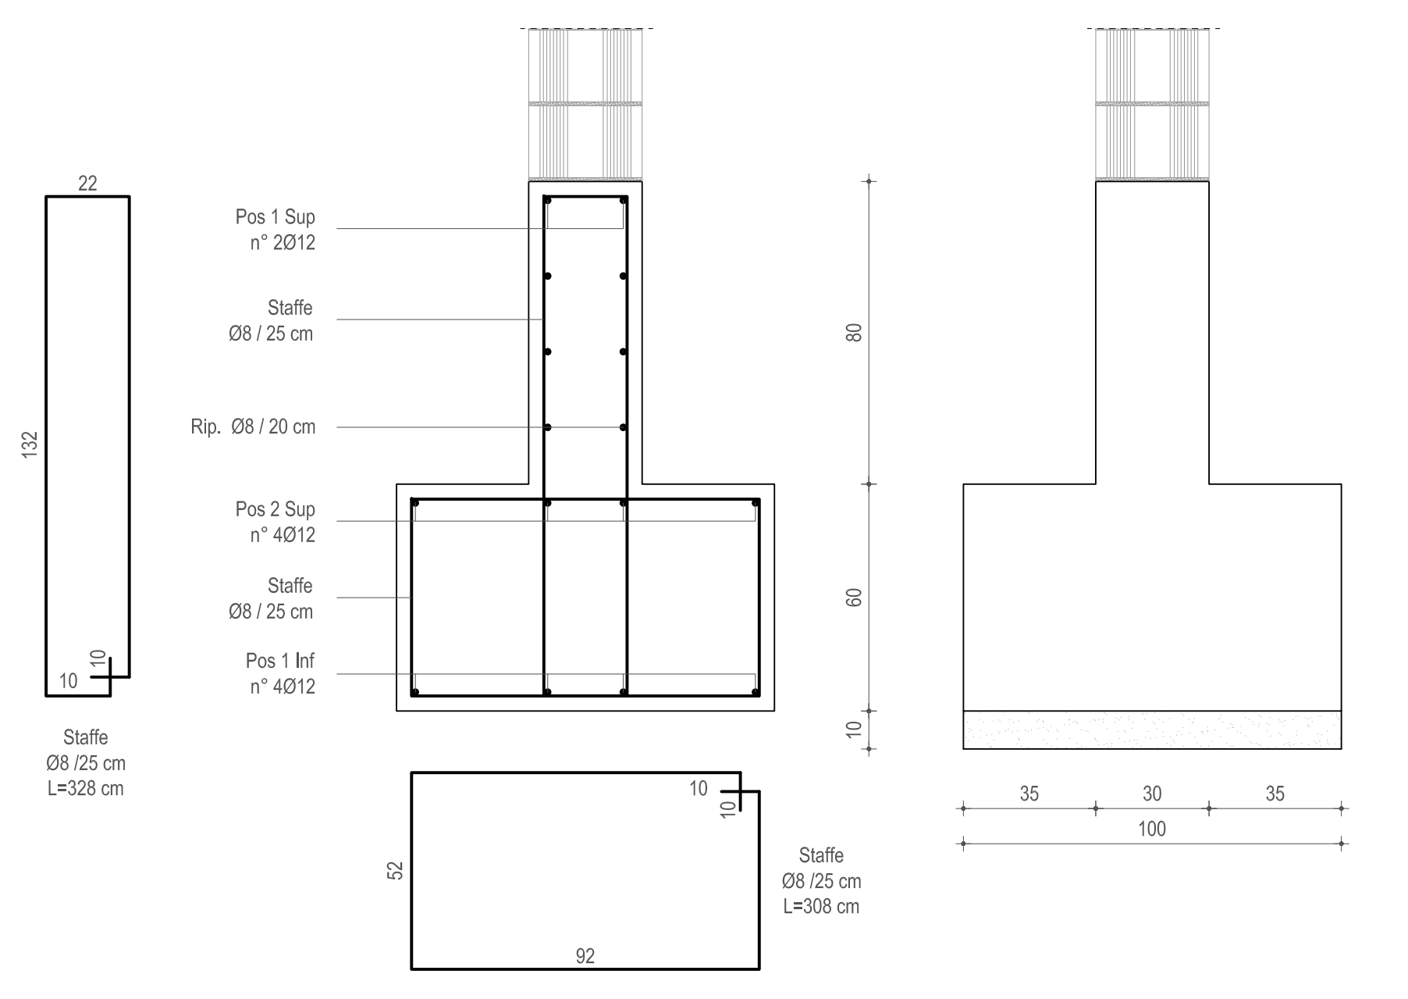

PARTICOLARE CHIAMATE SETTI
s=20 cm
-scala 1:20-

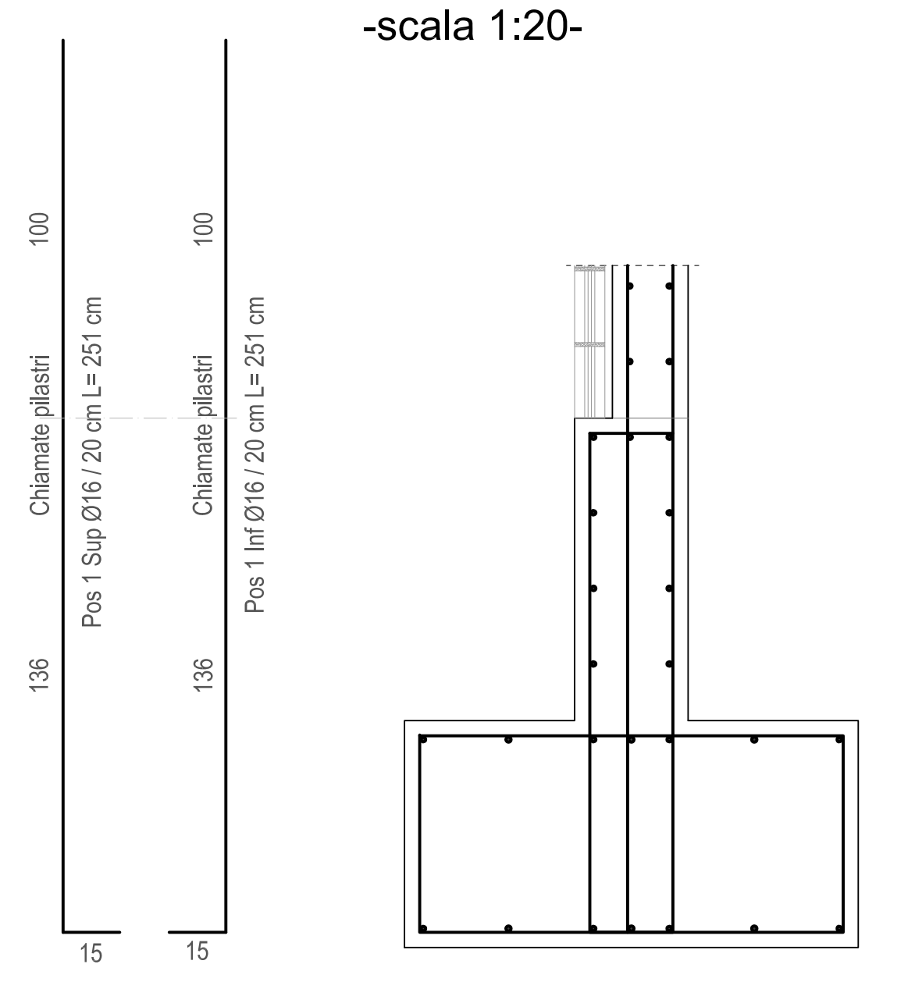
100
Chiamate pilastri
Pos 1 Sup Ø16 / 20 cm L= 251 cm
Pos 1 Inf Ø16 / 20 cm L= 251 cm
136
15

PARTICOLARE CHIAMATE SETTI E PILASTRI
s=30 cm
-scala 1:20-

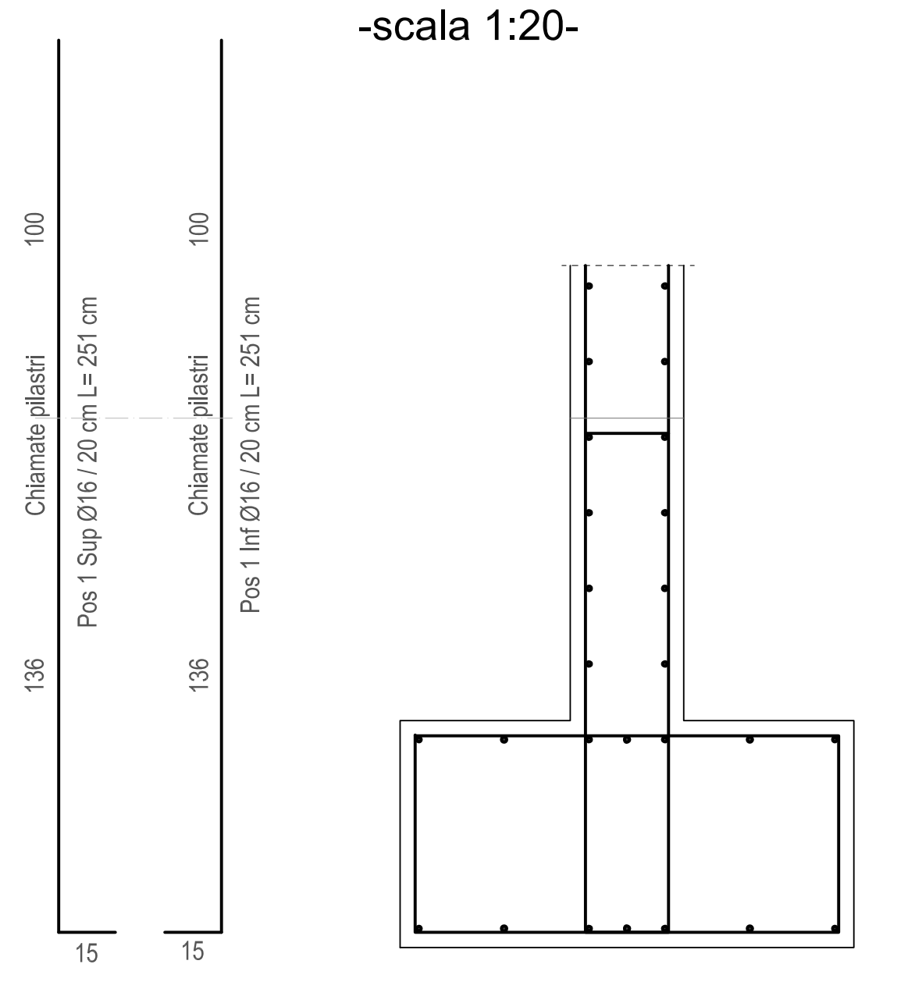
100
Chiamate pilastri
Pos 1 Sup Ø16 / 20 cm L= 251 cm
Pos 1 Inf Ø16 / 20 cm L= 251 cm
136
15

TRAVE ROVESCIA -TR 3-
-scala 1:20-

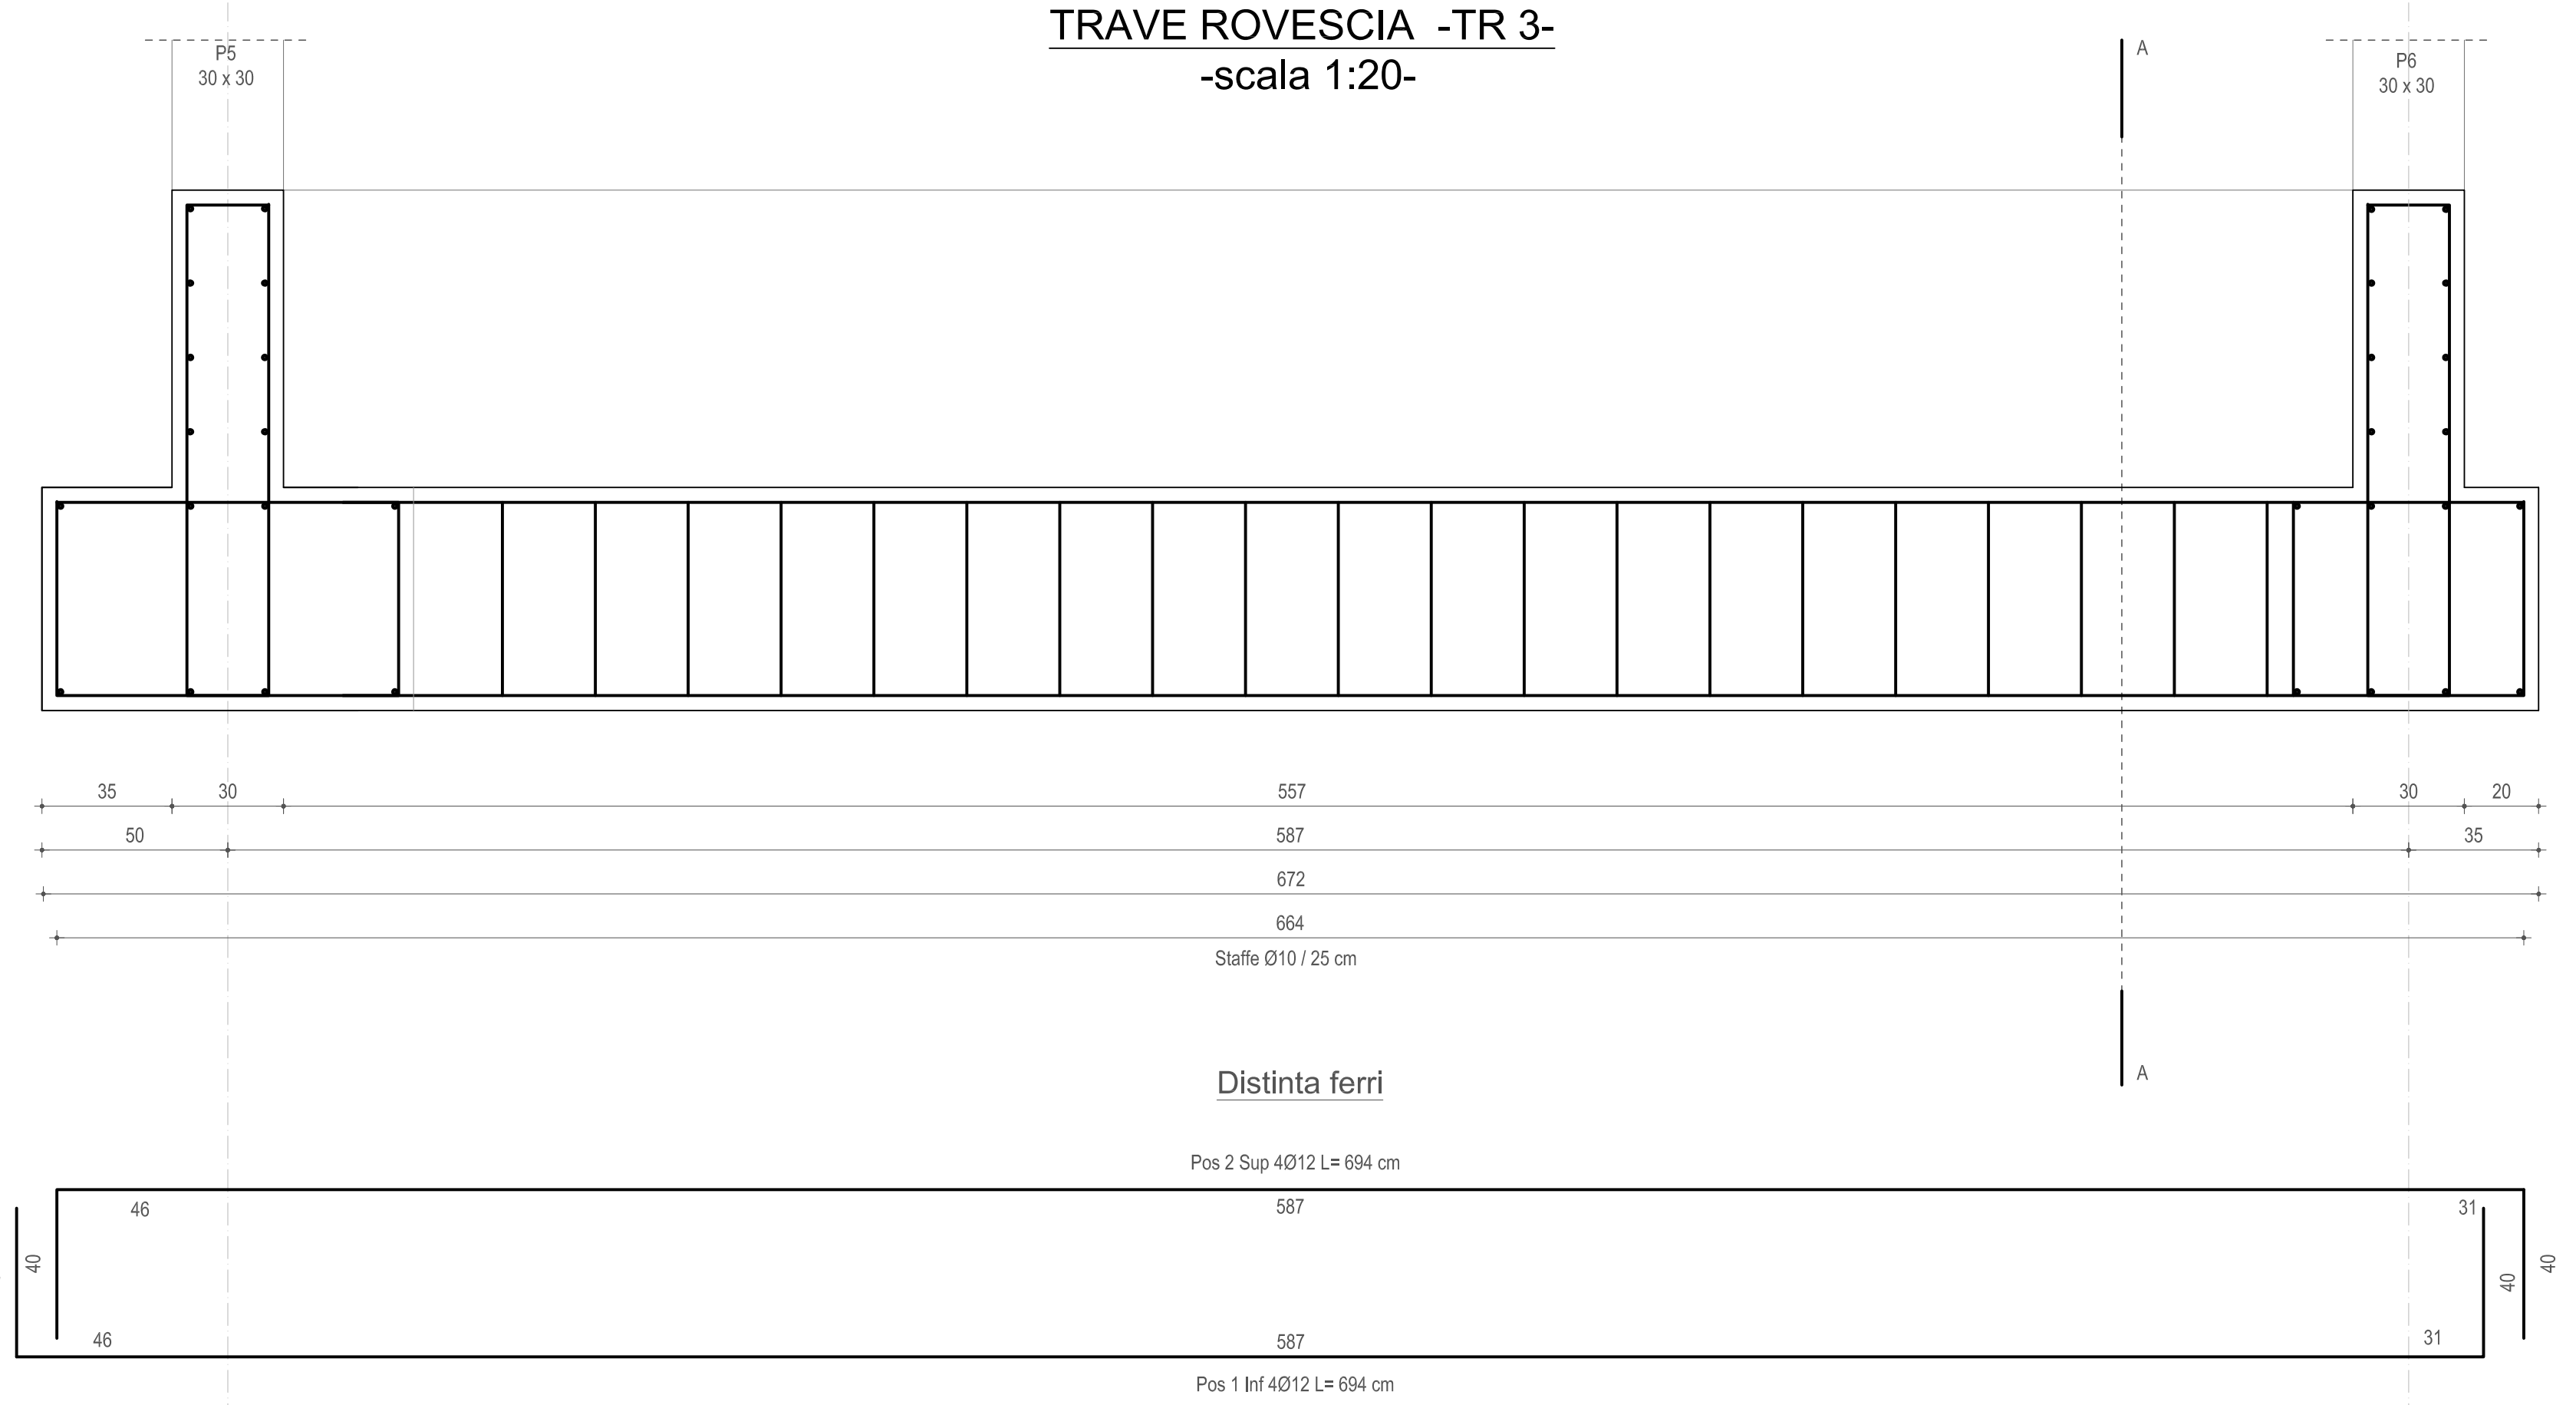

TRAVE ROVESCIA -TR 3-
-scala 1:20-
Sezione A-A

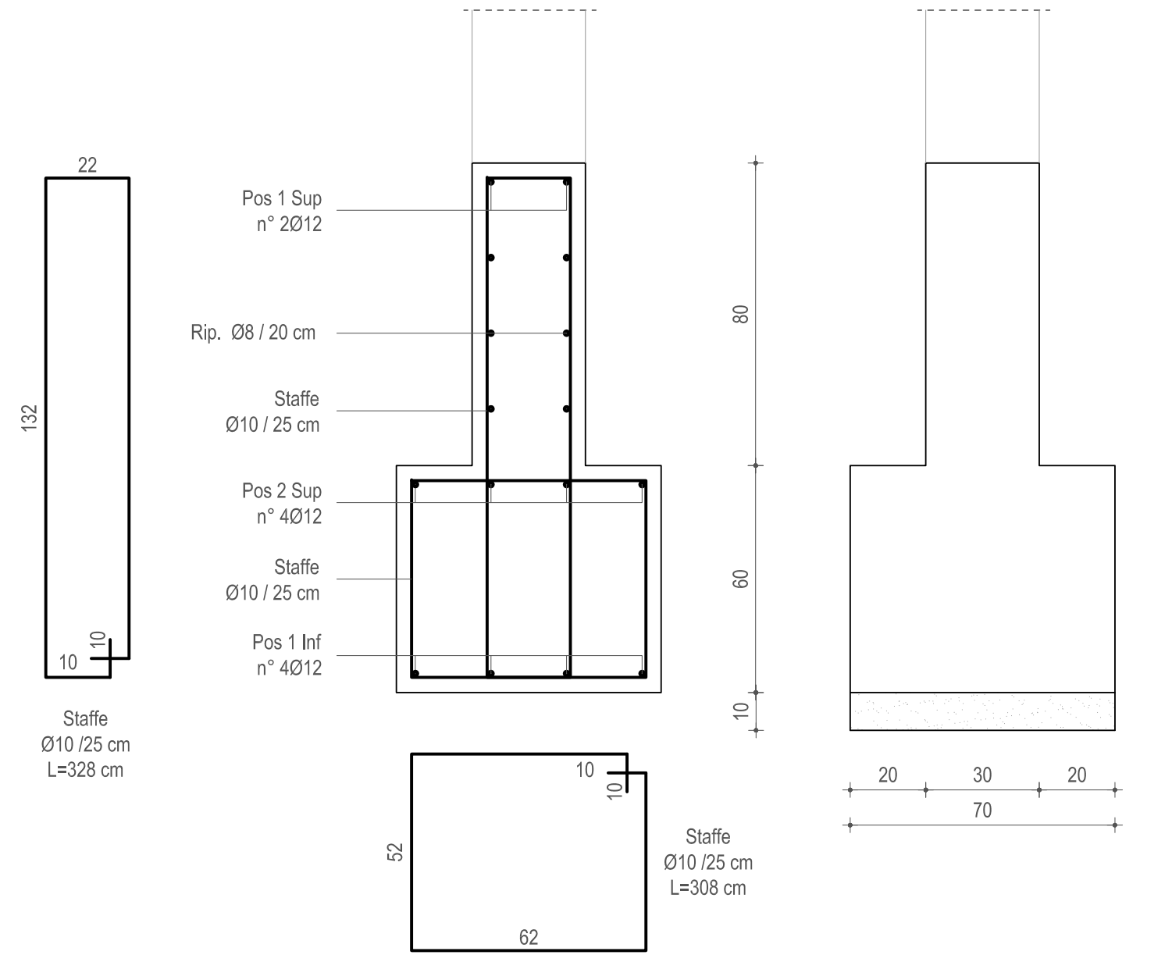

TRAVE ROVESCIA -TR 4-
-scala 1:20-

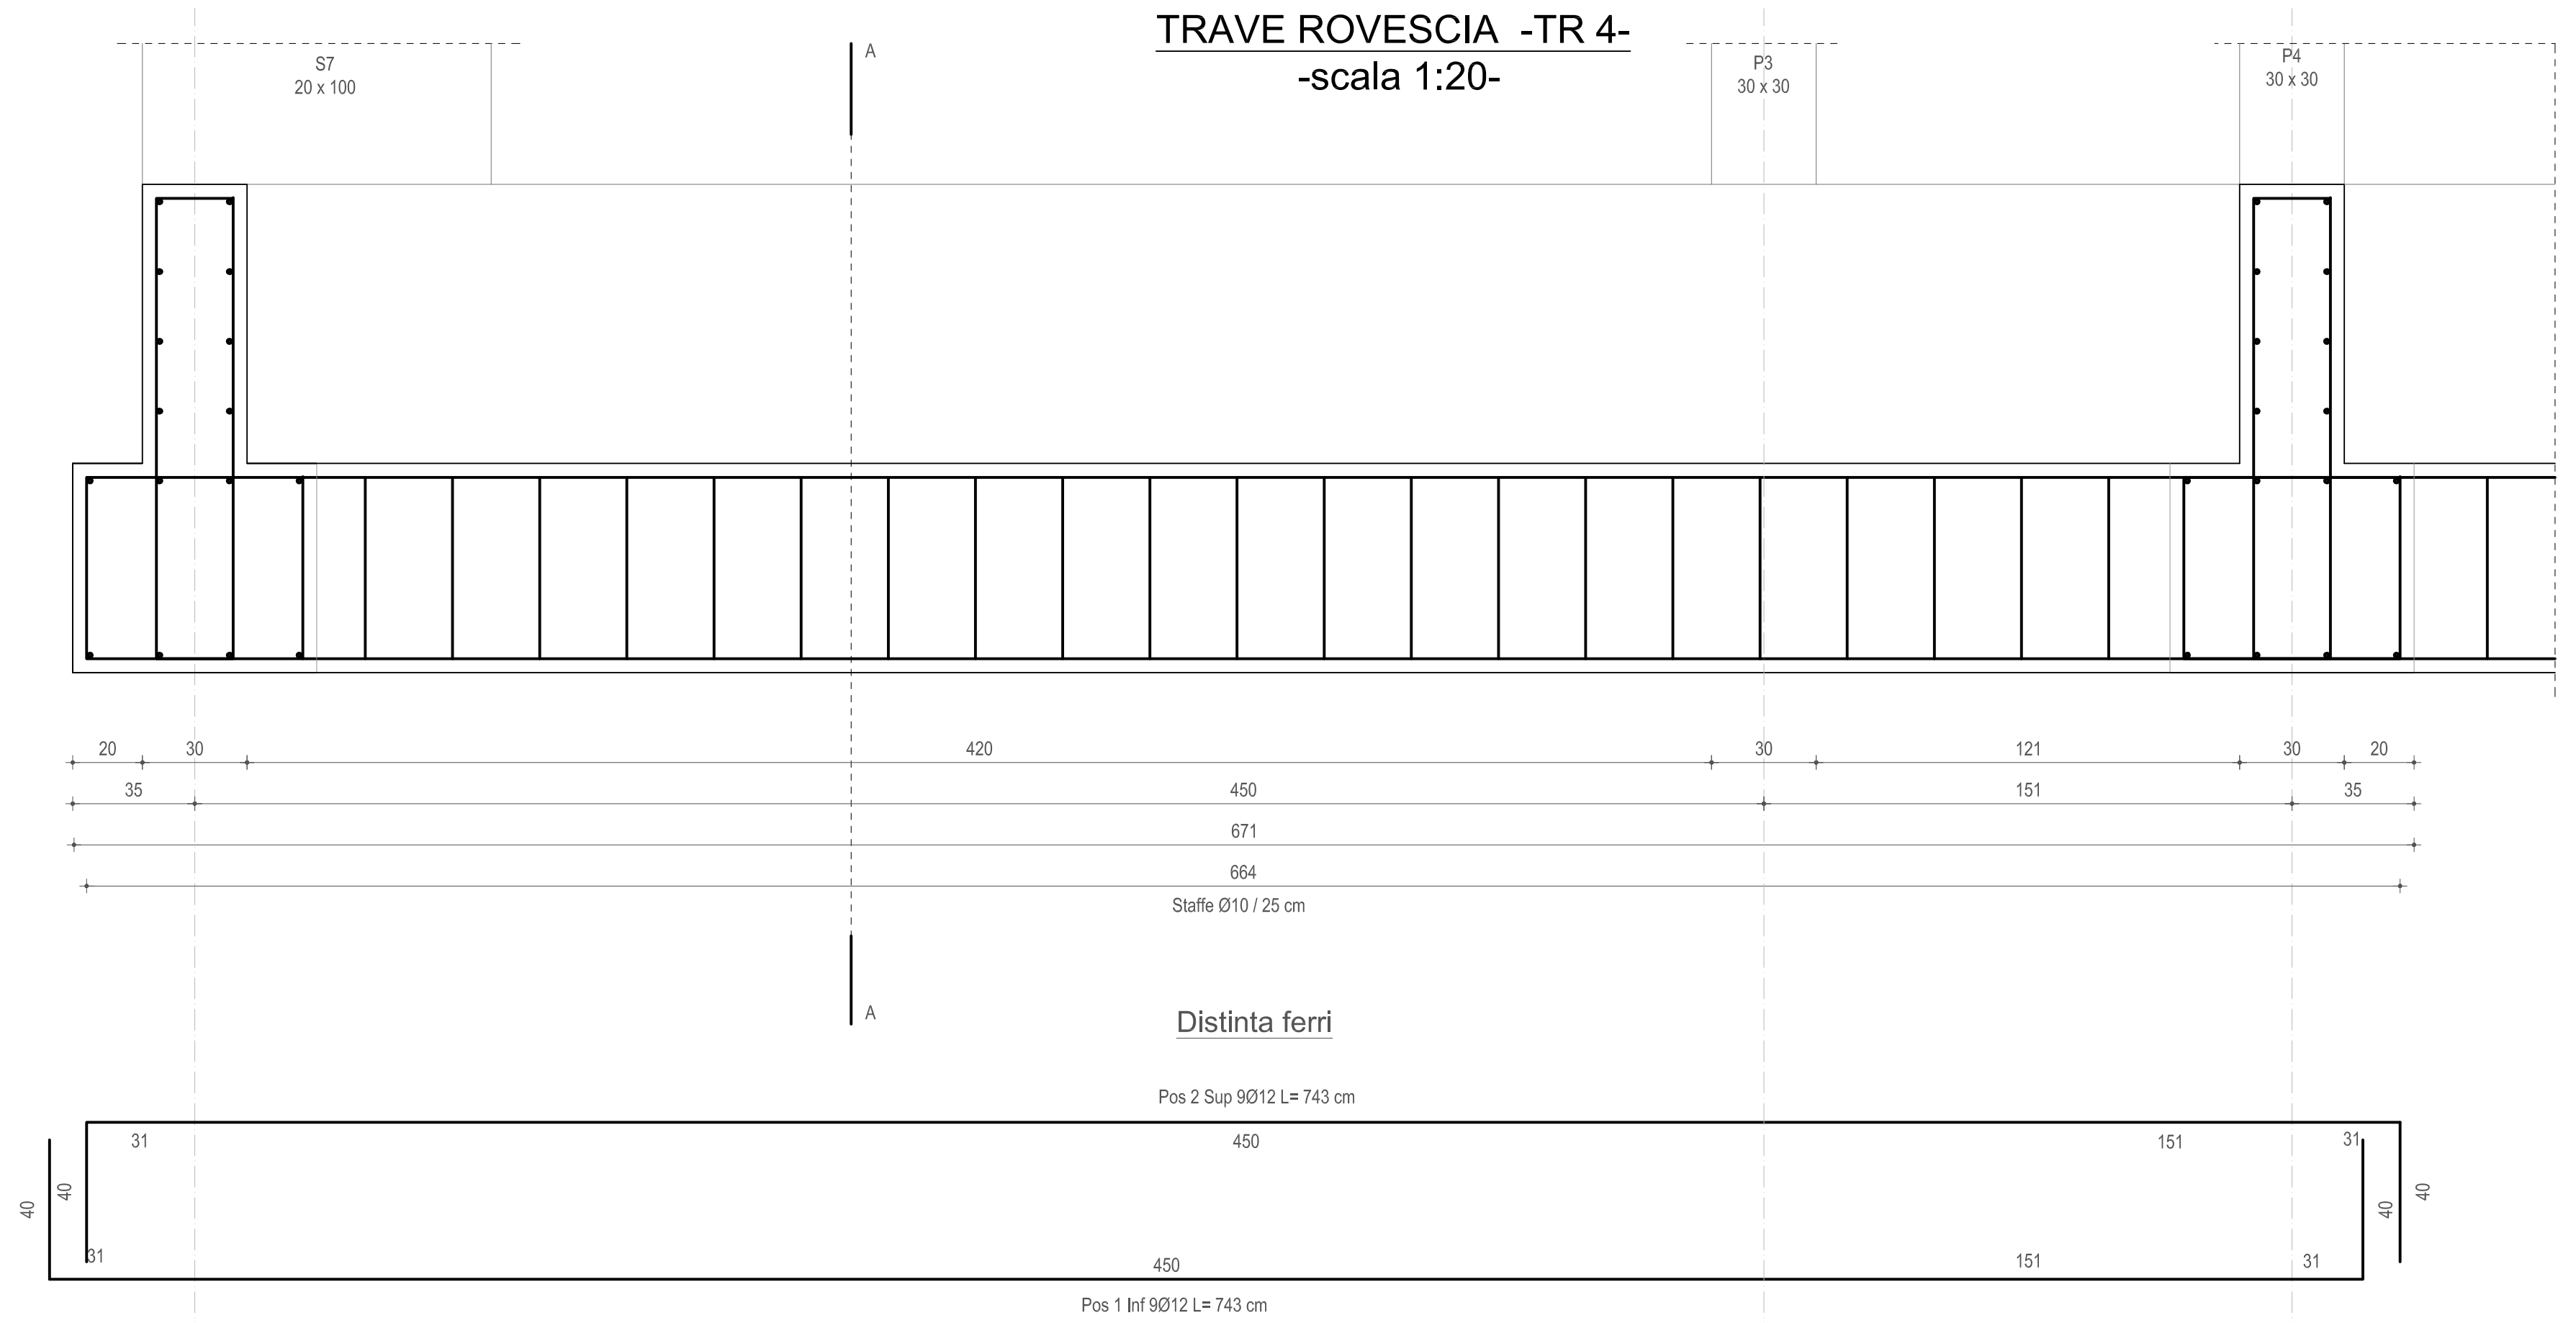

TRAVE ROVESCIA -TR 4-
-scala 1:20-
Sezione A-A

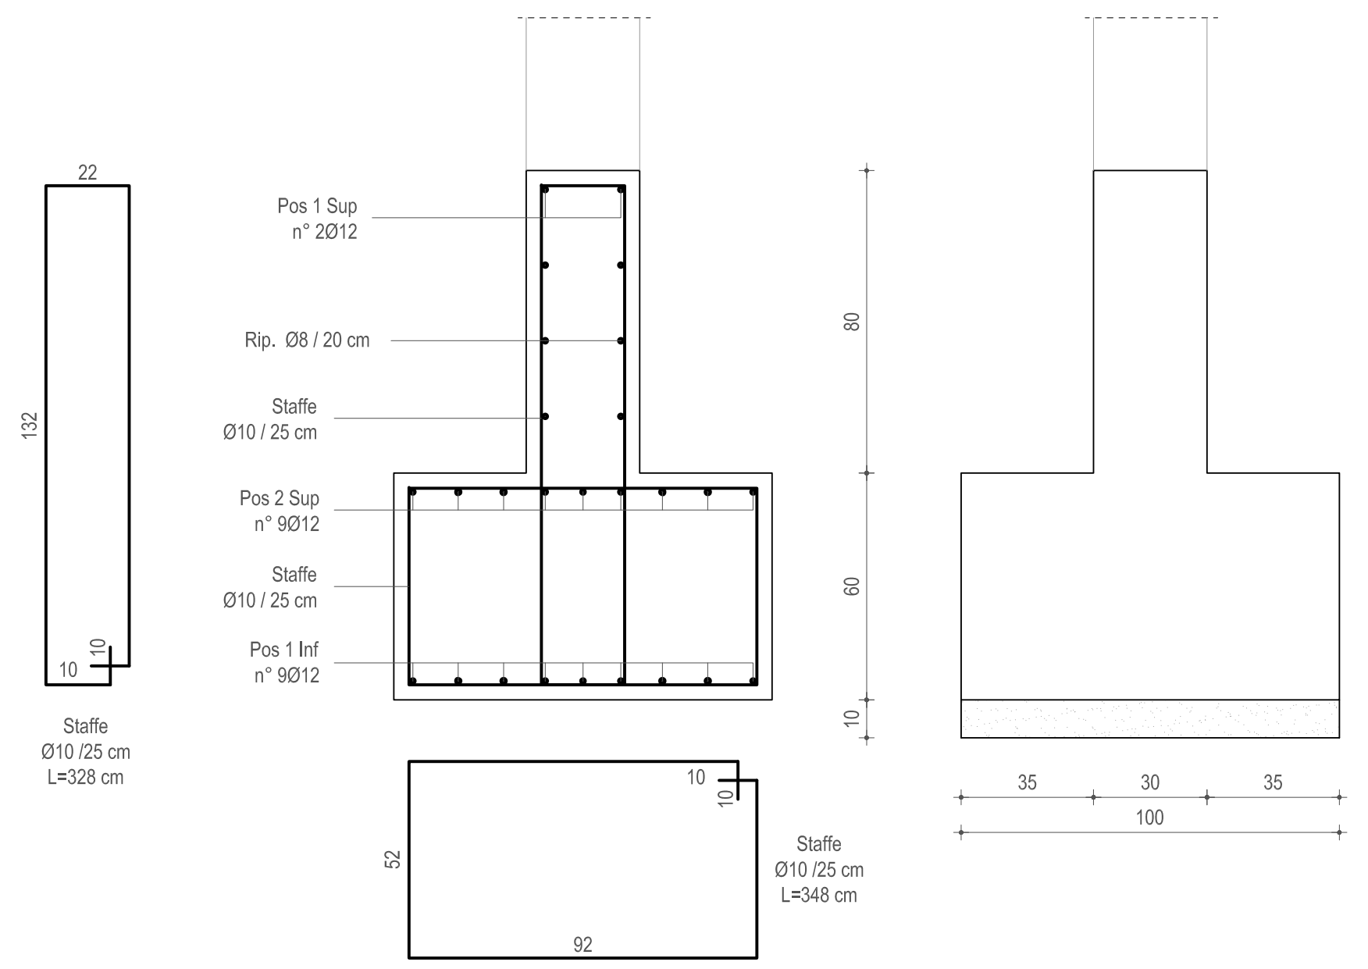

MATERIALI E PRESCRIZIONI

MATERIALI PRESCRITTI:

- Calcestruzzo per opere di: Fondazioni
  - Classe di resistenza : C25/30 (Rck 30)
  - Condizioni ambientali: Strutture completamente interrate in terreno permeabile
  - Classe di esposizione : XC2
  - Rapporto massimo acqua/cemento: 0,60
  - Classe di consistenza: S3 (Plastica)
  - Diametro massimo degli aggregati: 16 mm
- Calcestruzzo per opere di: Elevazione e Solai misti laterizio-c.a.
  - Classe di resistenza : C25/30 (Rck 30)
  - Condizioni ambientali: Strutture interne di edifici non industriali con umidità bassa
  - Classe di esposizione : XC1
  - Rapporto massimo acqua/cemento: 0,60
  - Classe di consistenza: S3 (Plastica)
  - Diametro massimo degli aggregati: 16 mm
- Calcestruzzo per opere di: Solette piene in C.A.
  - Classe di resistenza : C28/35 (Rck 35)
  - Condizioni ambientali: Strutture interne di edifici non industriali con umidità bassa
  - Classe di esposizione : XC1
  - Rapporto massimo acqua/cemento: 0,60
  - Classe di consistenza: S3 (Plastica)
  - Diametro massimo degli aggregati: 16 mm
- Acciaio per tutte le strutture: B450 C controllato

PRESCRIZIONE

Tutte le misure dovranno essere controllate in cantiere confrontandole con quelle del progetto architettonico e confermate dalla direzione lavori

---

COMUNE DI VOLTA MANTOVANA PROVINCIA DI MANTOVA

Oggetto
PROGETTO PER LA REALIZZAZIONE DI CASA UNIFAMILIARE.

[redacted]

Oggetto tavola
- Disegni esecutivi:
  Fondazioni

Denuncia C.A.

Tav. n° 1
Variante
Data
Scale 1:100, 1:20

[redacted]

[redacted]laboratori