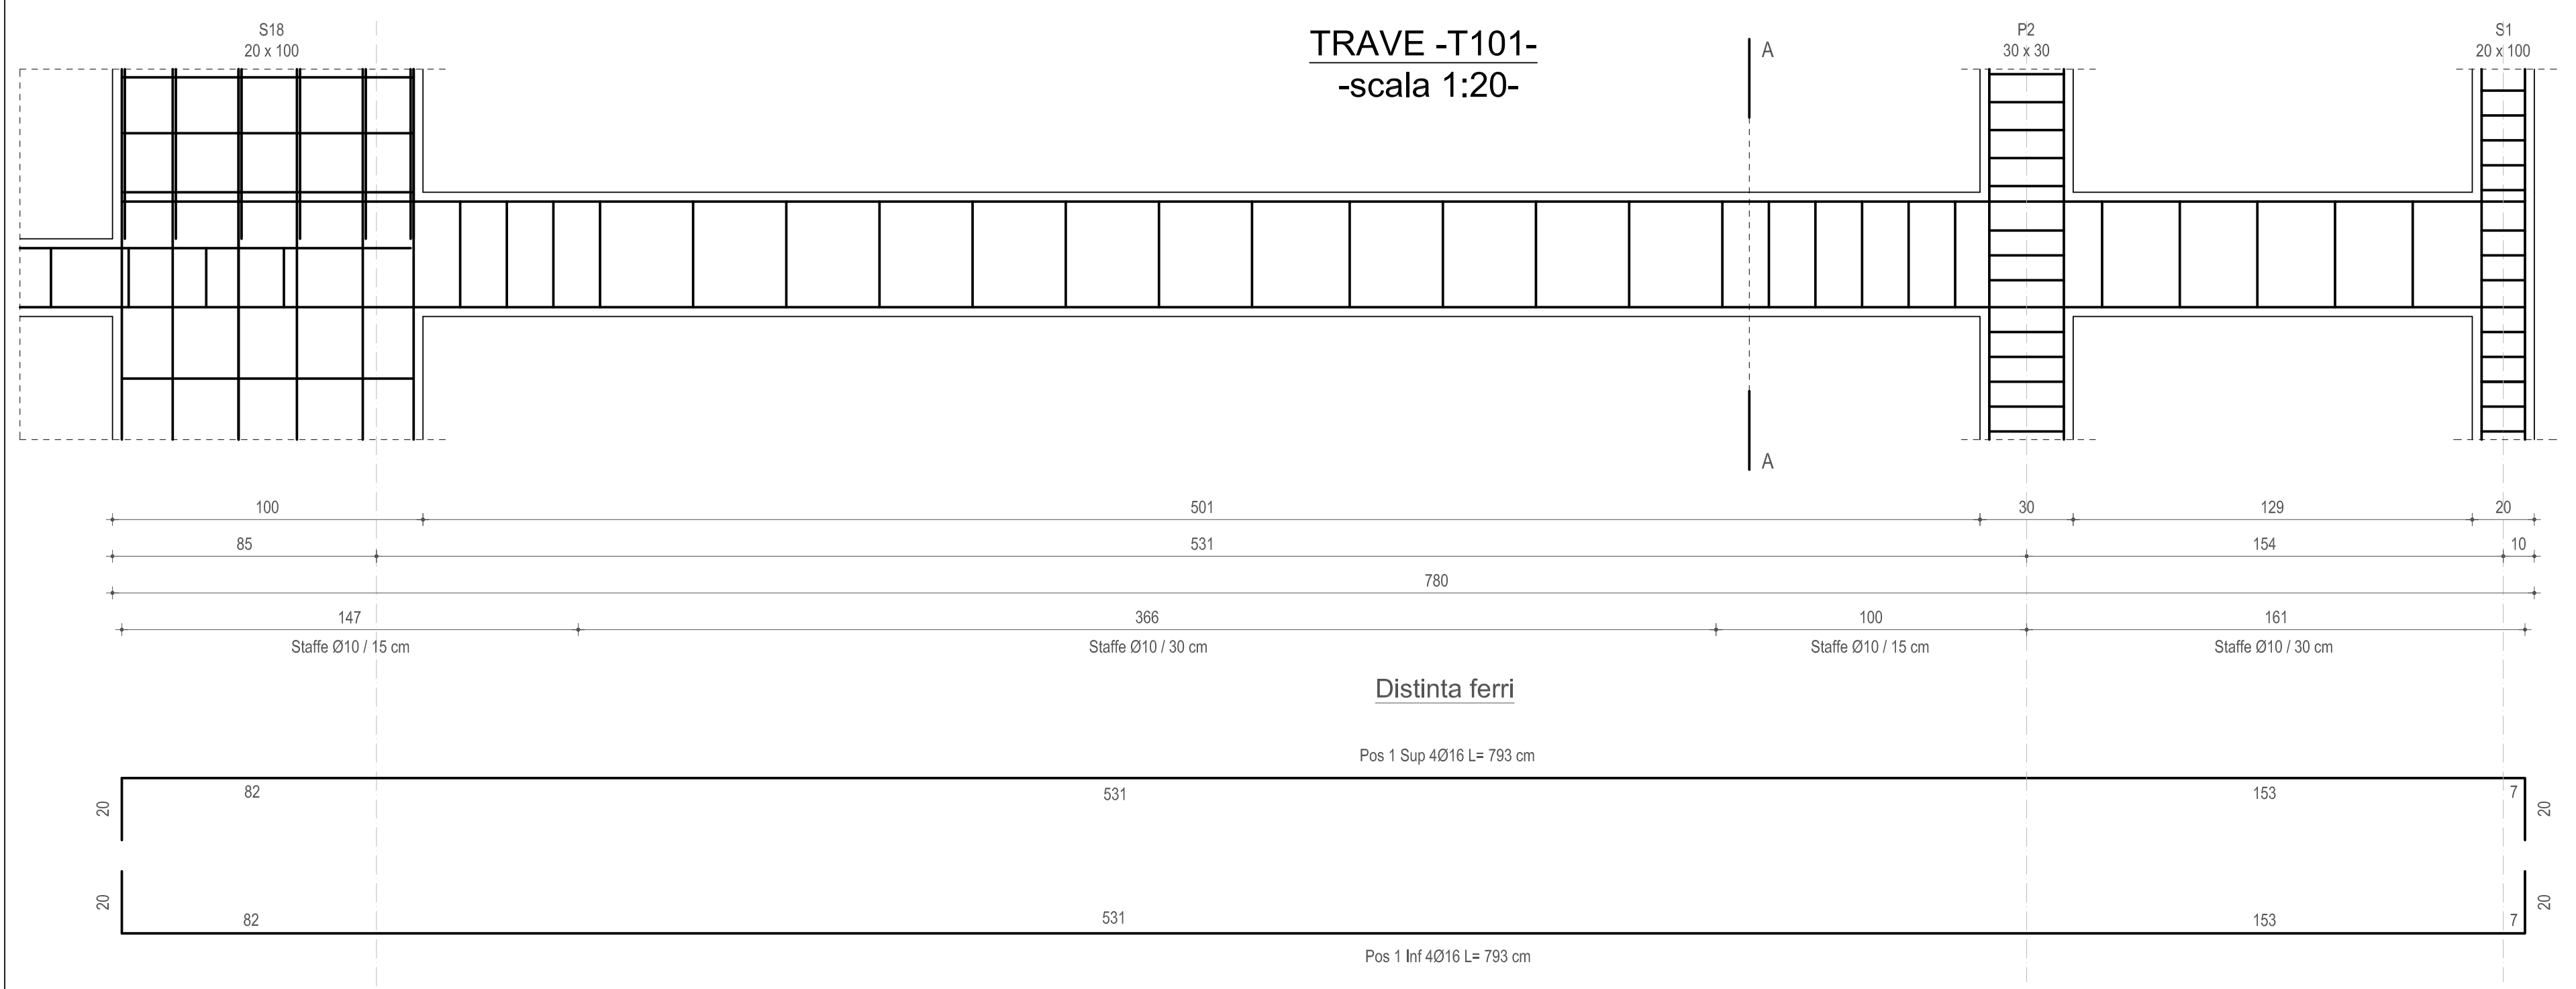

**TRAVE -T101-**
-scala 1:20-

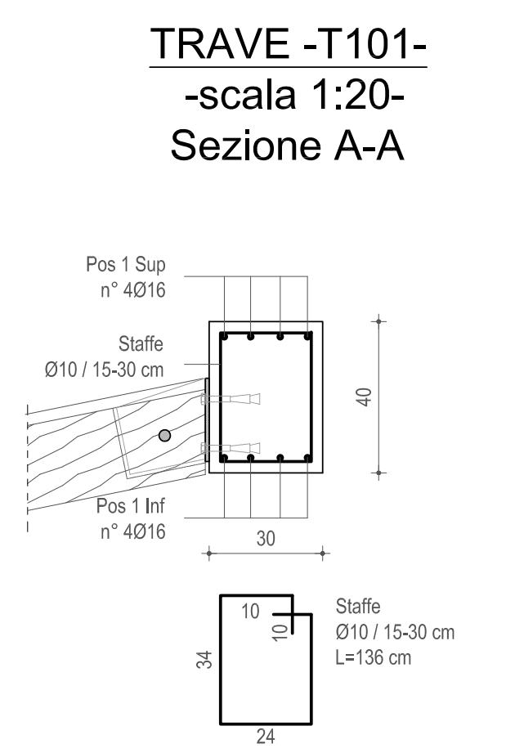

**TRAVE -T101-**
-scala 1:20-
Sezione A-A

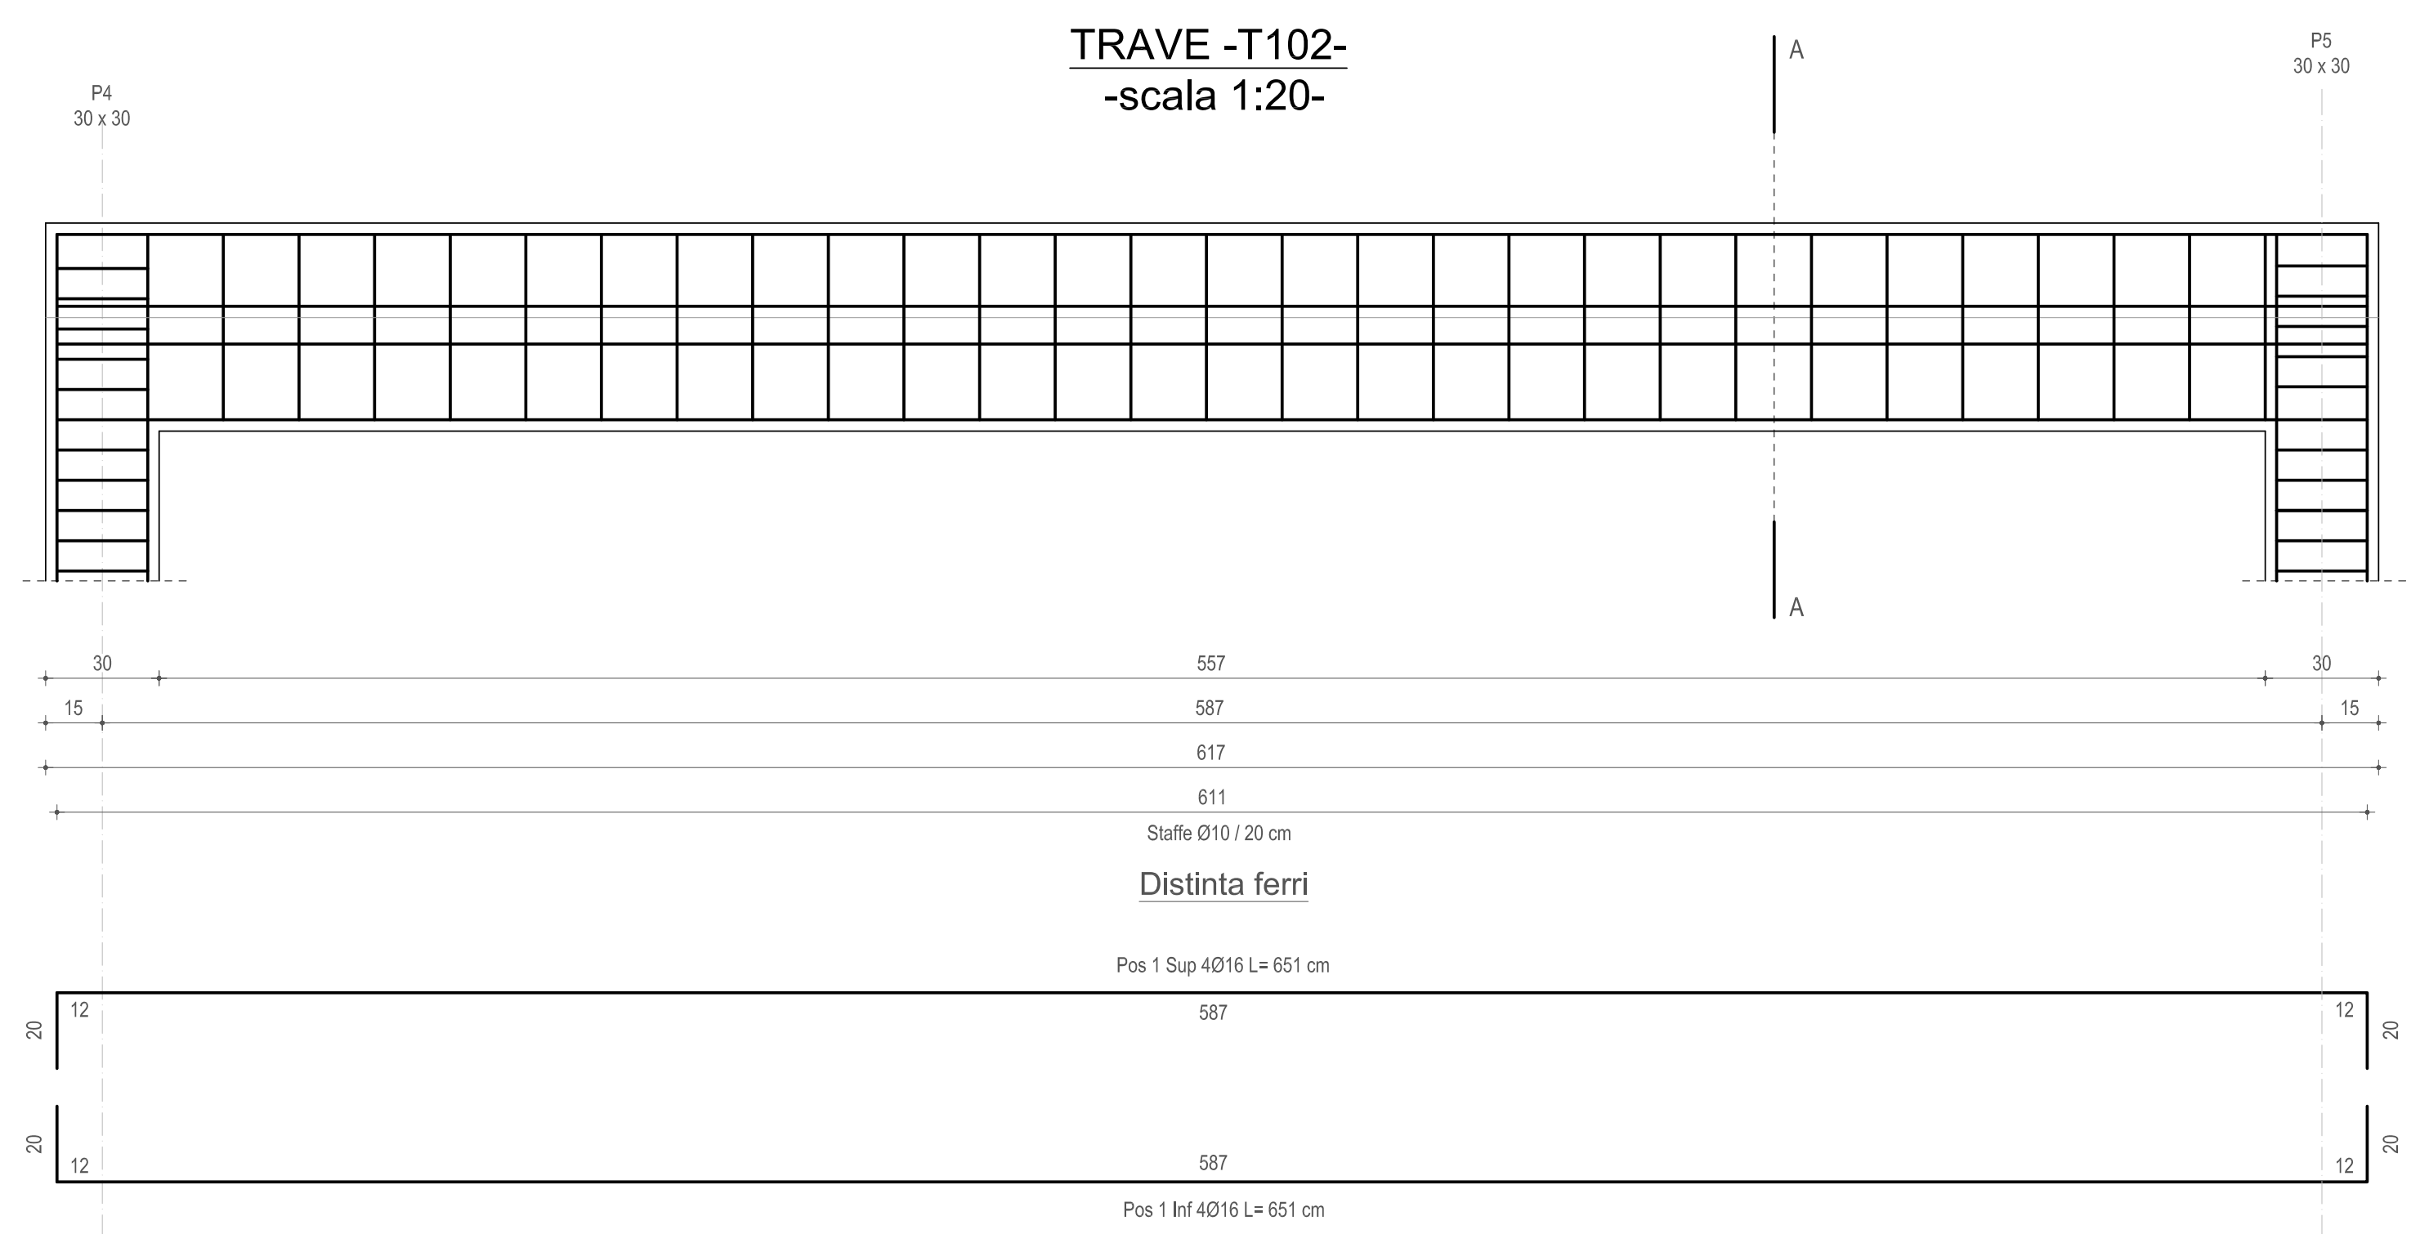

**TRAVE -T102-**
-scala 1:20-

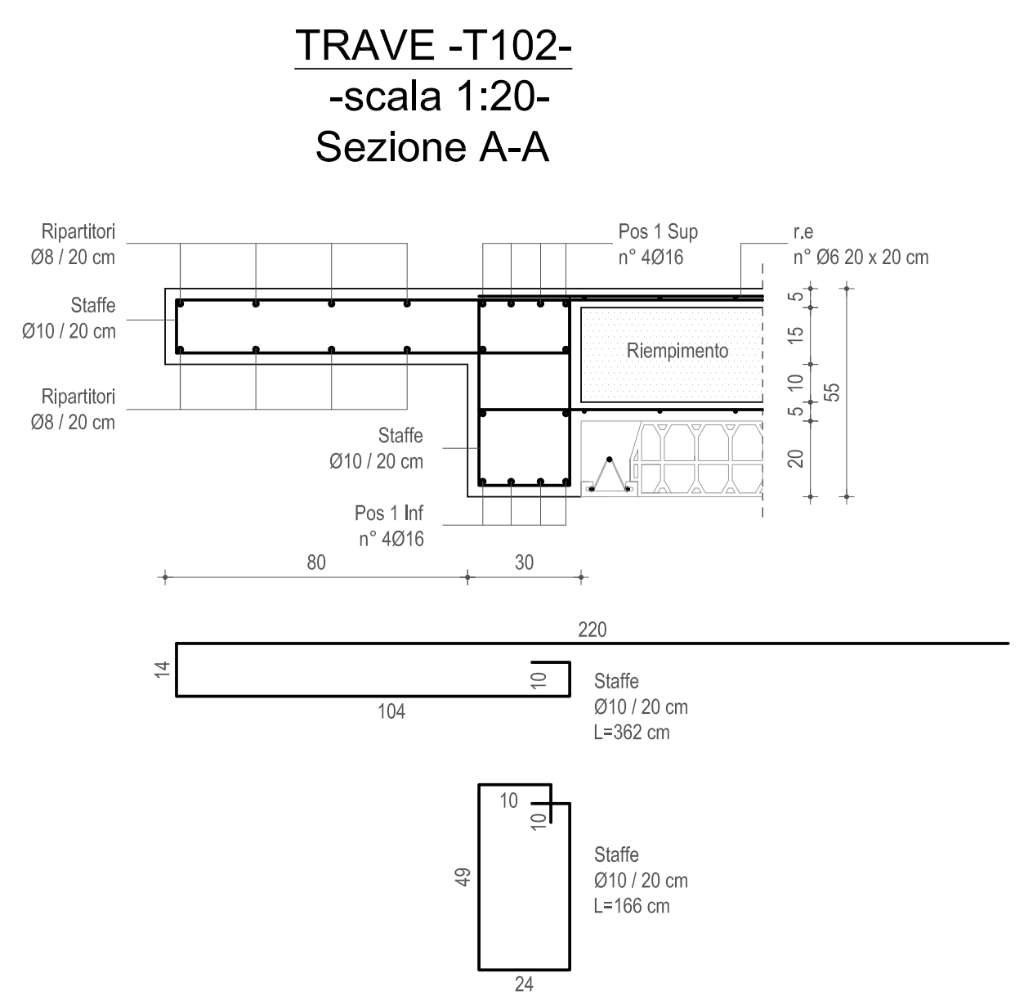

**TRAVE -T102-**
-scala 1:20-
Sezione A-A

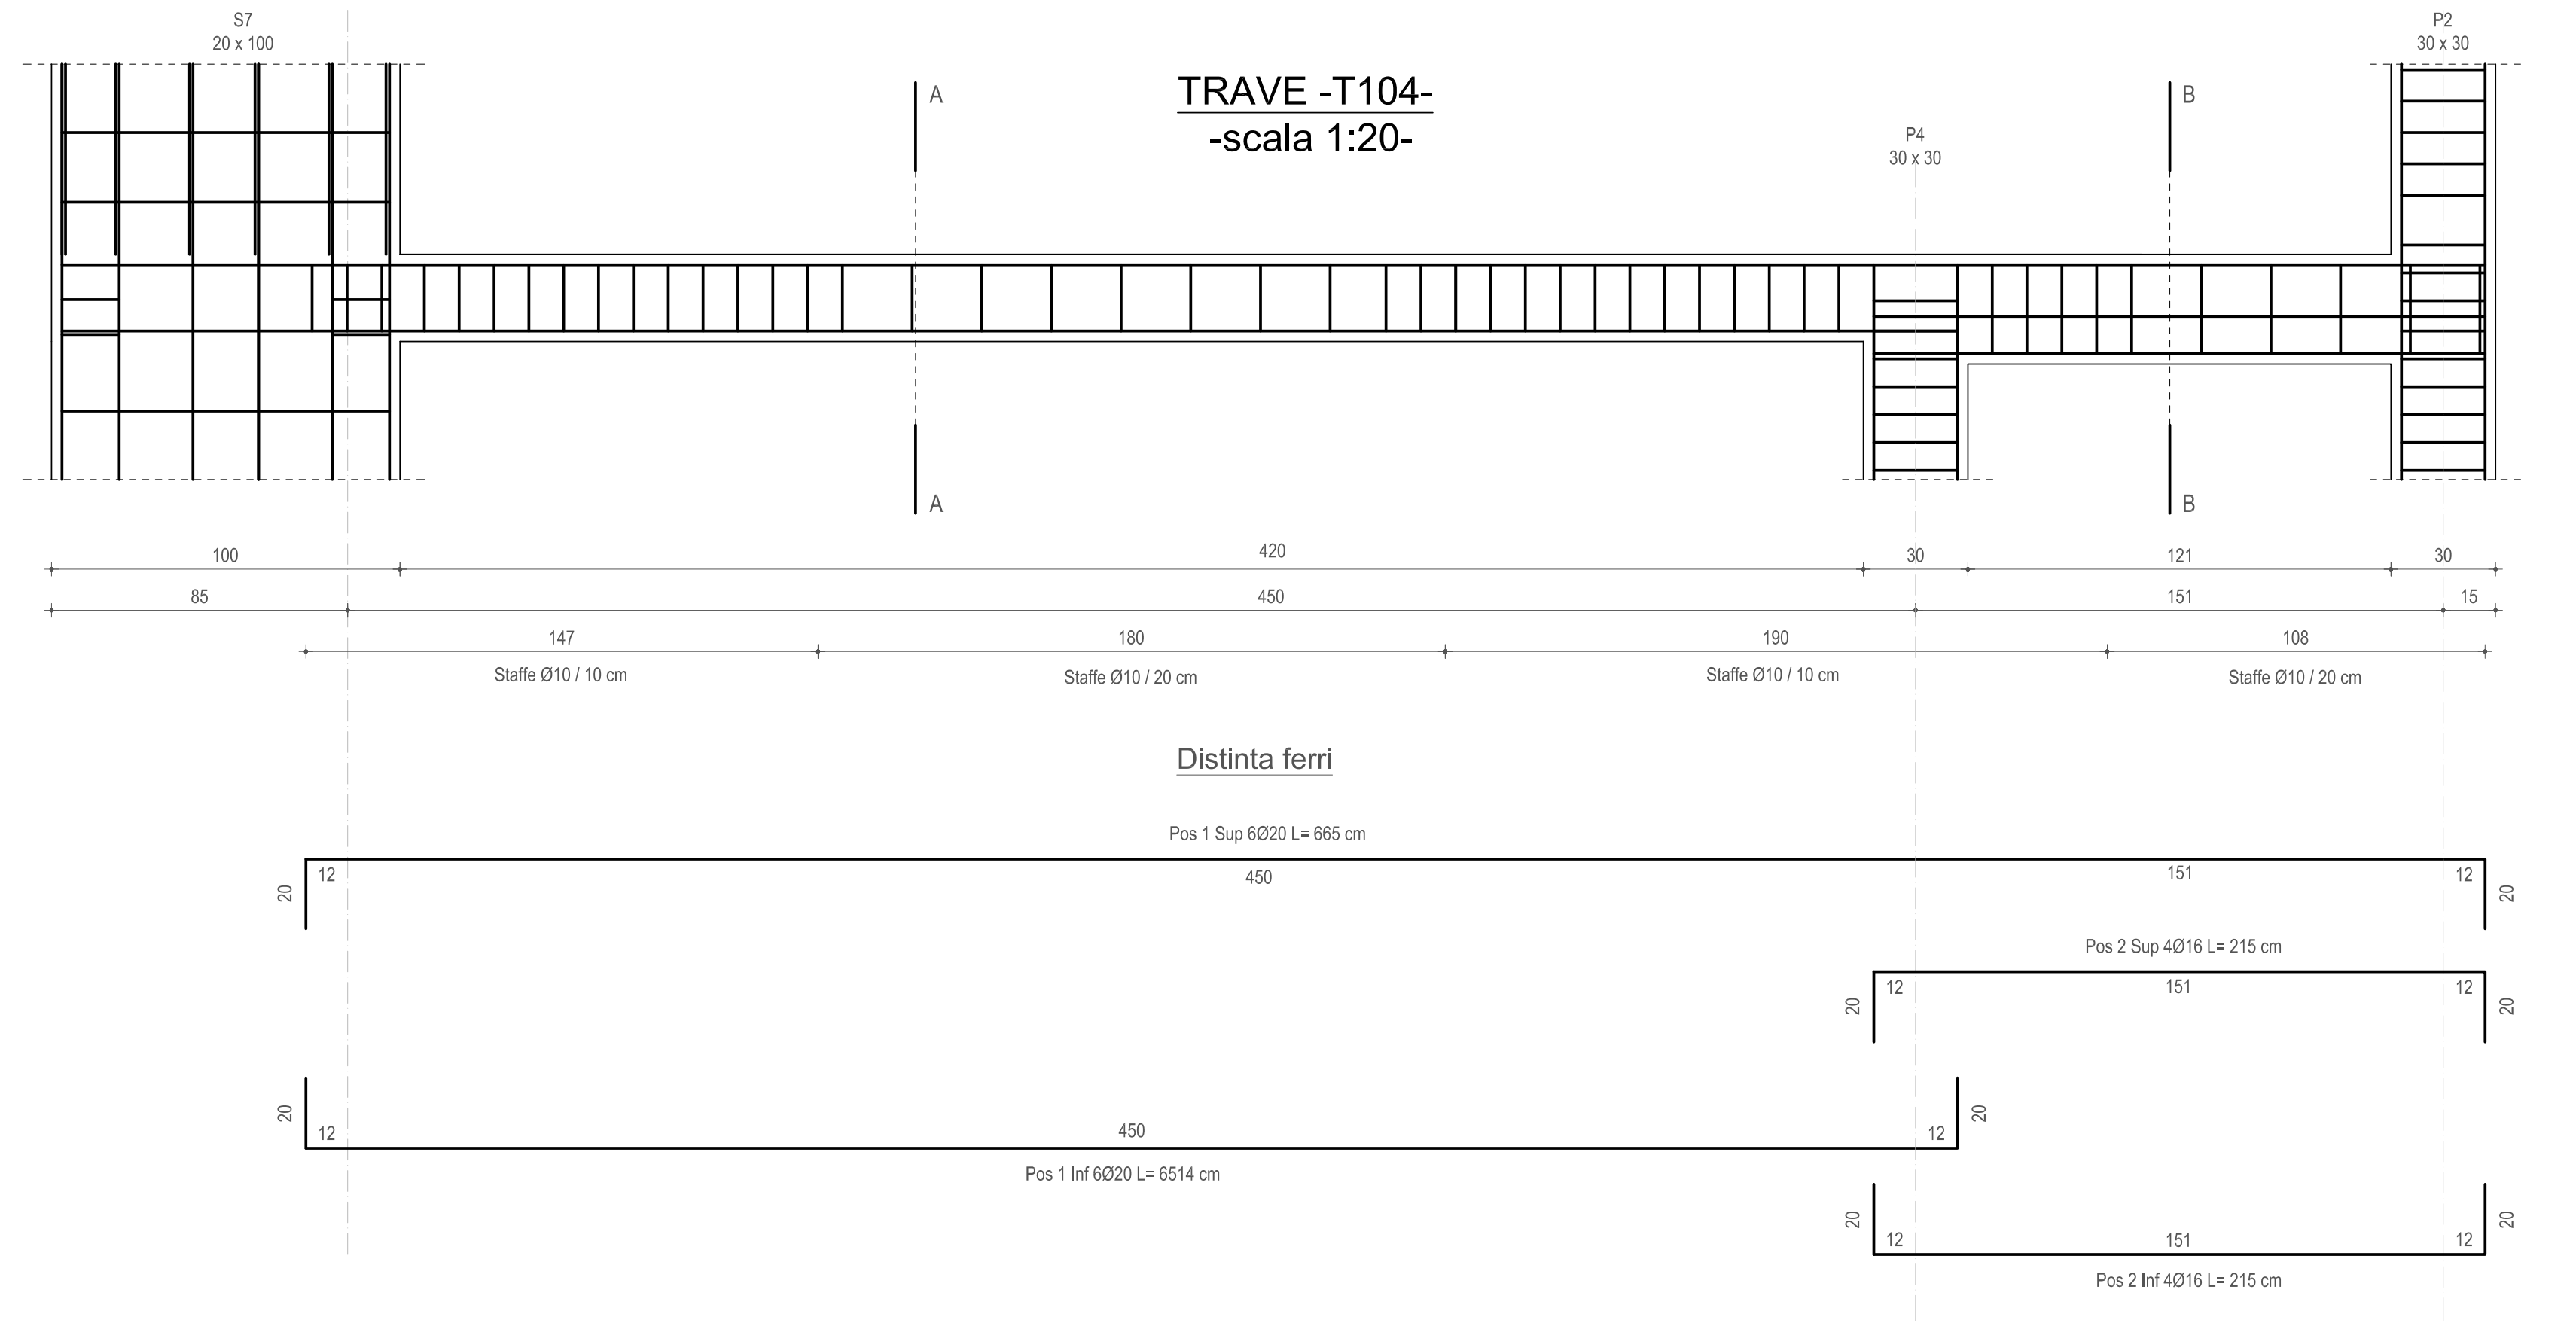

**TRAVE -T104-**
-scala 1:20-

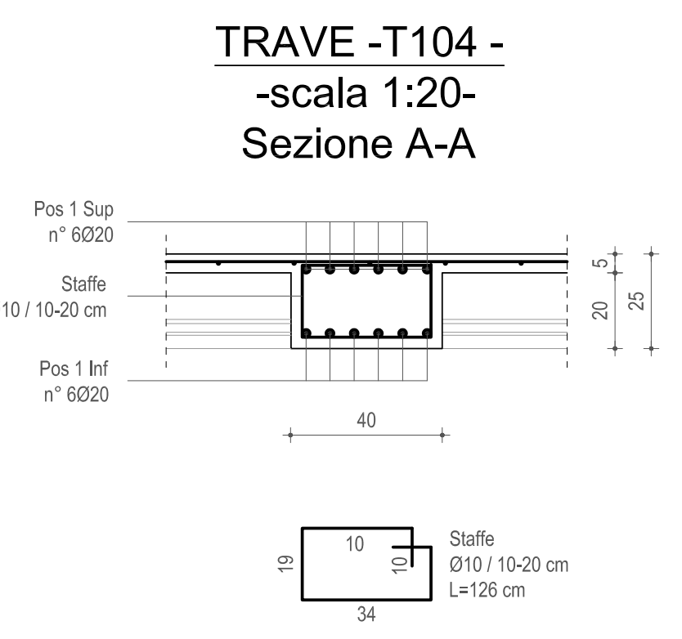

**TRAVE -T104 -**
-scala 1:20-
Sezione A-A

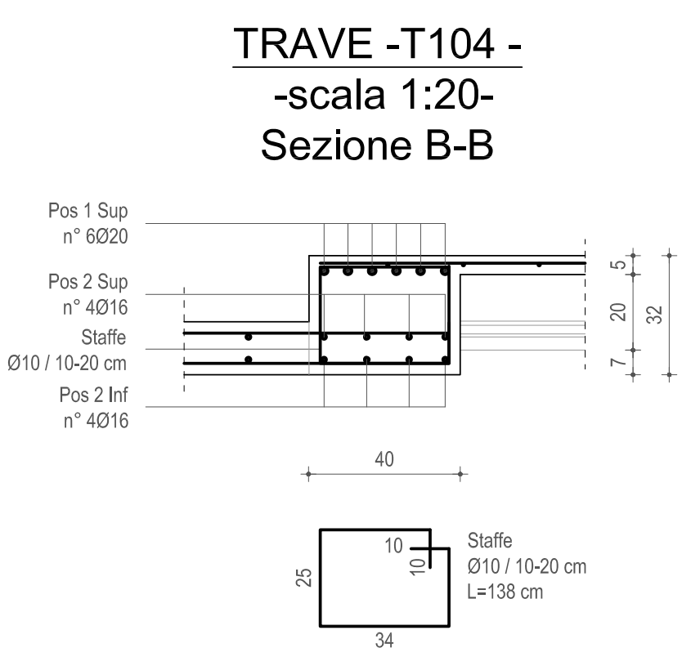

**TRAVE -T104 -**
-scala 1:20-
Sezione B-B

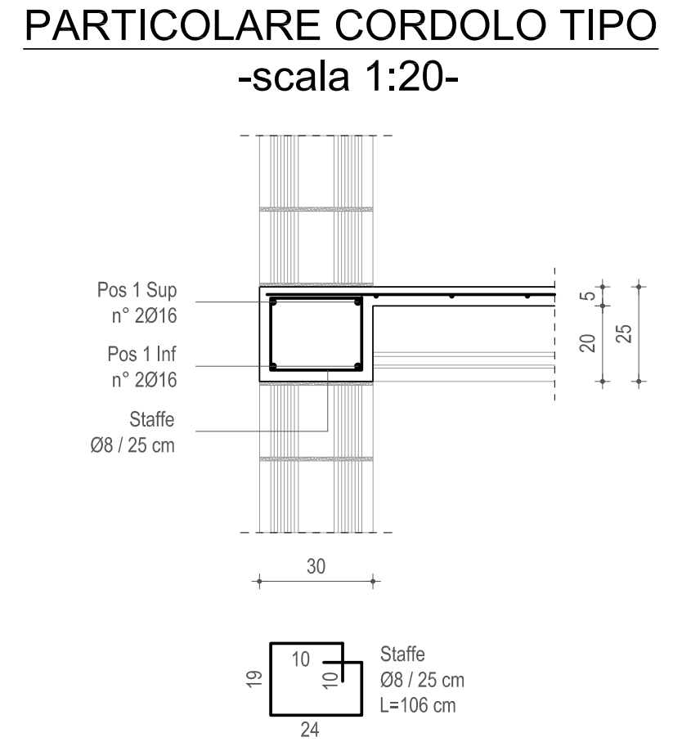

**PARTICOLARE CORDOLO TIPO**
-scala 1:20-

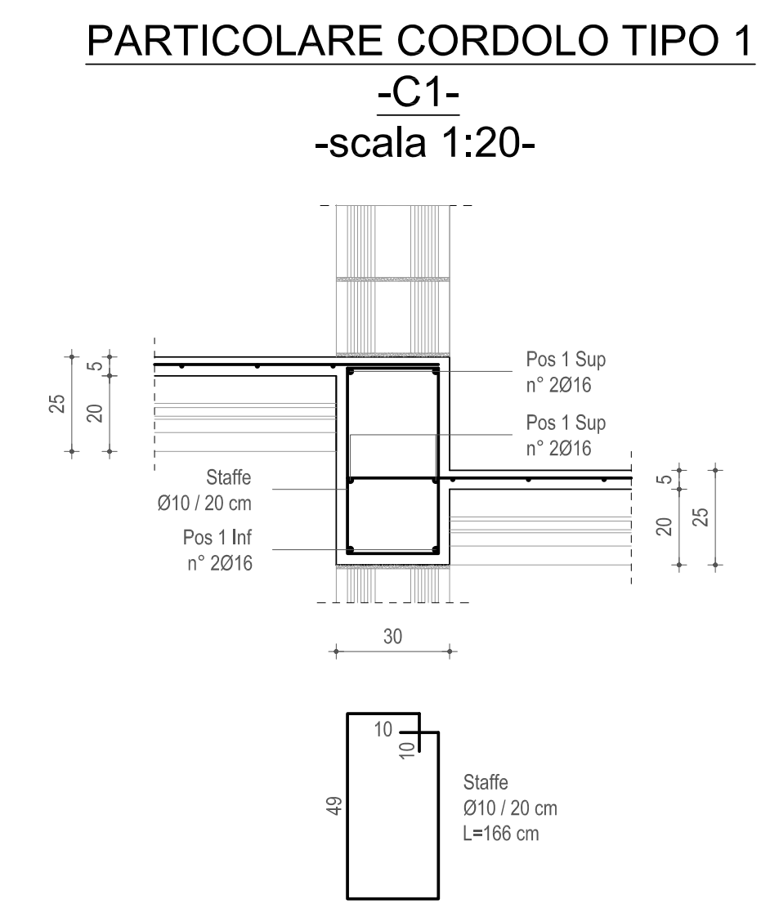

**PARTICOLARE CORDOLO TIPO 1**
-C1-
-scala 1:20-

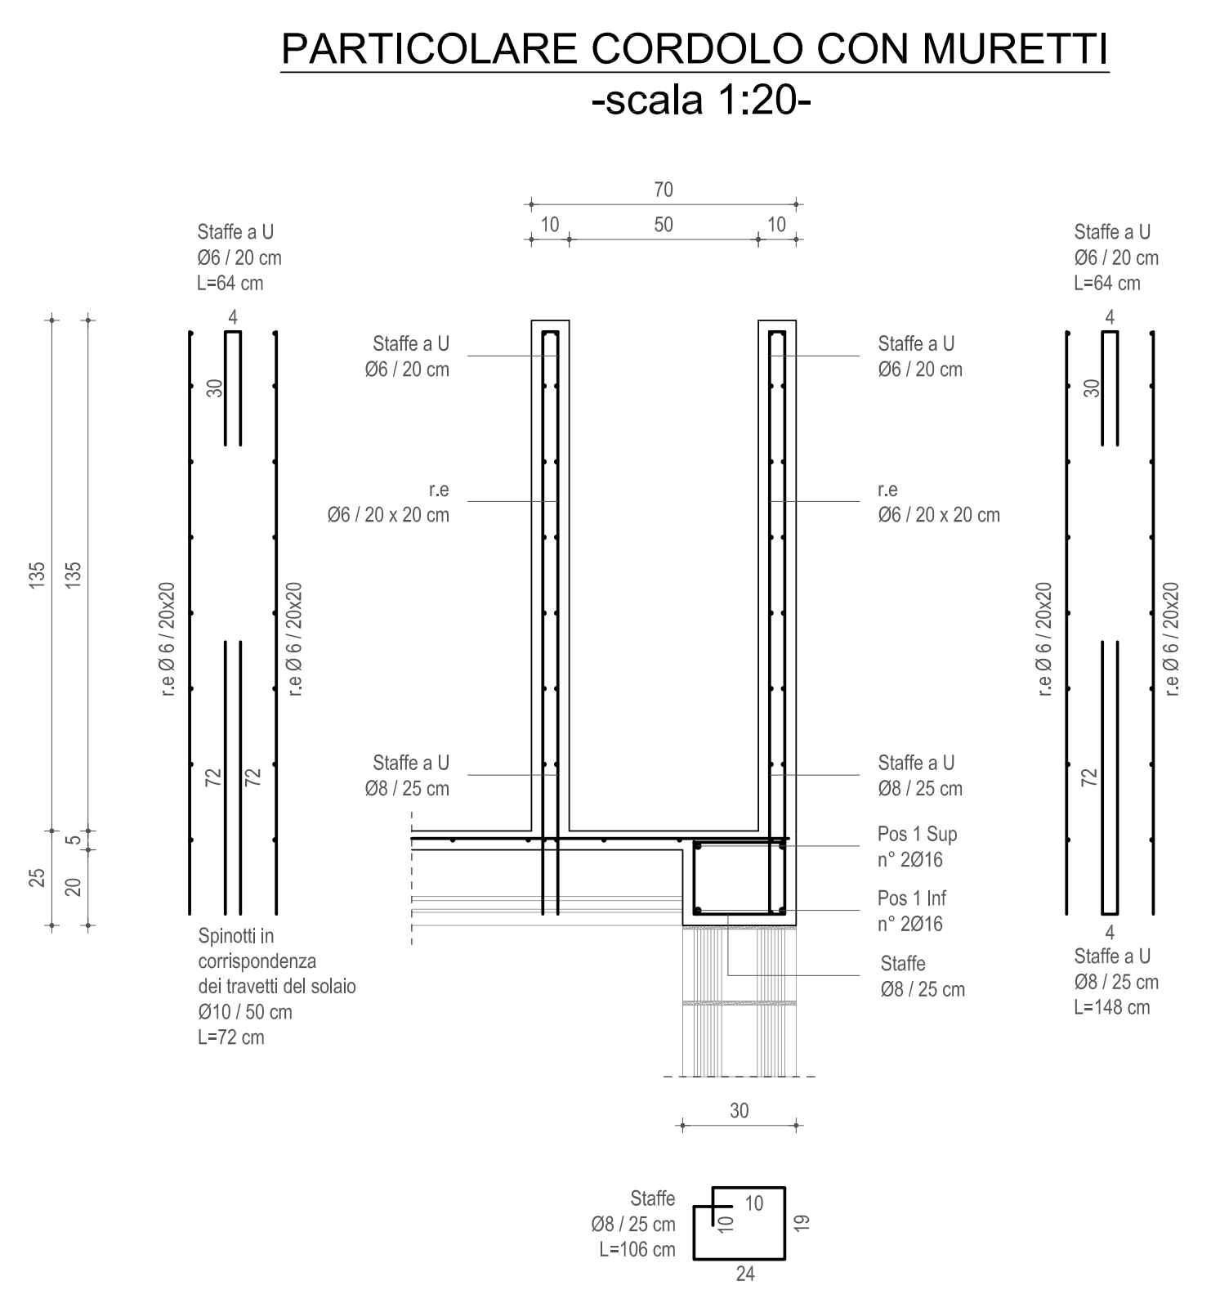

**PARTICOLARE CORDOLO CON MURETTI**
-scala 1:20-

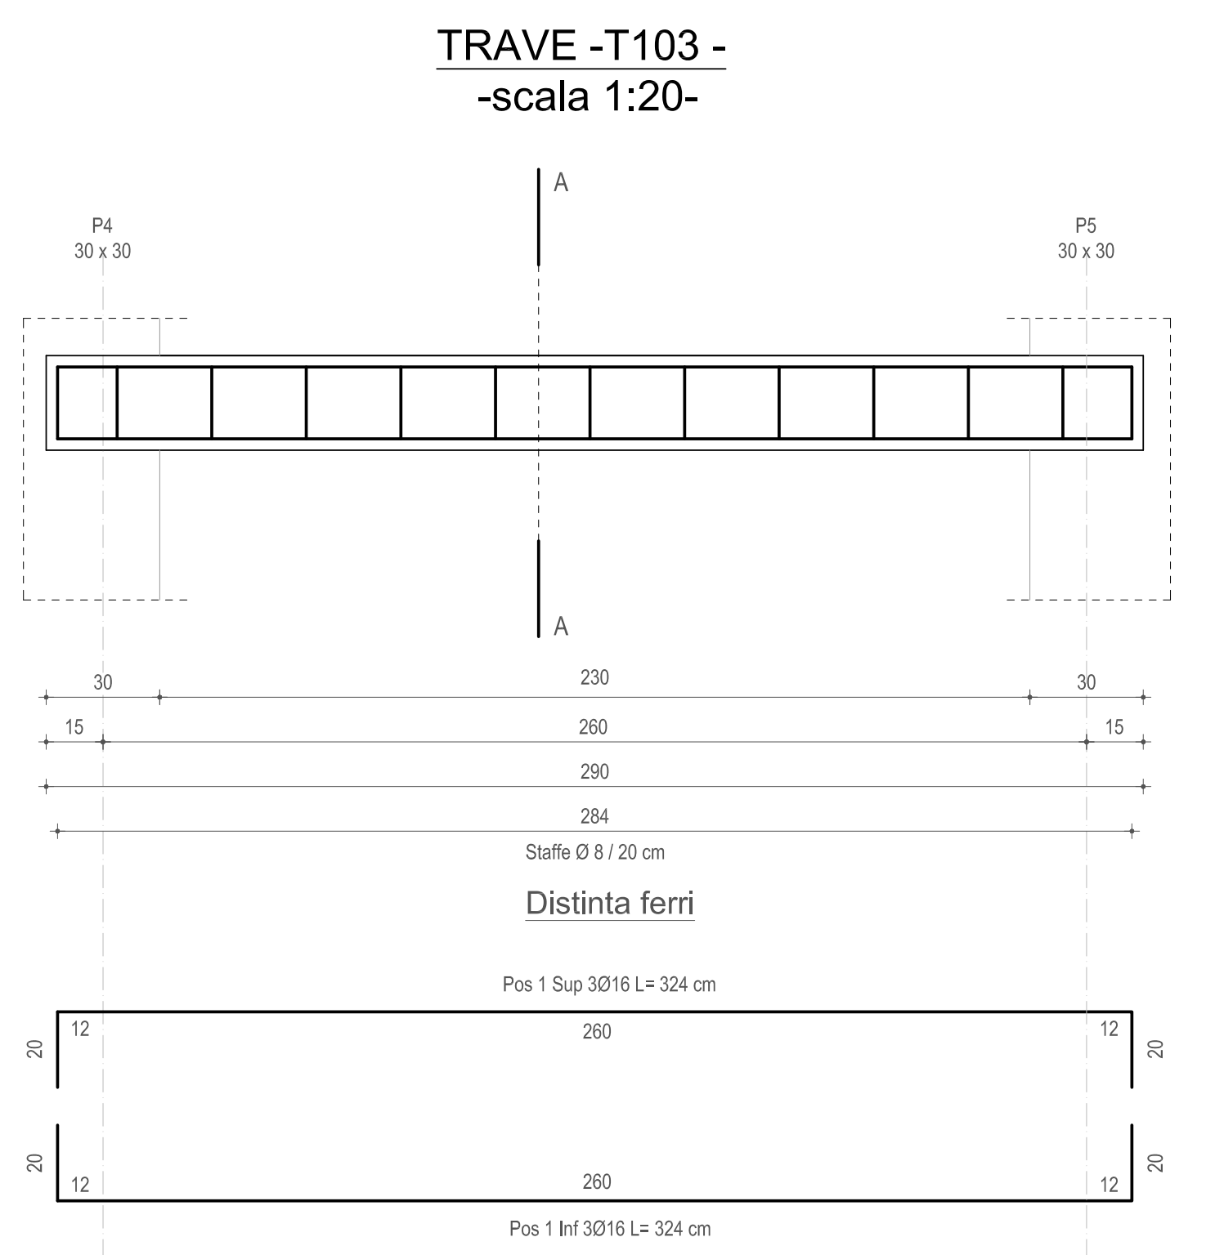

**TRAVE -T103 -**
-scala 1:20-

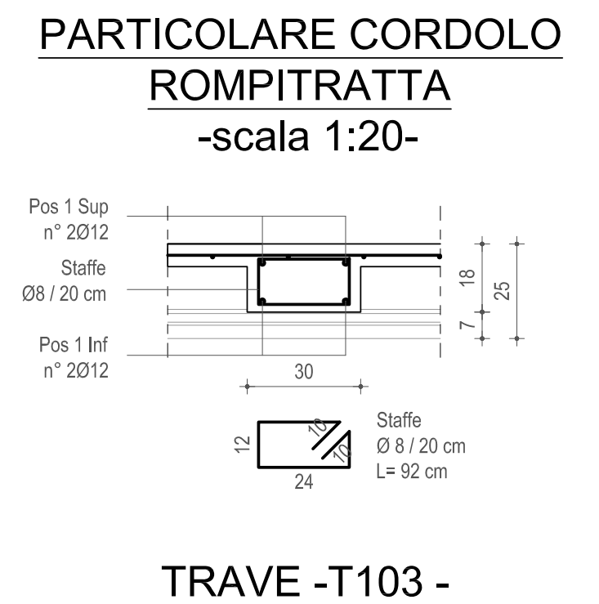

**PARTICOLARE CORDOLO ROMPITRATTA**
-scala 1:20-

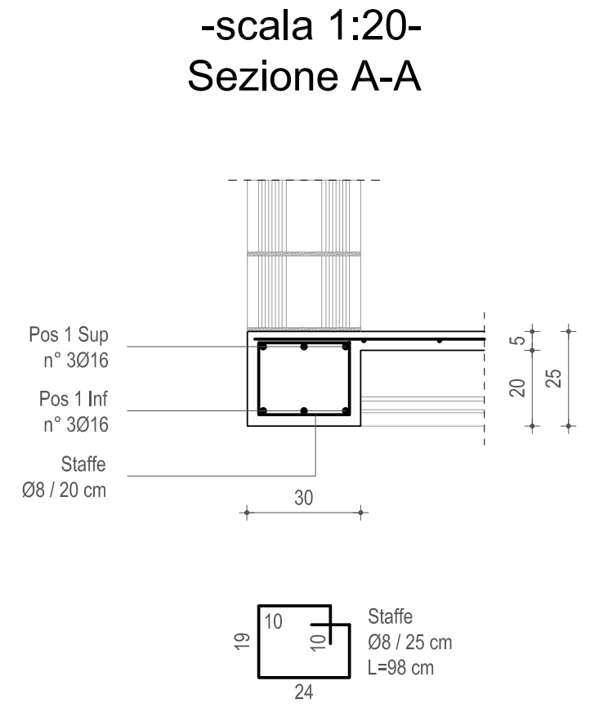

**TRAVE -T103 -**
-scala 1:20-
Sezione A-A

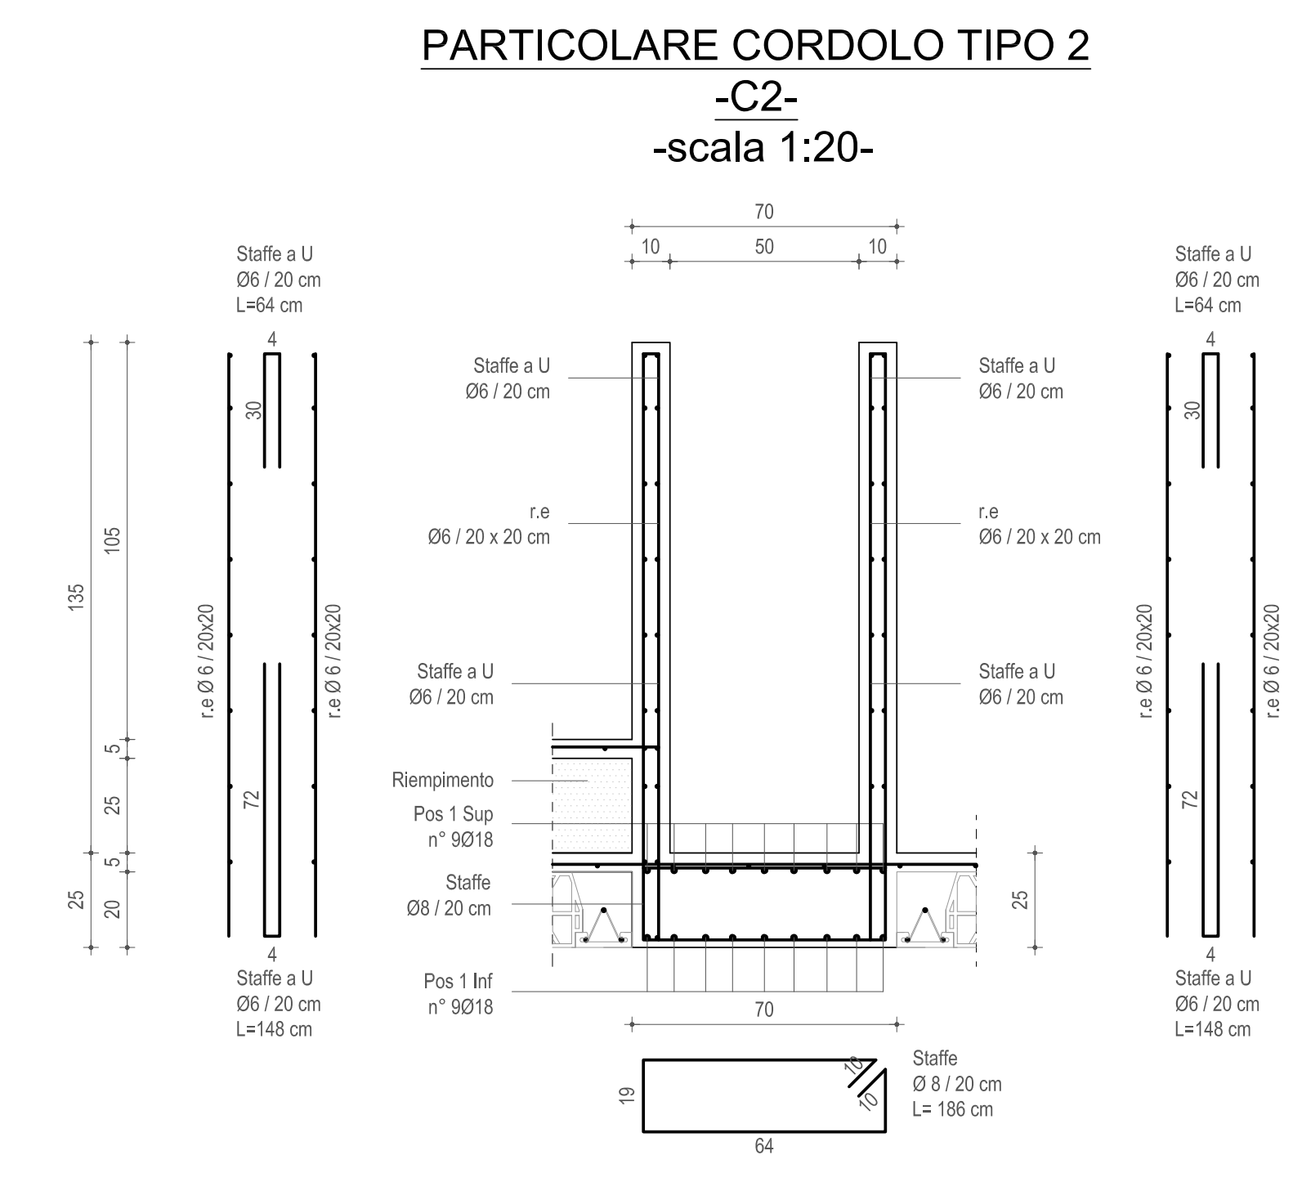

**PARTICOLARE CORDOLO TIPO 2**
-C2-
-scala 1:20-

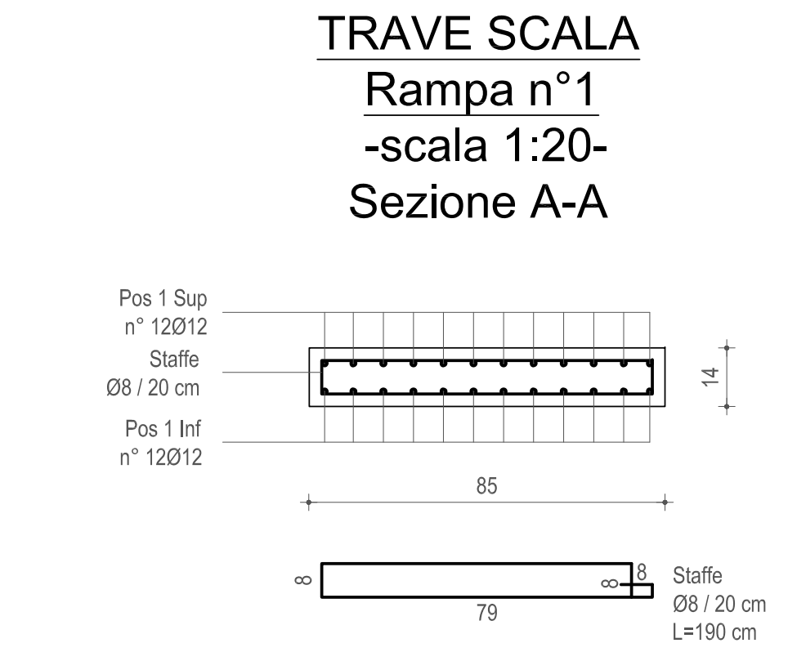

**TRAVE SCALA**
Rampa n°1
-scala 1:20-
Sezione A-A

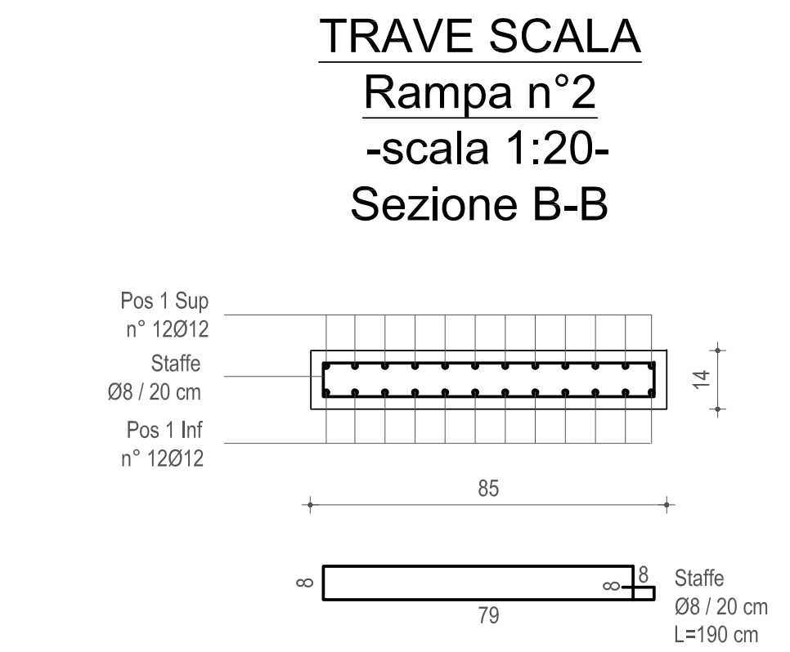

**TRAVE SCALA**
Rampa n°2
-scala 1:20-
Sezione B-B

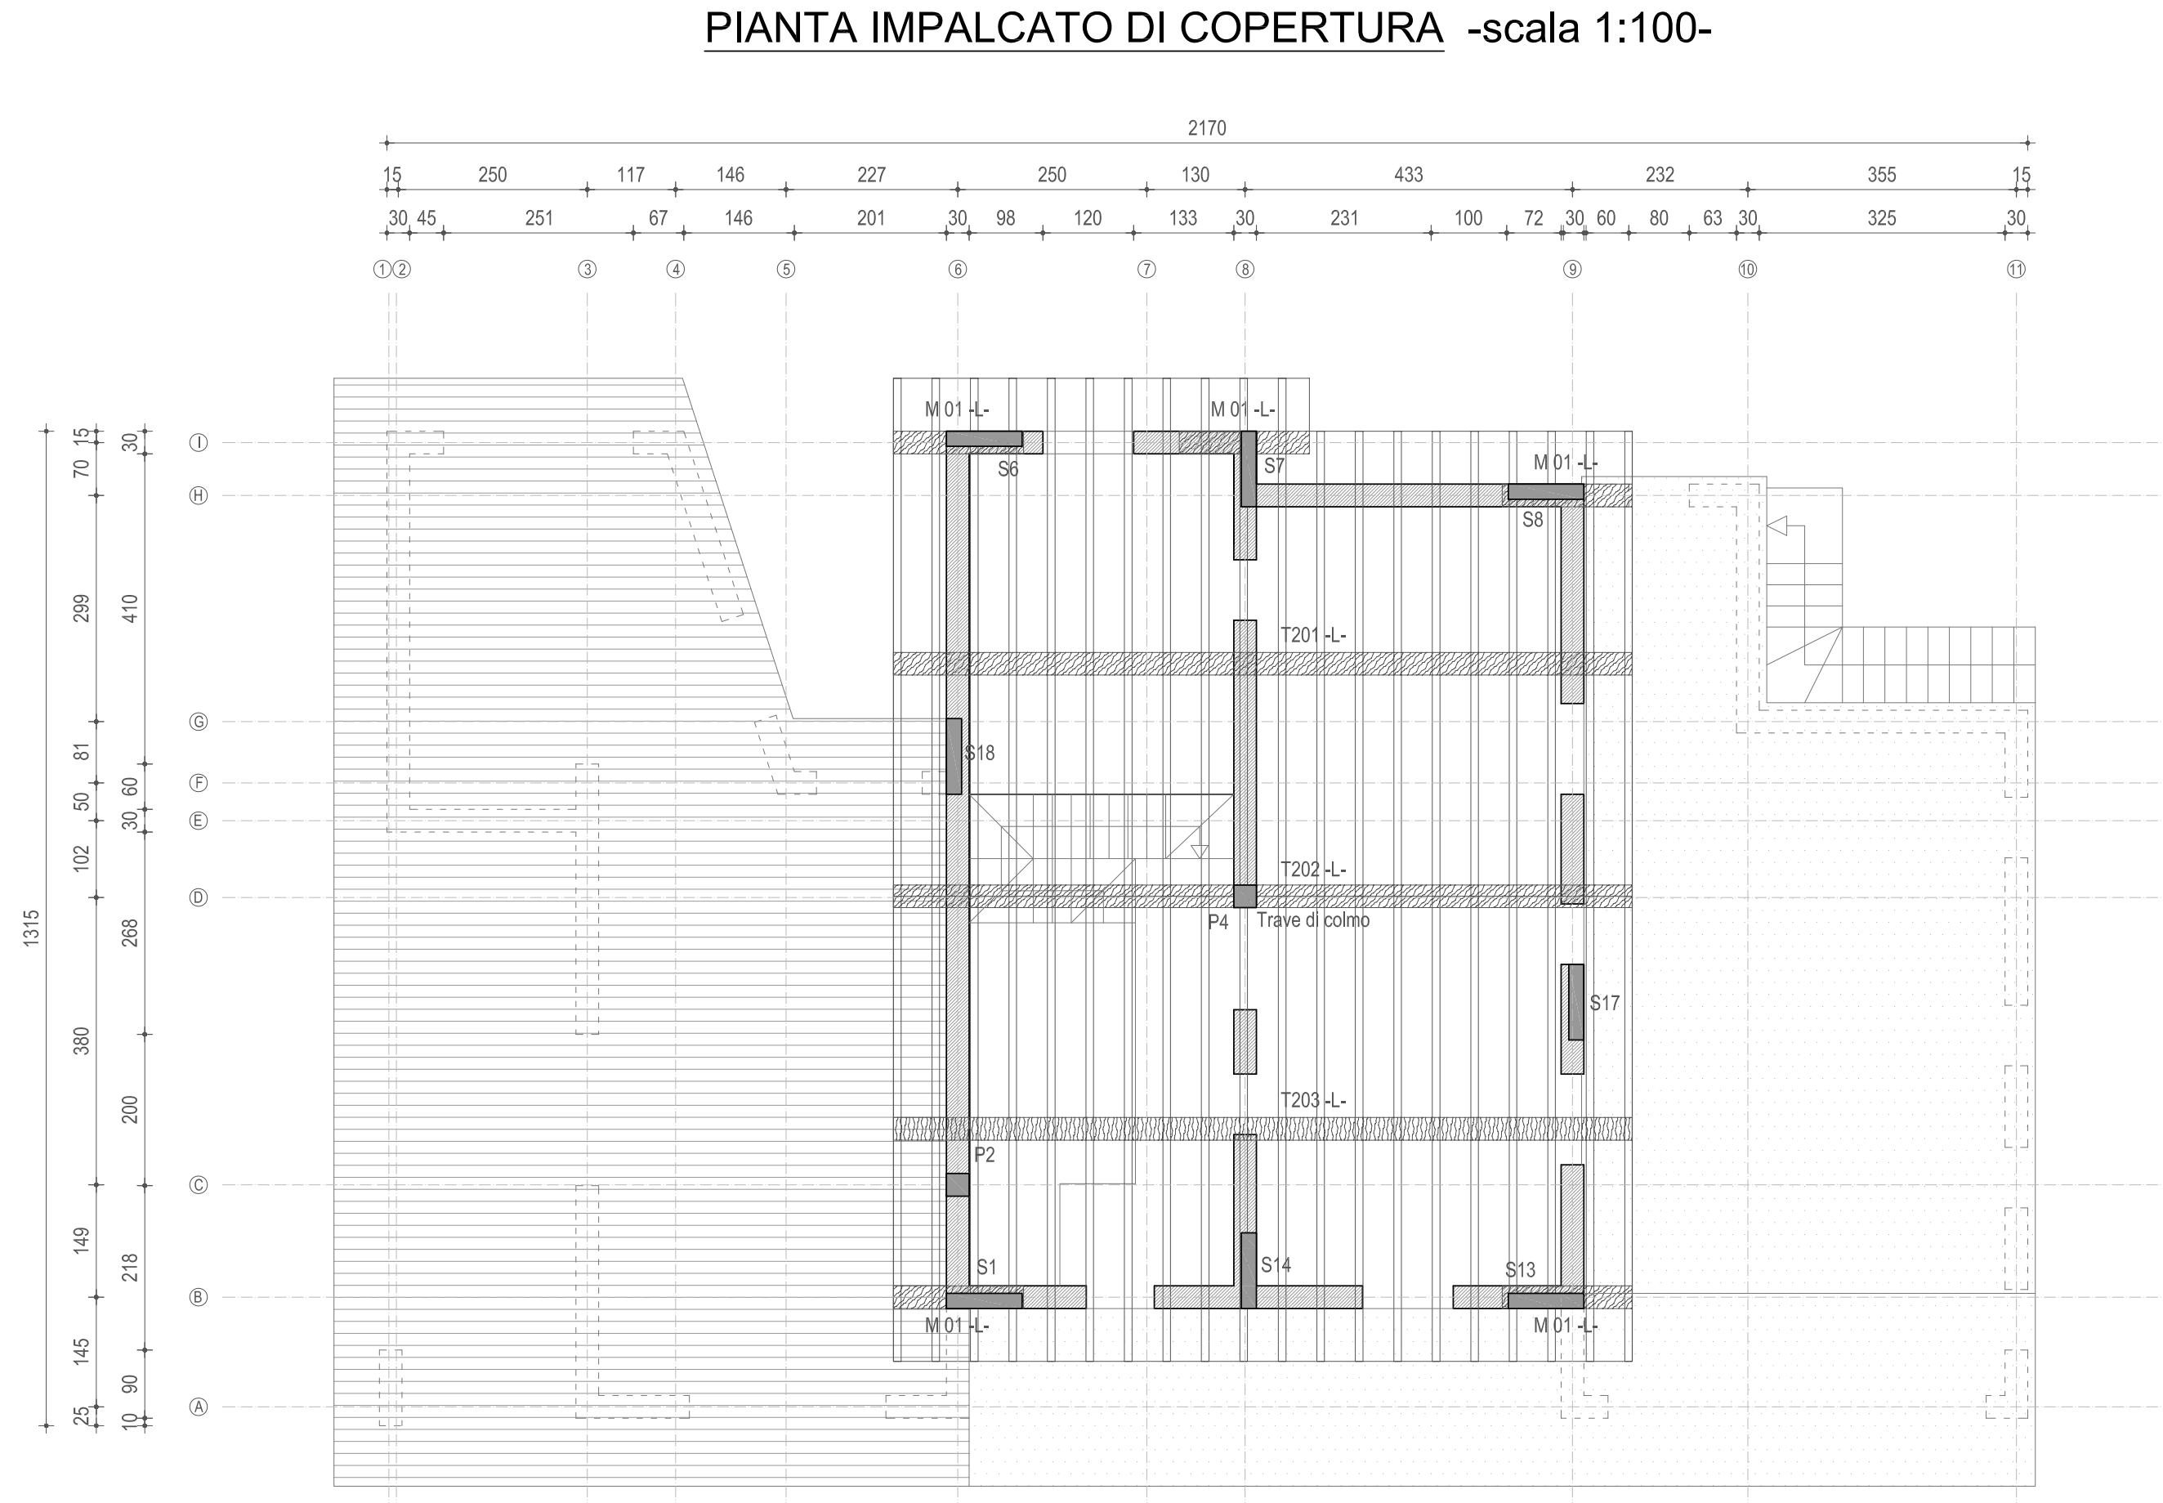

**PIANTA IMPALCATO DI COPERTURA** -scala 1:100-

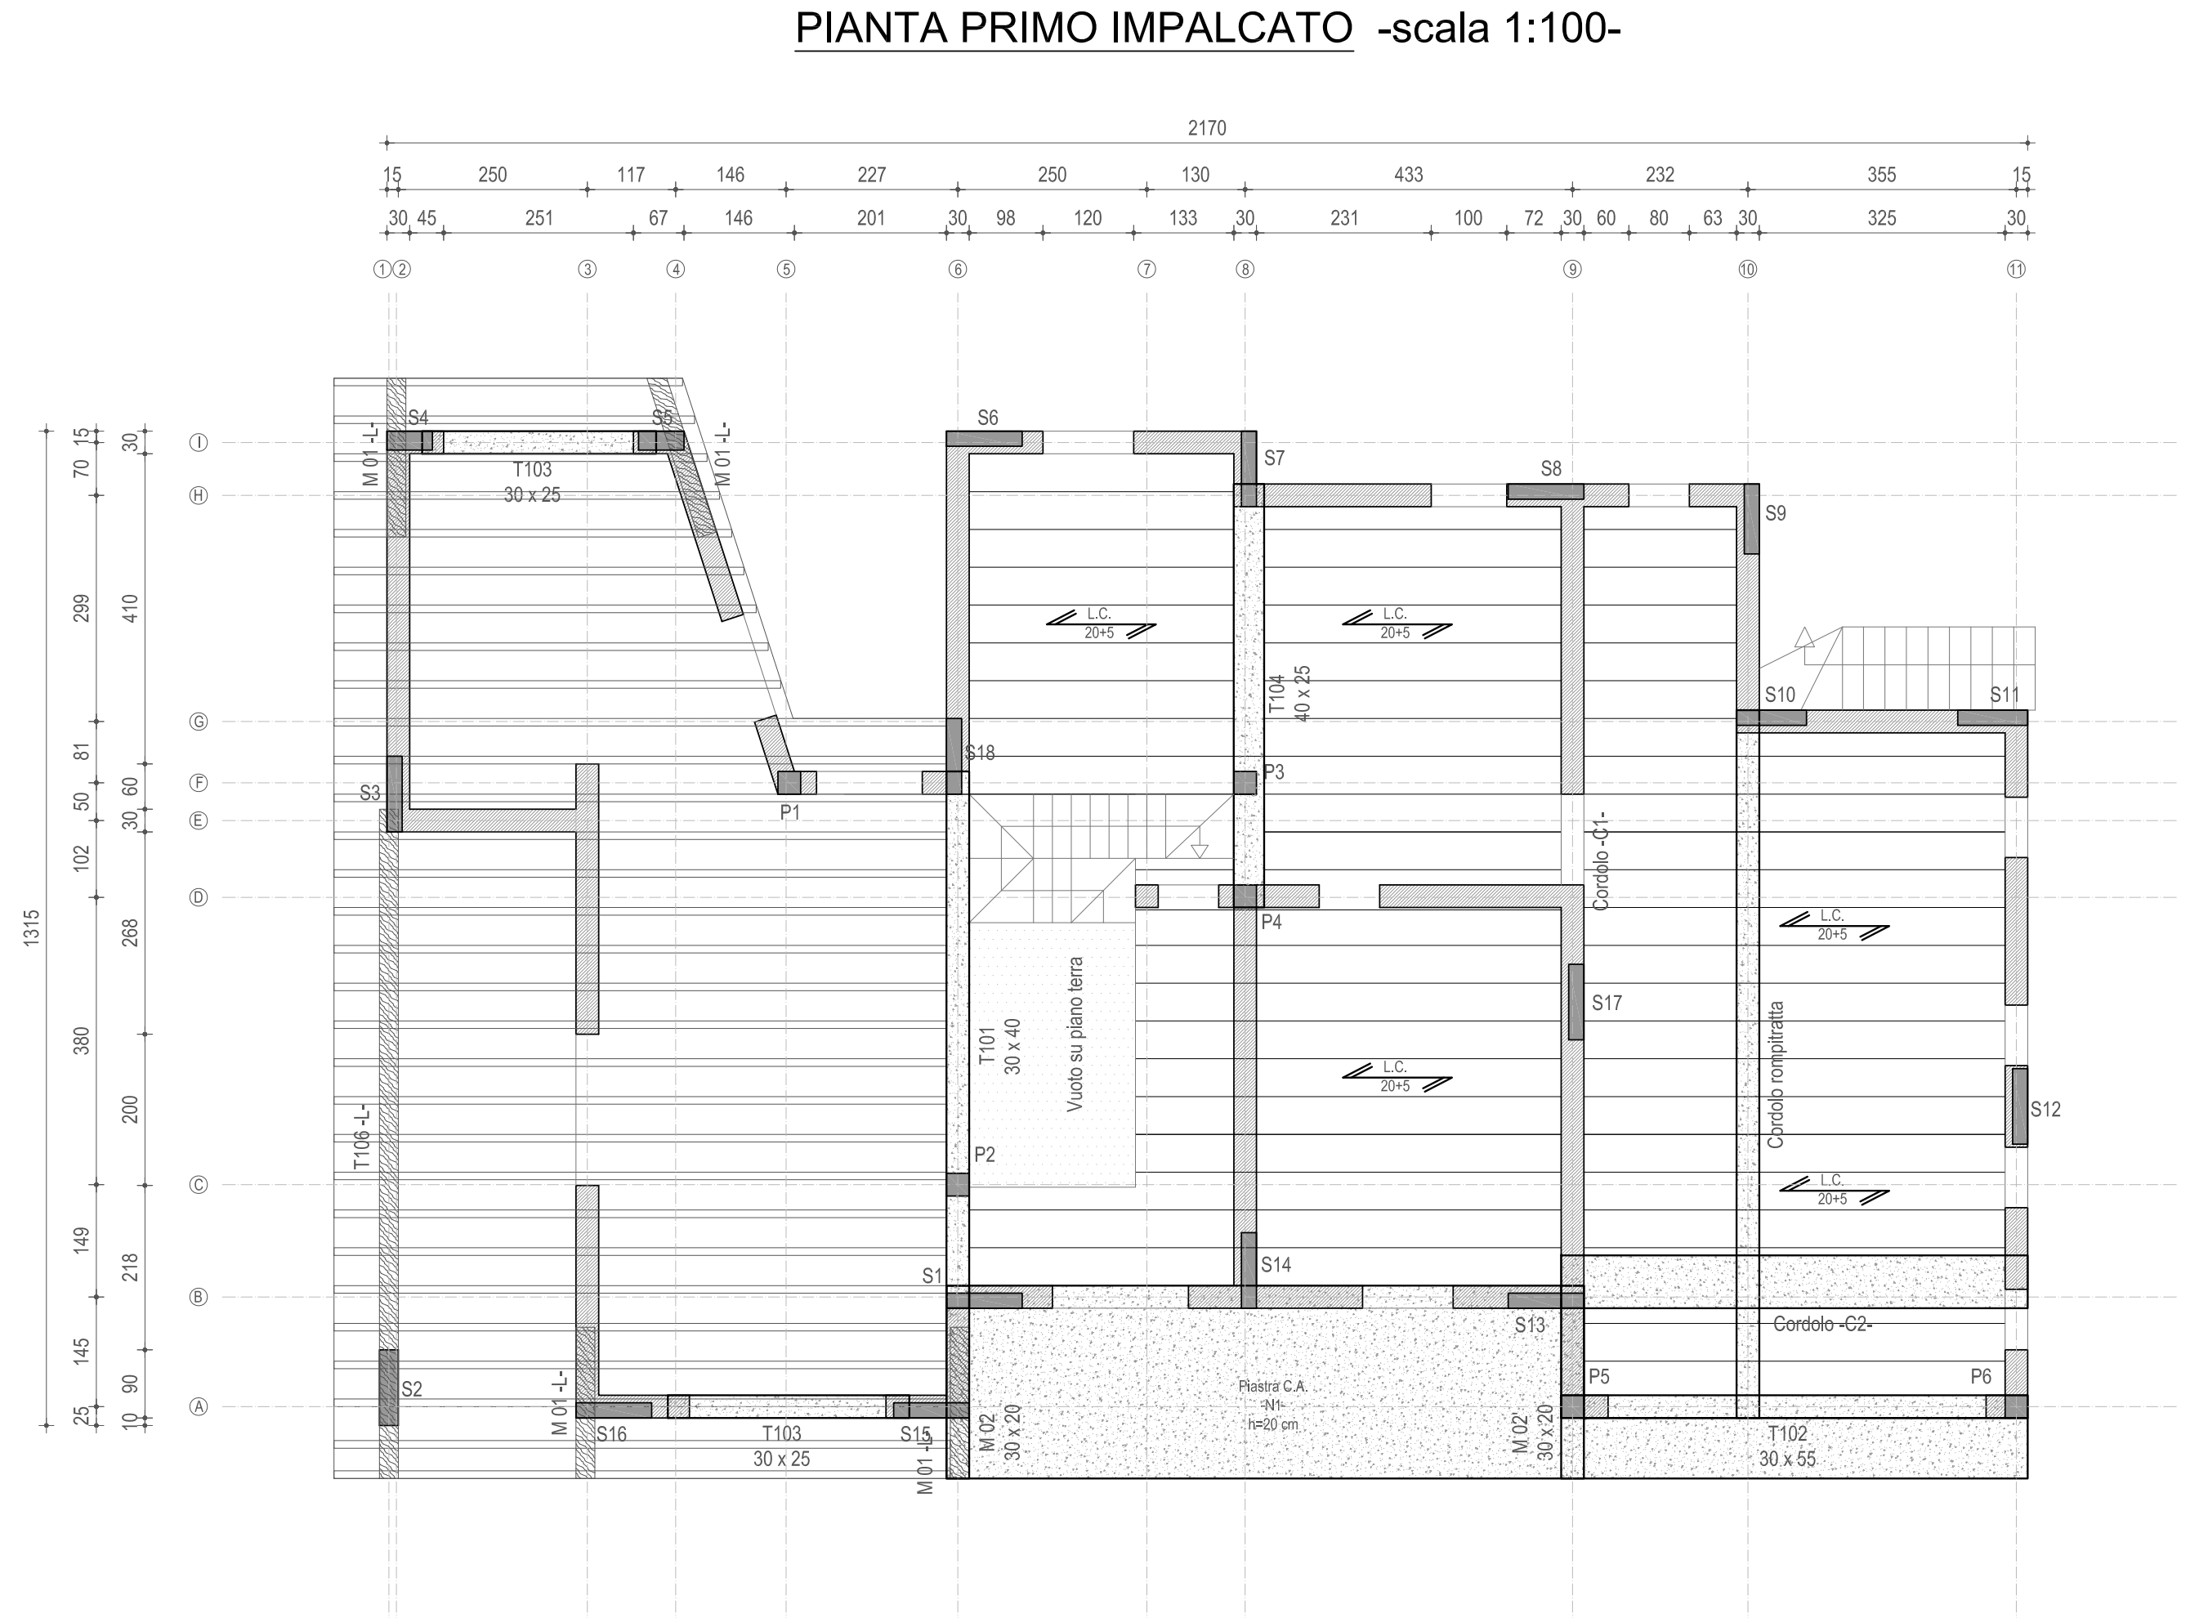

**PIANTA PRIMO IMPALCATO** -scala 1:100-

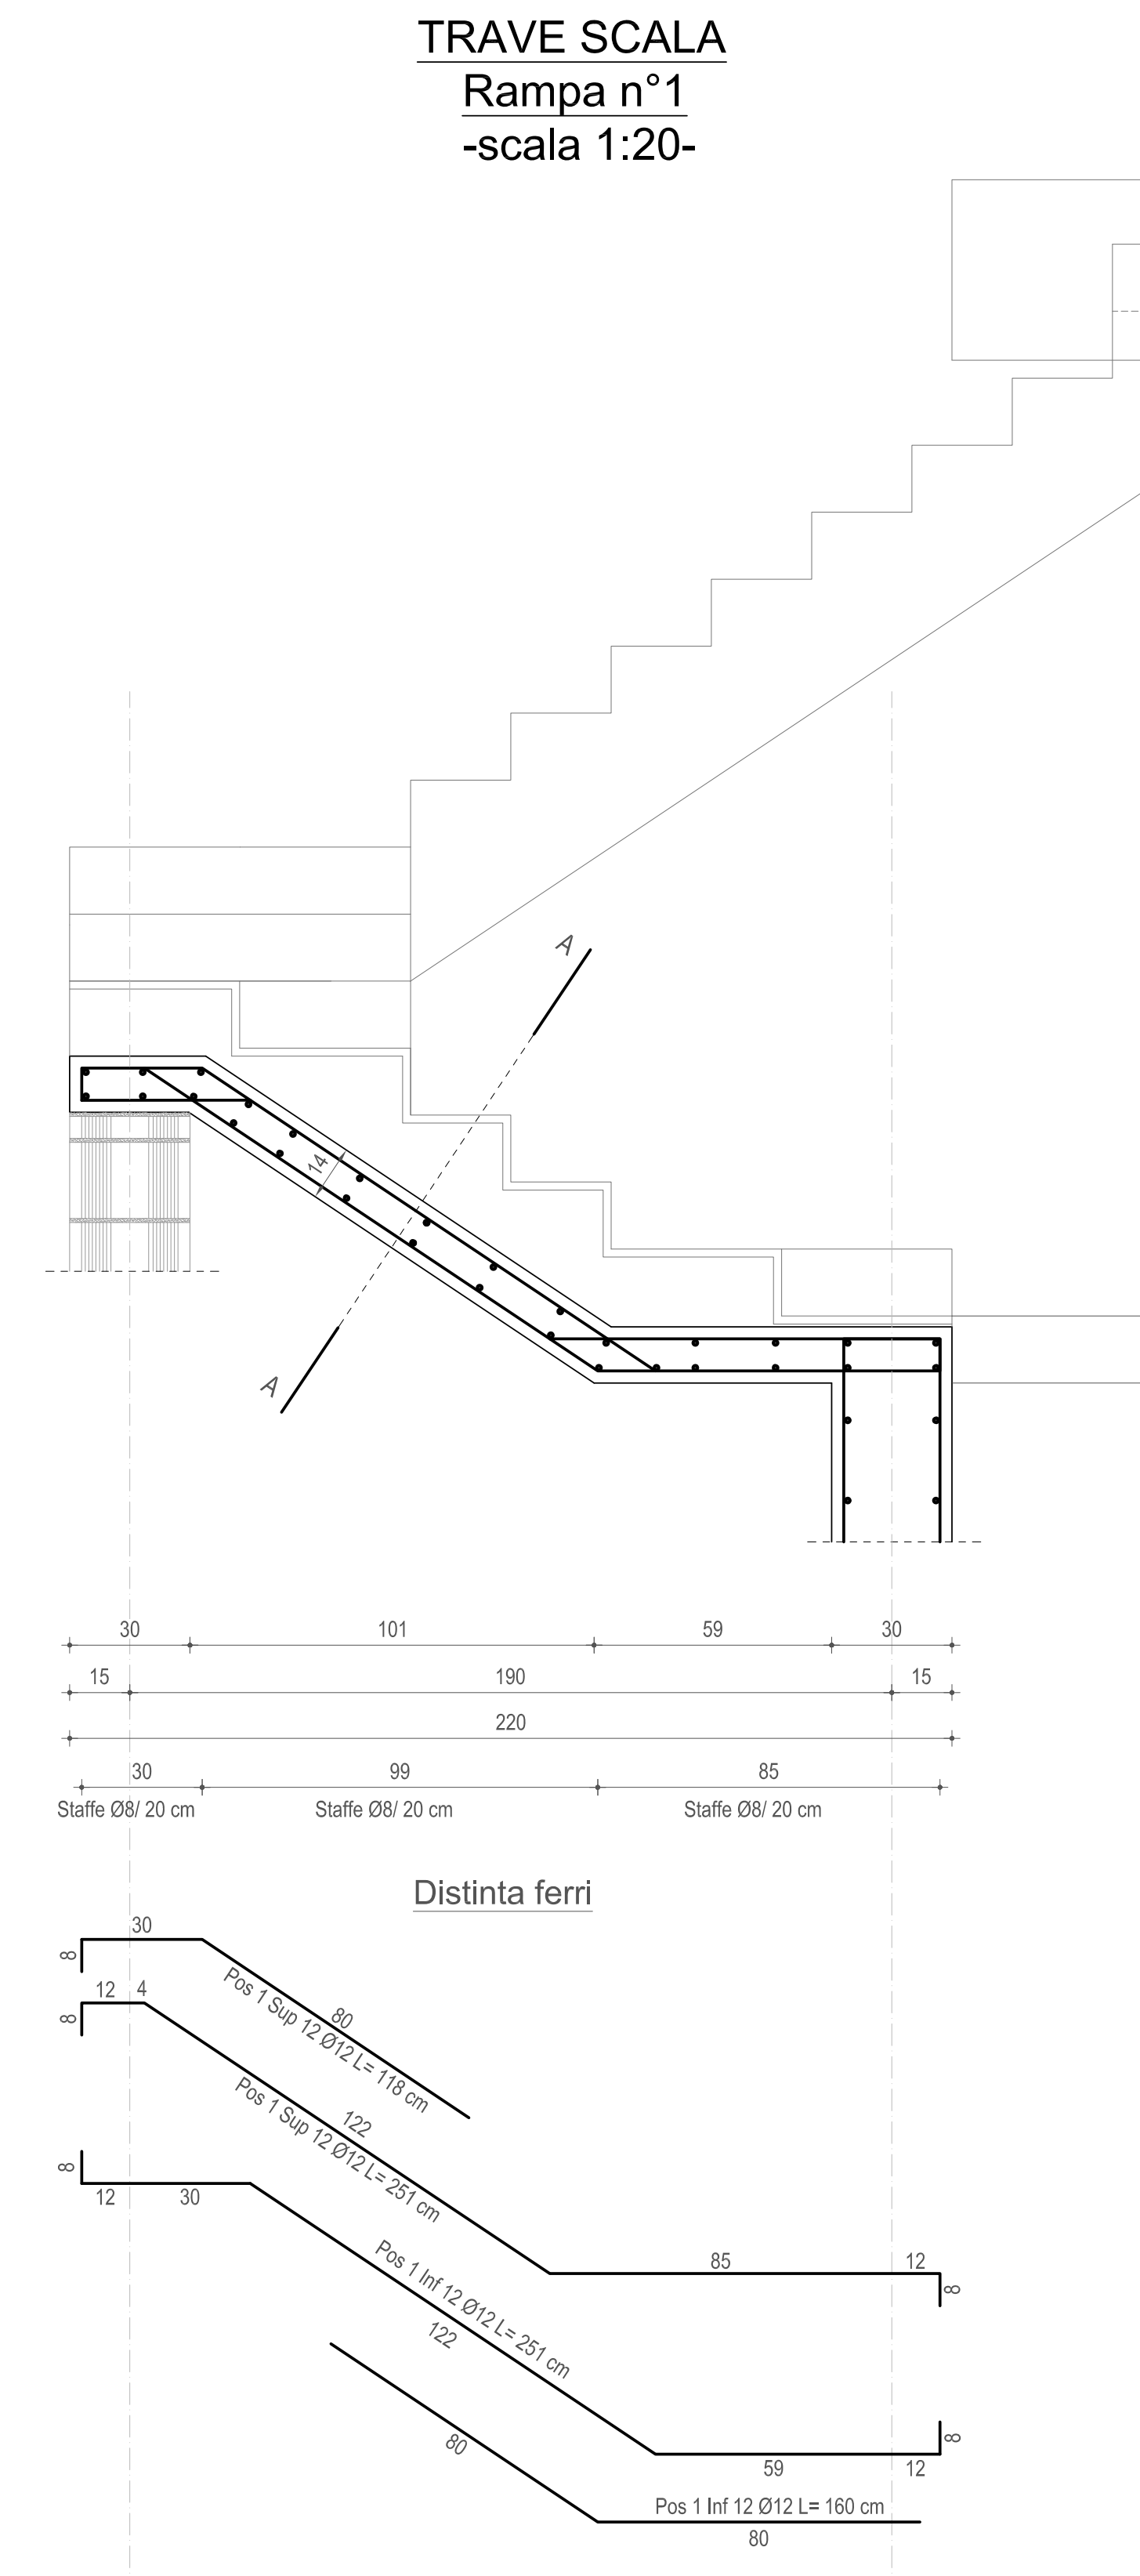

**TRAVE SCALA**
Rampa n°1
-scala 1:20-

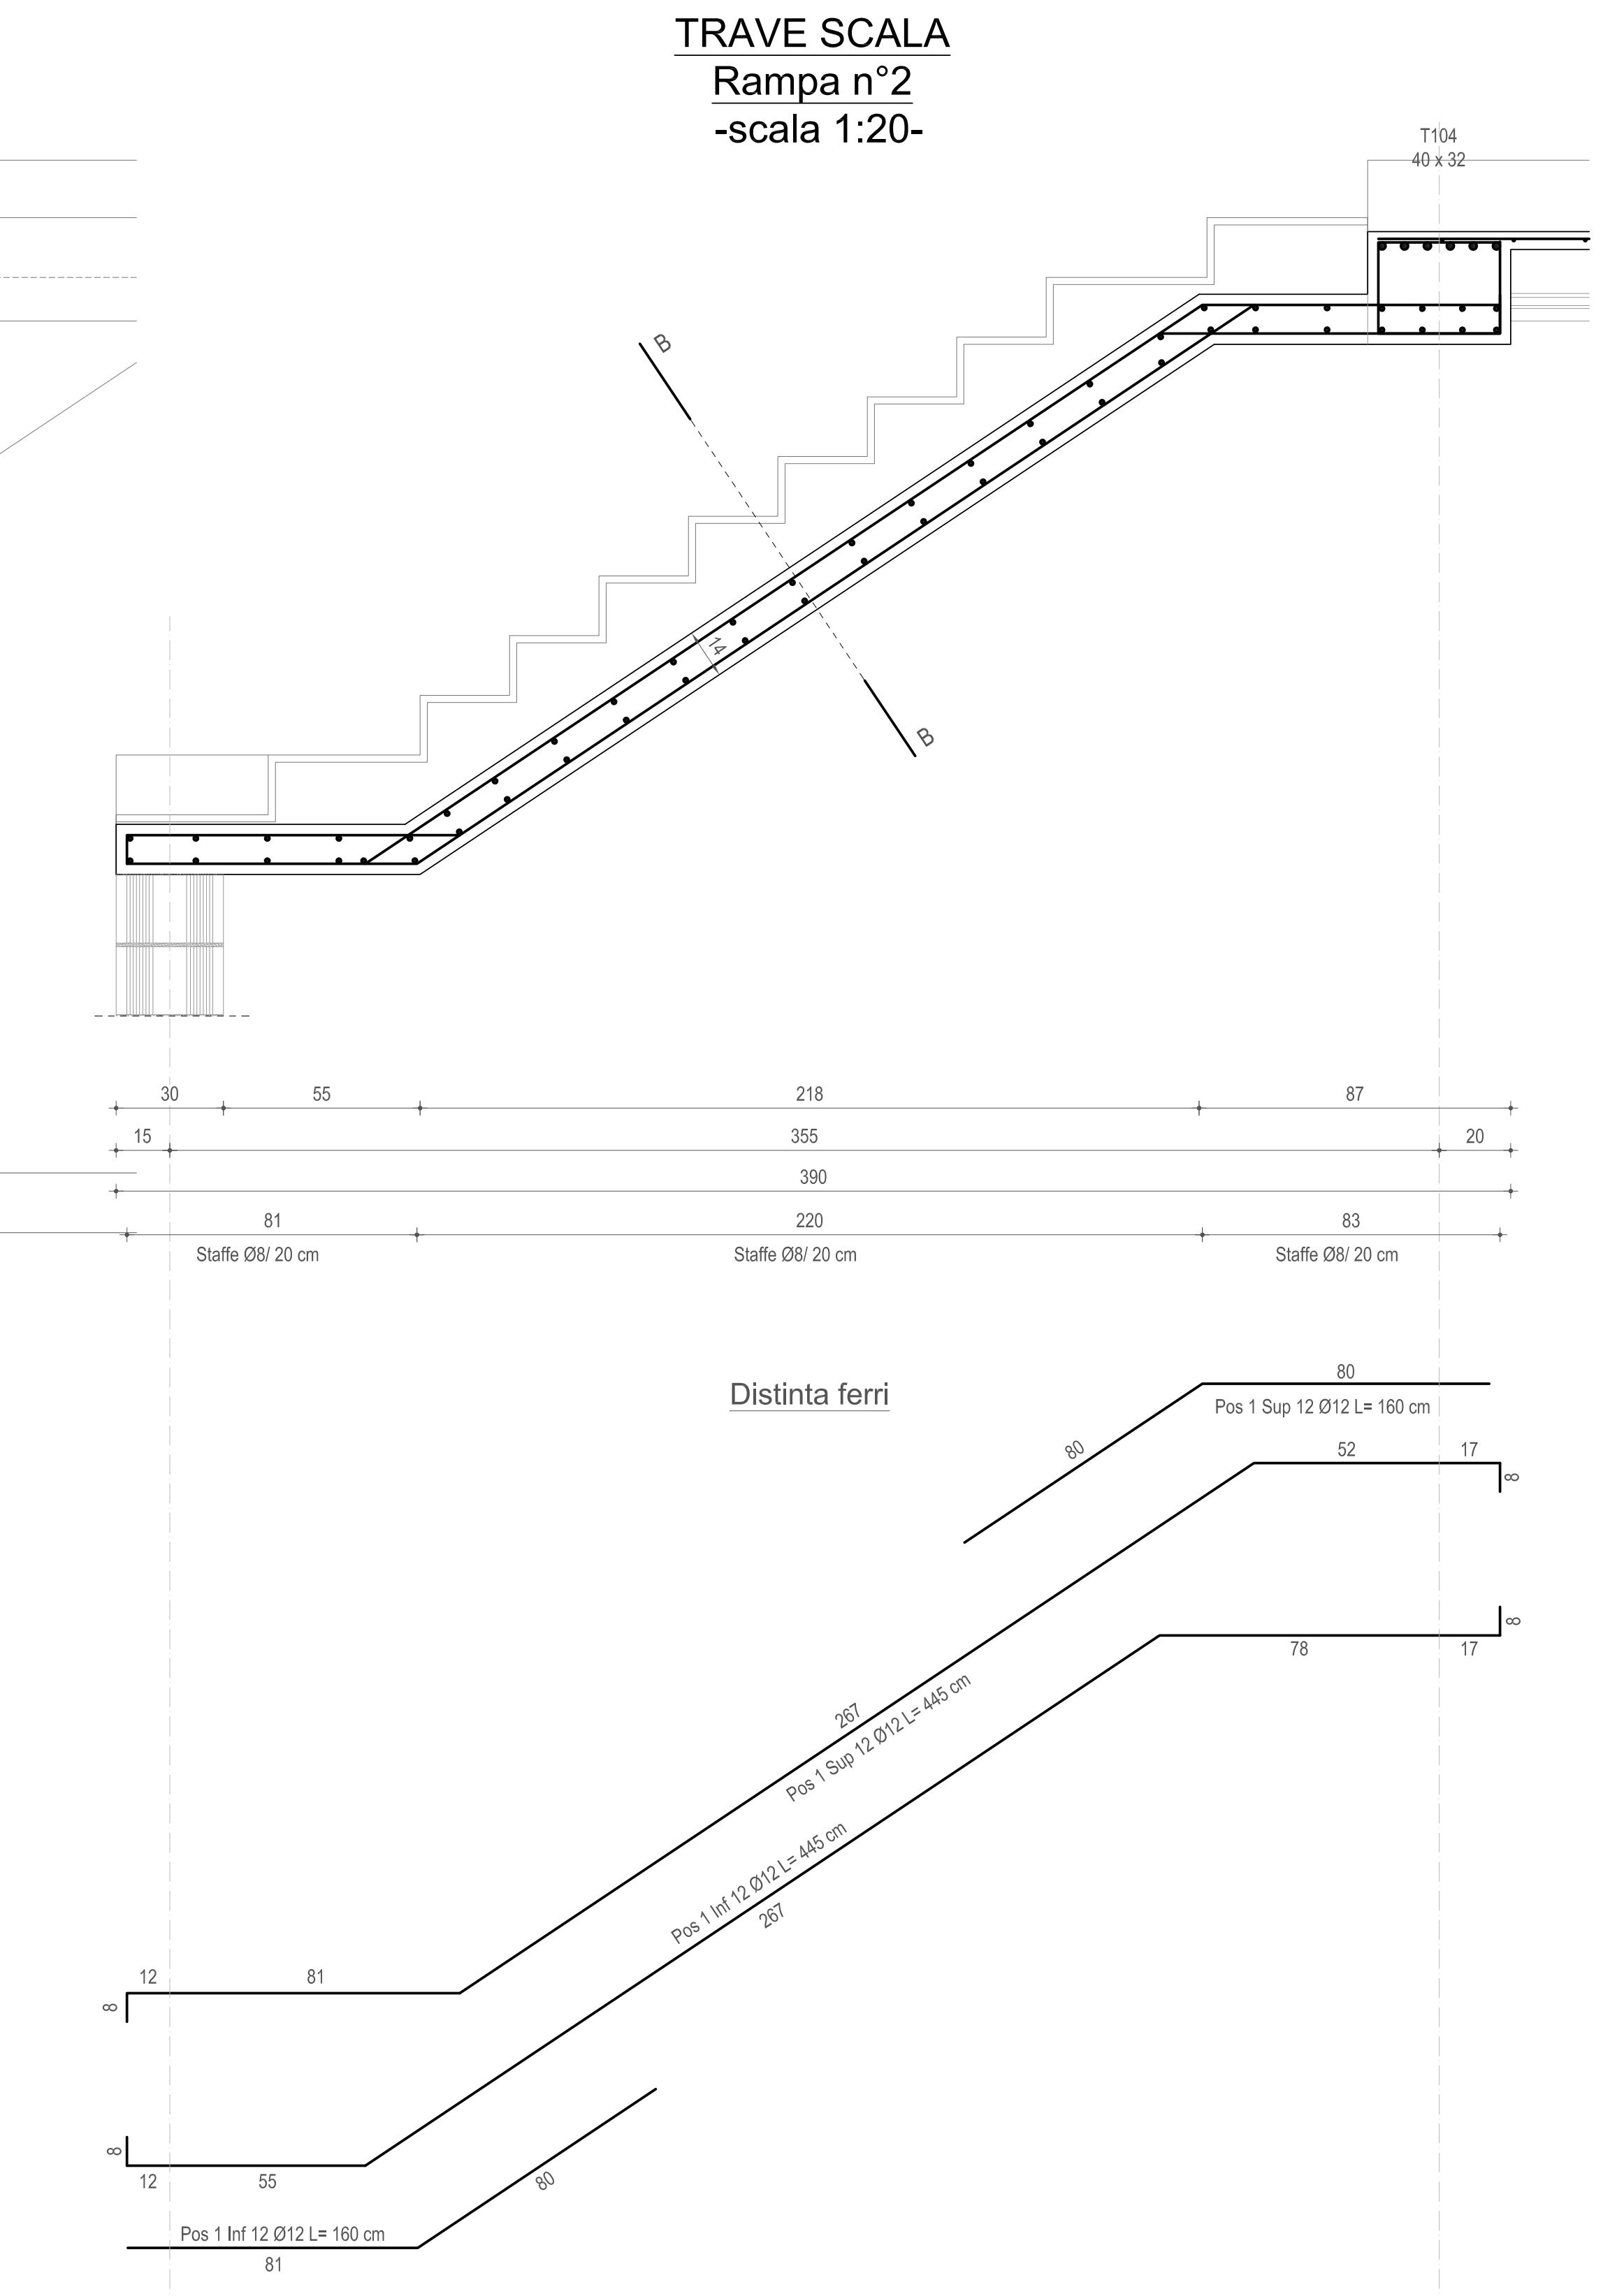

**TRAVE SCALA**
Rampa n°2
-scala 1:20-

## MATERIALI E PRESCRIZIONI

*MATERIALI PRESCRITTI:*

- Calcestruzzo per opere di: Fondazioni

  - Classe di resistenza : C25/30 (Rck 30)
  - Condizioni ambientali: Strutture completamente interrate in terreno permeabile
  - Classe di esposizione : XC2
  - Rapporto massimo acqua/cemento: 0,60
  - Classe di consistenza: S3 (Plastica)
  - Diametro massimo degli aggregati: 16 mm

- Calcestruzzo per opere di: Elevazione e Solai misti laterizio-c.a.
  - Classe di resistenza : C25/30 (Rck 30)
  - Condizioni ambientali: Strutture interne di edifici non industriali con umidità bassa
  - Classe di esposizione : XC1
  - Rapporto massimo acqua/cemento: 0,60
  - Classe di consistenza: S3 (Plastica)
  - Diametro massimo degli aggregati: 16 mm

- Calcestruzzo per opere di: Solette piene in C.A.

  - Classe di resistenza : C28/35 (Rck 35)
  - Condizioni ambientali: Strutture interne di edifici non industriali con umidità bassa
  - Classe di esposizione : XC1
  - Rapporto massimo acqua/cemento: 0,60
  - Classe di consistenza: S3 (Plastica)
  - Diametro massimo degli aggregati: 16 mm

- Acciaio per tutte le strutture: B450 C controllato

*PRESCRIZIONE*

Tutte le misure dovranno essere controllate in cantiere confrontandole con quelle del progetto architettonico e confermate dalla direzione lavori

COMUNE DI VOLTA MANTOVANA PROVINCIA DI MANTOVA

Oggetto

PROGETTO PER LA REALIZZAZIONE DI CASA UNIFAMILIARE.

Co[redacted]

Og[redacted]
- [redacted]
  Travi
  Scala
  Primo impalcato
  Impalcato di copertura

Tav. n° 2

Variante

Data

Scale
1:100, 1:20

Pro[redacted]

[redacted]boratori