PIASTRA -N1-
-scala 1:20-
Piantа

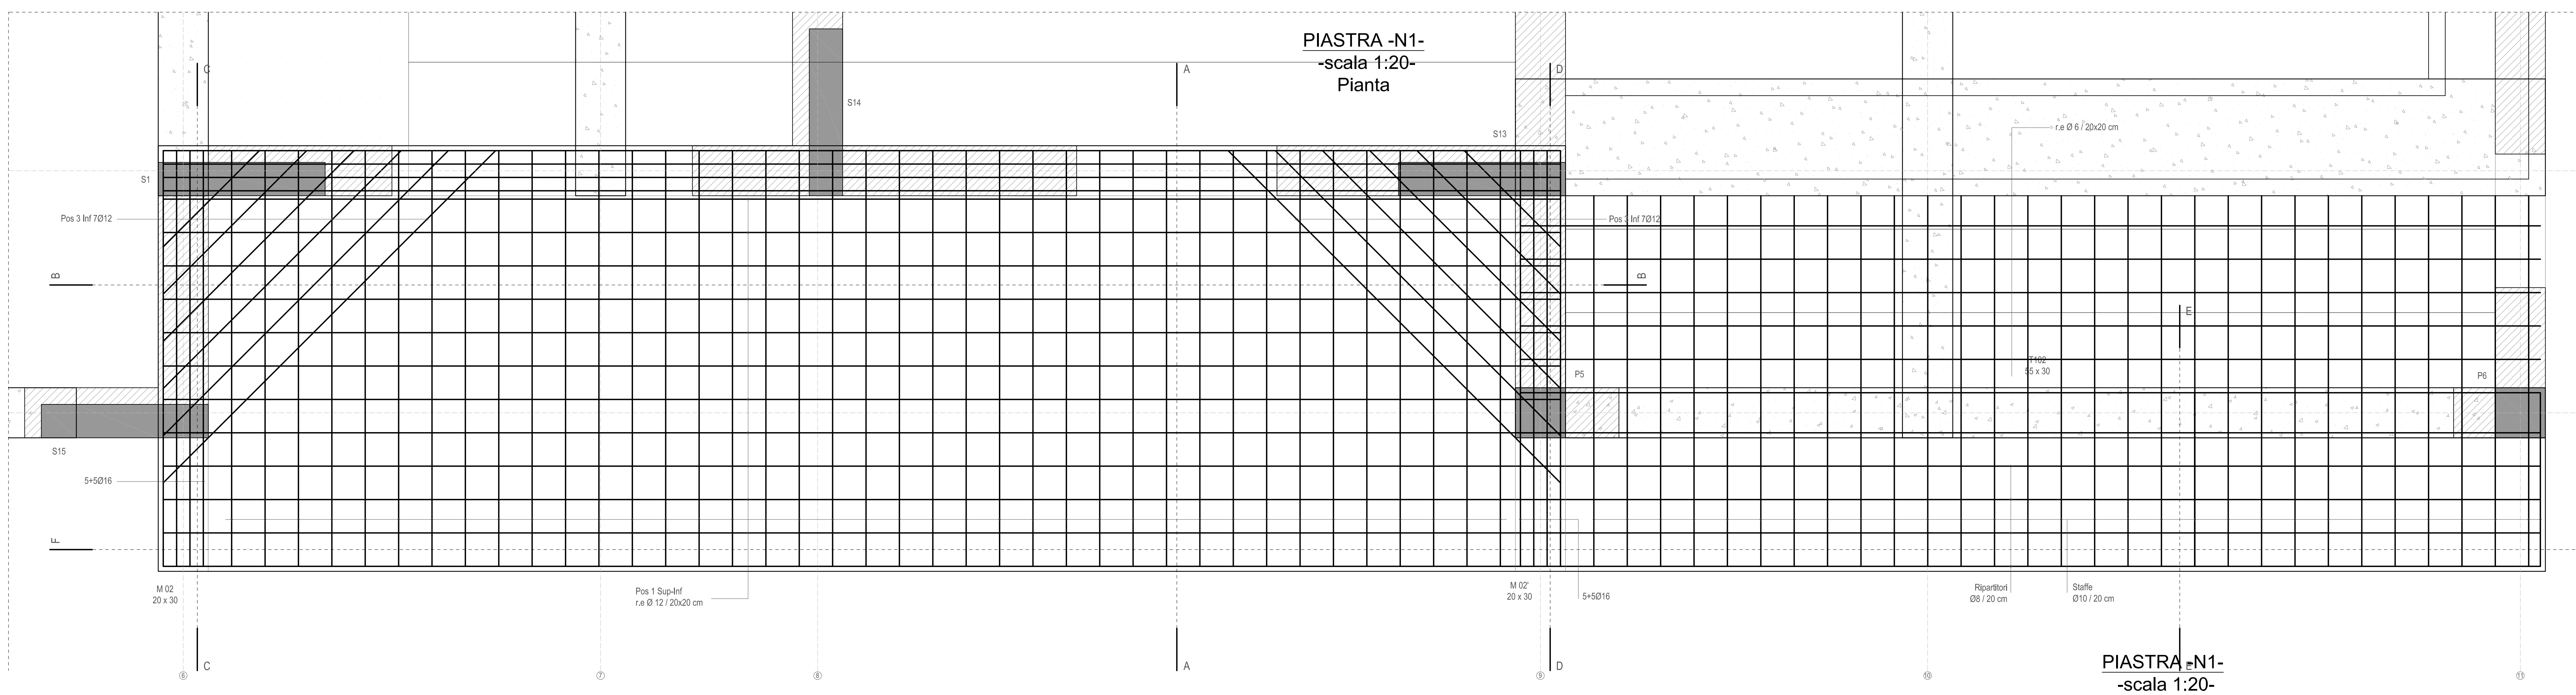

PIASTRA -N1-
-scala 1:20-
Sezione B-B

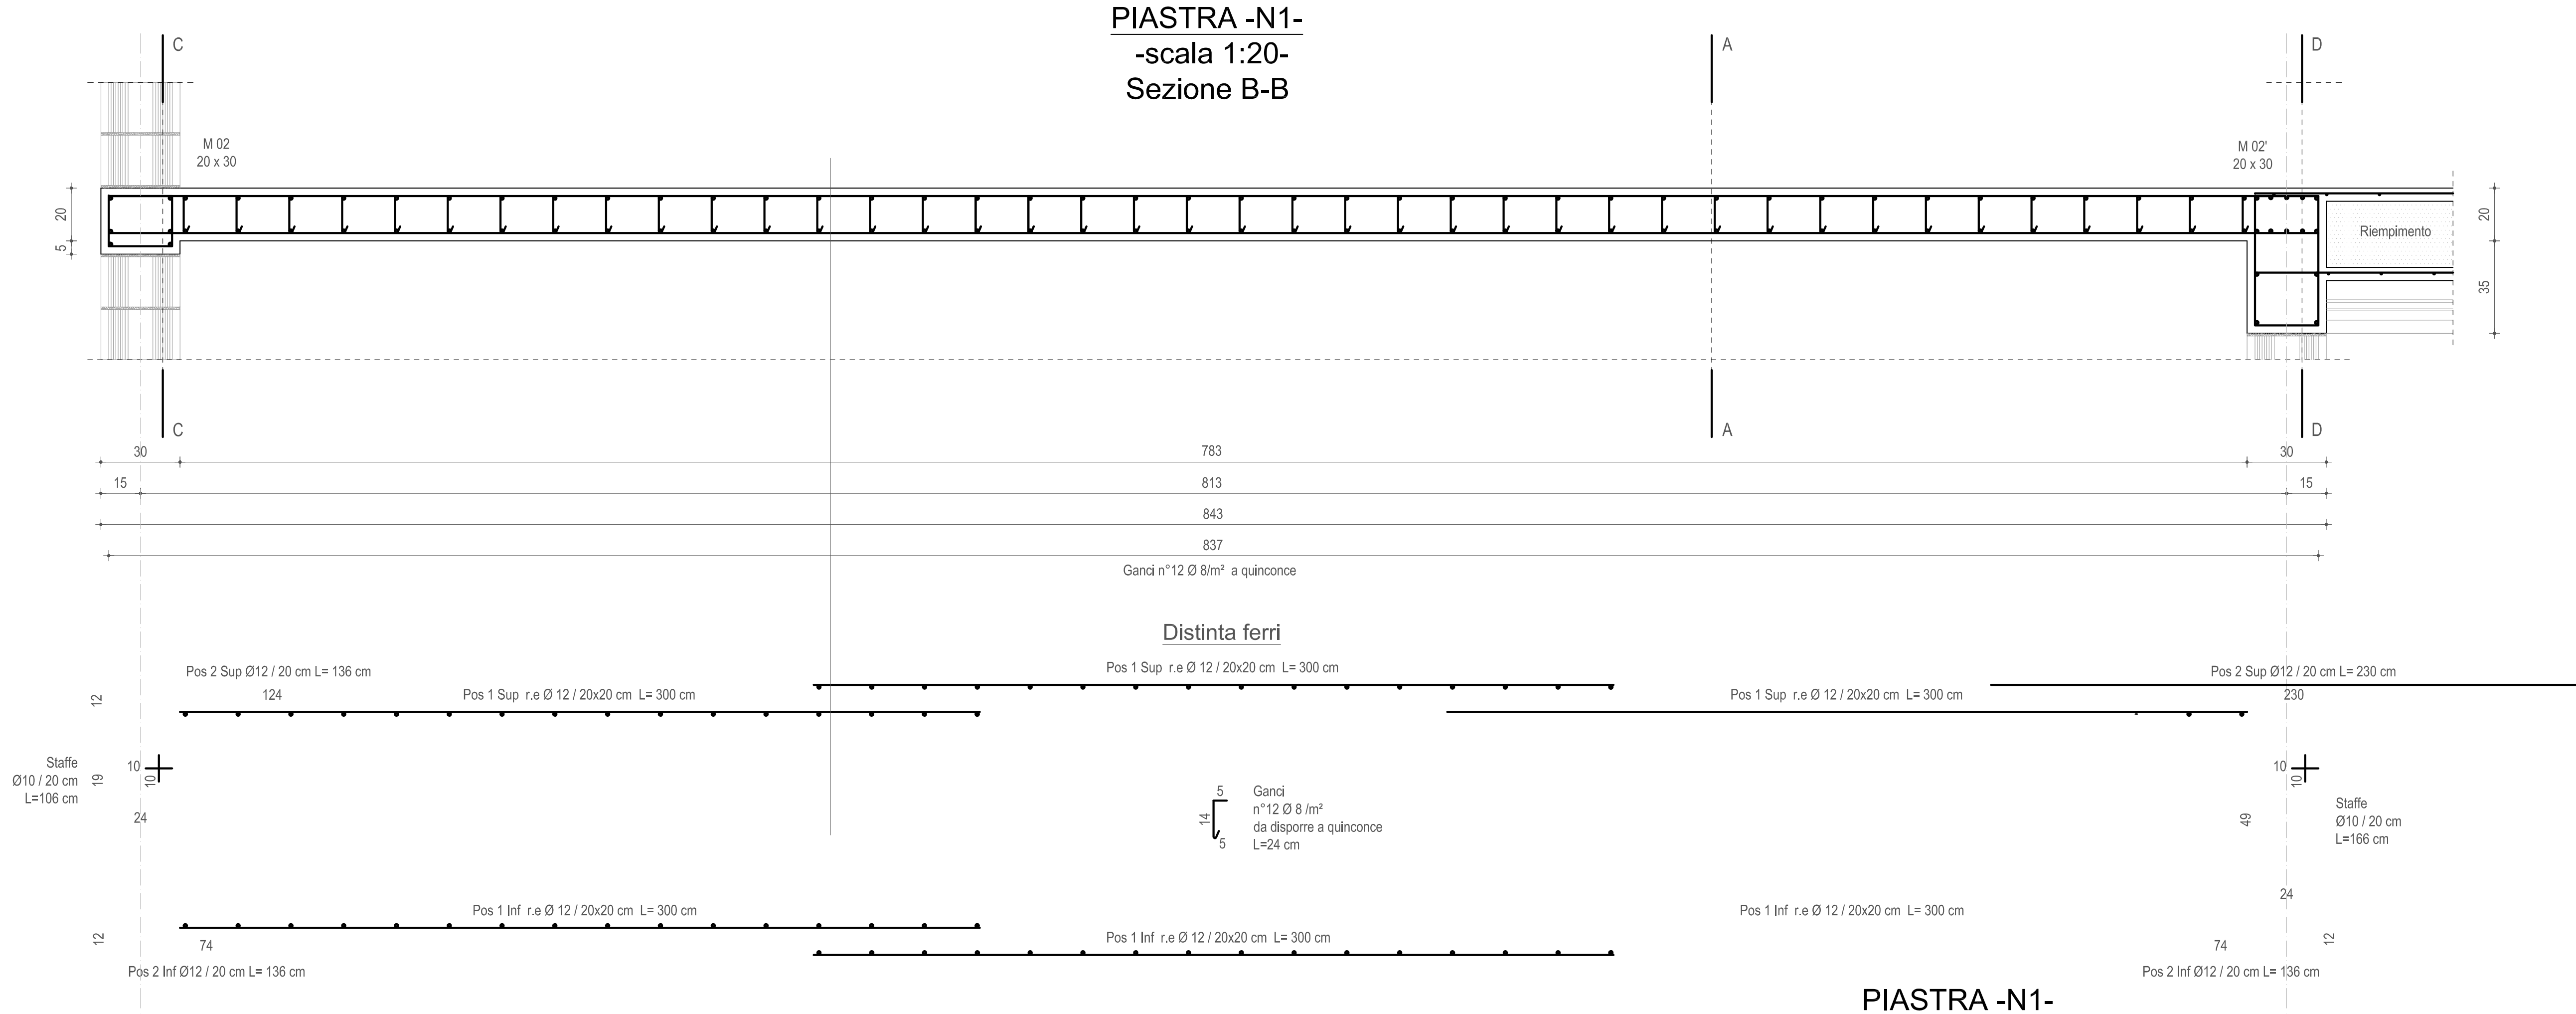
M 02
20 x 30
M 02'
20 x 30
Riempimento
C
A
D
30
783
30
15
813
15
843
837
Ganci n°12 Ø 8/m² a quinconce
Distinta ferri
Pos 2 Sup Ø12 / 20 cm L= 136 cm
124
Pos 1 Sup r.e Ø 12 / 20x20 cm L= 300 cm
Pos 1 Sup r.e Ø 12 / 20x20 cm L= 300 cm
Pos 1 Sup r.e Ø 12 / 20x20 cm L= 300 cm
Pos 2 Sup Ø12 / 20 cm L= 230 cm
230
Staffe
Ø10 / 20 cm
L=106 cm
Ganci
n°12 Ø 8 /m²
da disporre a quinconce
L=24 cm
Staffe
Ø10 / 20 cm
L=166 cm
Pos 1 Inf r.e Ø 12 / 20x20 cm L= 300 cm
Pos 1 Inf r.e Ø 12 / 20x20 cm L= 300 cm
Pos 1 Inf r.e Ø 12 / 20x20 cm L= 300 cm
74
Pos 2 Inf Ø12 / 20 cm L= 136 cm
Pos 2 Inf Ø12 / 20 cm L= 136 cm

PIASTRA -N1-
-scala 1:20-
Sezione A-A

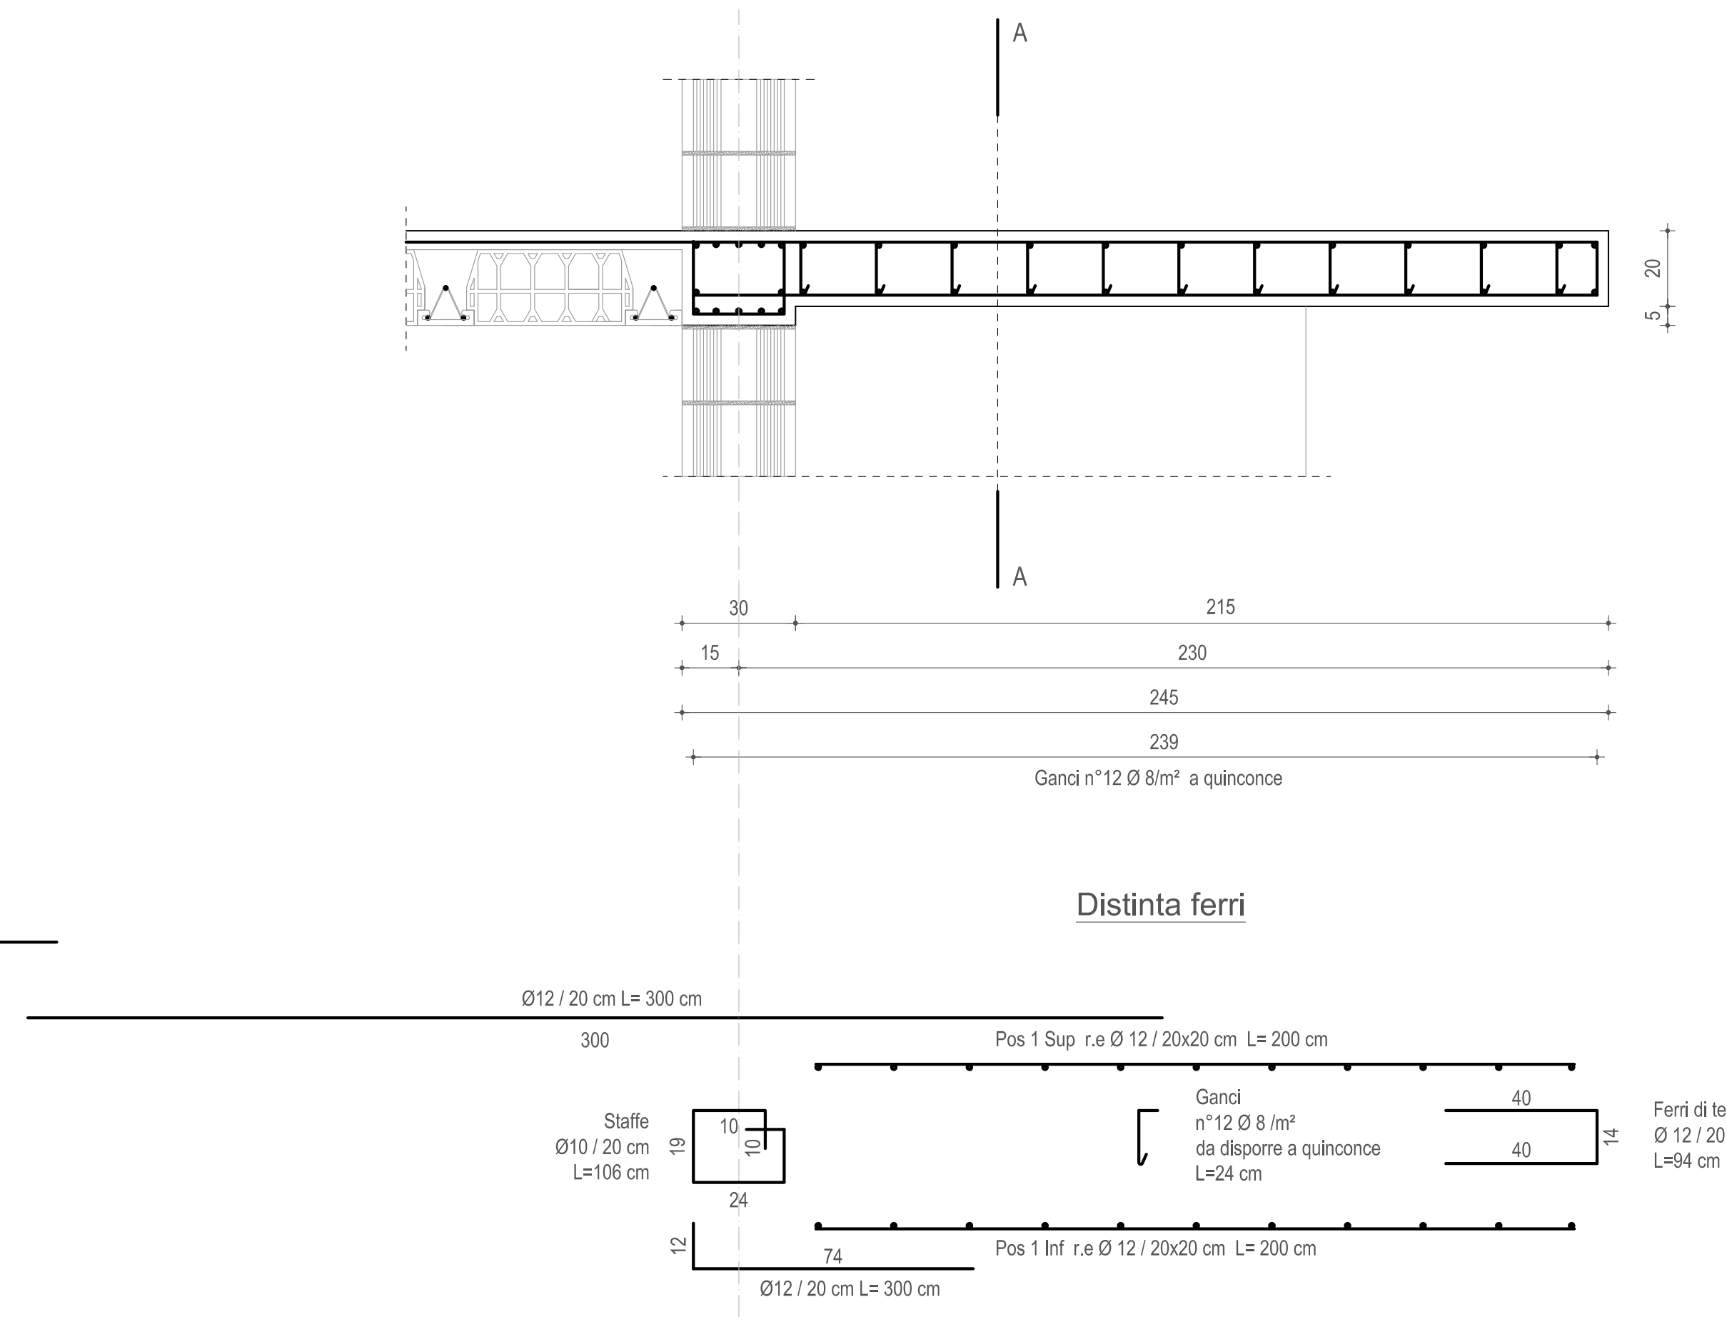

TRAVE -M2-
-scala 1:20-
Sezione C-C

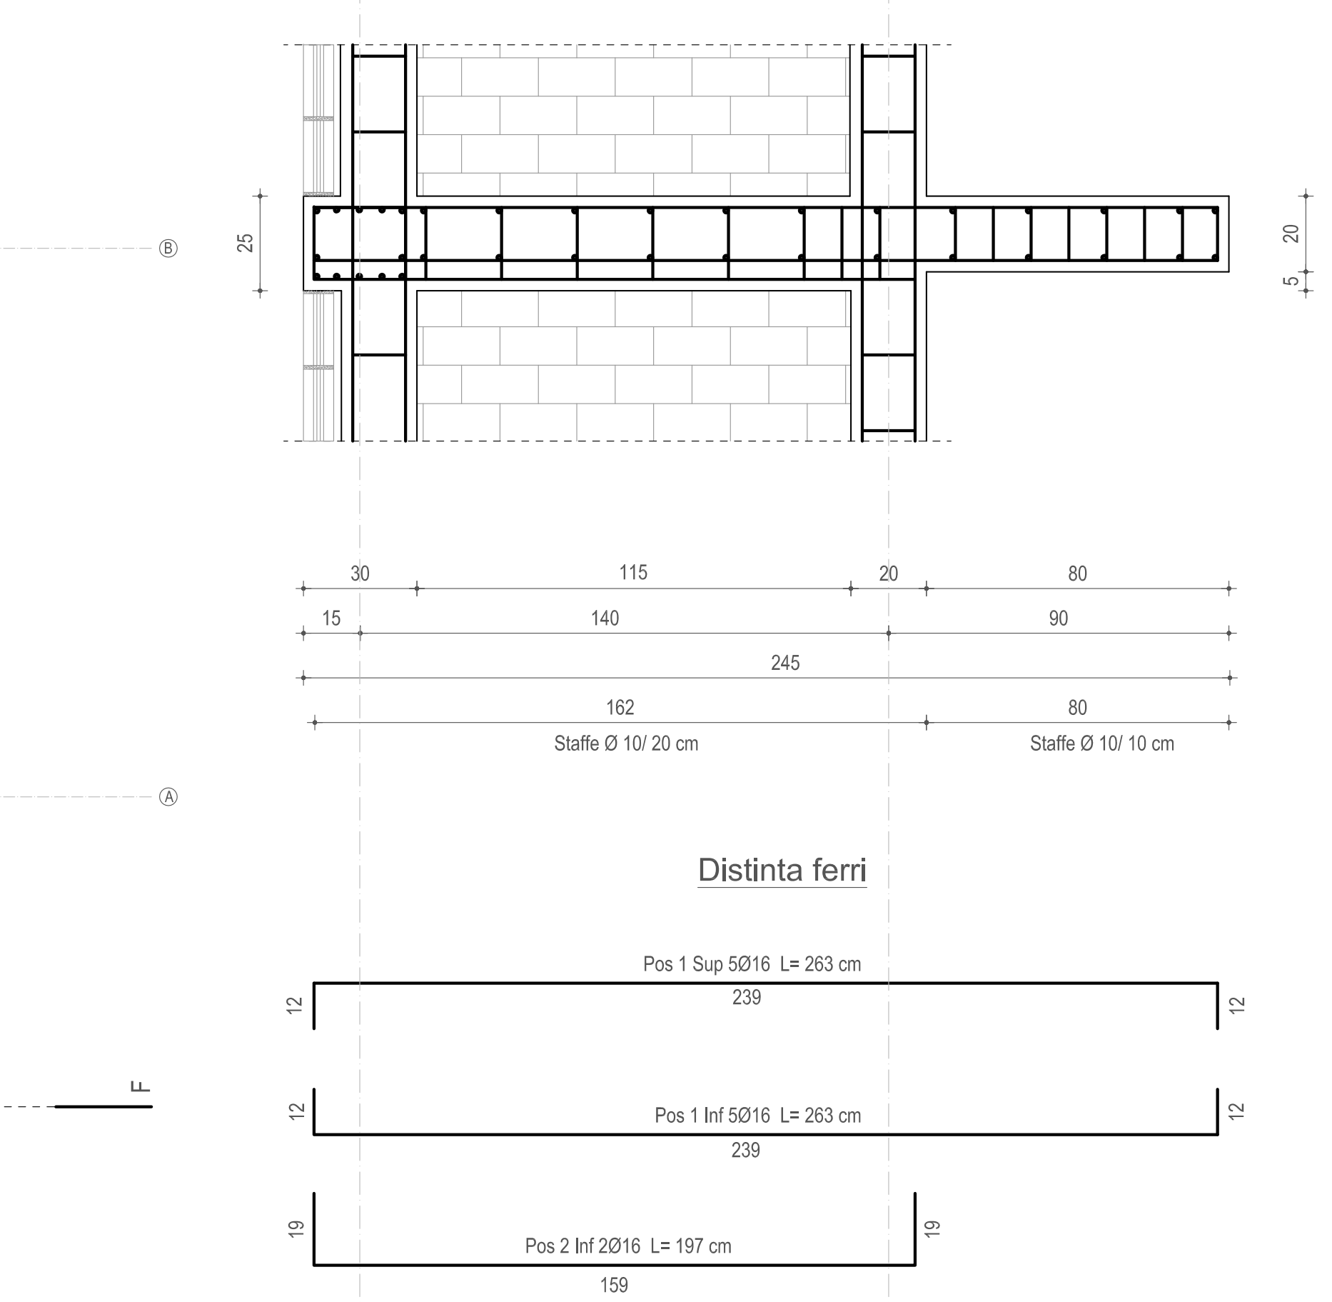

TRAVE -M2'-
-scala 1:20-
Sezione D-D

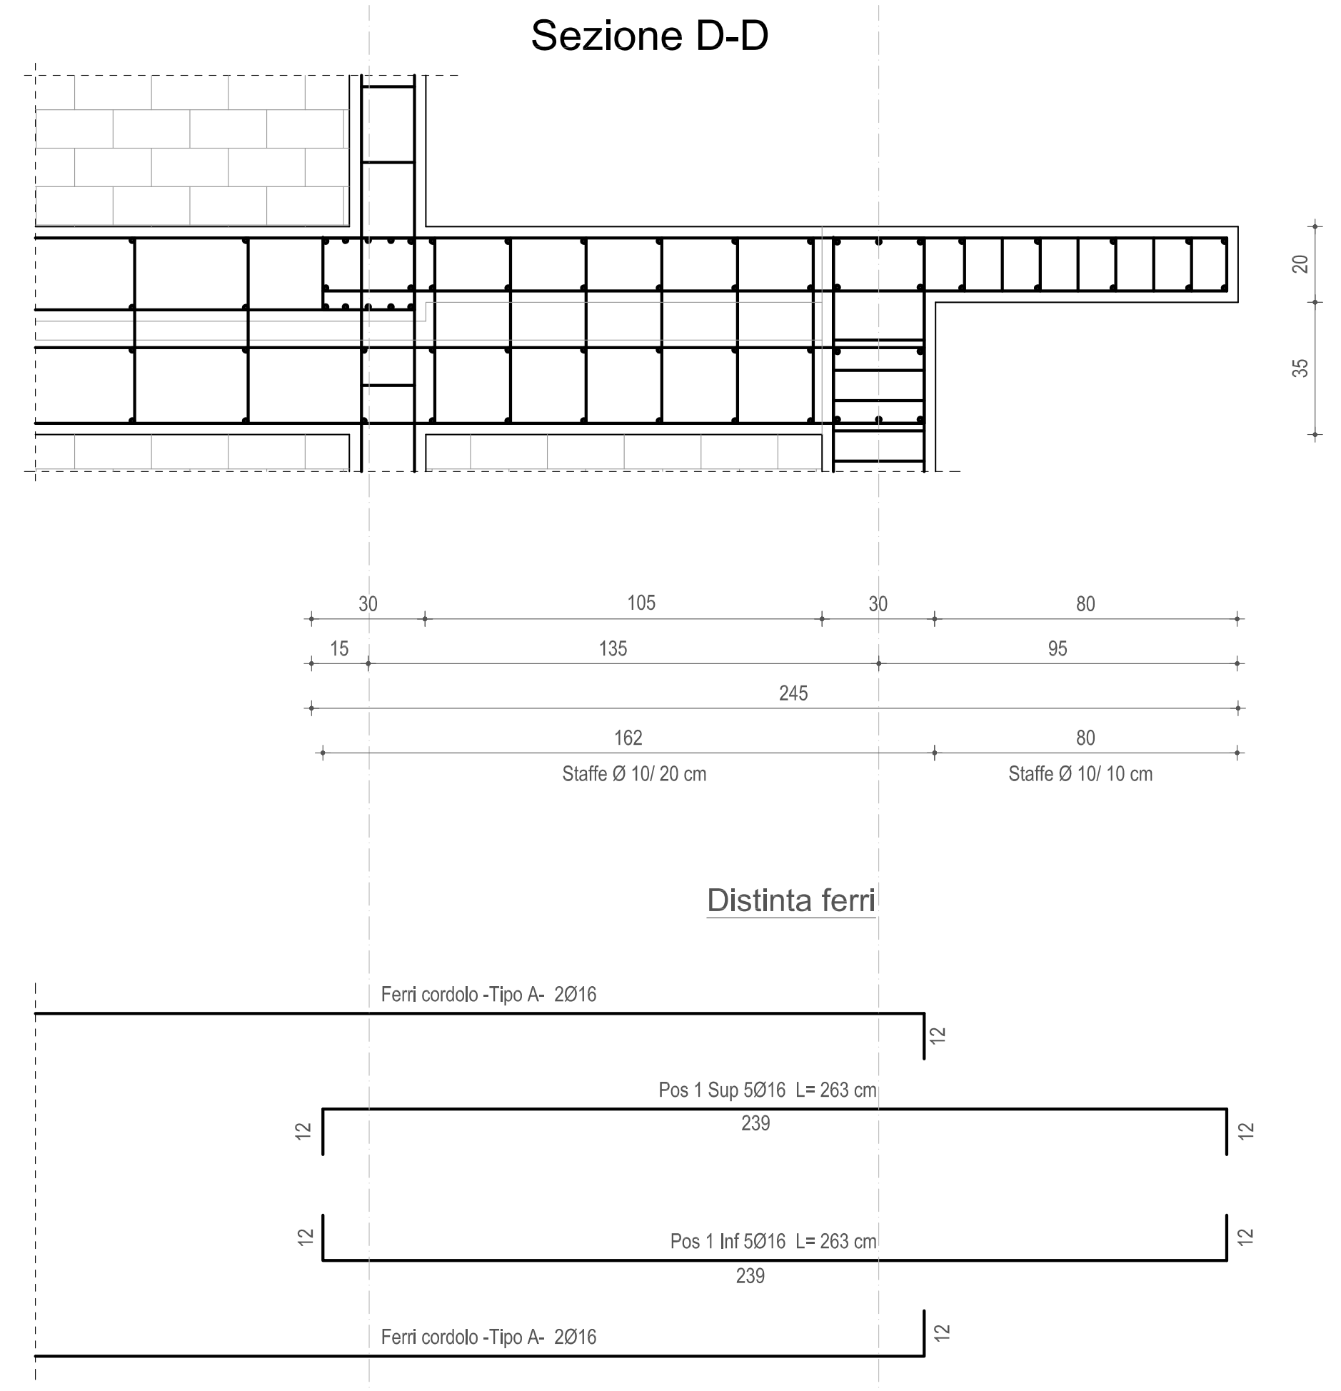

PIASTRA -N1-
-scala 1:20-
Sezione F-F

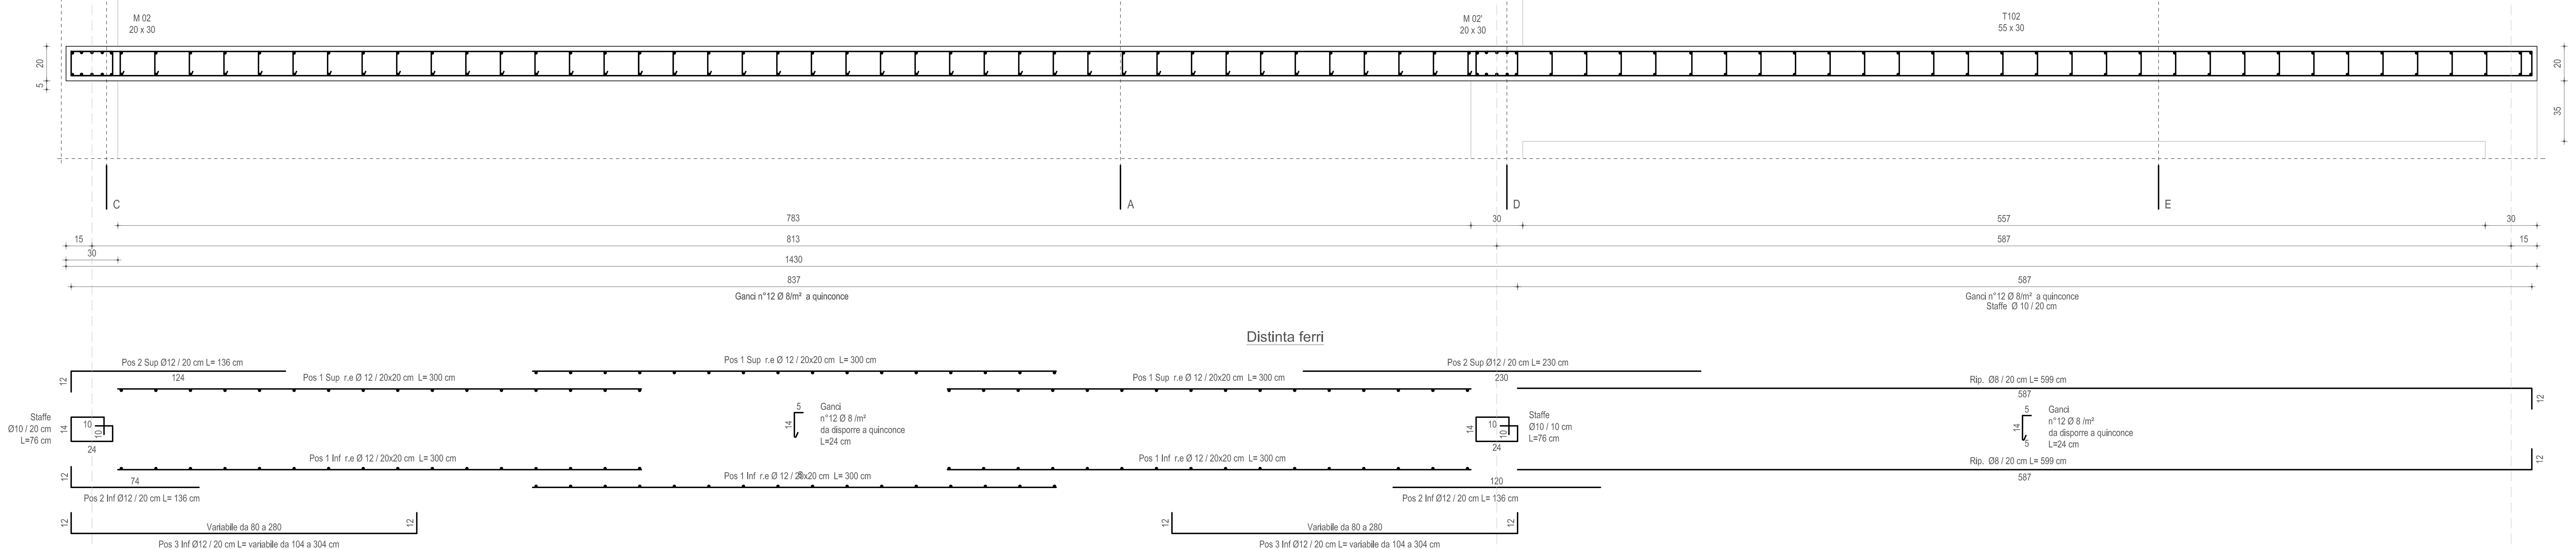
M 02
20 x 30
M 02'
20 x 30
T102
55 x 30
C
A
D
E
783
30
557
30
15
813
587
15
1430
837
587
Ganci n°12 Ø 8/m² a quinconce
Ganci n°12 Ø 8/m² a quinconce
Staffe Ø 10 / 20 cm
Distinta ferri
Pos 2 Sup Ø12 / 20 cm L= 136 cm
124
Pos 1 Sup r.e Ø 12 / 20x20 cm L= 300 cm
Pos 1 Sup r.e Ø 12 / 20x20 cm L= 300 cm
Pos 1 Sup r.e Ø 12 / 20x20 cm L= 300 cm
Pos 2 Sup Ø12 / 20 cm L= 230 cm
230
Rip. Ø8 / 20 cm L= 599 cm
587
Staffe
Ø10 / 20 cm
L=76 cm
Ganci
n°12 Ø 8 /m²
da disporre a quinconce
L=24 cm
Staffe
Ø10 / 10 cm
L=76 cm
Pos 1 Inf r.e Ø 12 / 20x20 cm L= 300 cm
Pos 1 Inf r.e Ø 12 / 20x20 cm L= 300 cm
Pos 1 Inf r.e Ø 12 / 20x20 cm L= 300 cm
Rip. Ø8 / 20 cm L= 599 cm
74
120
Pos 2 Inf Ø12 / 20 cm L= 136 cm
Pos 2 Inf Ø12 / 20 cm L= 136 cm
Variabile da 80 a 280
Pos 3 Inf Ø12 / 20 cm L= variabile da 104 a 304 cm
Variabile da 80 a 280
Pos 3 Inf Ø12 / 20 cm L= variabile da 104 a 304 cm

TRAVE -T102-
-scala 1:20-
Sezione E-E

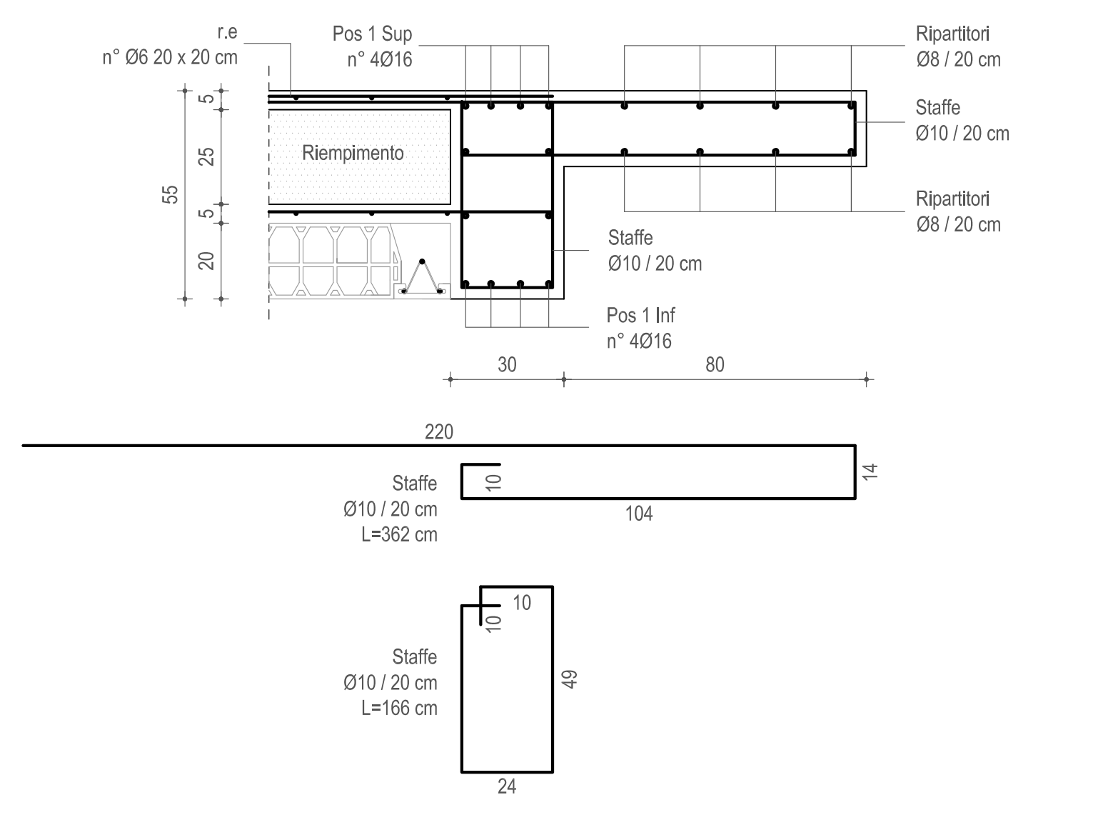

MATERIALI E PRESCRIZIONI

MATERIALI PRESCRITTI:

- Calcestruzzo per opere di: Fondazioni
    - Classe di resistenza : C25/30 (Rck 30)
    - Condizioni ambientali: Strutture completamente interrate in terreno permeabile
    - Classe di esposizione : XC2
    - Rapporto massimo acqua/cemento: 0,60
    - Classe di consistenza: S3 (Plastica)
    - Diametro massimo degli aggregati: 16 mm
- Calcestruzzo per opere di: Elevazione e Solai misti laterizio-c.a.
    - Classe di resistenza : C25/30 (Rck 30)
    - Condizioni ambientali: Strutture interne di edifici non industriali con umidità bassa
    - Classe di esposizione : XC1
    - Rapporto massimo acqua/cemento: 0,60
    - Classe di consistenza: S3 (Plastica)
    - Diametro massimo degli aggregati: 16 mm
- Calcestruzzo per opere di: Solette piene in C.A.
    - Classe di resistenza : C28/35 (Rck 35)
    - Condizioni ambientali: Strutture interne di edifici non industriali con umidità bassa
    - Classe di esposizione : XC1
    - Rapporto massimo acqua/cemento: 0,60
    - Classe di consistenza: S3 (Plastica)
    - Diametro massimo degli aggregati: 16 mm
- Acciaio per tutte le strutture: B450 C controllato

PRESCRIZIONE

Tutte le misure dovranno essere controllate in cantiere confrontandole con quelle del progetto architettonico e confermate dalla direzione lavori

La soletta in C.A. potrà essere scasserata trascorsi 28 gg dalla data di getto.

COMUNE DI VOLTA MANTOVANA PROVINCIA DI MANTOVA

Oggetto

PROGETTO PER LA REALIZZAZIONE DI CASA UNIFAMILIARE.

[redacted]

Oggetto tavola
- Disegni esecutivi:
  Soletta copertura

Denuncia C.A.

Tav. n° 3	Variante
Data	Scale 1:20

[redacted]

Collaboratori