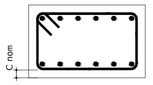
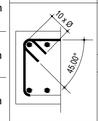
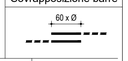
MATERIALI E PRESCRIZIONI

CALCESTRUZZO	FONDAZIONI MURI CONTRO TERRA	TRAVI - SOLETTE POGGIOLI - SCALE	PILASTRI-SETTI NUCLEI ASCENSORE
CLASSE DI RESISTENZA	C 25/30 R ck= 30 MPa	C 25/30 R ck= 30 MPa	C 25/30 R ck= 30 MPa
CLASSE DI ESPOSIZIONE	XC2	XC1	XC1
CLASSE DI CONSISTENZA (Slump)	S4	S4	S4
DIAMETRO MAX AGGREGATI	32 mm	22 mm	22 mm

ACCIAIO PER ARMATURE LENTE (6<Ø<40 mm)	TIPO	f yk	f tk	f yd
	B450C	> 450 MPa	> 540 MPa	> 391 MPa

COPRIFERRO NOMINALE C nom			Chiusura staffe	Ancoraggio barre
	FONDAZIONI MURI CONTRO TERRA	40 mm		
	TRAVI - SOLETTE POGGIOLI - SCALE	30 mm		Sovrapposizione barre
	PILASTRI - SETTI NUCLEI ASCENSORE	30 mm		

DIAMETRO BARRA	Ø < 12	12 < Ø < 16	16 < Ø < 25	25 < Ø < 40
DIAMETRO DEL MANDRINO	4 x Ø	5 x Ø	8 x Ø	10 x Ø

Acciaio (Secondo UNI EN 10025-2:2004)
Tipologia
S235JR
Caratteristiche meccaniche
S235JR
Tensione di snervamento (T ambiente): Spessore nominale >3≤16 mm — f_{yk} = 275 N/mm²
Tensione di rottura (T ambiente): Spessore nominale >3 ≤ 16 mm — f_{tk} = 410-560 N/mm²
Deformazione massima a rottura (T ambiente): Spessore nominale >3 ≤ 40 mm — A% = 23%
Resilienza: T=20°C Spessore nominale <150 mm — Resilienza=27J

Bulloni
Tipologia
Ad alta resistenza: Classe 8.8
Caratteristiche meccaniche f_{yb} ≤ 649 N/mm²
f_{tb} ≤ 800 N/mm²

Saldature
Tipologia
Giunto: Ad angolo (A)
Testa a Testa (T-T)
Dimensione


S1≥S2
l=S2
a=0,71xS2


S1≥S2
l=S2
a=0,5xS2

COMUNE DI MOGLIA — PROVINCIA DI MANTOVA

Committente

PROGETTO STRUTTURE

Oggetto tavola
FONDAZIONI

Tav. n°
01


Revisione

Data


Scale
1:20

Progettista


PIANTA FONDAZIONI - Scala 1:20

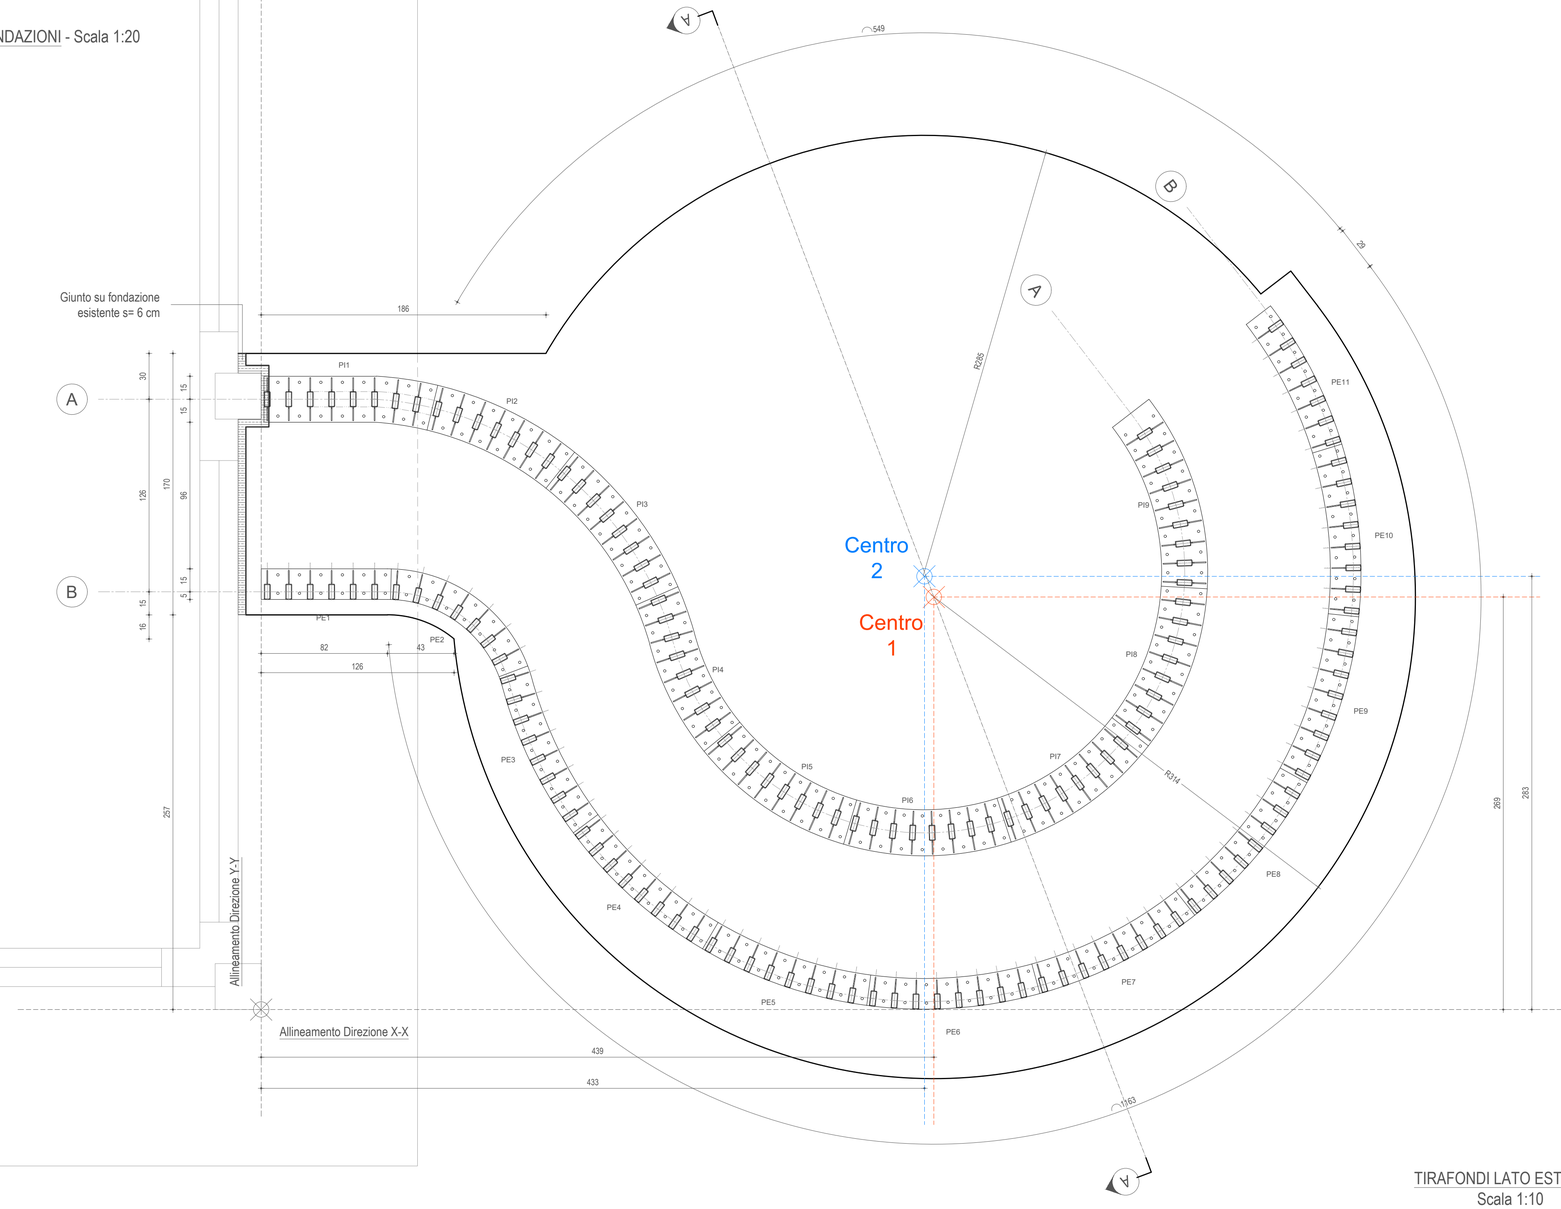

SEZIONE A-A - Scala 1:20

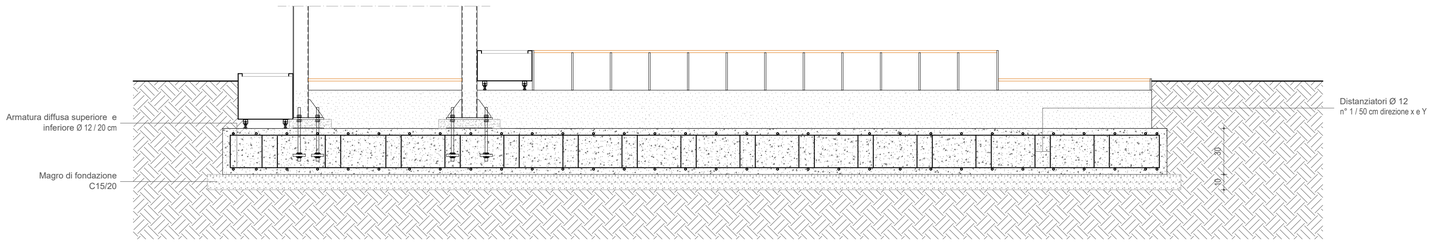


Armatura diffusa lato superiore - Direzione X e Y Ø 12 / 20 cm - Sovrapposizione minima 100 cm

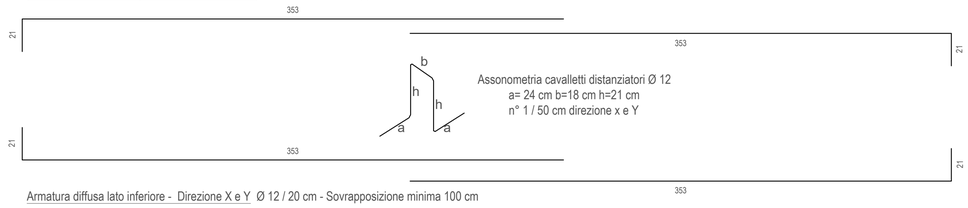


Armatura diffusa lato inferiore - Direzione X e Y Ø 12 / 20 cm - Sovrapposizione minima 100 cm

TIRAFONDI LATO ESTERNO
Scala 1:10

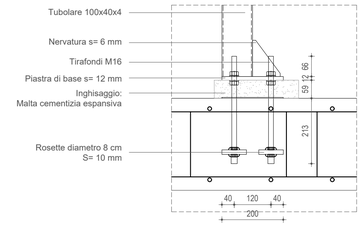

TIRAFONDI LATO INTERNO
Scala 1:10

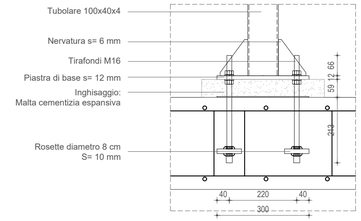

MATERIALI E PRESCRIZIONI

CALCESTRUZZO	FONDAZIONI MURI CONTRO TERRA	TRAVI - SOLETTE POGGIOLI - SCALE	PILASTRI-SETTI NUCLEI ASCENSORE
CLASSE DI RESISTENZA	C 25/30 R ck= 30 MPa	C 25/30 R ck= 30 MPa	C 25/30 R ck= 30 MPa
CLASSE DI ESPOSIZIONE	XC2	XC1	XC1
CLASSE DI CONSISTENZA (Slump)	S4	S4	S4
DIAMETRO MAX AGGREGATI	32 mm	22 mm	22 mm

ACCIAIO PER ARMATURE LENTE (6<Ø<40 mm)	TIPO	f yk	f tk	f yd
	B450C	> 450 MPa	> 540 MPa	> 391 MPa

COPRIFERRO NOMINALE C nom			Chiusura staffe	Ancoraggio barre
C nom	FONDAZIONI	40 mm	10 x Ø, 45/90°	10 x Ø
	MURI CONTRO TERRA			Sovrapposizione barre
	TRAVI - SOLETTE	30 mm		60 x Ø
	POGGIOLI - SCALE			
	PILASTRI - SETTI	30 mm		
	NUCLEI ASCENSORE			

DIAMETRO BARRA	Ø < 12	12 < Ø < 16	16 < Ø < 25	25 < Ø < 40
DIAMETRO DEL MANDRINO	4 x Ø	5 x Ø	8 x Ø	10 x Ø

Acciaio (Secondo UNI EN 10025-2:2004)
Tipologia
S235JR
Caratteristiche meccaniche
S235JR
Tensione di snervamento (T ambiente): Spessore nominale >3≤16 mm — f_{yK} = 275 N/mm²
Tensione di rottura (T ambiente): Spessore nominale >3 ≤ 16 mm — f_{tk} = 410-560 N/mm²
Deformazione massima a rottura (T ambiente): Spessore nominale >3 ≤ 40 mm — A% = 23%
Resilienza: T=20°C Spessore nominale <150 mm — Resilienza=27J
Bulloni
Tipologia
Ad alta resistenza: Classe 8.8
Caratteristiche meccaniche — f_{yb} ≤ 649 N/mm² ; f_{tb} ≤ 800 N/mm²
Saldature
Tipologia
Giunto: Ad angolo (A) — S1≥S2, l=S2, a=0,71xS2
Testa a Testa (T-T) — S1≥S2, l=S2, a=0,5xS2
Dimensione

COMUNE DI MOGLIA — PROVINCIA DI MANTOVA

Committente

PROGETTO STRUTTURE

Oggetto tavola
ELEVAZIONE E IMPALCATI

Tav. n°
02


Revisione

Data


Scale
1:20

Progettista


PROSPETTO - Scala 1:25

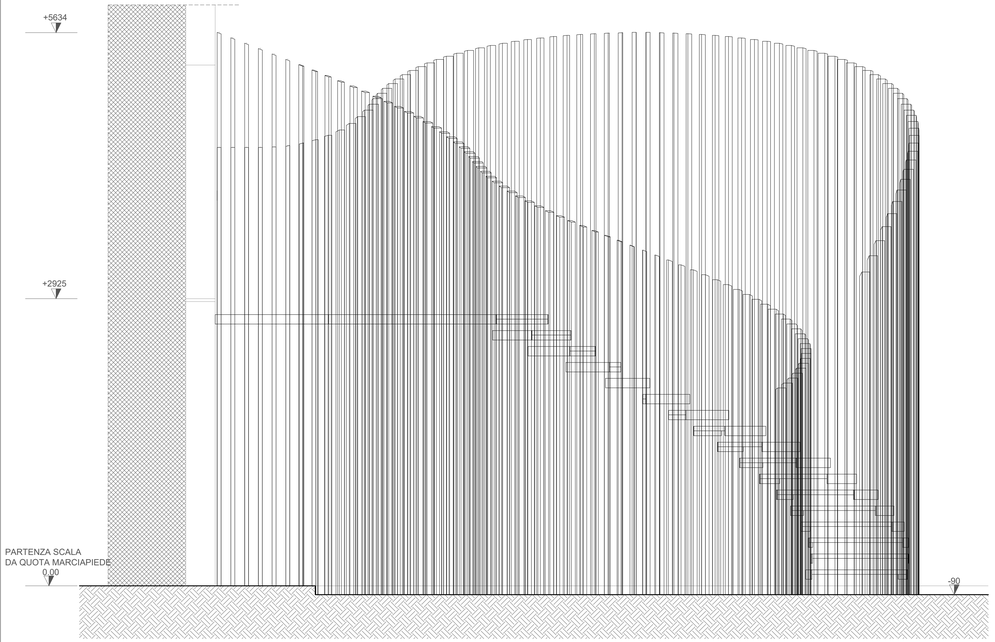


SEZIONE TIPO - Scala 1:25

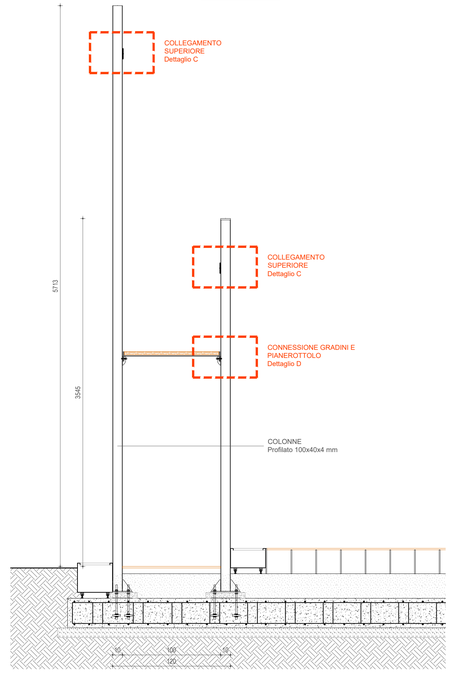


DETTAGLIO A - Pianerottolo - Scala 1:10

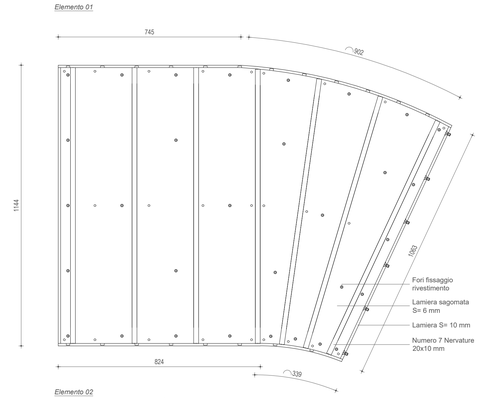


PIANTA ELEVAZIONE - Scala 1:25

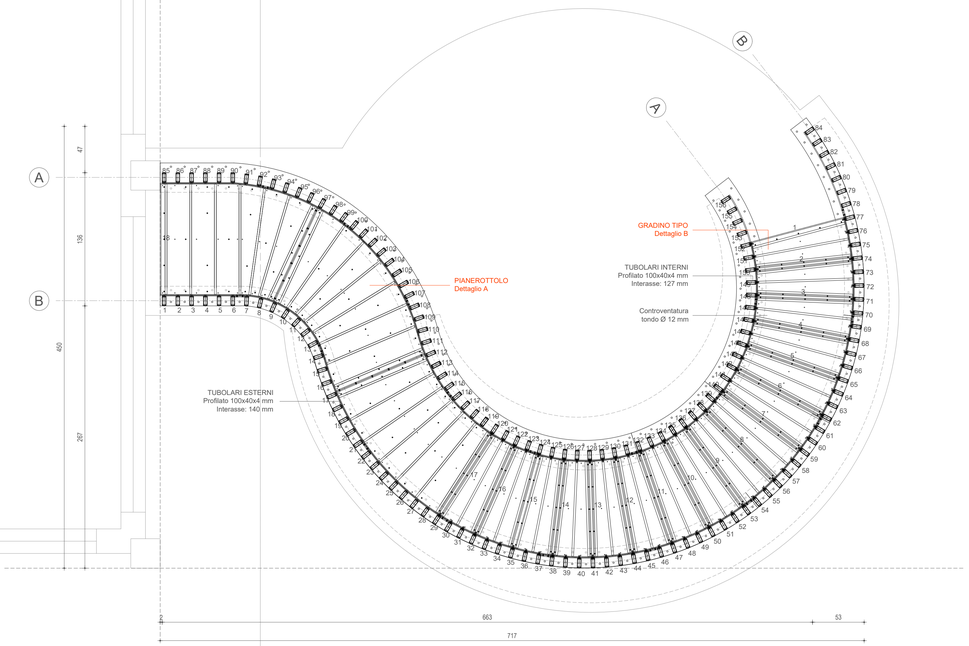

DETTAGLIO B - Gradino Tipo - Scala 1:10
Numero 16

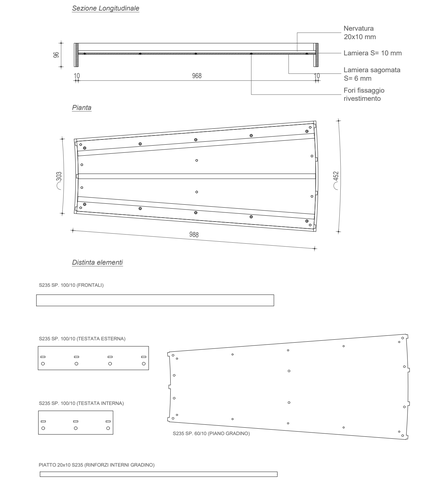

DETTAGLIO D - Scala 1:5

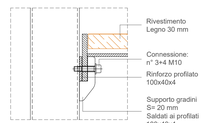

DETTAGLIO C - Scala 1:5

