PRESCRIZIONI

MATERIALI PRESCRITTI:

CONSOLIDAMENTO SOLAIO LIGNEO

- Calcestruzzo leggero tipo " CENTRO STORICO " conforme a UNI En 206-1 con le seguenti caratteristiche:
  - · Classe di resistenza : LC 25/28 (Rck 28)
  - · Classe di esposizione : XC1
- Acciaio in barre per C.A. per tutte le strutture: B450 C controllato
- Acciaio per reti elettrosaldate: B450 A
- Connettori: Tirafondi 0192 - UNIFIX
- Legno massiccio da costruzione in conformità a UNI EN 338:
  - Tipologia: Conifere
  - Classe di reistenza minima: C16

PRESCRIZIONE

-Tutte le misure dovranno essere controllate in cantiere e approvate dalla direzione lavori;

- Avvisare la direzione lavori prima dell'esecuzione di ogni getto;

COMUNE DI MANTOVA PROVINCIA DI MANTOVA

Oggetto

[illegible]

[illegible]

Riferimenti Catastali

Oggetto tavola

- Piante
- Particolari

PROGETTO STRUTTURE

Tav. n° 1

Variante


Data

Scale 1:10 - 1:50

[illegible]

Collaboratori

PIANTA PRIMO IMPALCATO Scala 1:50

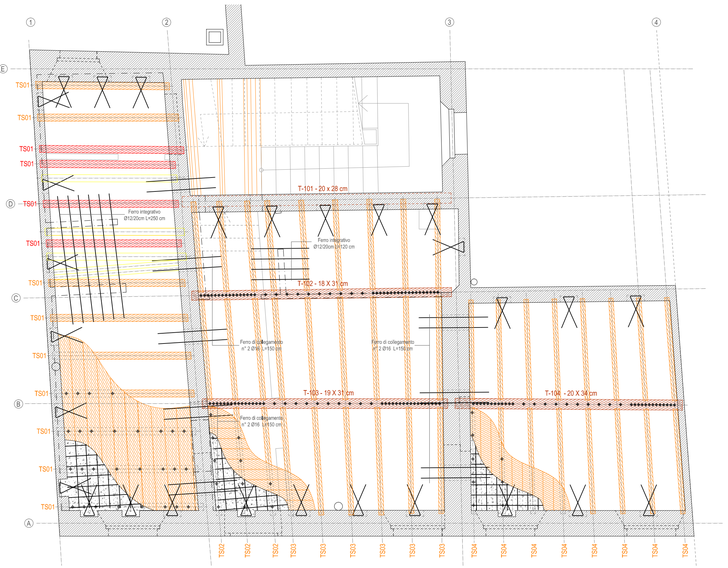

ABACO ORDITURE			
TS-01	Travetto esistente	Base: 14 cm	Altezza: 17 cm
TS-01	Travetto ricollocato	Base: 14 cm	Altezza: 17 cm
TS-02	Travetto esistente	Base: 10 cm	Altezza: 12 cm
TS-03	Travetto esistente	Base: 10 cm	Altezza: 14 cm
TS-04	Travetto esistente	Base: 9 cm	Altezza: 12 cm
T-101	Trave esistente	Base: 20 cm	Altezza: 28 cm
T-102	Trave esistente	Base: 18 cm	Altezza: 31 cm
T-103	Trave esistente	Base: 19 cm	Altezza: 31 cm
T-104	Trave esistente	Base: 20 cm	Altezza: 34 cm

TS-01 — Simbolo

Connettori ad uncino Ø 12 L= 14 cm posati su tavolato continuo
Connettori a spaziatura variabile
- ai quarti estremi della trave: 22.5 cm
- nella metà centrale della trave: 45.0 cm
Numero di connettori per trave: 10


TS-02 TS-03 TS-04 — Simbolo

Connettori ad uncino Ø 12 L= 14 cm posati su tavolato continuo
Connettori a spaziatura costante
- ai quarti estremi della trave: 45.0 cm
- nella metà centrale della trave: 45.0 cm
Numero di connettori per trave: 5

T102 - T103 - T104 — Simbolo


Connettori ad uncino Ø 14 L= 30 cm posati su trave con traviccello interrotto sulla trave.
Connettori a spaziatura variabile
- ai quarti estremi della trave: 7 cm
- nella metà centrale della trave: 21 cm
Numero di connettori per trave: 31
Disporre armatura inferiore di: 1.85 cm²/trave
Disporre staffe per area di: 2.30 cm²/m

PIANTA COPERTURA Scala 1:50

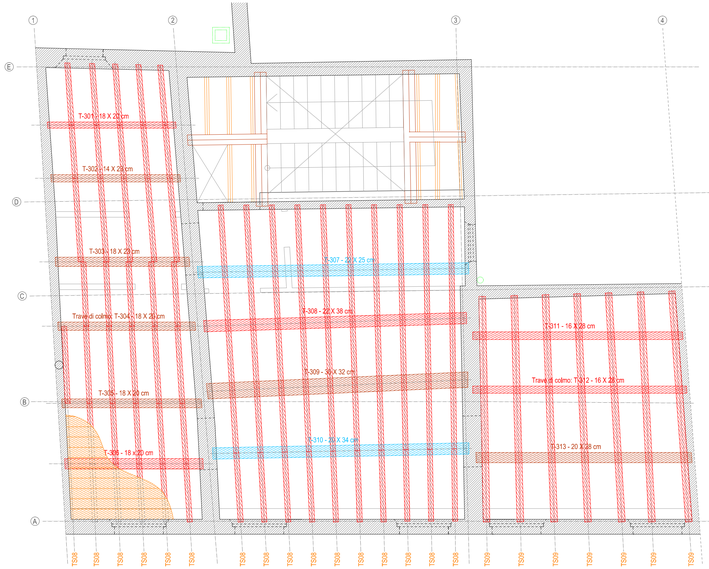

ABACO ORDITURE			
TS-08	Travetti da sostituire	Base: 10 cm	Altezza: 10 cm
TS-09	Travetto da sostituire	Base: 10 cm	Altezza: 10 cm
T-301	Trave da sostituire	Base: 18 cm	Altezza: 20 cm
T-302	Trave esistente	Base: 14 cm	Altezza: 23 cm
T-303	Trave esistente	Base: 18 cm	Altezza: 23 cm
T-304	Trave di colmo	Base: 18 cm	Altezza: 20 cm
T-305	Trave da sostituire	Base: 18 cm	Altezza: 20 cm
T-306	Trave da sostituire	Base: 18 cm	Altezza: 20 cm
T-307	Trave da consolidare	Base: 22 cm	Altezza: 25 cm
T-308	Trave da sostituire	Base: 22 cm	Altezza: 36 cm
T-309	Trave esistente	Base: 30 cm	Altezza: 32 cm
T-310	Trave da consolidare	Base: 20 cm	Altezza: 34 cm
T-311	Trave da sostituire	Base: 16 cm	Altezza: 28 cm
T-312	Trave da sostituire	Base: 16 cm	Altezza: 28 cm
T-313	Trave esistente	Base: 20 cm	Altezza: 28 cm

PIANTA SECONDO IMPALCATO Scala 1:50

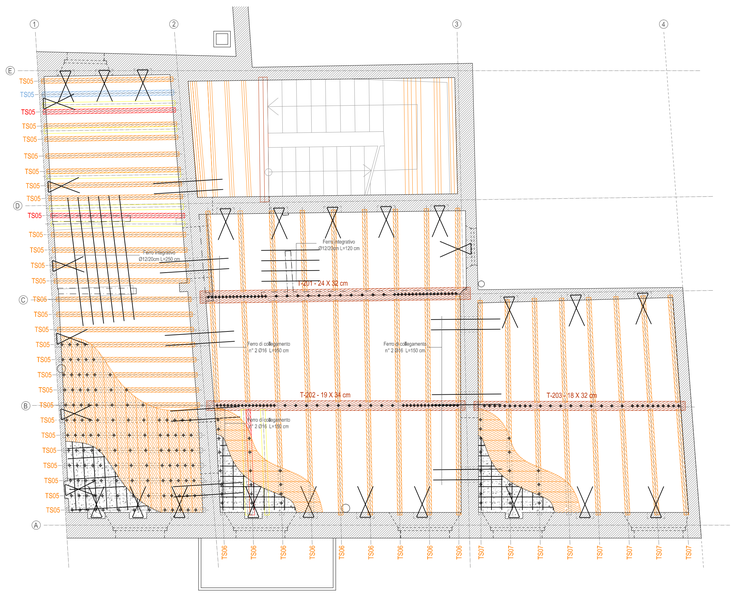

ABACO ORDITURE			
TS-05	Travetto esistente	Base: 9 cm	Altezza: 12 cm
TS-05	Travetto ricollocato	Base: 9 cm	Altezza: 12 cm
TS-05	Travetto esistente	Base: 10 cm	Altezza: 13 cm
TS-06	Travetto esistente	Base: 9 cm	Altezza: 12 cm
TS-07	Travetto esistente	Base: 9 cm	Altezza: 13 cm
T-201	Trave esistente	Base: 24 cm	Altezza: 32 cm
T-202	Trave esistente	Base: 19 cm	Altezza: 34 cm
T-203	Trave esistente	Base: 18 cm	Altezza: 32 cm

TS-05 — Simbolo

Connettori ad uncino Ø 12 L= 14 cm posati su tavolato continuo
Connettori a spaziatura variabile
- ai quarti estremi della trave: 15 cm
- nella metà centrale della trave: 30 cm
Numero di connettori per trave: 25

TS-06 TS-07 — Simbolo

Connettori ad uncino Ø 12 L= 14 cm posati su tavolato continuo
Connettori a spaziatura costante
- ai quarti estremi della trave: 18.5 cm
- nella metà centrale della trave: 37 cm
Numero di connettori per trave: 10


T201 - T202 — Simbolo

Connettori ad uncino Ø 14 L= 30 cm posati su trave con traviccello interrotto sulla trave.Connettori a spaziatura variabile
- ai quarti estremi della trave: 7 cm
- nella metà centrale della trave: 21 cm
Numero di connettori per trave: 46
Disporre armatura inferiore di: 1.31 cm²/trave
Disporre staffe per area di: 2.51 cm²/m


T203 — Simbolo

Connettori ad uncino Ø 14 L= 30 cm posati su trave con traviccello interrotto sulla trave.Connettori a spaziatura variabile
- ai quarti estremi della trave: 10 cm
- nella metà centrale della trave: 20 cm
Numero di connettori per trave: 32
Disporre armatura inferiore di: 1.31 cm²/trave
Disporre staffe per area di: 2.51 cm²/m


PARTICOLARE COLLEGAMENTO Scala 1:10

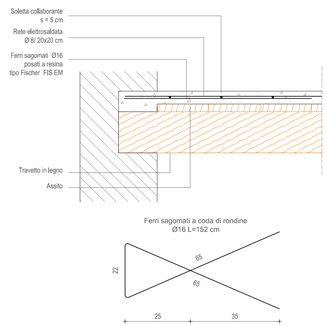

PARTICOLARE CORDOLO COPERTURA Scala 1:10

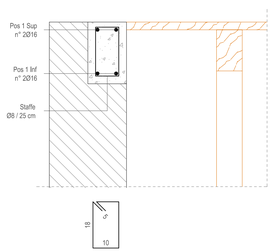

PARTICOLARE CORDOLO TRAVI Scala 1:10

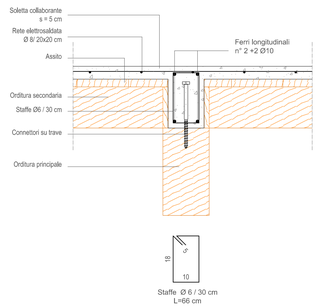

PARTICOLARE CORDOLO TRAVI DI COPERTURA DA CONSOLIDARE Scala 1:10

