MATERIALI E PRESCRIZIONI

MATERIALI PRESCRITTI:

Acciaio (Secondo UNI EN 10025-2:2004)
Tipologia
S275JR
Caratteristiche meccaniche
S275JR
Tensione di snervamento (T ambiente): Spessore nominale >3≤16 mm f_{yk} = 275 N/mm²
Tensione di rottura (T ambiente): Spessore nominale >3 ≤ 16 mm f_{tk} = 410-560 N/mm²
Deformazione massima a rottura (T ambiente): Spessore nominale >3 ≤ 40 mm A% = 23%
Resilienza: T=20°C Spessore nominale <150 mm Resilienza=27J

Bulloni
Tipologia
Ad alta resistenza: Classe 8.8
Caratteristiche meccaniche f_{yb} ≤ 649 N/mm²
f_{tb} ≤ 800 N/mm²

Saldature
Tipologia
Giunto: Ad angolo (A)
Testa a Testa (T-T)
Dimensione

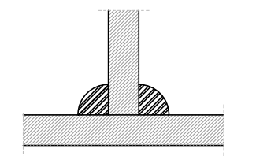

S1≥S2
l=S2
a=0,71xS2

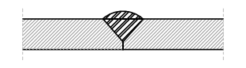

S1≥S2
l=S2
a=0,5xS2

Criteri di accettabilità (UNI EN ISO 5817:2008)
Livello di qualità: C

PRESCIZIONE: Tutte le misure esecutive devono essere controllare in sito prima della realizzazione dell'opera in presenza della D.L.

COMUNE DI PESCHIERA PROVINCIA DI VERONA

Oggetto

Progetto per la realizzazione di scenografia a struttura metallica da realizzarsi presso immobile sito in Peschiera del Garda (VR) riferimento SPORTLER S.p.a

Committente
[redacted]

PROGETTO STRUTTURE

Oggetto tavola	Tav. n°	Revisione
- Piante - Sezioni - Particolari costruttivi	01	
	Data	Scale 1:100 - 1:50 - 1:10

[redacted]

PIANTA
Scala 1:100

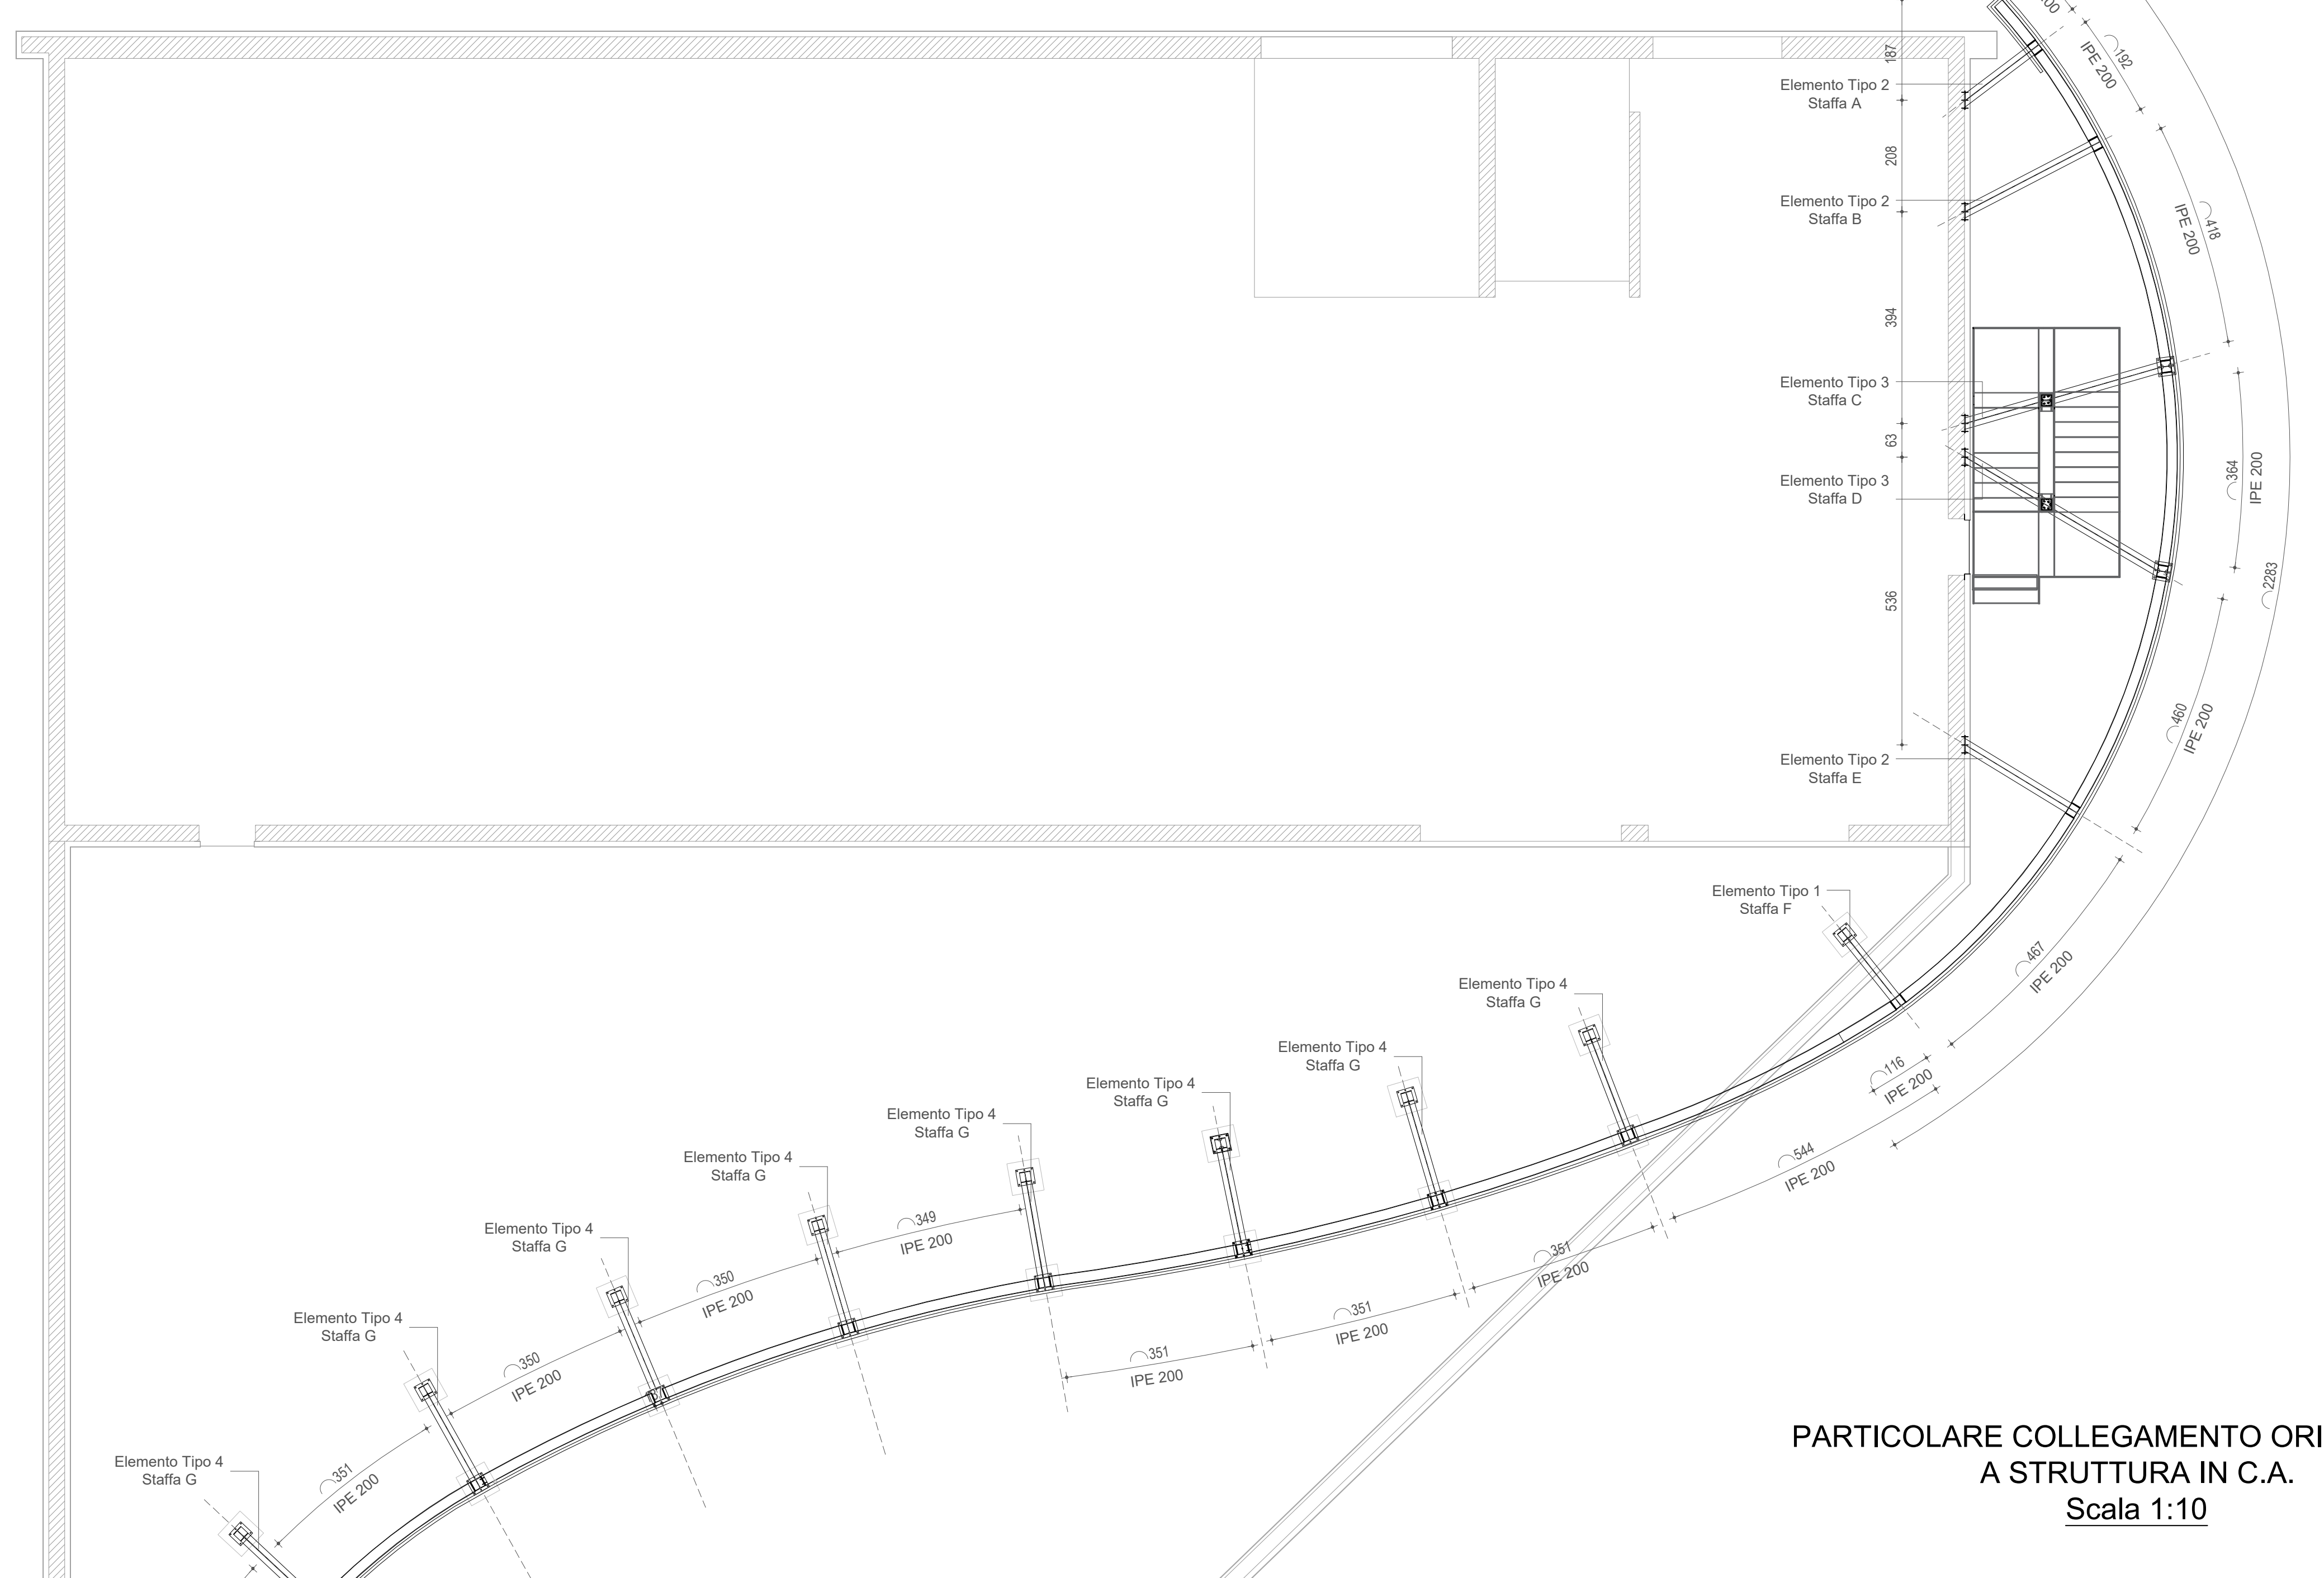

ELEMENTO TIPO 1
Scala 1:50

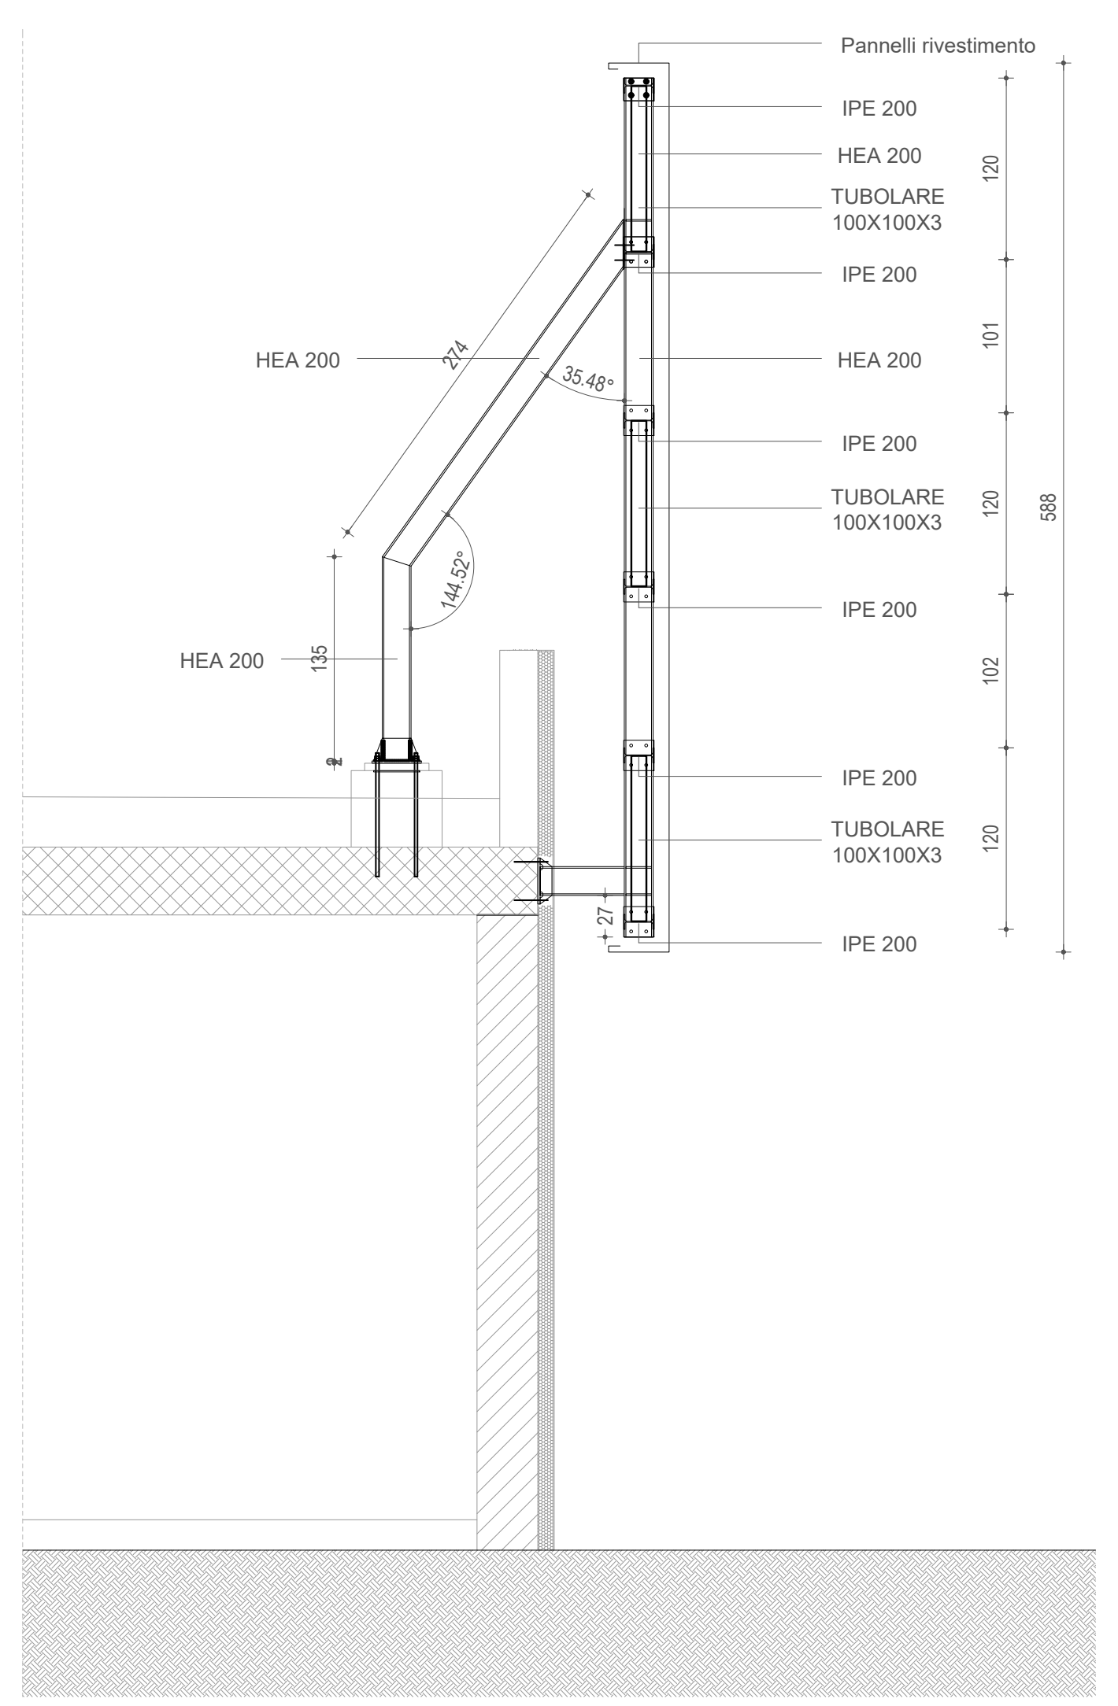

ELEMENTO TIPO 2
Scala 1:50

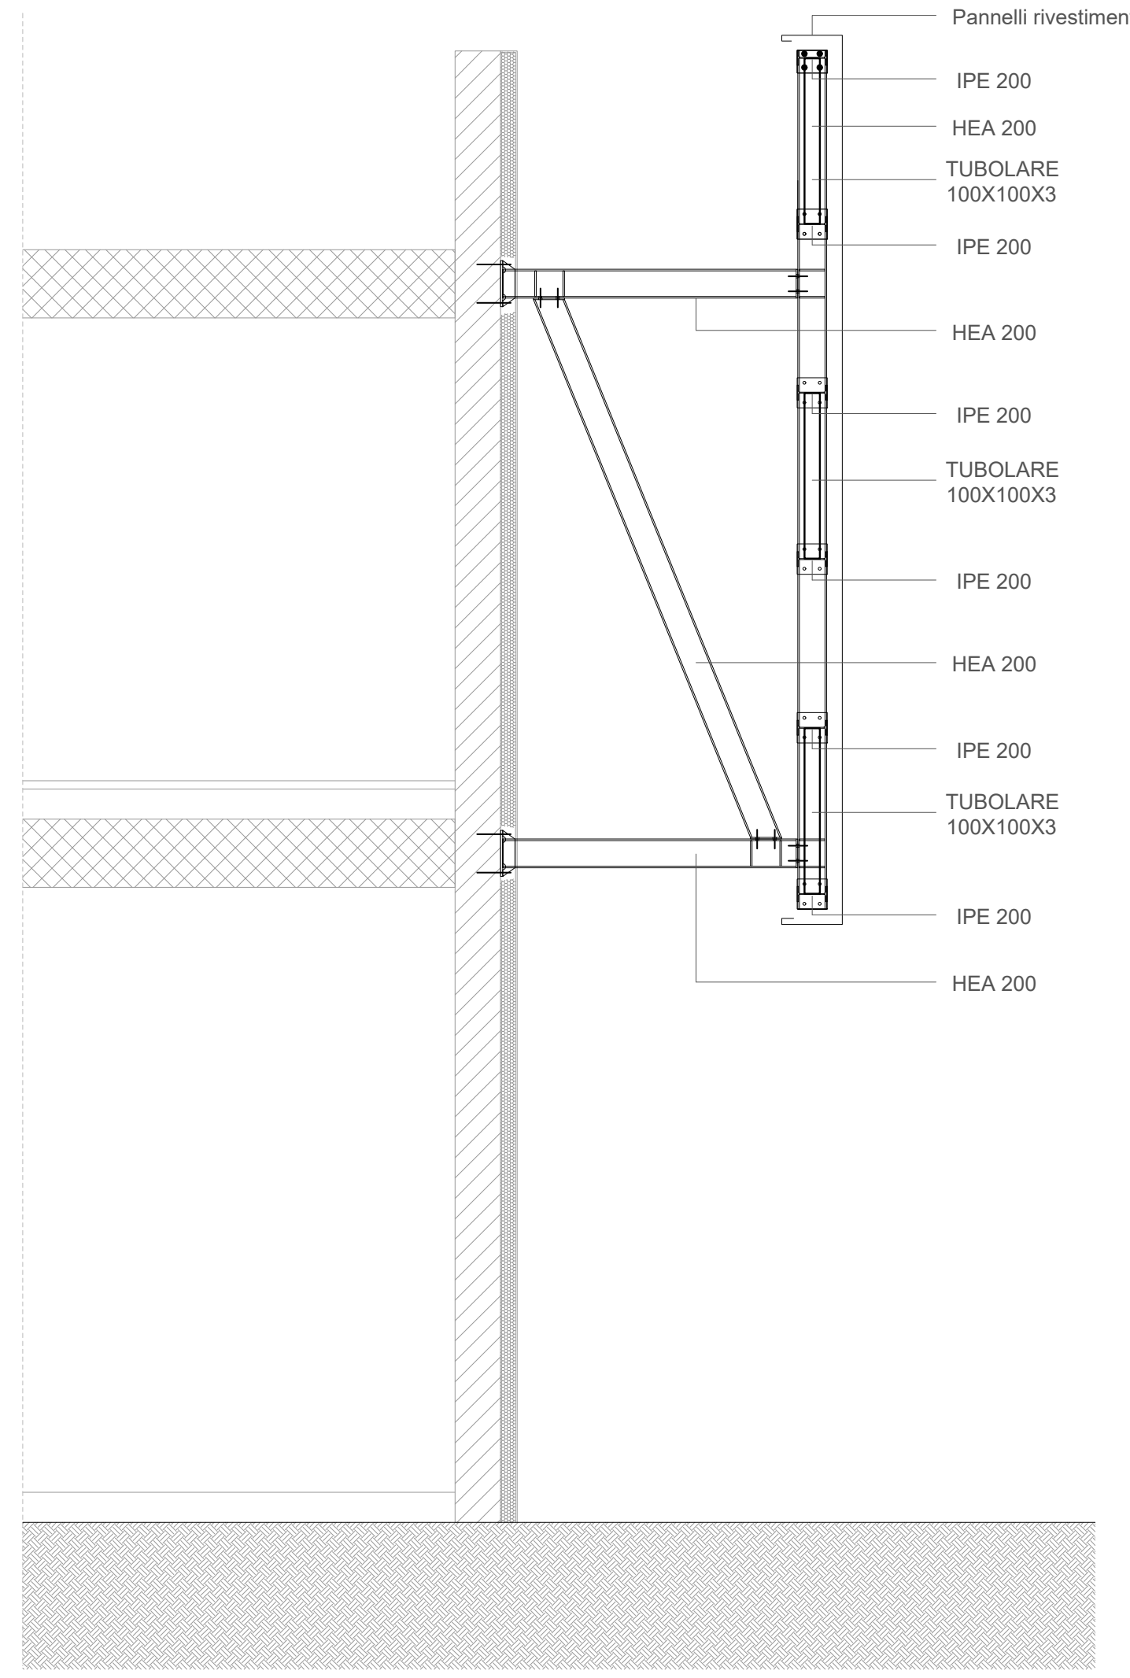

ELEMENTO TIPO 3
Scala 1:50

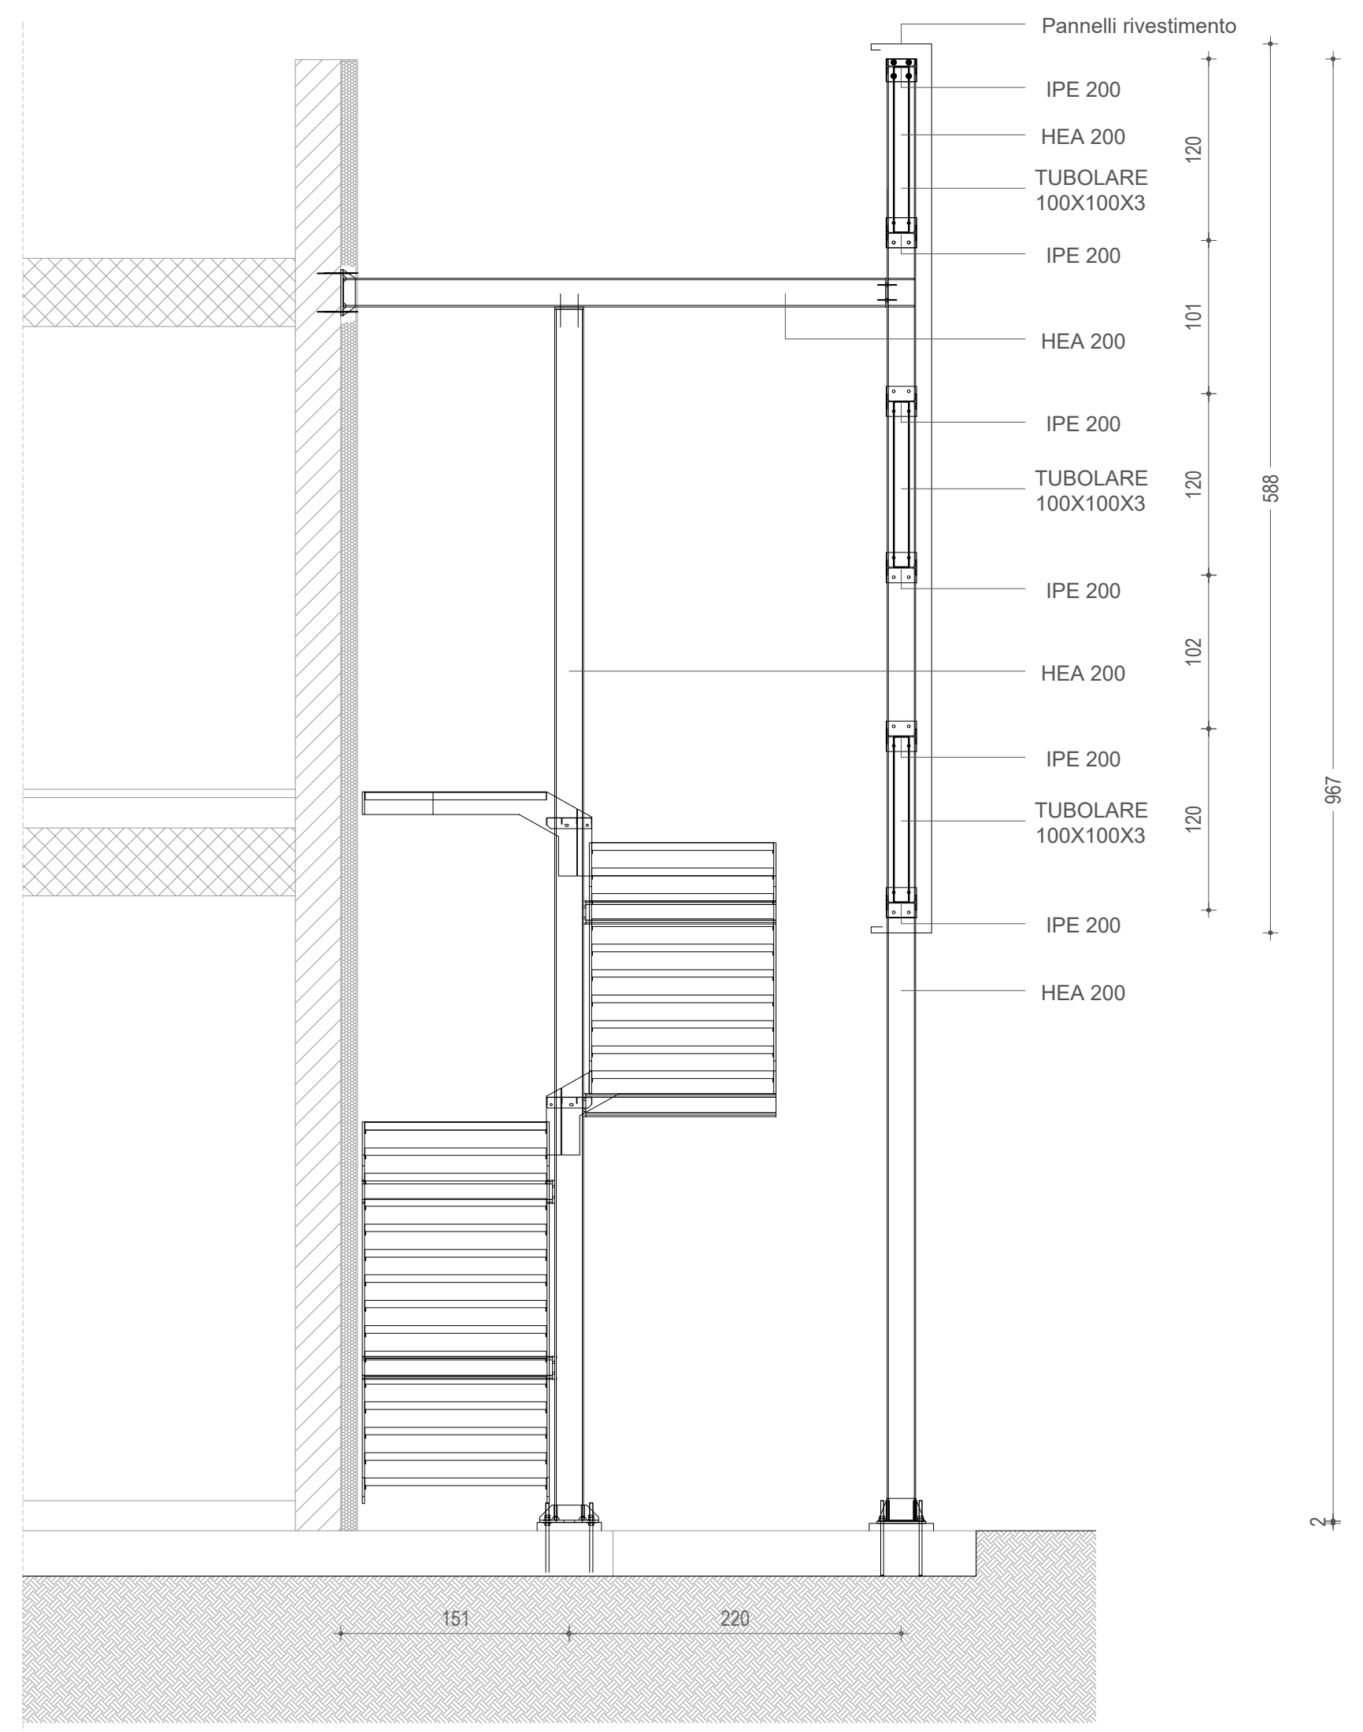

MODELLO DI CALCOLO

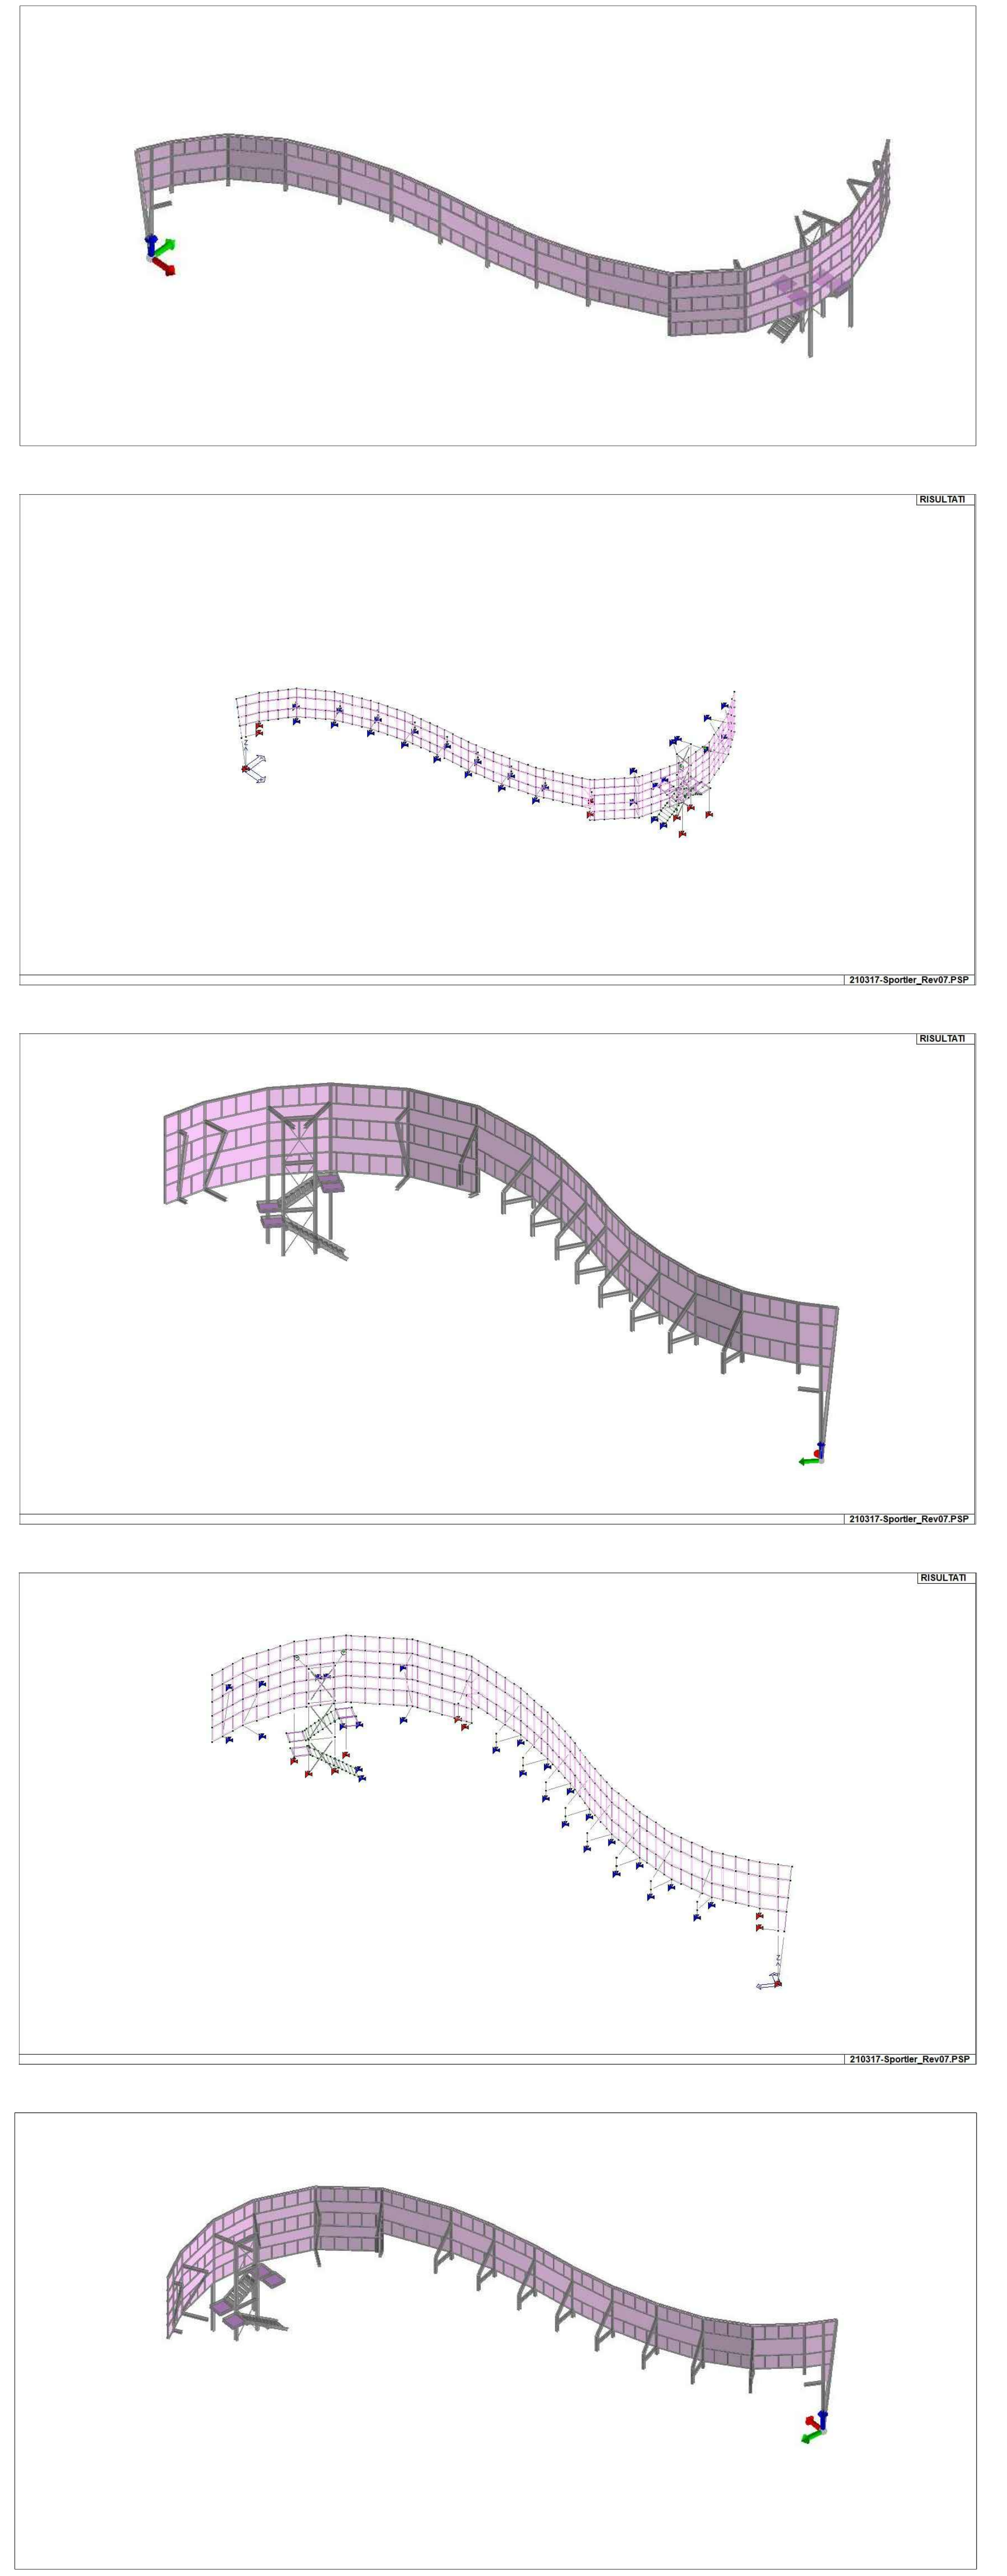

PARTICOLARE COLLEGAMENTO ORIZZONTALE A STRUTTURA IN C.A.
Scala 1:10

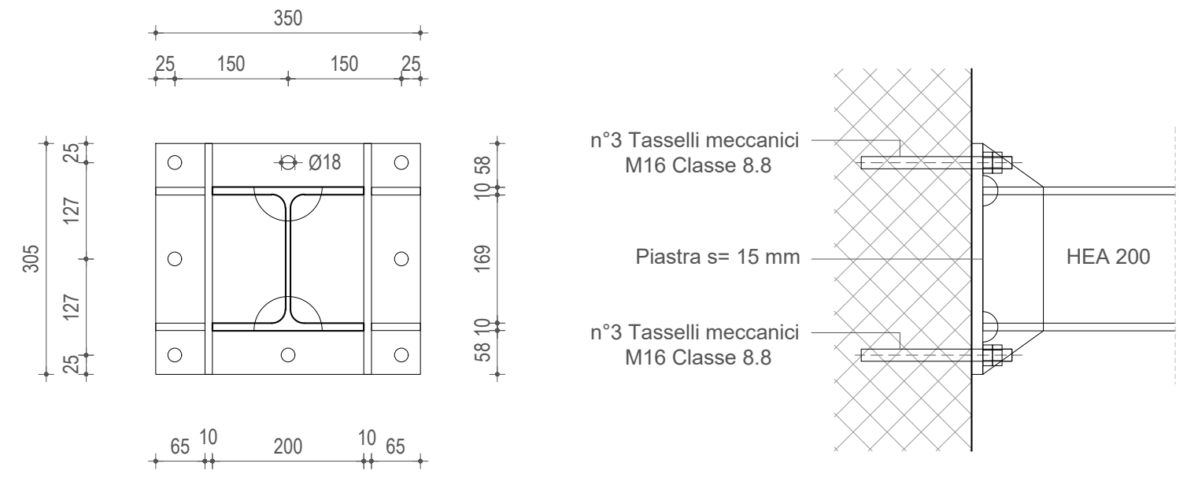
350
25
150
150
25
Ø18
305
127
127
58
10
169
10
58
65
10
200
10
65
n°3 Tasselli meccanici M16 Classe 8.8
Piastra s= 15 mm
n°3 Tasselli meccanici M16 Classe 8.8
HEA 200

PARTICOLARE COLLEGAMENTO VERTICALE A STRUTTURA IN C.A.
Scala 1:10

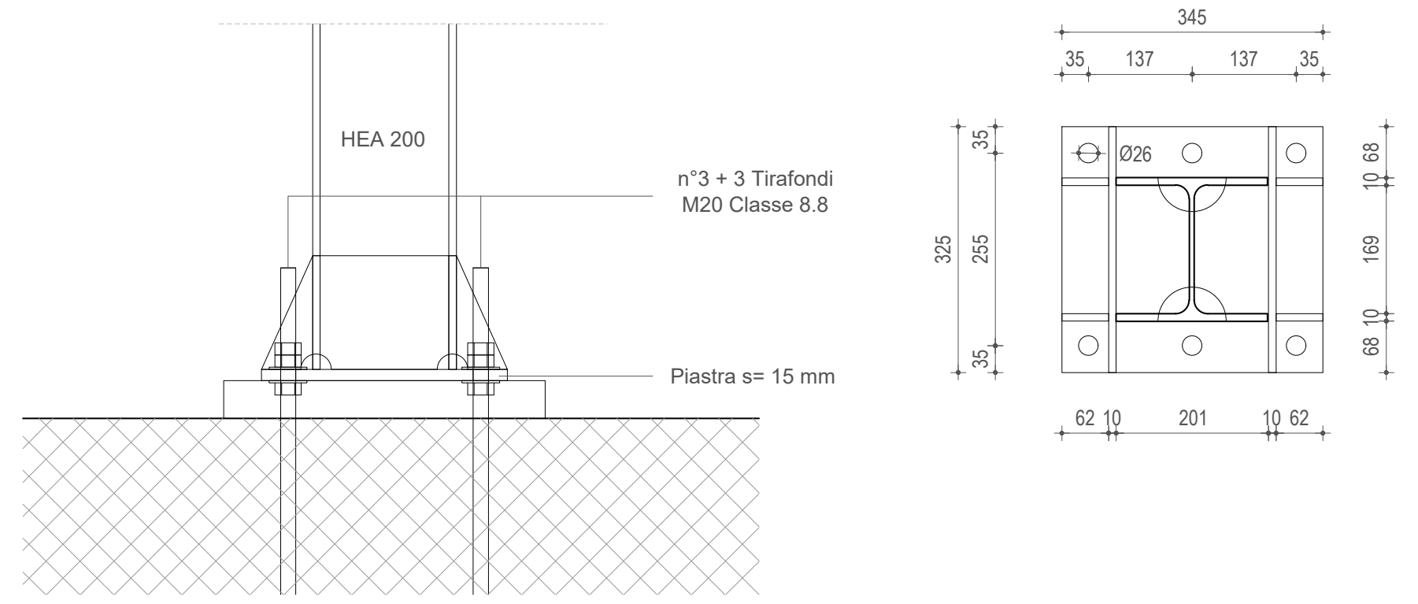

ELEMENTO TIPO 4
Scala 1:50

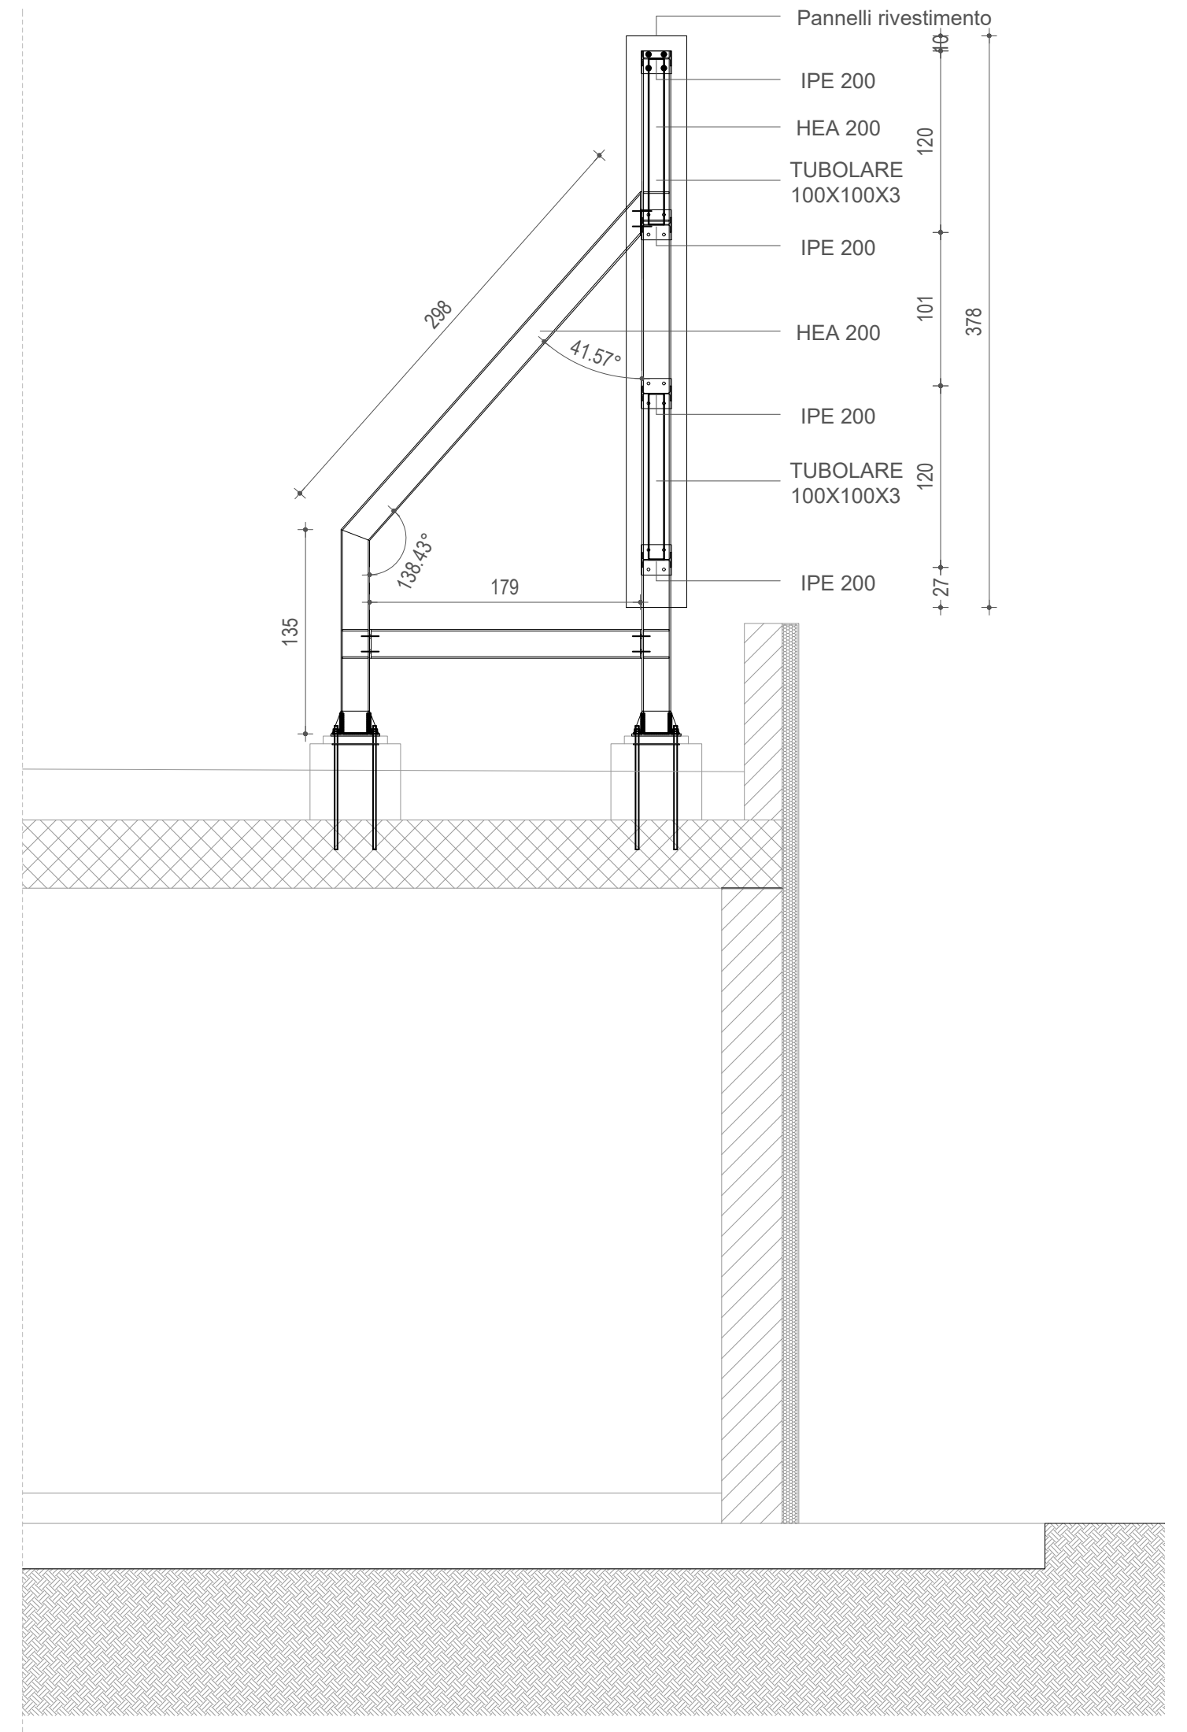

ELEMENTO TIPO 5
Scala 1:50

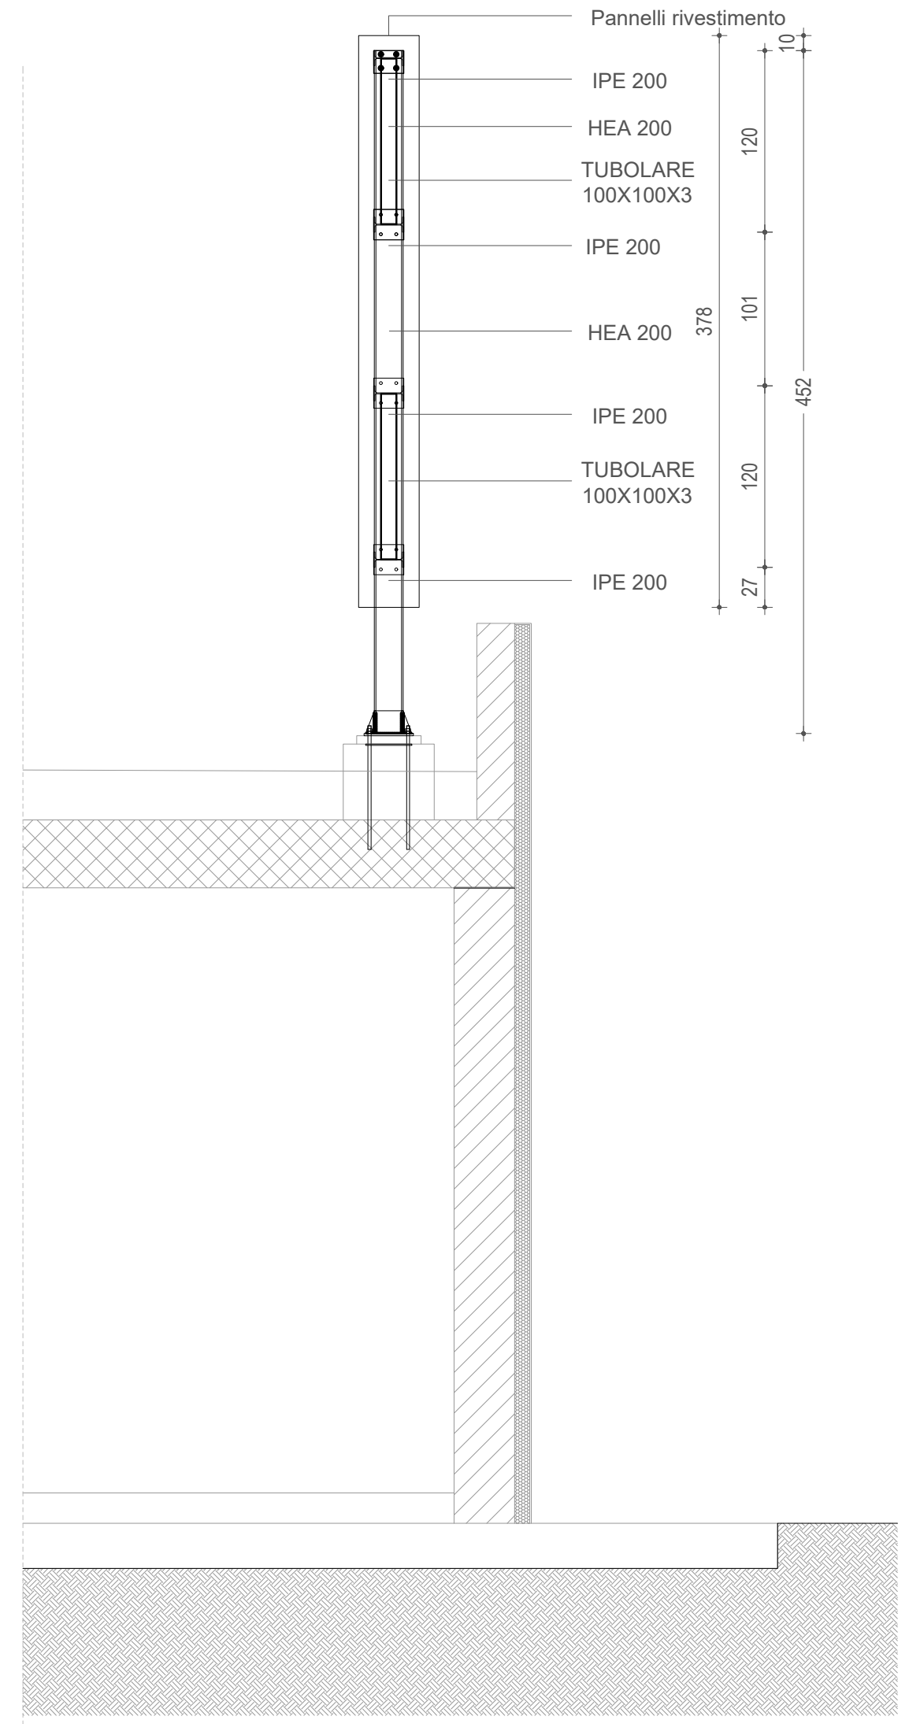

PROSPETTO FRONTALE
Scala 1:100