


Particolare armatura d'angolo
scala 1: 20

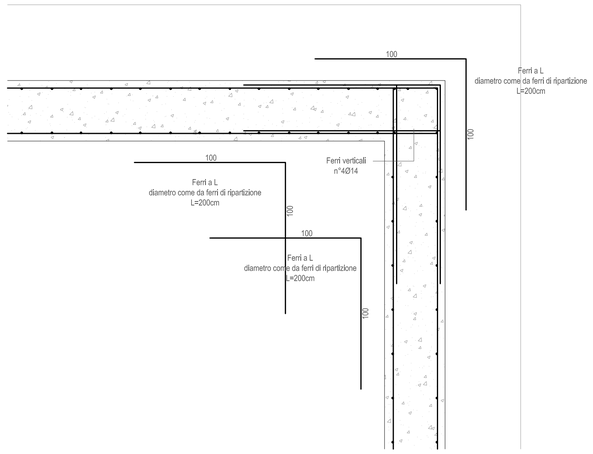


Particolare giunti di dilatazione
scala 1:10

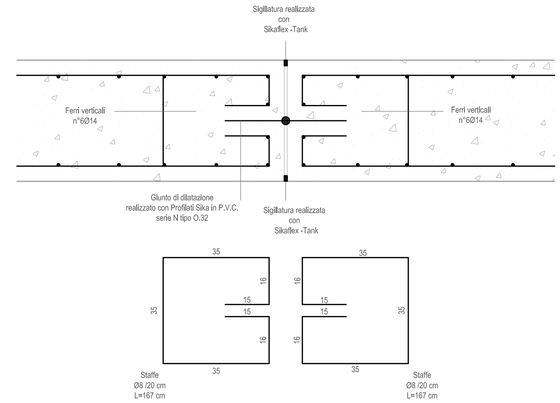

Pianta Vasca
scala 1:200

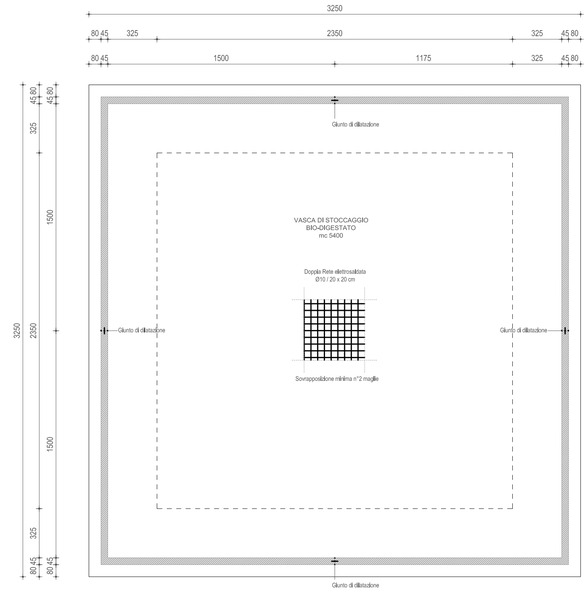

Muro Vasca
scala 1:25

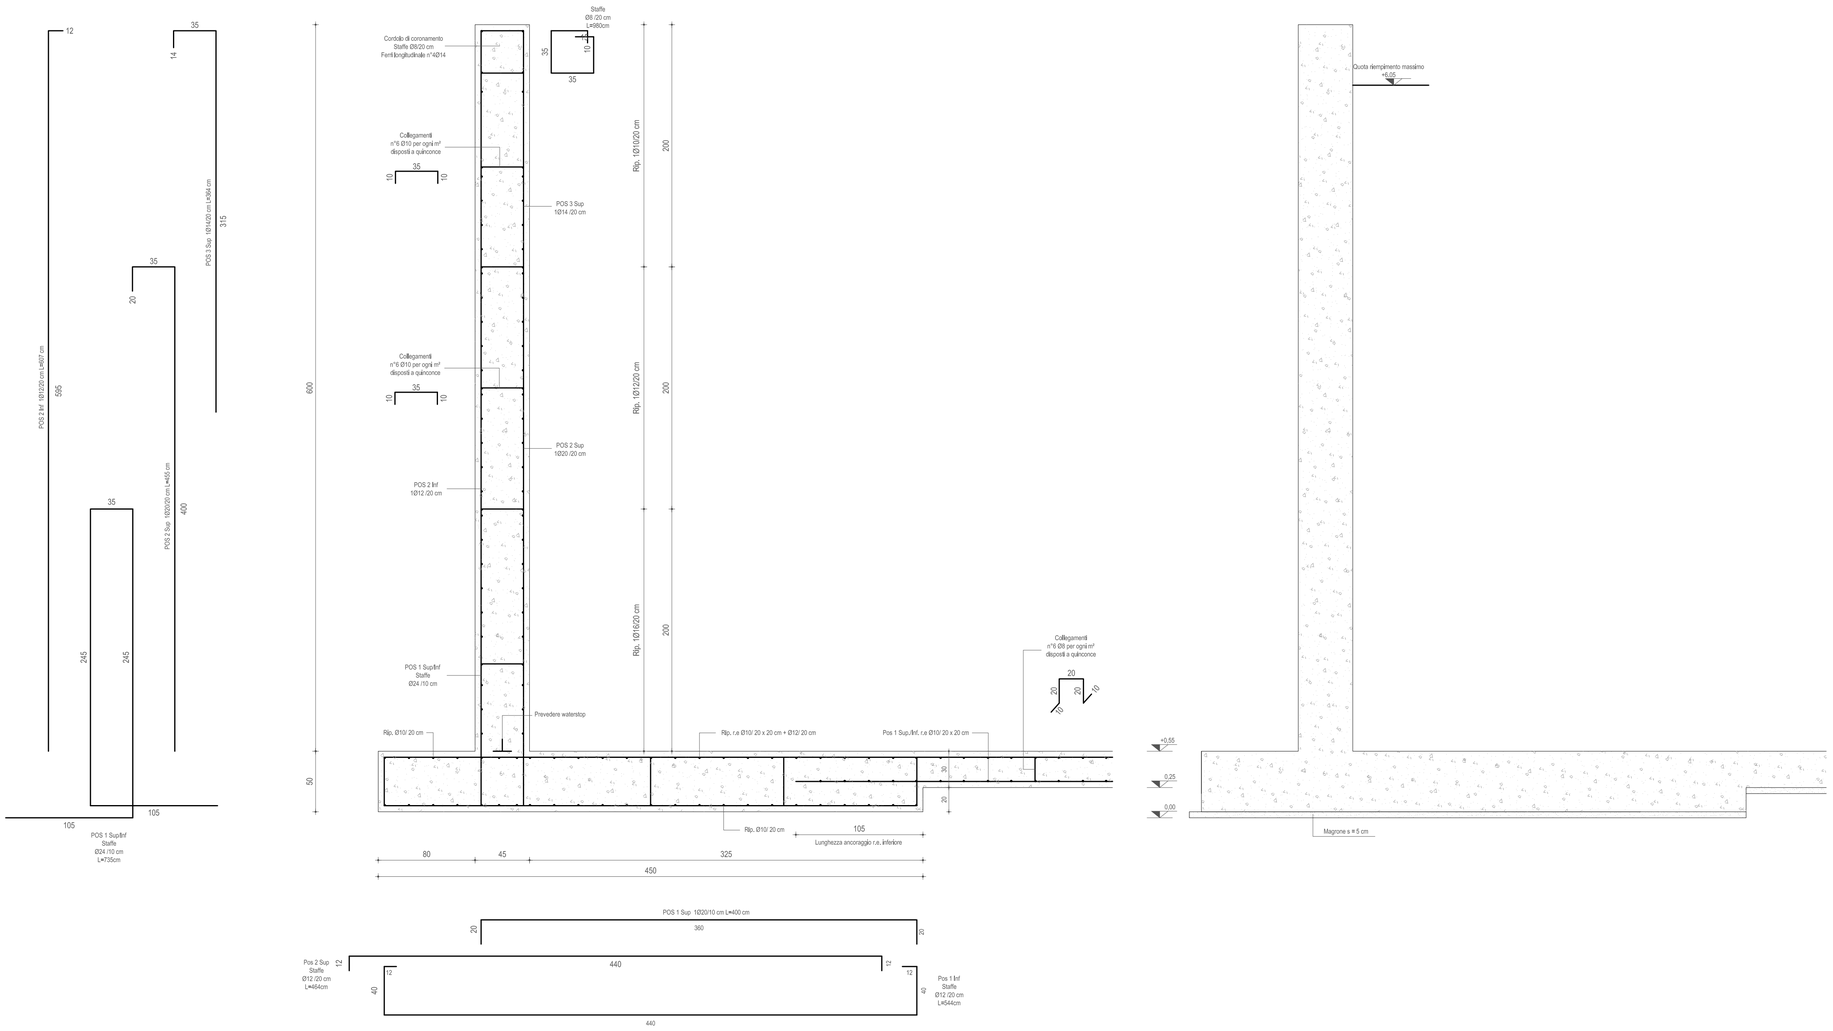

COMUNE DI SALIZZOLE — PROVINCIA DI VERONA

MATERIALI PRESCRITTI:

- CLS per opere di fondazione e muri in c.a. C28/35

Classe di esposizione	XA1
Rapporto a/c massimo	0,55
Ricoprimento minimo	50 mm
Classe di consistenza allo scarico	S4
Granulometria inerti	Ømax=20mm

- Acciaio per tutte le strutture — B450 C controllato

Oggetto

PROGETTO PER LA REALIZZAZIONE DI A DI IMPIANTO BIOGAS

[redacted]

Riferimenti Catastali

Oggetto tavola

- Disegni esecutivi:
  Vasca stoccaggio Bio-digestato

Denuncia C.A.

Tav. n° 1

Variante

Data

Scale
1:200, 1:25, 1:50

[redacted]

Collaboratori