MATERIALI E PRESCRIZIONI

MATERIALI PRESCRITTI:

- Calcestruzzo per opere di: Fondazioni

  - Classe di resistenza : C25/30 (Rck 30)
  - Condizioni ambientali: Strutture completamente interrate in terreno permeabile
  - Classe di esposizione : XC2
  - Rapporto massimo acqua/cemento: 0,60
  - Classe di consistenza: S3 (Plastica)
  - Diametro massimo degli aggregati: 16 mm

- Calcestruzzo per opere di: Elevazione Travi e Solai misti laterizio-c.a.
  - Classe di resistenza : C25/30 (Rck 30)
  - Condizioni ambientali: Strutture interne di edifici non industriali con umidità bassa
  - Classe di esposizione : XC1
  - Rapporto massimo acqua/cemento: 0,60
  - Classe di consistenza: S3 (Plastica)
  - Diametro massimo degli aggregati: 16 mm

- Calcestruzzo per opere di: Solette piene in C.A.

  - Classe di resistenza : C25/30 (Rck 30)
  - Condizioni ambientali: Strutture interne di edifici non industriali con umidità bassa
  - Classe di esposizione : XC1
  - Rapporto massimo acqua/cemento: 0,60
  - Classe di consistenza: S3 (Plastica)
  - Diametro massimo degli aggregati: 16 mm

- Acciaio per tutte le strutture: B450 C controllato

COMUNE DI RODIGO PROVINCIA DI MANTOVA

Oggetto

[redacted]

[redacted]

Impresa Esecutrice

-

Oggetto tavola


- Disegni esecutivi: Fondazioni

PROGETTO STRUTTURE


Tav. n°	Variante
1	Integrazione sostitutiva
Data	Scale
	1:100 - 1:20

[redacted]


Pianta fondazioni -scala 1:100-

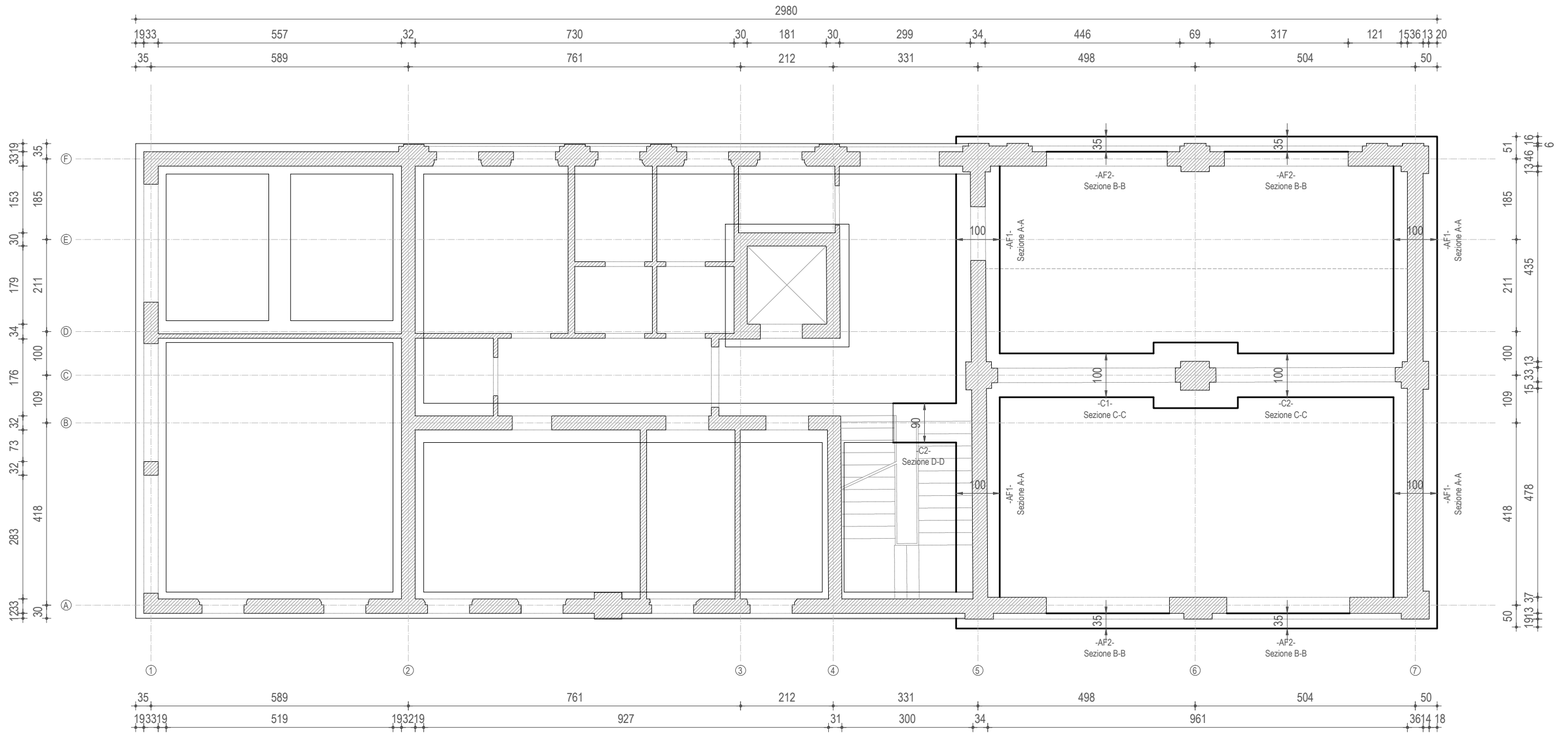


Allargamento fondazione
-AF 1-
Sezione A-A
-scala 1:20-

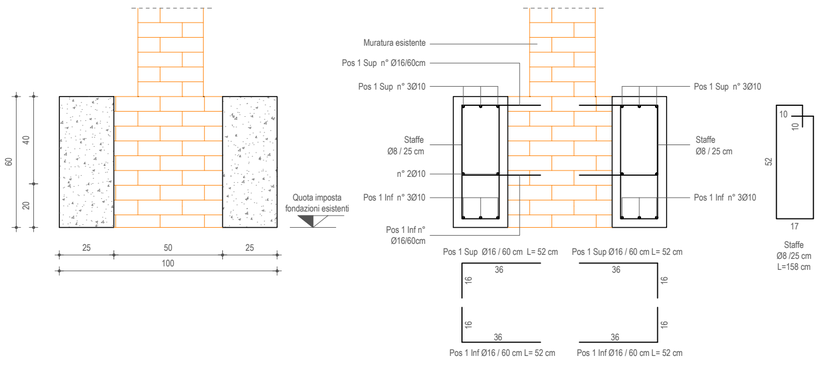

Cordolo
-C 1-
Sezione C-C
-scala 1:20-

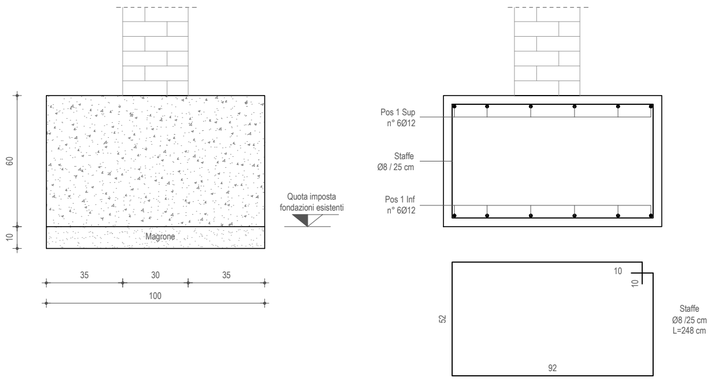

Allargamento fondazione
-AF 2-
Sezione B-B
-scala 1:20-

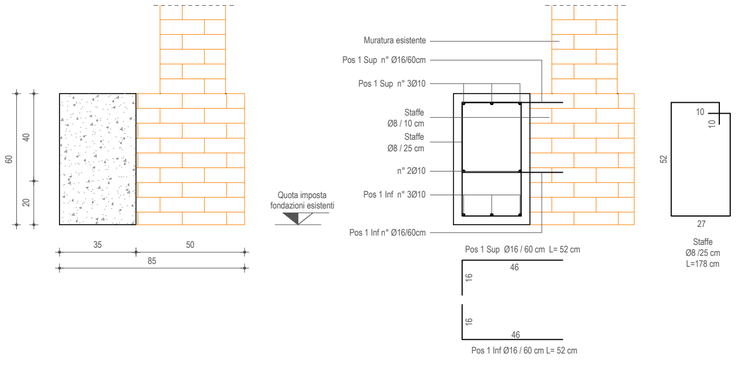

Cordolo
-C 2-
Sezione D-D
-scala 1:20-

