MATERIALI E PRESCRIZIONI

MATERIALI PRESCRITTI:

- Calcestruzzo per opere di: Fondazioni

  - Classe di resistenza : C25/30 (Rck 30)
  - Condizioni ambientali: Strutture completamente interrate in terreno permeabile
  - Classe di esposizione : XC2
  - Rapporto massimo acqua/cemento: 0,60
  - Classe di consistenza: S3 (Plastica)
  - Diametro massimo degli aggregati: 16 mm

- Calcestruzzo per opere di: Elevazione Travi e Solai misti laterizio-c.a.
  - Classe di resistenza : C25/30 (Rck 30)
  - Condizioni ambientali: Strutture interne di edifici non industriali con umidità bassa
  - Classe di esposizione : XC1
  - Rapporto massimo acqua/cemento: 0,60
  - Classe di consistenza: S3 (Plastica)
  - Diametro massimo degli aggregati: 16 mm

- Calcestruzzo per opere di: Solette piene in C.A.

  - Classe di resistenza : C25/30 (Rck 30)
  - Condizioni ambientali: Strutture interne di edifici non industriali con umidità bassa
  - Classe di esposizione : XC1
  - Rapporto massimo acqua/cemento: 0,60
  - Classe di consistenza: S3 (Plastica)
  - Diametro massimo degli aggregati: 16 mm

- Acciaio per tutte le strutture: B450 C controllato

- Fascia unidirezionale di fibre di carbonio e resina epossidica: Ruredil X WRAP 310

- Rete bidirezionale in fibre di PBO: RUREGOLD XR MURATURA + RIREGOLD MX MURATURA

COMUNE DI RODIGO — PROVINCIA DI MANTOVA

Oggetto

[redacted]

Committente

[redacted]

Impresa Esecutrice

-

Oggetto tavola

- Disegni esecutivi:
  Consolidamento Maschi Murari
  Irrigidimento Solaio Copertura
  Tiranti


PROGETTO STRUTTURE

Tav. n°	Variante
2	Integrazione sostitutiva
Data	Scale
	1:100 - 1:20

Progettisti

[redacted]

Pianta Piano Terra
Consolidamento Maschi Murari
-scala 1:100-

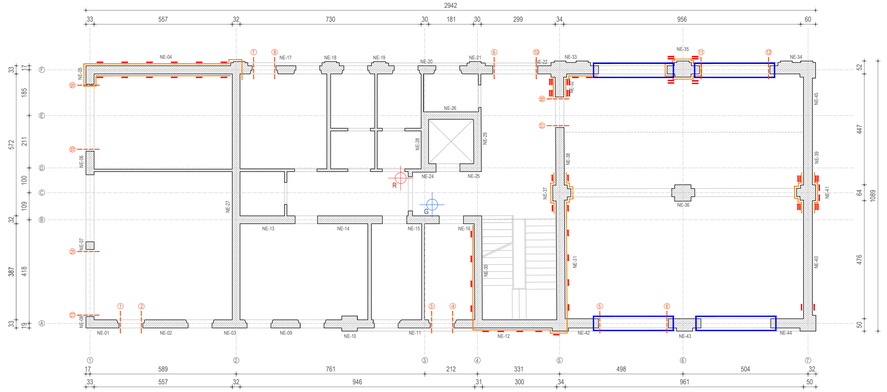


Fascia unidirezionale di fibre di carbonio e resina epossidica tipo Ruredil X WRAP 310 Lamina FRP posata orizzontalmente interasse 100 cm

Fascia unidirezionale di fibre di carbonio e resina epossidica tipo Ruredil X WRAP 310 posata verticalmente

Rinforzo strutturale con rete bidirezionale in fibre di PBO tipo RUREGOLD XR MURATURA + RIREGOLD MX MURATURA


Pianta Piano Primo
Consolidamento Maschi Murari
-scala 1:100-

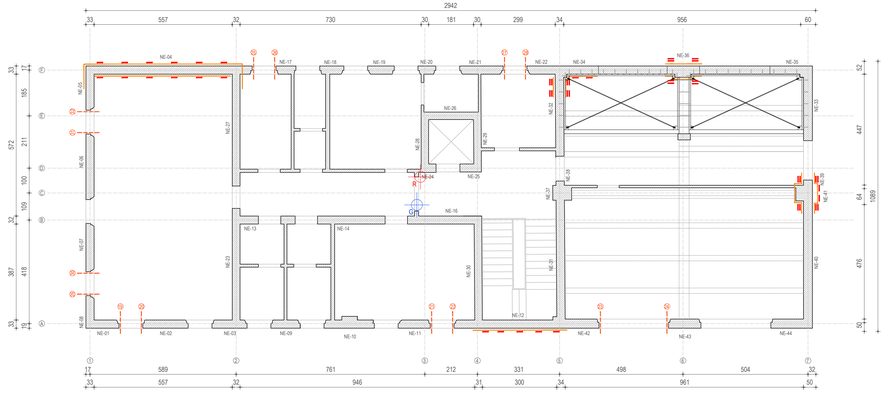


Fascia unidirezionale di fibre di carbonio e resina epossidica tipo Ruredil X WRAP 310 Lamina FRP posata orizzontalmente interasse 100 cm

Fascia unidirezionale di fibre di carbonio e resina epossidica tipo Ruredil X WRAP 310 posata verticalmente


Pianta Copertura
-scala 1:100-

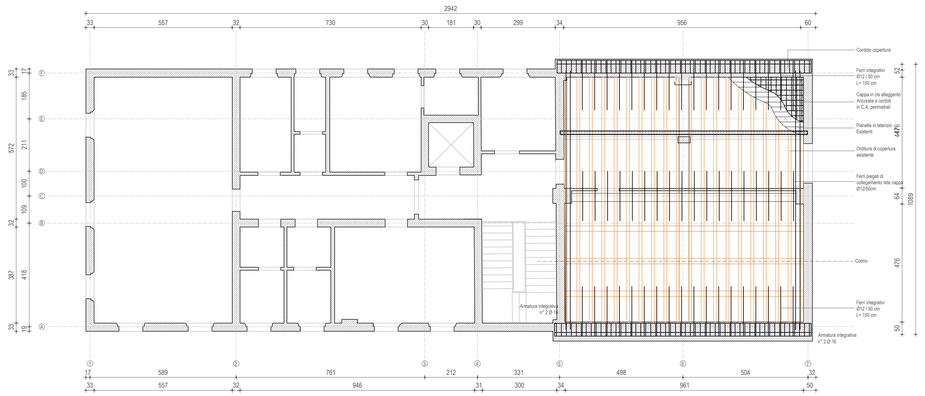


Collegamento orizzontale
-scala 1:25-

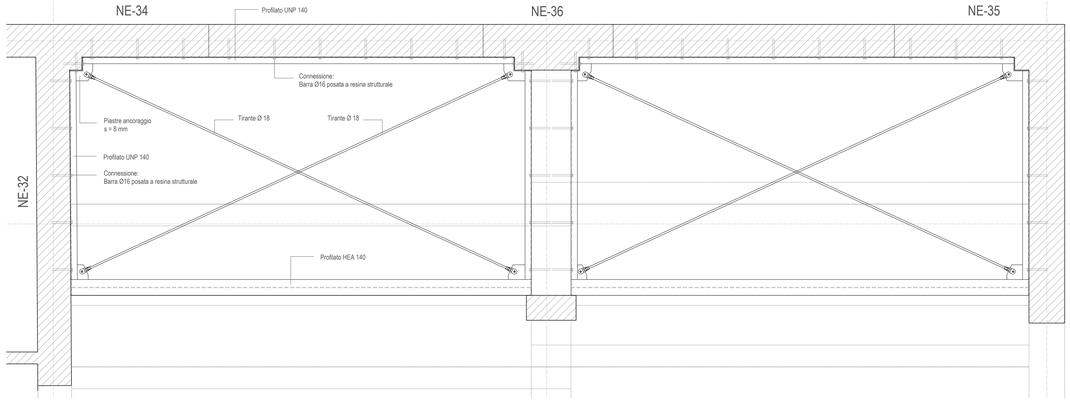

Particolare cordolo copertura
-scala 1:20-

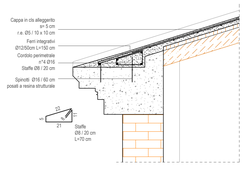

Particolare Ancoraggio FASCIA
Prospetto
-scala 1:20-

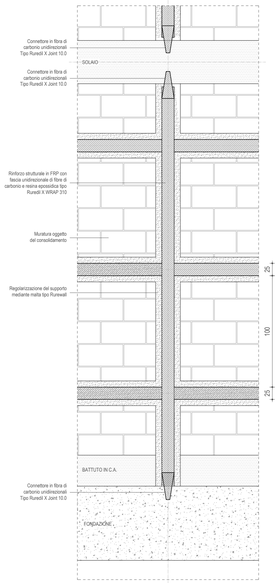

Particolare consolidamento Archi
Prospetto
-scala 1:20-

