MATERIALI E PRESCRIZIONI

MATERIALI PRESCRITTI:

- Calcestruzzo per opere di: Fondazioni

  - Classe di resistenza : C25/30 (Rck 30)
  - Condizioni ambientali: Strutture completamente interrate in terreno permeabile
  - Classe di esposizione : XC2
  - Rapporto massimo acqua/cemento: 0,60
  - Classe di consistenza: S3 (Plastica)
  - Diametro massimo degli aggregati: 16 mm

- Calcestruzzo per opere di: Elevazione Travi e Solai misti laterizio-c.a.
  - Classe di resistenza : C25/30 (Rck 30)
  - Condizioni ambientali: Strutture interne di edifici non industriali con umidità bassa
  - Classe di esposizione : XC1
  - Rapporto massimo acqua/cemento: 0,60
  - Classe di consistenza: S3 (Plastica)
  - Diametro massimo degli aggregati: 16 mm

- Calcestruzzo per opere di: Solette piene in C.A.

  - Classe di resistenza : C25/30 (Rck 30)
  - Condizioni ambientali: Strutture interne di edifici non industriali con umidità bassa
  - Classe di esposizione : XC1
  - Rapporto massimo acqua/cemento: 0,60
  - Classe di consistenza: S3 (Plastica)
  - Diametro massimo degli aggregati: 16 mm

- Acciaio per tutte le strutture: B450 C controllato

- Rete bidirezionale in fibre di PBO: RUREGOLD XR MURATURA + RIREGOLD MX MURATURA

Acciaio (Secondo UNI EN 10025-2:2004)
Tipologia
S235JR
Caratteristiche meccaniche
S235JR
Tensione di snervamento (T ambiente);Spessore nominale >3≤16 mm f_{yk} = 235 N/mm²
Tensione di rottura (T ambiente): Spessore nominale >3 ≤ 100 mm f_{tk} = 360-5100 N/mm²
Deformazione massima a rottura (T ambiente): Spessore nominale >3 ≤ 40 mm A% = 22%
Resilienza: T=20°C Spessore nominale <150 mm Resilienza=27J

COMUNE DI RODIGO PROVINCIA DI MANTOVA

Oggetto

[redacted]

[redacted]

Impresa Esecutrice
-

Oggetto tavola
- Disegni esecutivi:
  Piante
  Sezioni
  Particolari Costruttivi


PROGETTO STRUTTURE

Tav. n°	Variante
U	Integrazione sostitutiva
Data	Scale
	1:50 - 1:20- 1:10 -1:5


Progettisti

[redacted]


Pianta Piano Seminterrato -scala 1:50-

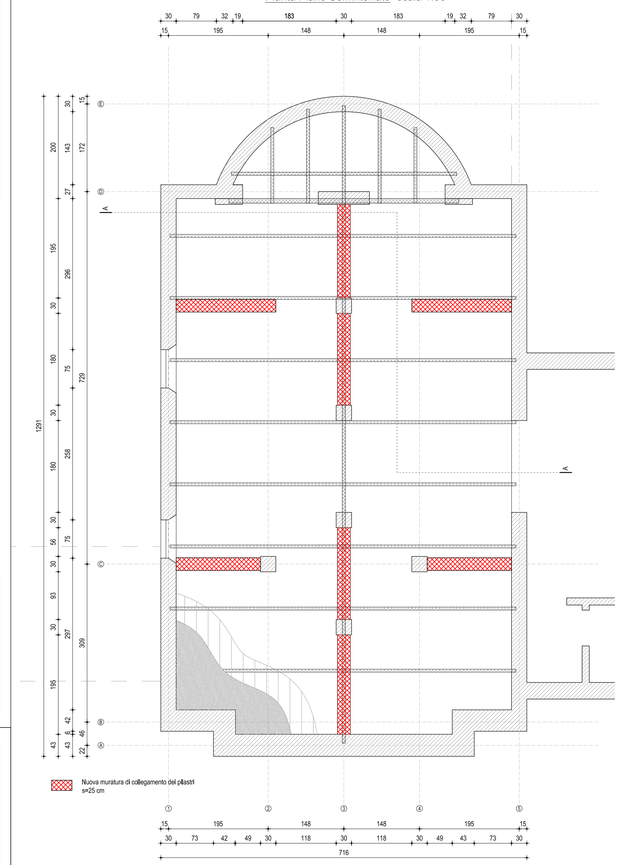


Pianta Piano Rialzato -scala 1:50-

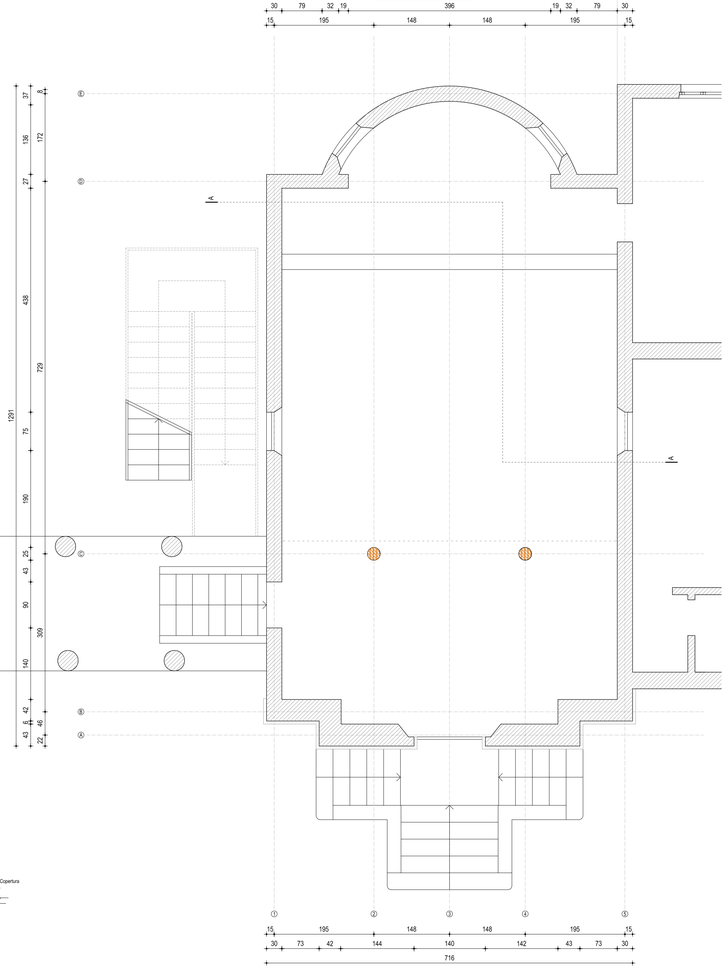


Pianta Copertura -scala 1:50-

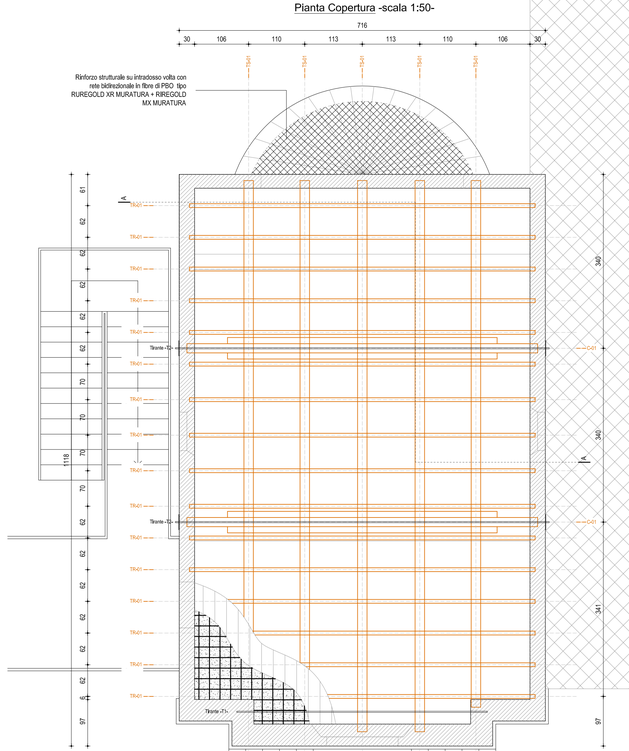


Sezione A-A -scala 1:50-

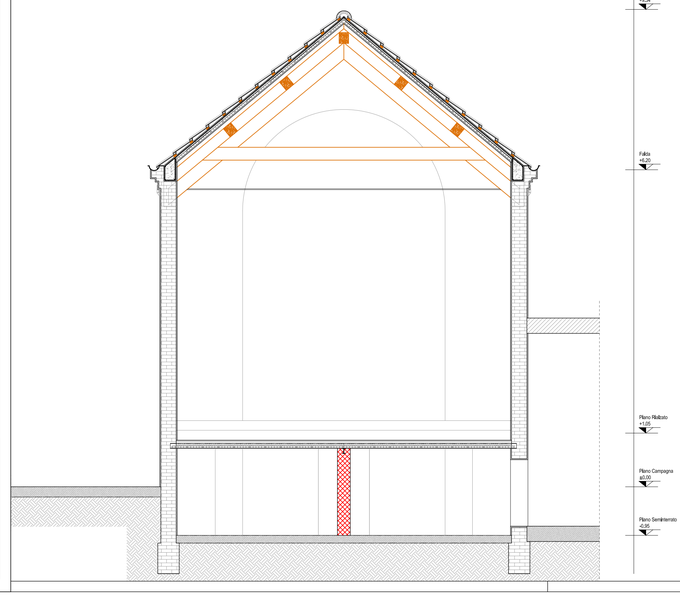


Particolare cordolo - Muratura Esistente
Copertura
Sezione
-scala 1:20-

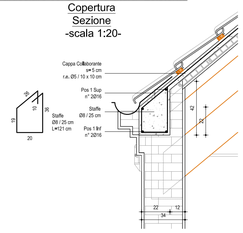


Particolare Ancoraggio Tirante
-scala 1:10-

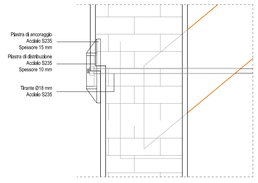

Particolare cordolo - Muratura Esistente
Corrispondenza capriate
Sezione
-scala 1:20-

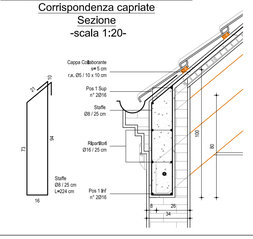

Distinta Piastra ancoraggio
-scala 1:5-

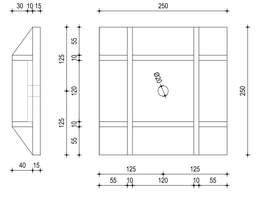

Particolare Angolo Copertura
Facciata
-scala 1:20-

