MATERIALI E PRESCRIZIONI

MATERIALI PRESCRITTI:

Calcestruzzo
Per opere di: Fondazioni

- Classe di resistenza : C25/30 (Rck 30)
- Condizioni ambientali: Strutture completamente interrate in terreno permeabile
- Classe di esposizione : XC2
- Rapporto massimo acqua/cemento: 0,60
- Classe di consistenza: S3 (Plastica)
- Diametro massimo degli aggregati: 16 mm

Acciaio per C.A.
Per tutte le strutture B450 C controllato

Acciaio (Secondo UNI EN 10025-2:2004)
Tipologia
S275JR
Caratteristiche meccaniche
S275JR
Tensione di snervamento (T ambiente): Spessore nominale >3≤16 mm f_{yk} = 275 N/mm²
Tensione di rottura (T ambiente): Spessore nominale >3 ≤ 16 mm f_{tk} = 410-560 N/mm²
Deformazione massima a rottura (T ambiente): Spessore nominale >3 ≤ 40 mm A% = 23%
Resilienza: T=20°C Spessore nominale <150 mm Resilienza=27J

Bulloni
Tipologia
Ad alta resistenza: Classe 8.8
Caratteristiche meccaniche $f_{yb} \leq 649$ N/mm²
$f_{tb} \leq 800$ N/mm²

Saldature
Tipologia
Giunto: Ad angolo (A)
Testa a Testa (T-T)
Dimensione

S1≥S2
l=S2
a=0,71xS2



S1≥S2
l=S2
a=0,5xS2

Criteri di accettabilità (UNI EN ISO 5817:2008)
Livello di qualità: C

COMUNE DI GOITO — PROVINCIA DI MANTOVA

Oggetto

[redacted]

Committente

[redacted]

PROGETTO STRUTTURE

Oggetto tavola
- Fondazioni
- Piante
- Sezioni
- Particolari costruttivi

Tav. n° 01


Variante -

Data


Scale 1:20

[redacted]


PIANTA FONDAZIONI
Scala 1:100

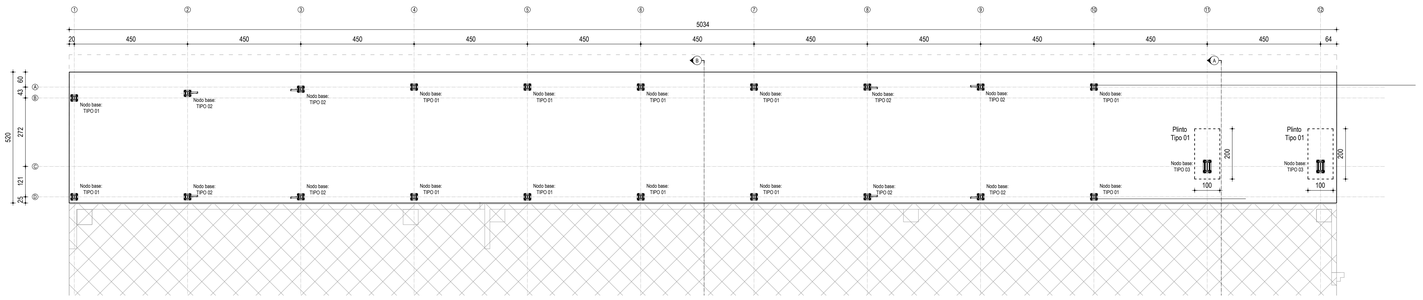


PIANTA FONDAZIONI
Scala 1:100

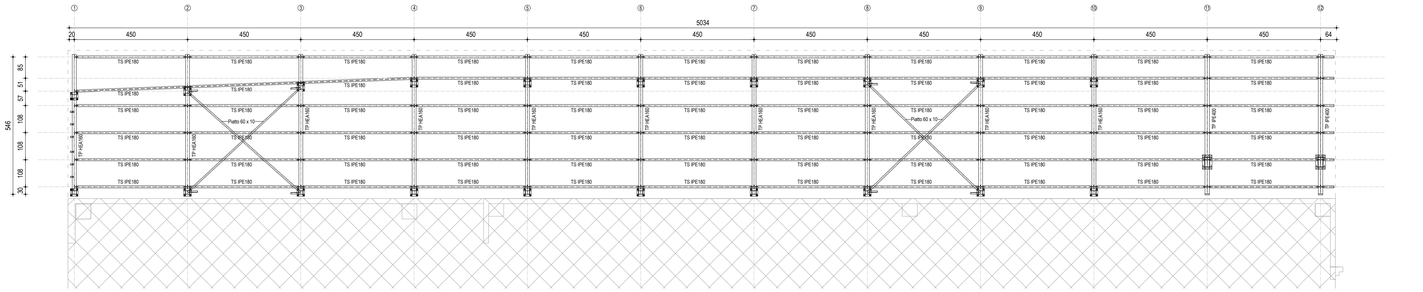


PLINTO TIPO 01 - N°2
Scala 1:20
base rettangolare 100 x 200
Pianta armatura inferiore

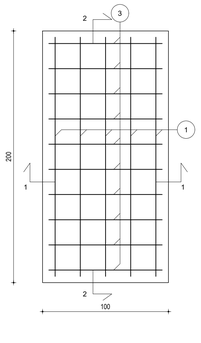


SEZIONE PLATEA A-A
Scala 1:20

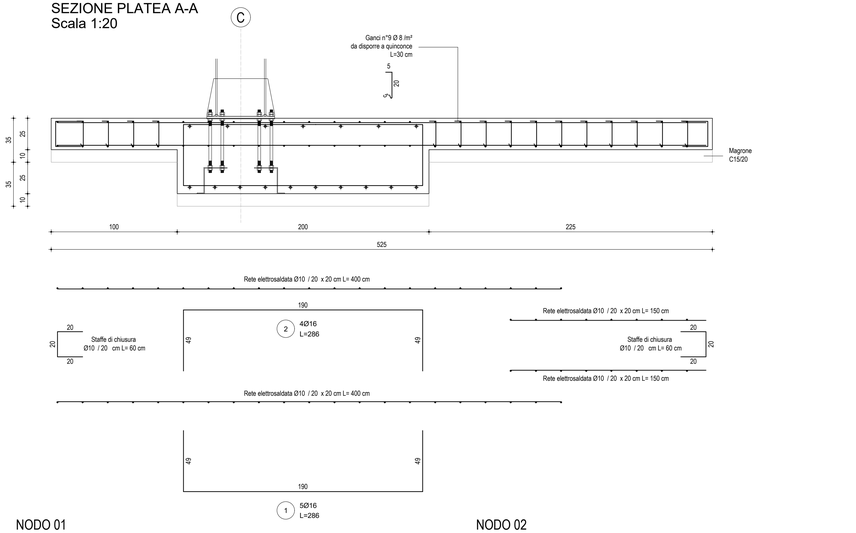



NODO 01
Scala 1:10

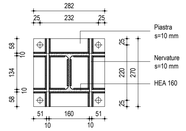

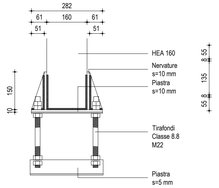


NODO 02
Scala 1:10

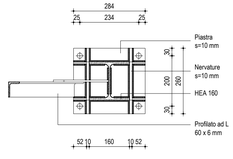


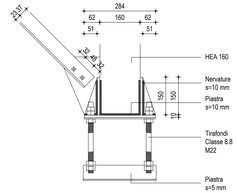


SEZIONE A-A
Scala 1:50

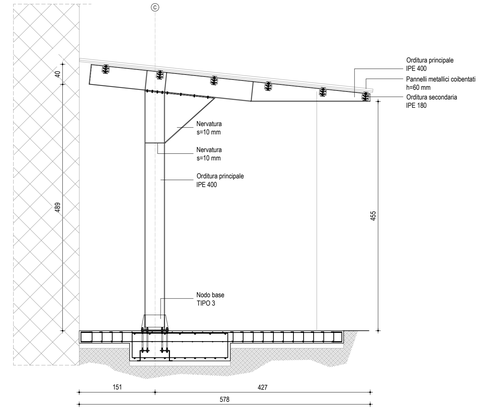


SEZIONE B-B
Scala 1:50

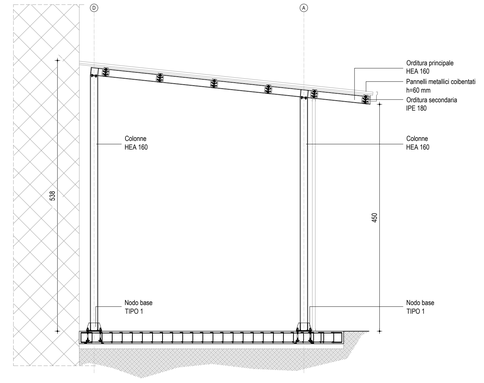

NODO 03
Scala 1:10

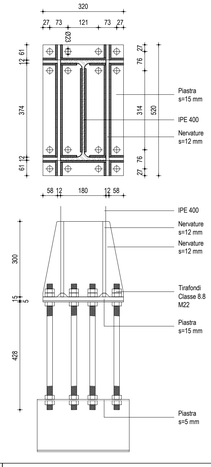

NODO COLONNA- TRAVE SECONDARIA
Scala 1:10

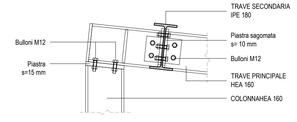

NODO TRAVE PRINCIPALE - TRAVE SECONDARIA
Scala 1:10

